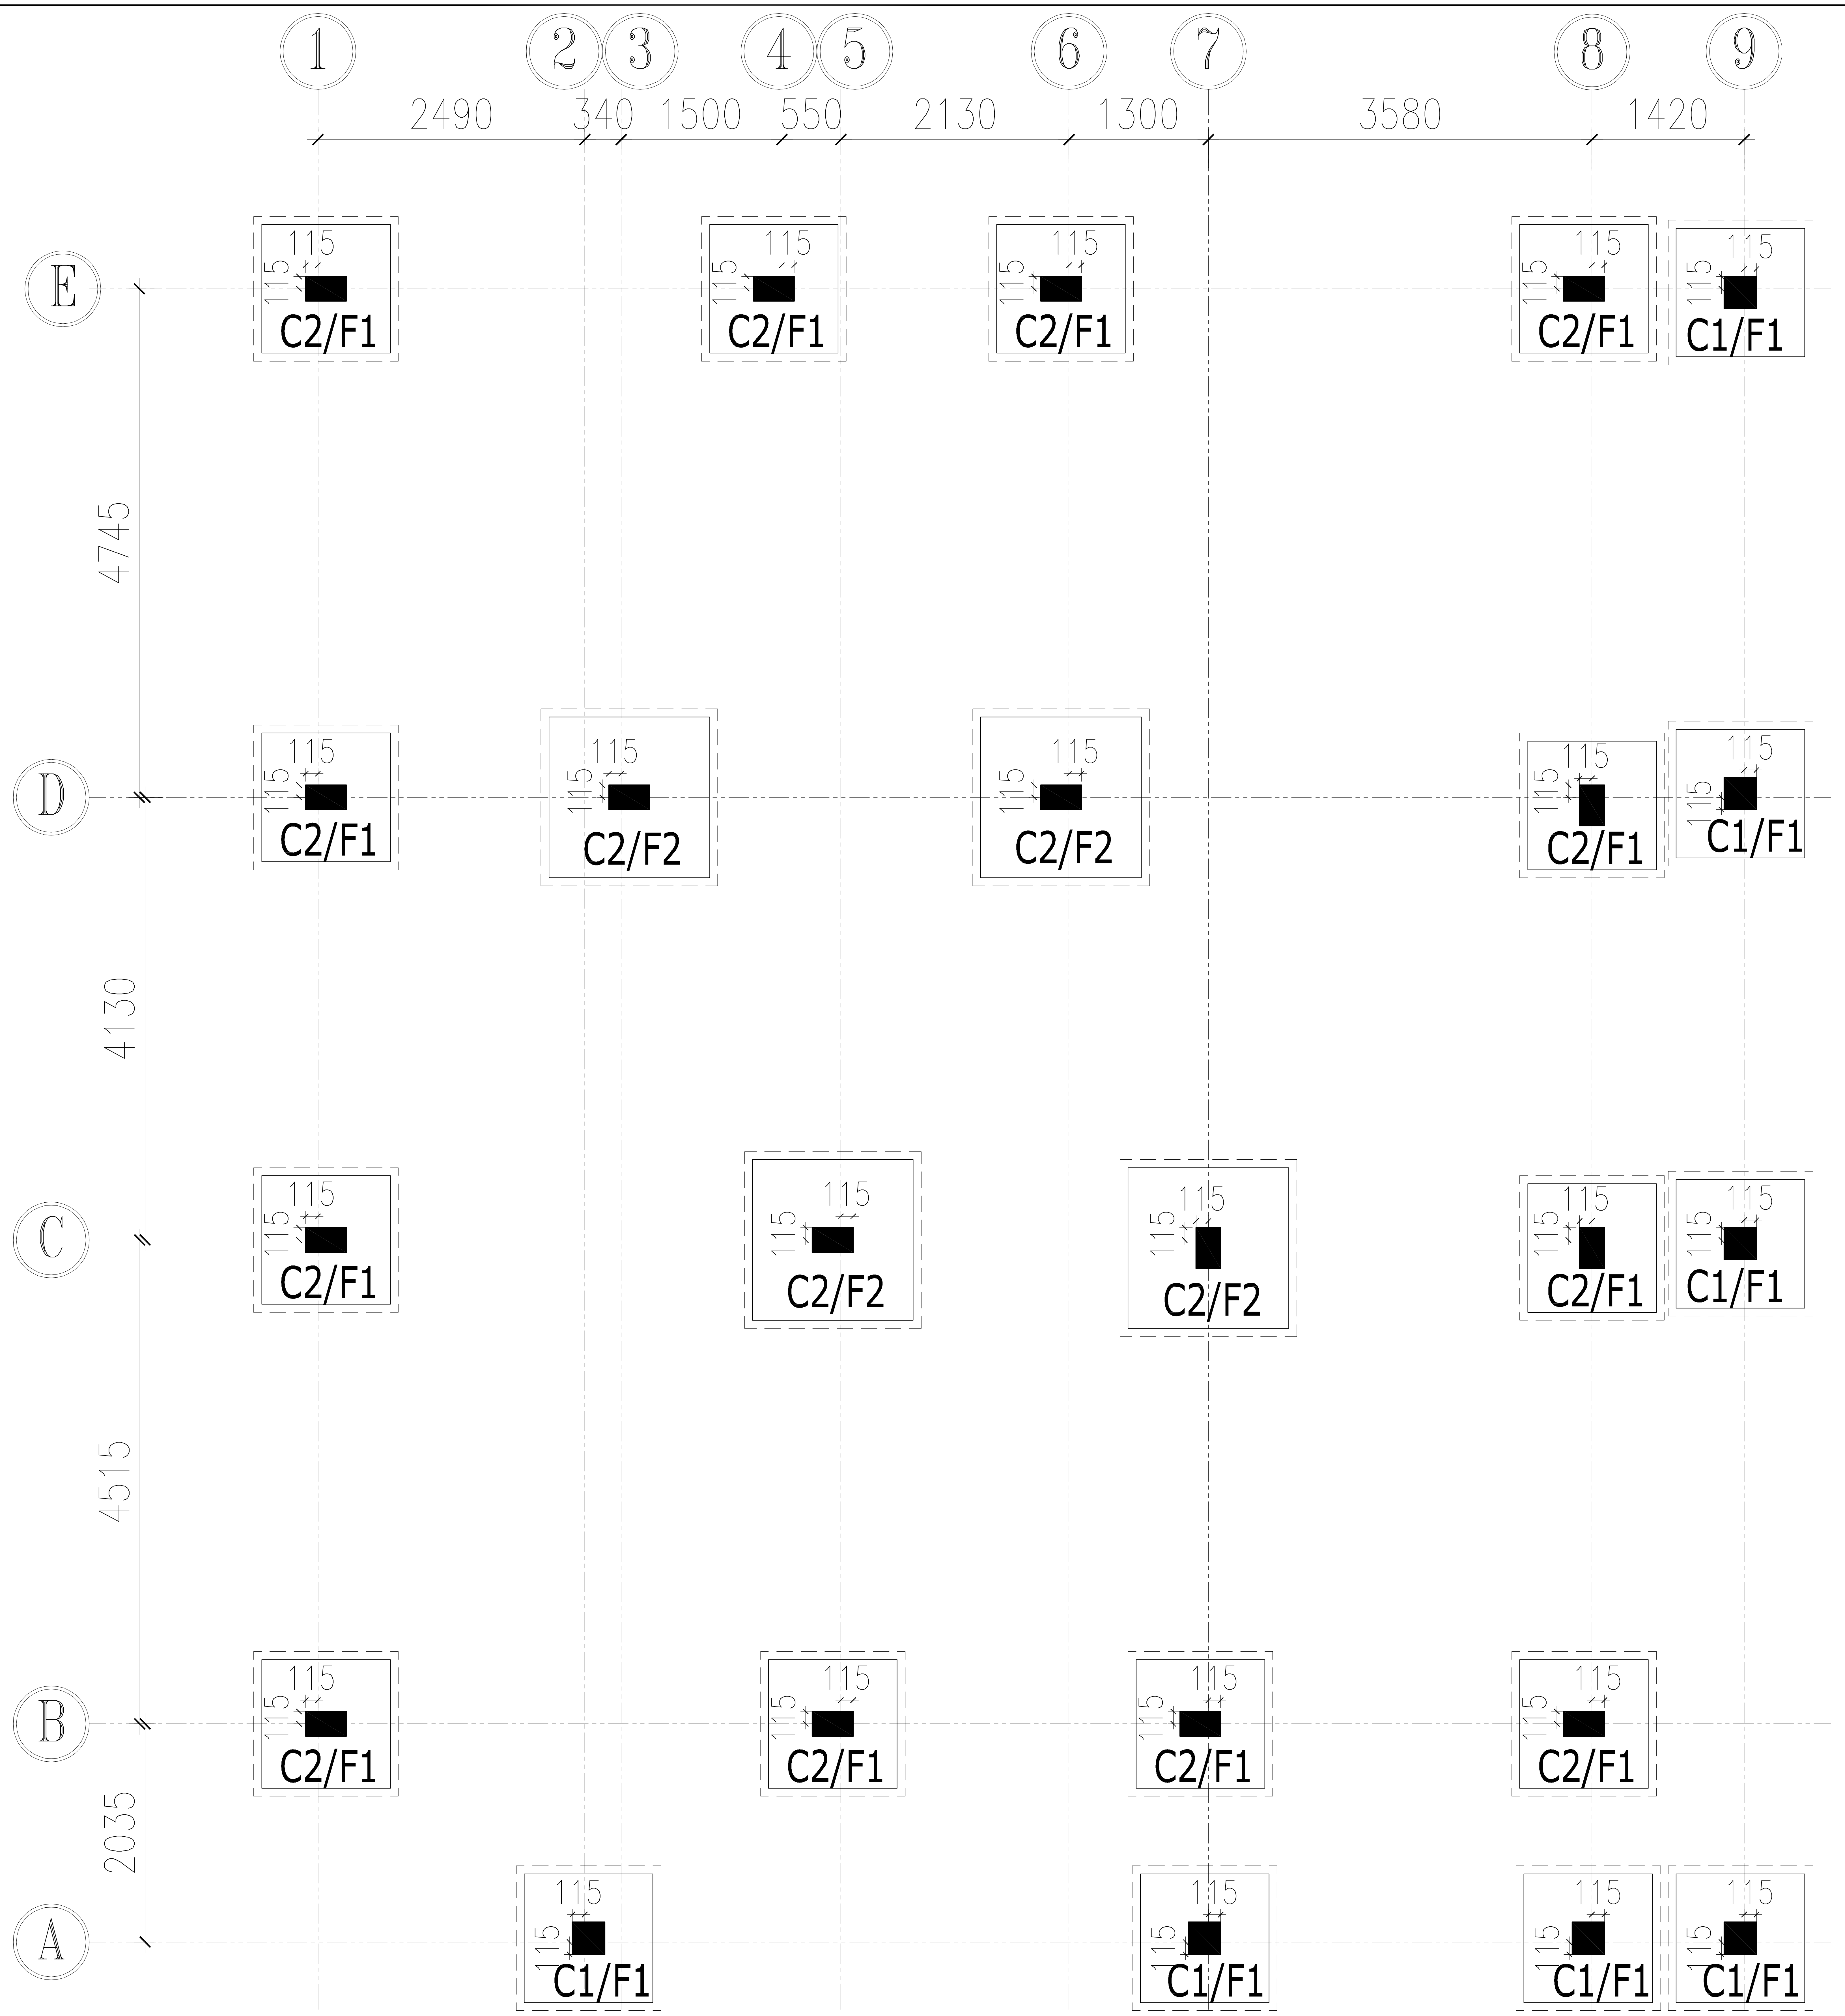
1
2
3
4
5
6
7
8
9
2490
340
1500
550
2130
1300
3580
1420
E
D
C
B
A
4745
4130
4515
2035
115
C2/F1
C2/F2
C1/F1

- THIS DRAWING SHALL BE READ IN CONJUNCTION WITH ALL RELEVANT ARCHITECTURAL, STRUCTURAL AND SERVICES DRAWINGS. ANY DISCREPANCY NOTICED SHALL BE BROUGHT TO THE ATTENTION OF THE CONSULTANTS AND RESOLVED AS SOON AS POSSIBLE BUT ALWAYS PRIOR TO

DIRECTION:

N

ARCHITECTURAL CONSULTANT:

also.
design
a little story of design

STRUCTURAL& MEP CONSULTANTS

JASHRITHA ASSOCIATES
AND MEP PLANNERS
4th FLOOR(4B), HIG 129, KPHB COLONY, KUKATPALLY,
(SUB BRANCH:PR NAGAR ERRAGADDA.)
HYDERABAD 500072, TELANGANA, INDIA
Phone : 9700441106.
E-mail : jashreyansh.consultatns@gmail.com
& jashritha.mep@gmail.com

PROJECT:

ANKURA HOMES_THE WOODS
AT KEESARAGUTTA

DRAWING TITLE:

1625_EAST VILLA
MARKING PLAN

DESIGN ENGG : AJAY	APPROVED :
SCALE : NTS	DRAWN : PK
DATE : 05-10-2026	CHECKED : PRADEEP

DRAWING NO:	SD-01	REV.NO:	02

COLUMN SCHEDULE

COLUMN ID	GRADE OF CONCRETE	COLUMN SIZE	REFERENCE SECTION
C1	M - 25	300 x 300 #12 -4Nos	A1
C2	M - 25	230 x 380 #16 -4Nos + #12 -4Nos	A2

ARRANGEMENT OF TIES, LINKS & MAIN BARS IN COLUMN

4 BARS ARRANGEMENT	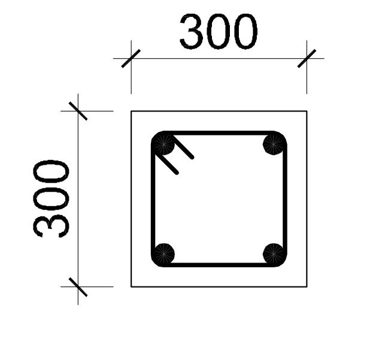 300 300 4 EQUAL DIA (A1)	8 BARS ARRANGEMENT	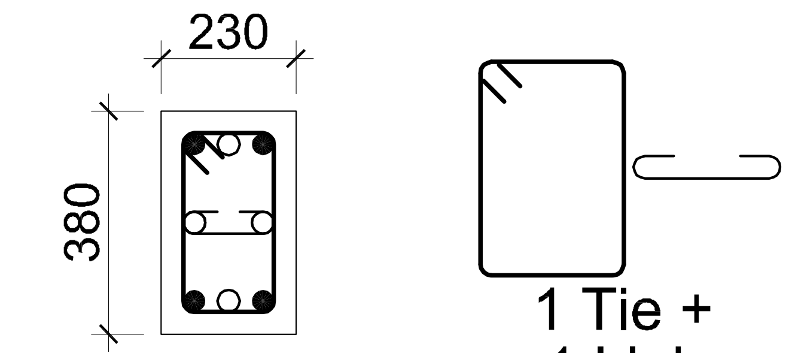 230 380 • 4 LARGER DIA ○ 4 LARGER DIA (A2) 1 Tie + 1 Link #8 @150c/c

FLAT FOOTING SCHEDULE:

GROUP	MIX	SIZE	DEPTH	BOTTOM REINFORCEMENT PARALLEL TO	
				SHORTER DIRECTION	LONGER DIRECTION
F1	M - 25	1200 x 1200	375	#10 -10 NOS	#10 -10 NOS
F2	M - 25	1500 x 1500	400	#10 -15 NOS	#10 -15 NOS

GENERAL NOTES:

1. DO NOT SCALE THIS DRAWING. FOLLOW FIGURED DIMENSIONS ONLY.
2. ALL DIMENSIONS ARE IN MM ONLY AND LEVELS ARE IN METERS UNLESS SPECIFIED.
3. S.B.C OF SOIL IS CONSIDERED AS 270 KN/M^2 @ 2.0M DEPTH
4. USE VIBRATED REINFORCED CONCRETE CONFORMING TO IS:456-2000. THE GRADES FOR DIFFERENT COMPONENTS ARE AS FOLLOWS

COMPONENT	FOOTING	COLUMNS	BEAMS	SLABS	WATER TANK SIDE WALLS
MIX	M25	M25	M25	M25	M25

5. GRADE OF STEEL SHALL BE Fe 500 CONFORMING TO IS:1786-85 & AMENDMENTS.
6. LAPS SHALL BE STAGGERED AND LAP LENGTHS ARE AS FOLLOWS.

MIX	M25
Ld	48 Dia

7. NOT MORE THAN 50% OF COLUMN REINFORCEMENT SHALL BE LAPPED AT A PARTICULAR LOCATION.
8. CLEAR COVERS ARE AS FOLLOWS

FOOTING TO MAIN BAR	COLUMN TO MAIN BAR	BEAMS TO STIRRUPS	SLABS TO MAIN BAR
50mm	40mm	20mm	20mm

9. CURING SHOULD BE DONE ATLEAST FOR 21 DAYS.
10. THIS DRAWING SHOULD BE READ IN CONJUNCTION WITH RELEVANT ARCHITECTURAL DRAWINGS.
11. STRIPPING TIME OF FORMWORK SHALL CONFORM TO CLAUSE 11.3 OF IS:456-2000.
12. FOR TIES,LINKS IN COLUMNS Y8-150mm c/c REFER COLUMN SCHEDULE DWG.
13. FOR EXACT LOCATION OF WALLS REFER RELEVANT ARCHITECTURAL DRAWINGS FOR NECESSARY DETAILS.
14. ANY DISCREPANCY FROM THE DRAWING SHALL BE BROUGHT TO THE NOTICE OF CONSULTANTS.
15. THE STRUCTURE IS DESIGNED FOR GROUND FLOOR ONLY

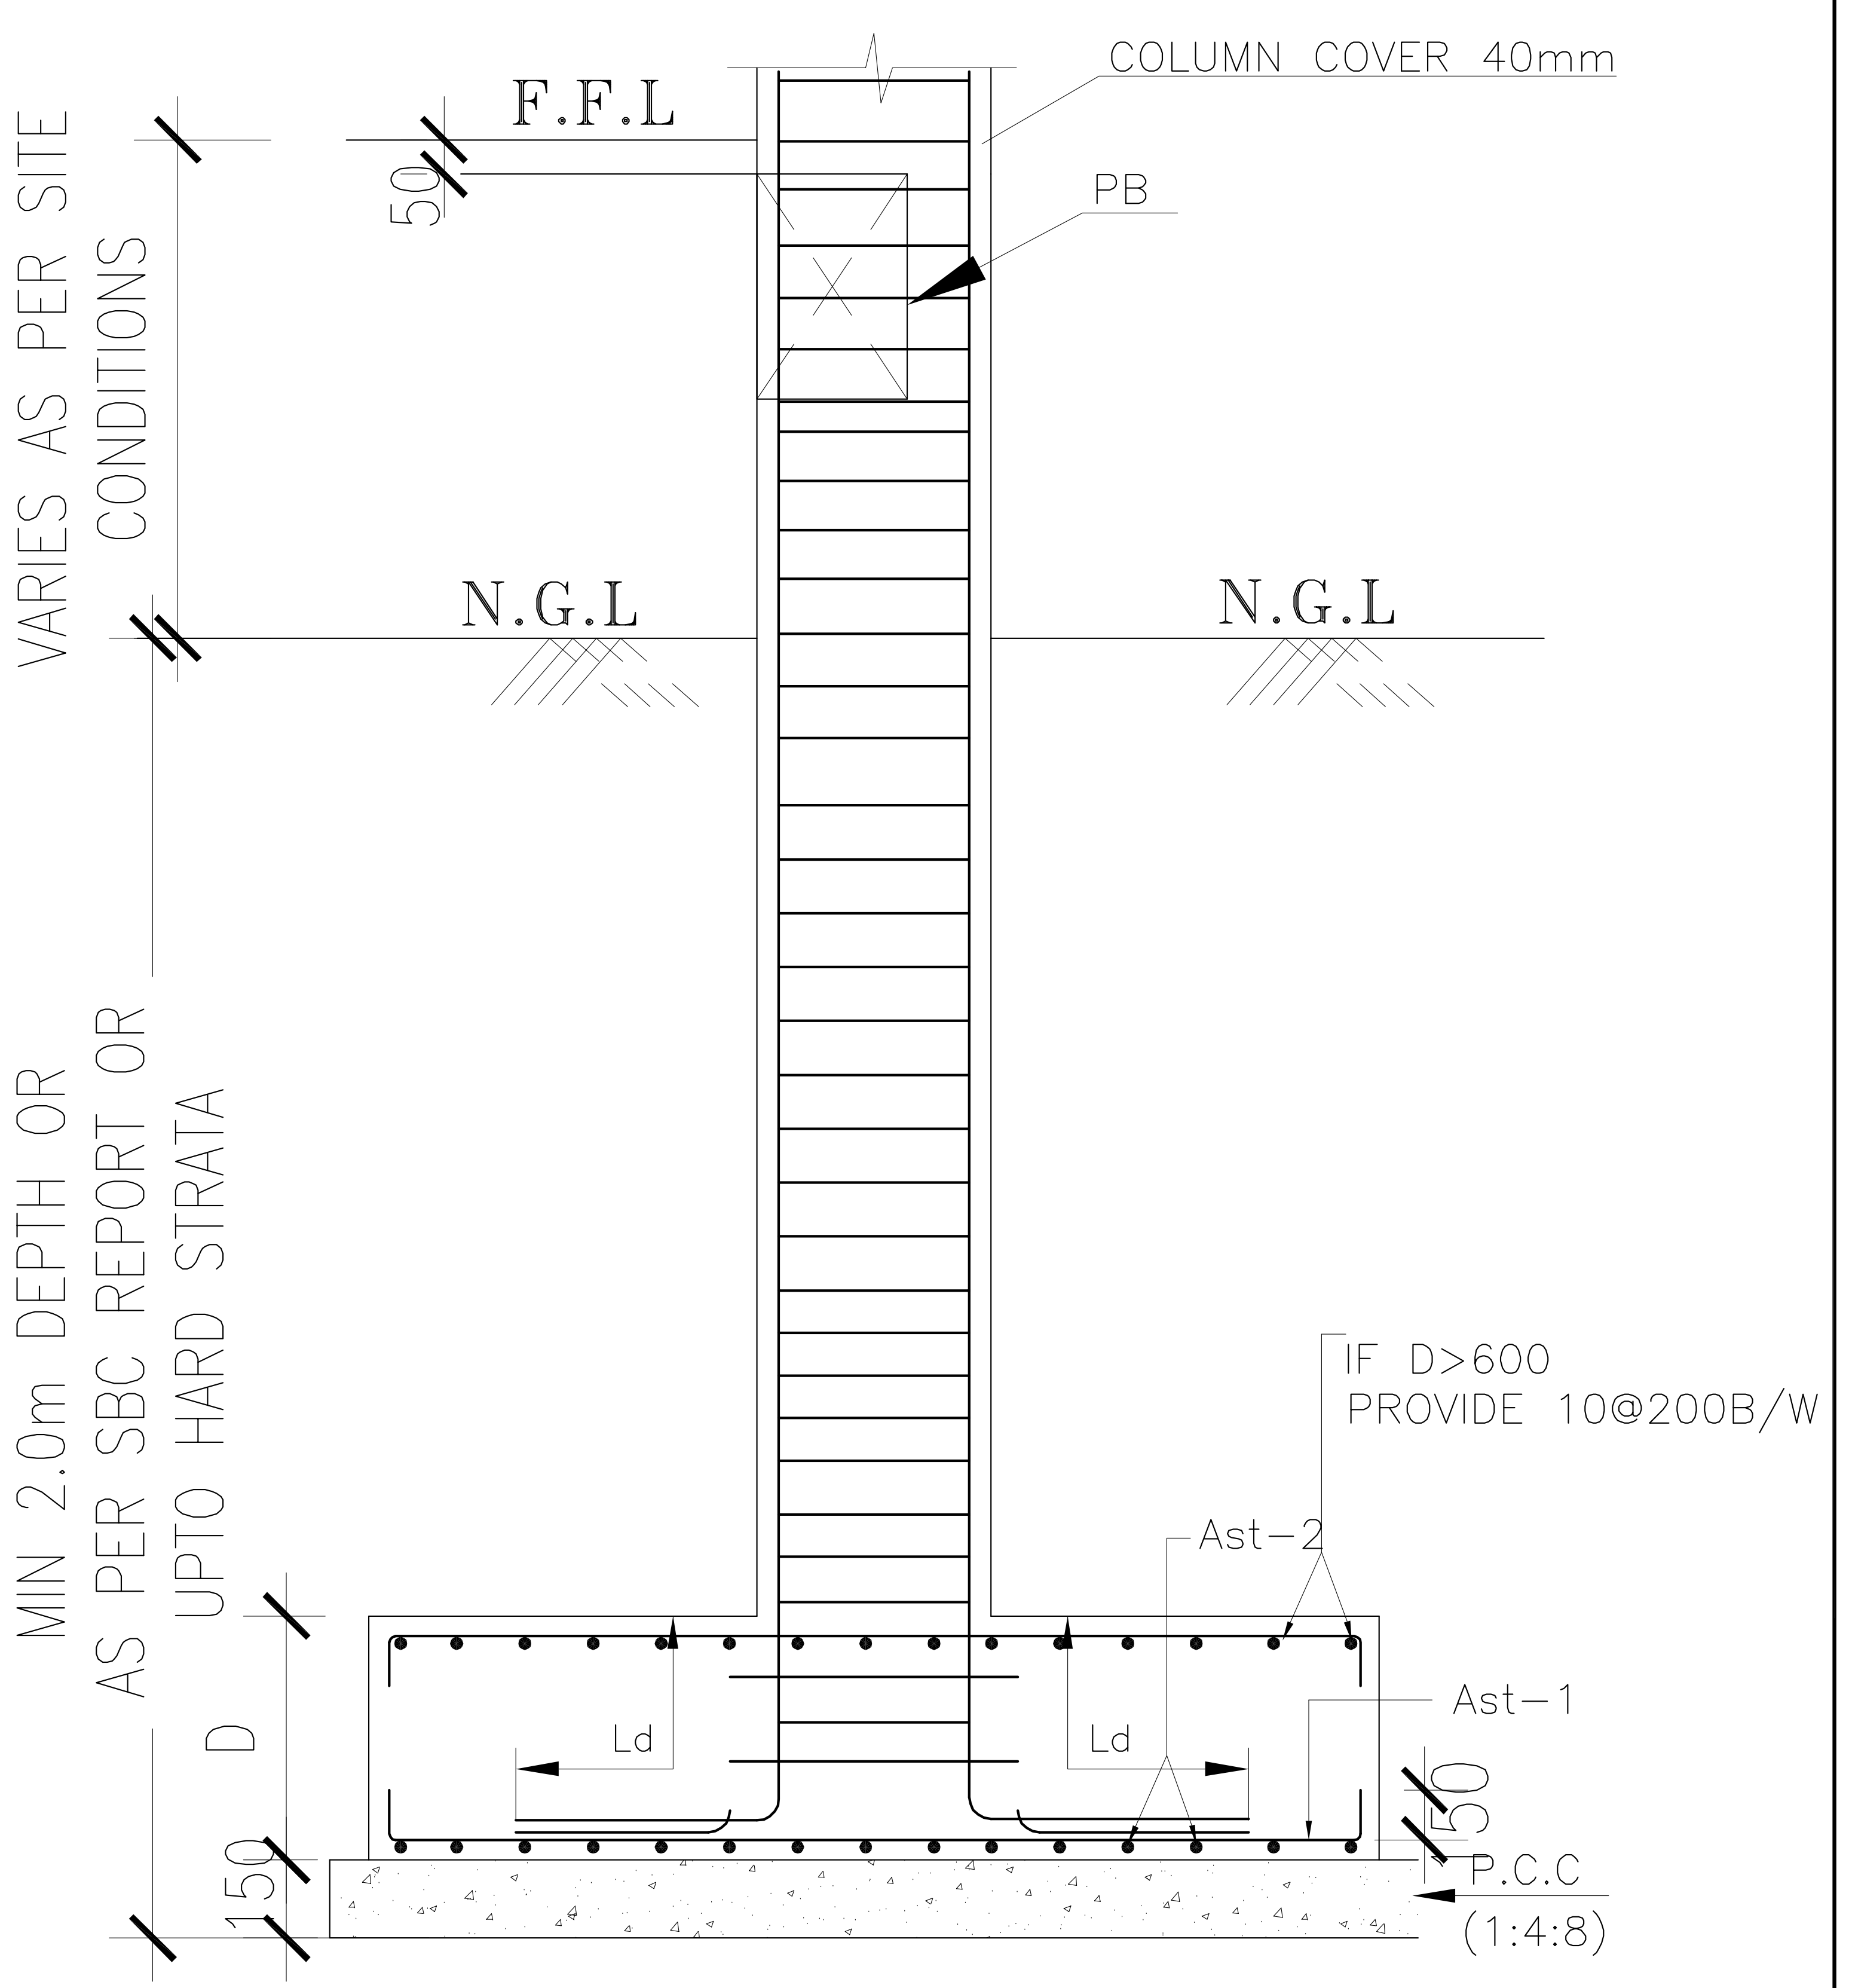

SECTION X-X

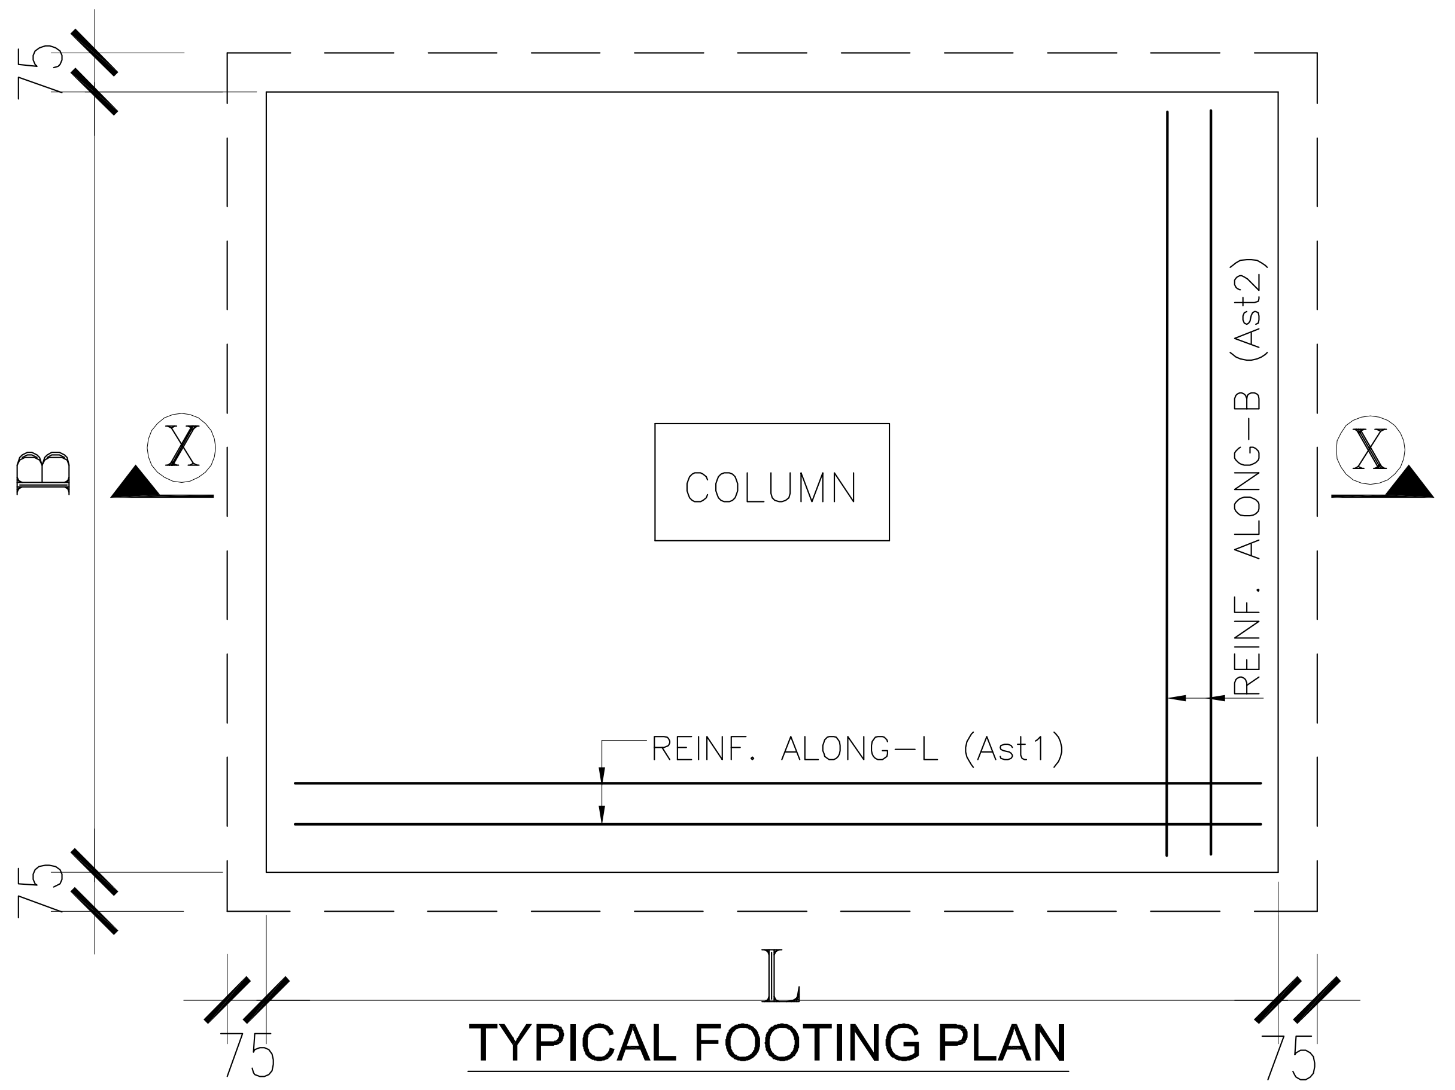

TYPICAL FOOTING PLAN

- THIS DRAWING SHALL BE READ IN CONJUNCTION WITH ALL RELEVANT ARCHITECTURAL, STRUCTURAL AND SERVICES DRAWINGS. ANY DISCREPANCY NOTICED SHALL BE BROUGHT TO THE ATTENTION OF THE CONSULTANTS AND RESOLVED AS SOON AS POSSIBLE BUT ALWAYS PRIOR TO

ARCHITECTURAL CONSULTANT:

also. design

STRUCTURAL& MEP CONSULTANTS

JASHRITHA ASSOCIATES
AND MEP PLANNERS
4th FLOOR(4B), HIG 129, KPHB COLONY, KUKATPALLY,
(SUB BRANCH:PR NAGAR ERRAGADDA.)
HYDERABAD 500072, TELANGANA, INDIA
Phone : 9700441106.
E-mail : jashreyansh.consultatns@gmail.com
& jashritha.mep@gmail.com

PROJECT:

ANKURA HOMES_THE WOODS
AT KEESARAGUTTA

DRAWING TITLE:

1625_EAST VILLA
COLUMN & FOOTING
SCHEDULE

DESIGN ENGG : AJAY	APPROVED :
SCALE : NTS	DRAWN : PK
DATE : 05-10-2026	CHECKED : PRADEEP
DRAWING NO: SD-02	REV.NO: 01

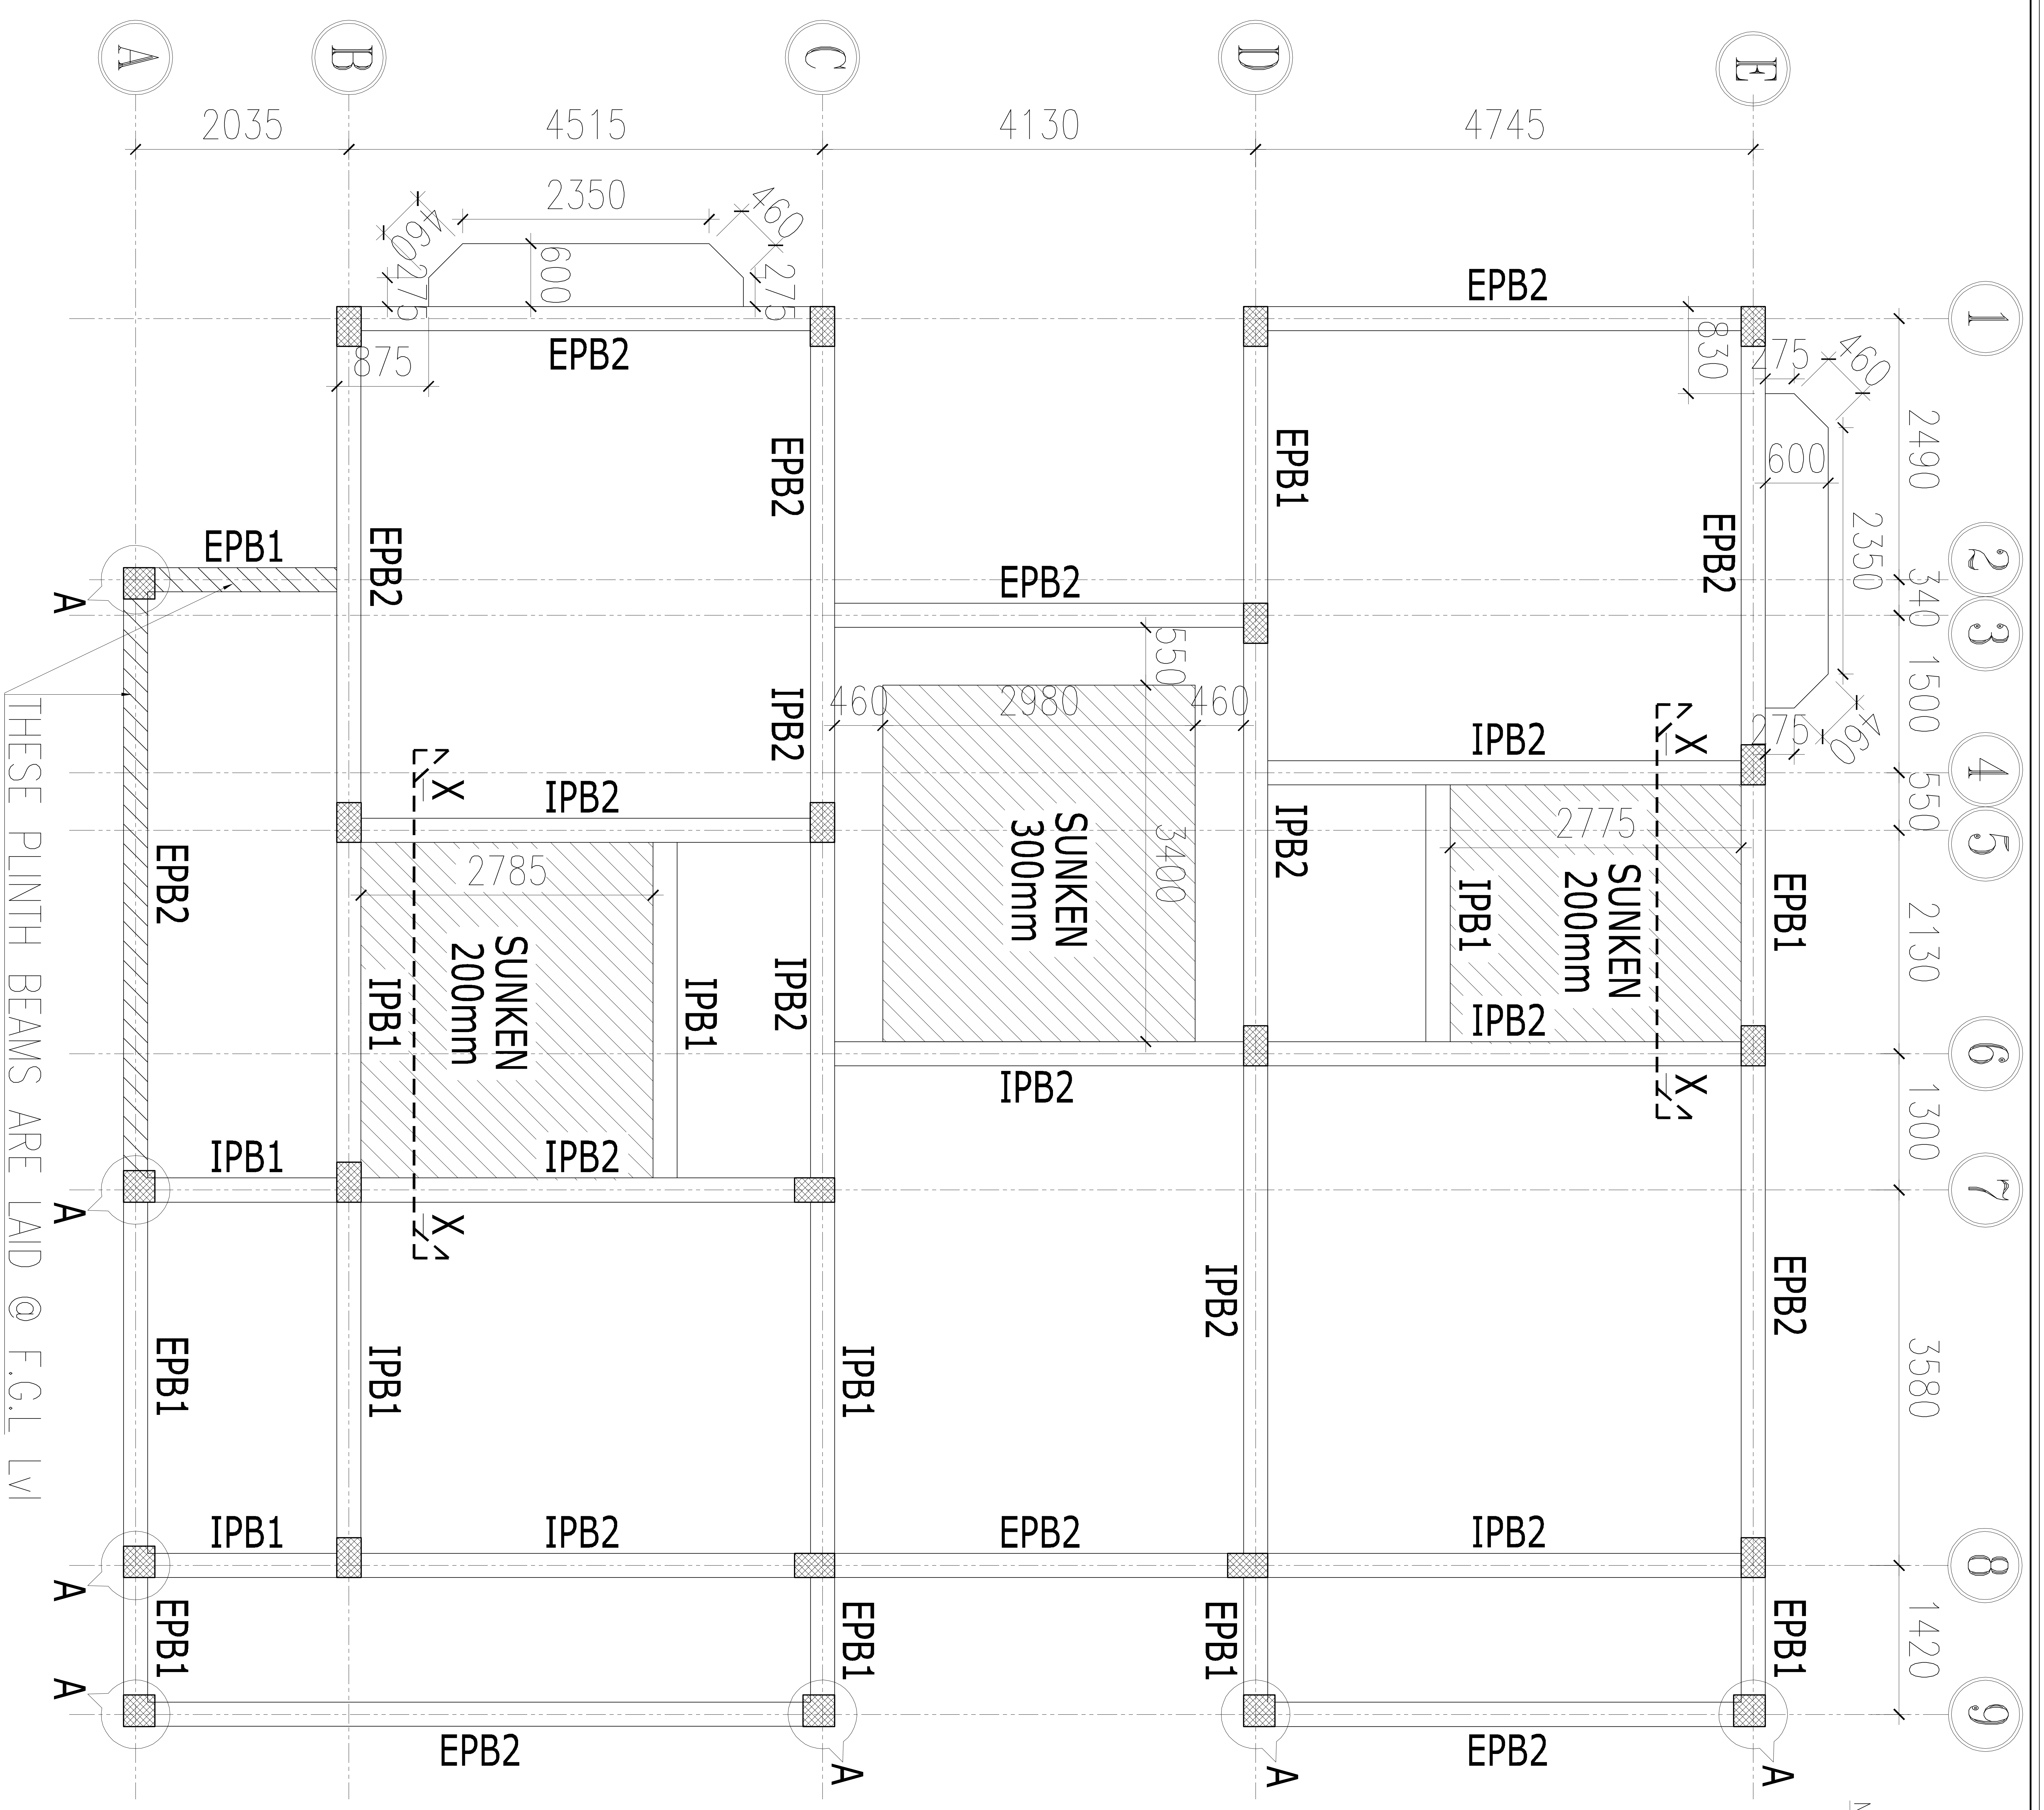
A
B
C
D
E
2035
4515
4130
4745
2350
460
460
275
275
600
875
830
1
2
3
4
5
6
7
8
9
2490
2350
340
1500
550
2130
1300
3580
1420
EPB1
EPB2
IPB1
IPB2
550
460
2980
460
3400
2785
2775
SUNKEN 300mm
SUNKEN 200mm
SUNKEN 200mm
X
A
THESE PLINTH BEAMS ARE LAID @ F.G.L Lvl

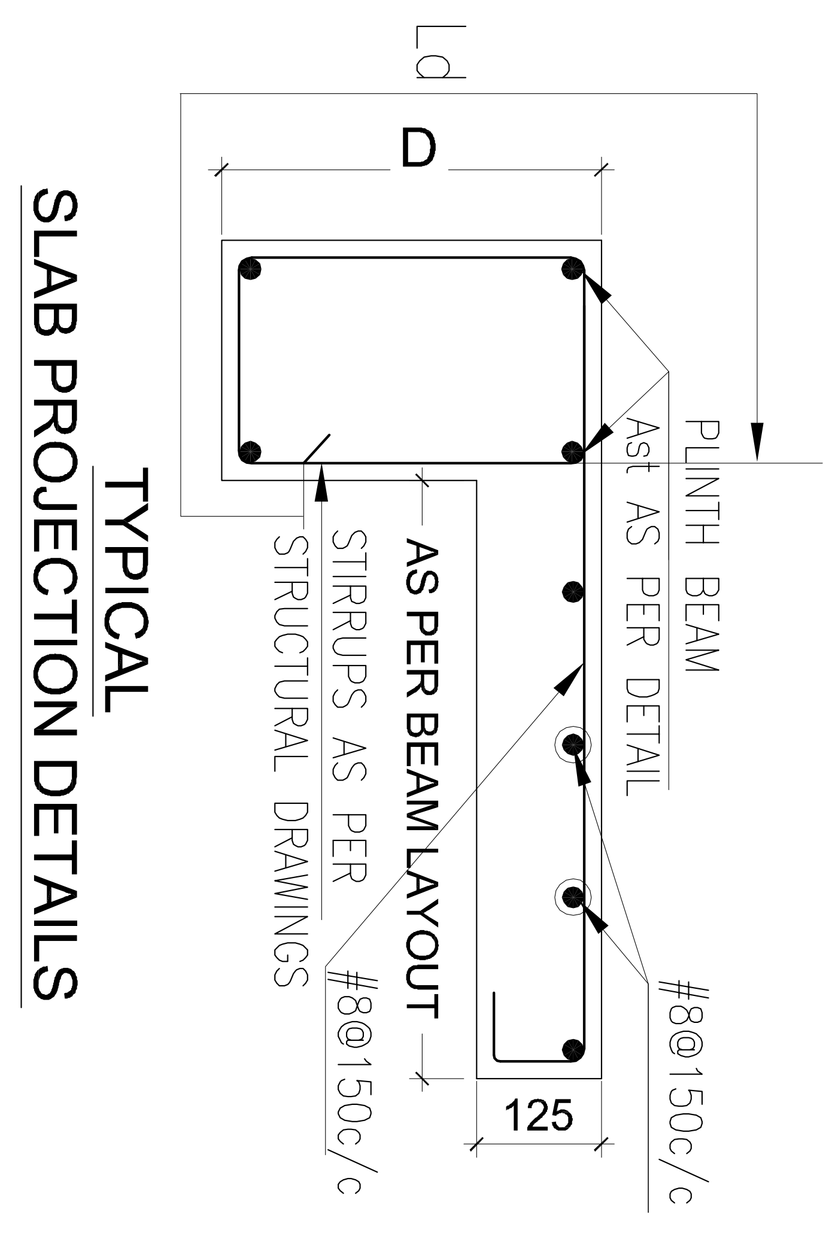
Ld
D
PLINTH BEAM
Ast AS PER DETAIL
AS PER BEAM LAYOUT
STIRRUPS AS PER STRUCTURAL DRAWINGS
#8@150c/c
#8@150c/c
125

TYPICAL SLAB PROJECTION DETAILS

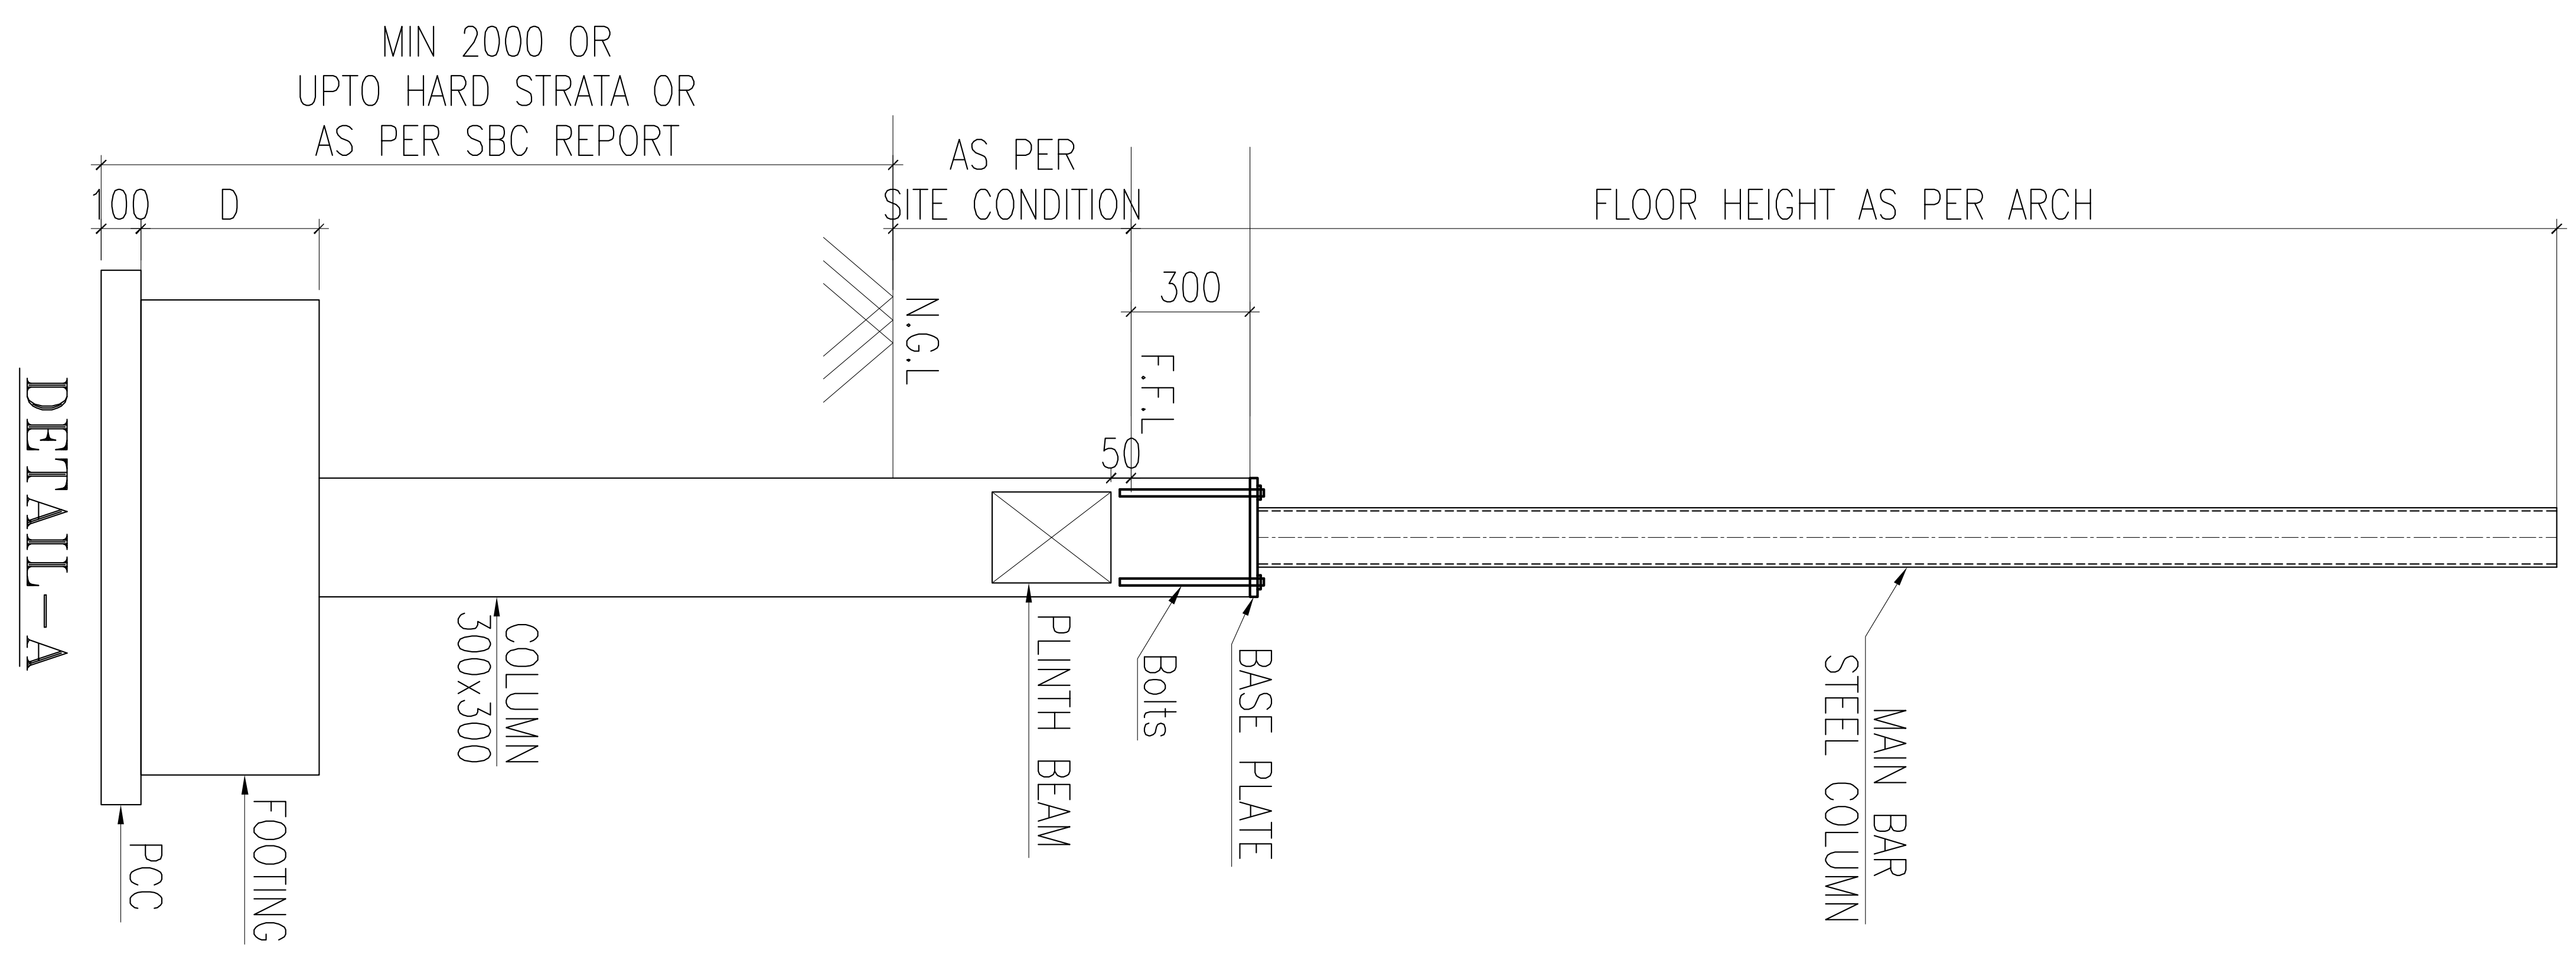
MIN 2000 OR UPTO HARD STRATA OR AS PER SBC REPORT
AS PER SITE CONDITION
FLOOR HEIGHT AS PER ARCH
100
D
300
50
N.G.L
F.F.L
COLUMN 300x300
PCC
FOOTING
PLINTH BEAM
Bolts
BASE PLATE
MAIN BAR STEEL COLUMN

DETAIL-A

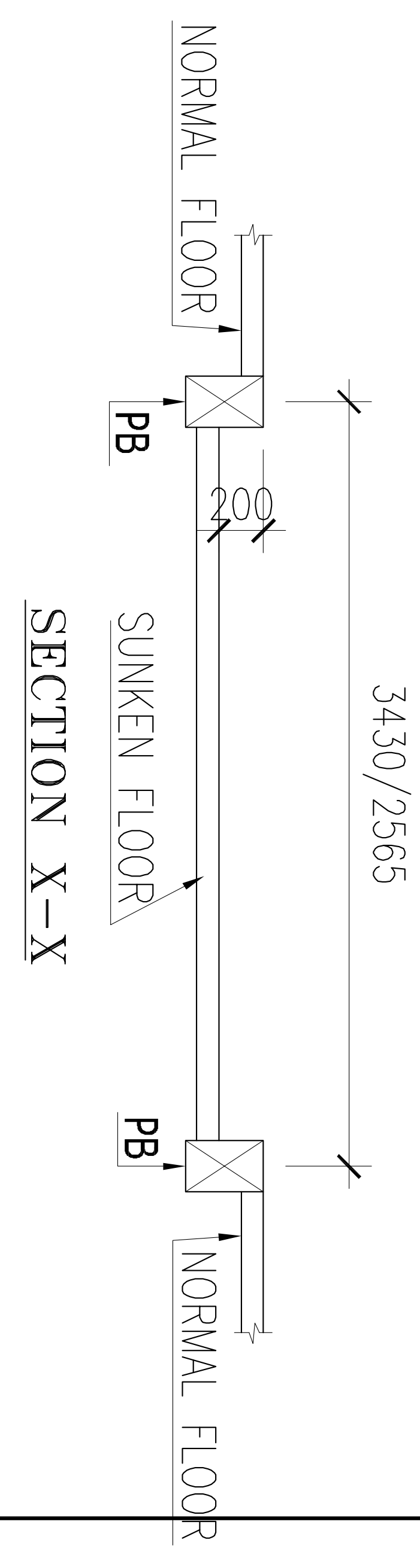
NORMAL FLOOR
PB
200
SUNKEN FLOOR
3430/2565
PB
NORMAL FLOOR

SECTION X-X

- THIS DRAWING SHALL BE READ IN CONJUNCTION WITH ALL RELEVANT ARCHITECTURAL, STRUCTURAL AND SERVICES DRAWINGS. ANY DISCREPANCY NOTICED SHALL BE BROUGHT TO THE ATTENTION OF THE CONSULTANTS AND RESOLVED AS SOON AS POSSIBLE BUT ALWAYS PRIOR TO

DIRECTION:

N

ARCHITECTURAL CONSULTANT:

also. design

STRUCTURAL& MEP CONSULTANTS

JASHRITHA ASSOCIATES
AND MEP PLANNERS
4th FLOOR(4B), HIG 129, KPHB COLONY, KUKATPALLY,
(SUB BRANCH:PR NAGAR ERRAGADDA,)
HYDERABAD 500072, TELANGANA, INDIA
Phone : 9700441106,
E-mail : jashreyansh.consultatns@gmail.com
& jashritha.mep@gmail.com

PROJECT:

ANKURA HOMES_THE WOODS
AT KEESARAGUTTA

DRAWING TITLE:

1625_EAST VILLA
PLINTH BEAM LAYOUT

DESIGN ENGG : AJAY	APPROVED :
SCALE : NTS	DRAWN : PK
DATE : 05-10-2026	CHECKED : PRADEEP
DRAWING NO: SD-03	REV.NO: 02

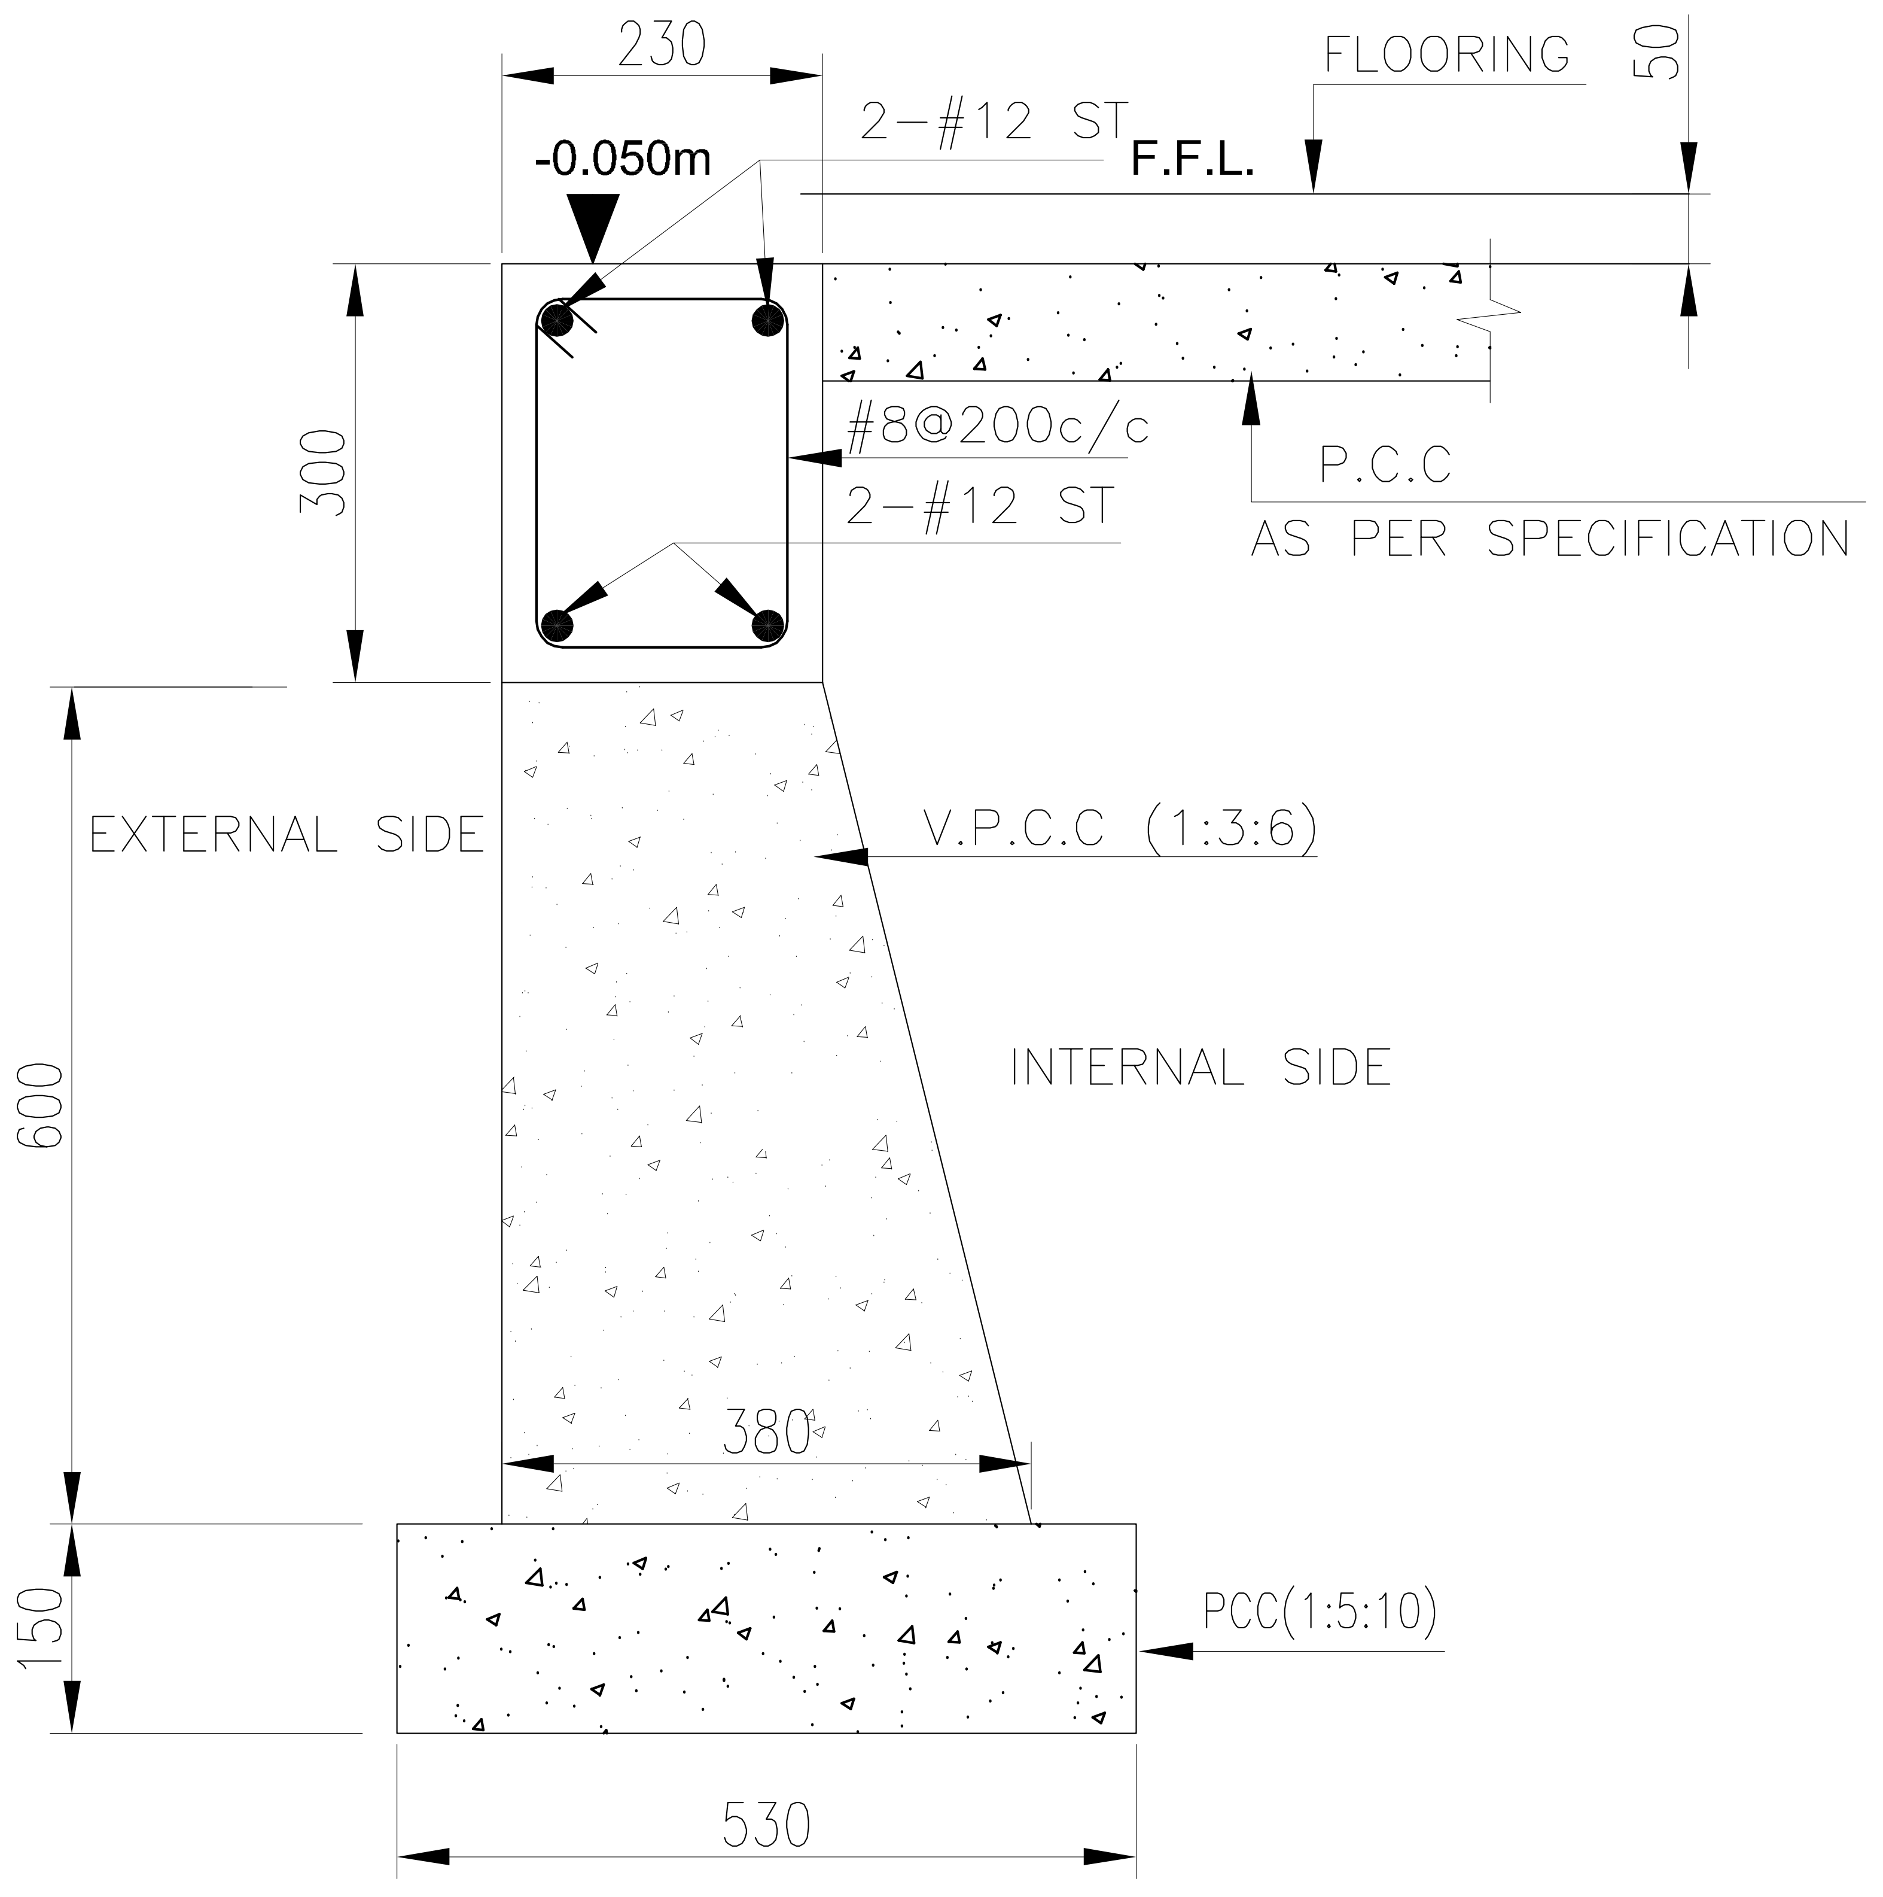
230
-0.050m
2–#12 ST
F.F.L.
FLOORING
50
300
#8@200c/c
2–#12 ST
P.C.C
AS PER SPECIFICATION
EXTERNAL SIDE
V.P.C.C (1:3:6)
INTERNAL SIDE
600
380
150
PCC(1:5:10)
530

EPB1

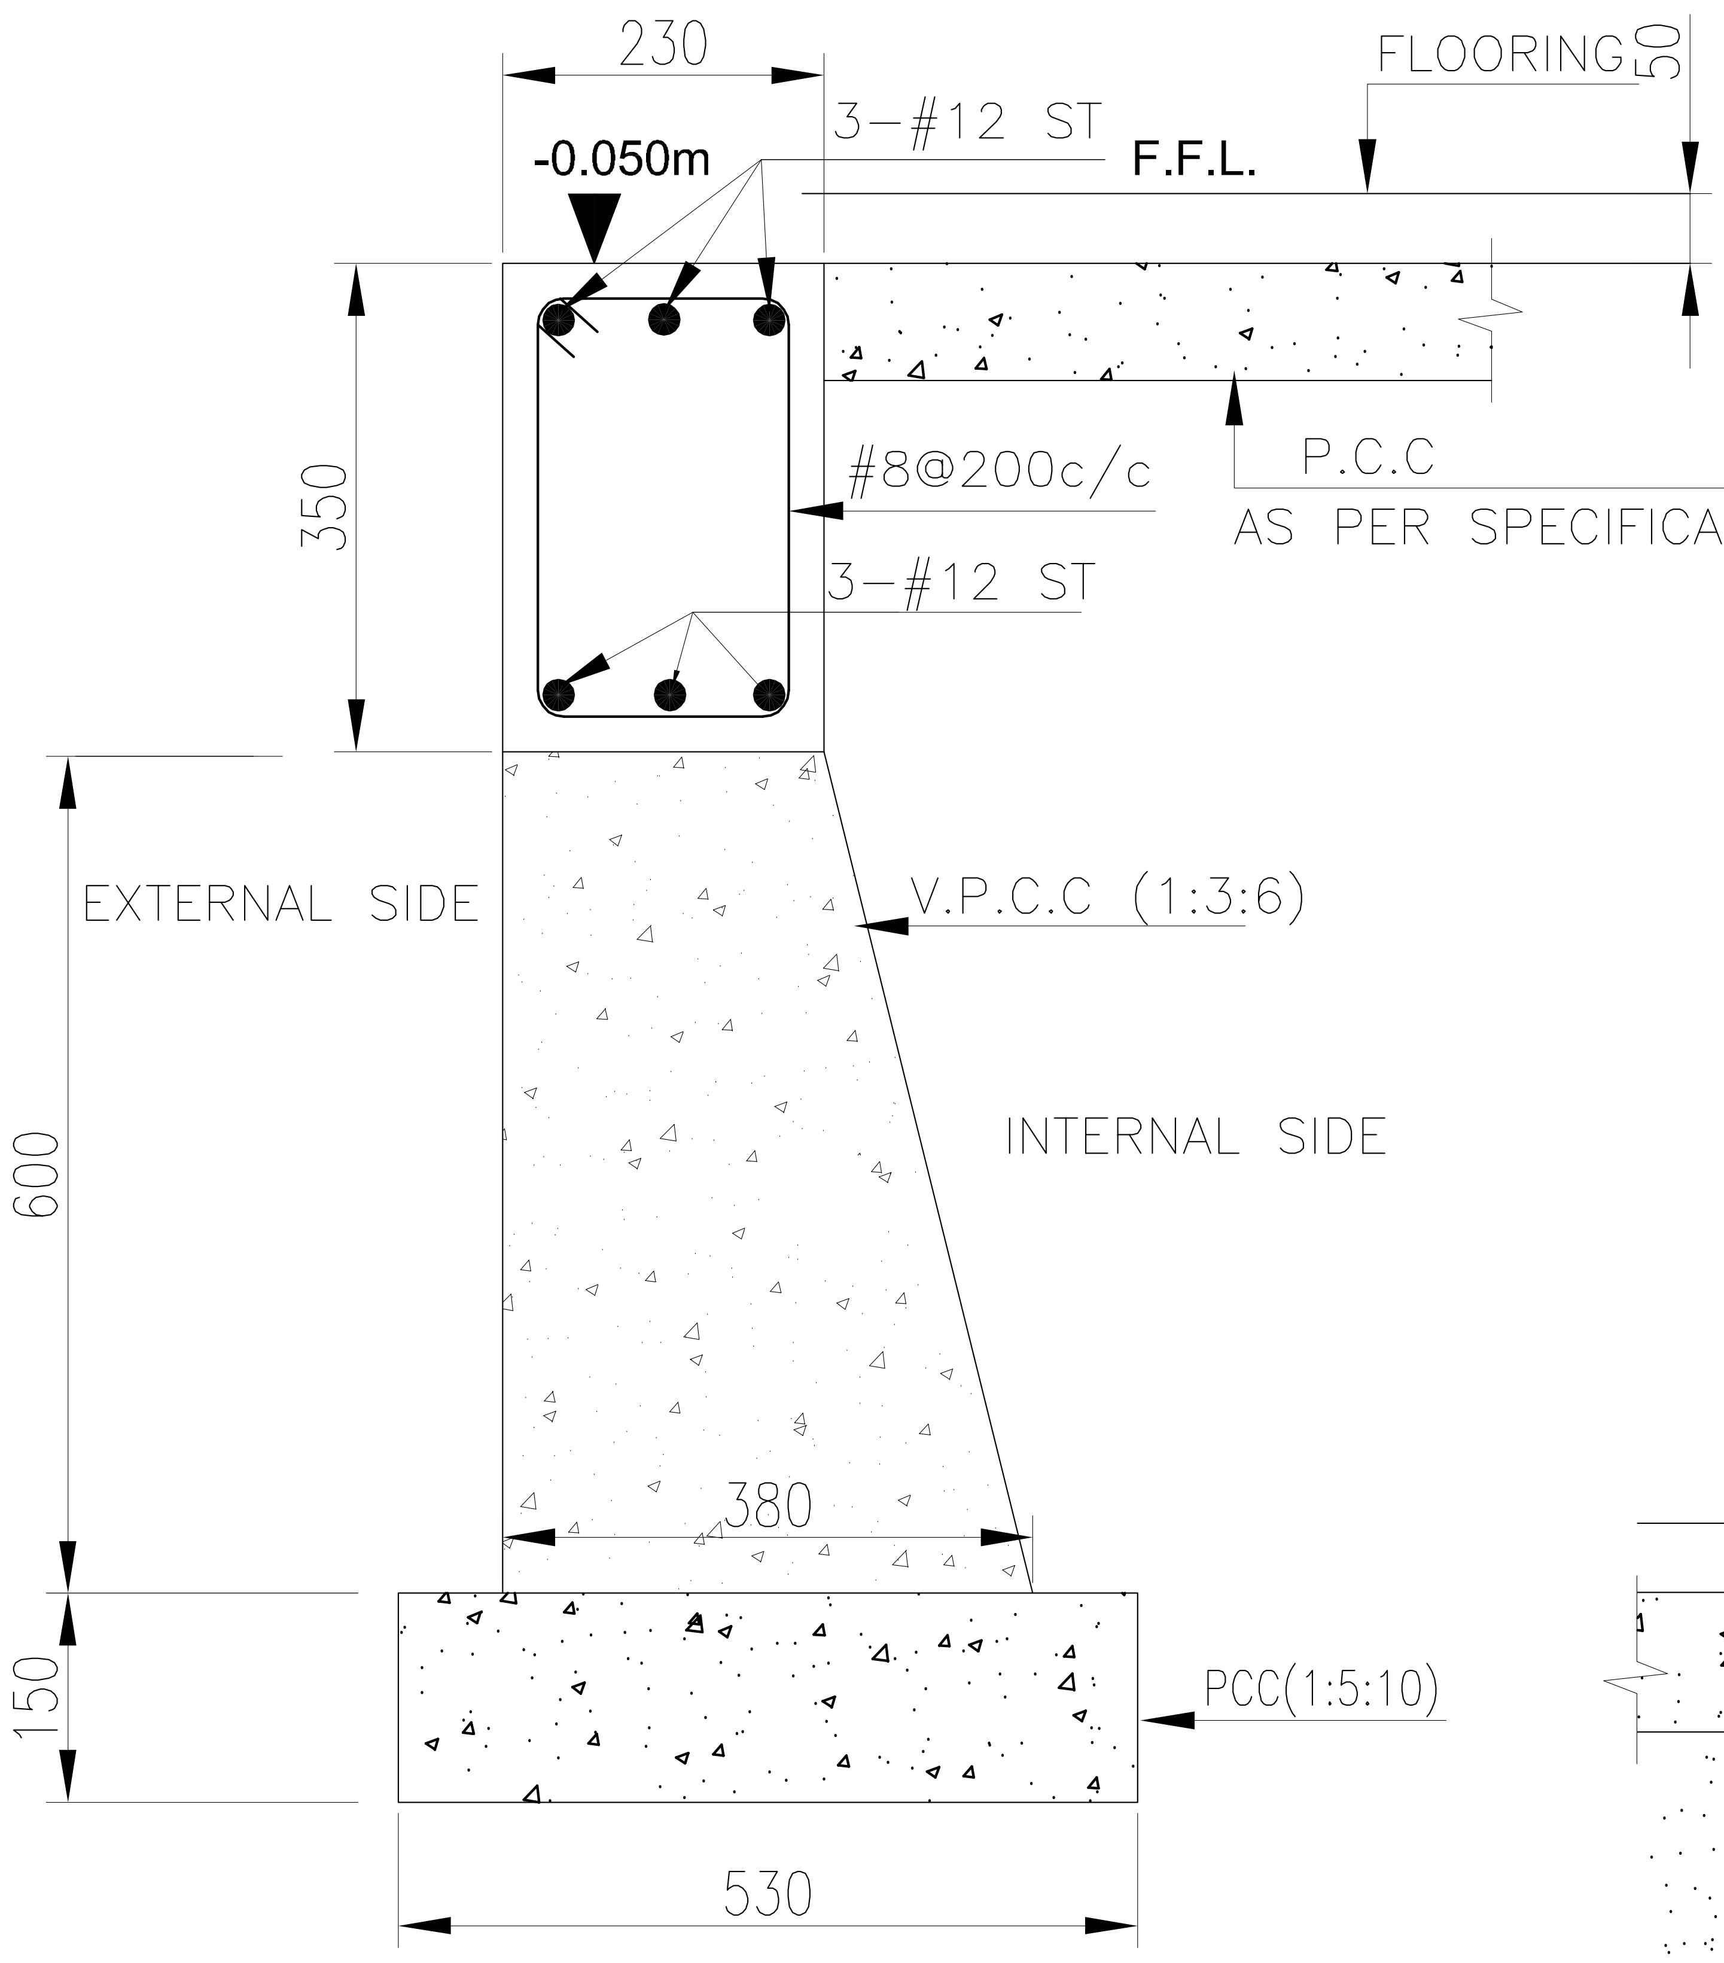
230
-0.050m
3–#12 ST
F.F.L.
FLOORING
50
350
#8@200c/c
3–#12 ST
P.C.C
AS PER SPECIFICATION
EXTERNAL SIDE
V.P.C.C (1:3:6)
INTERNAL SIDE
600
380
150
PCC(1:5:10)
530

EPB2

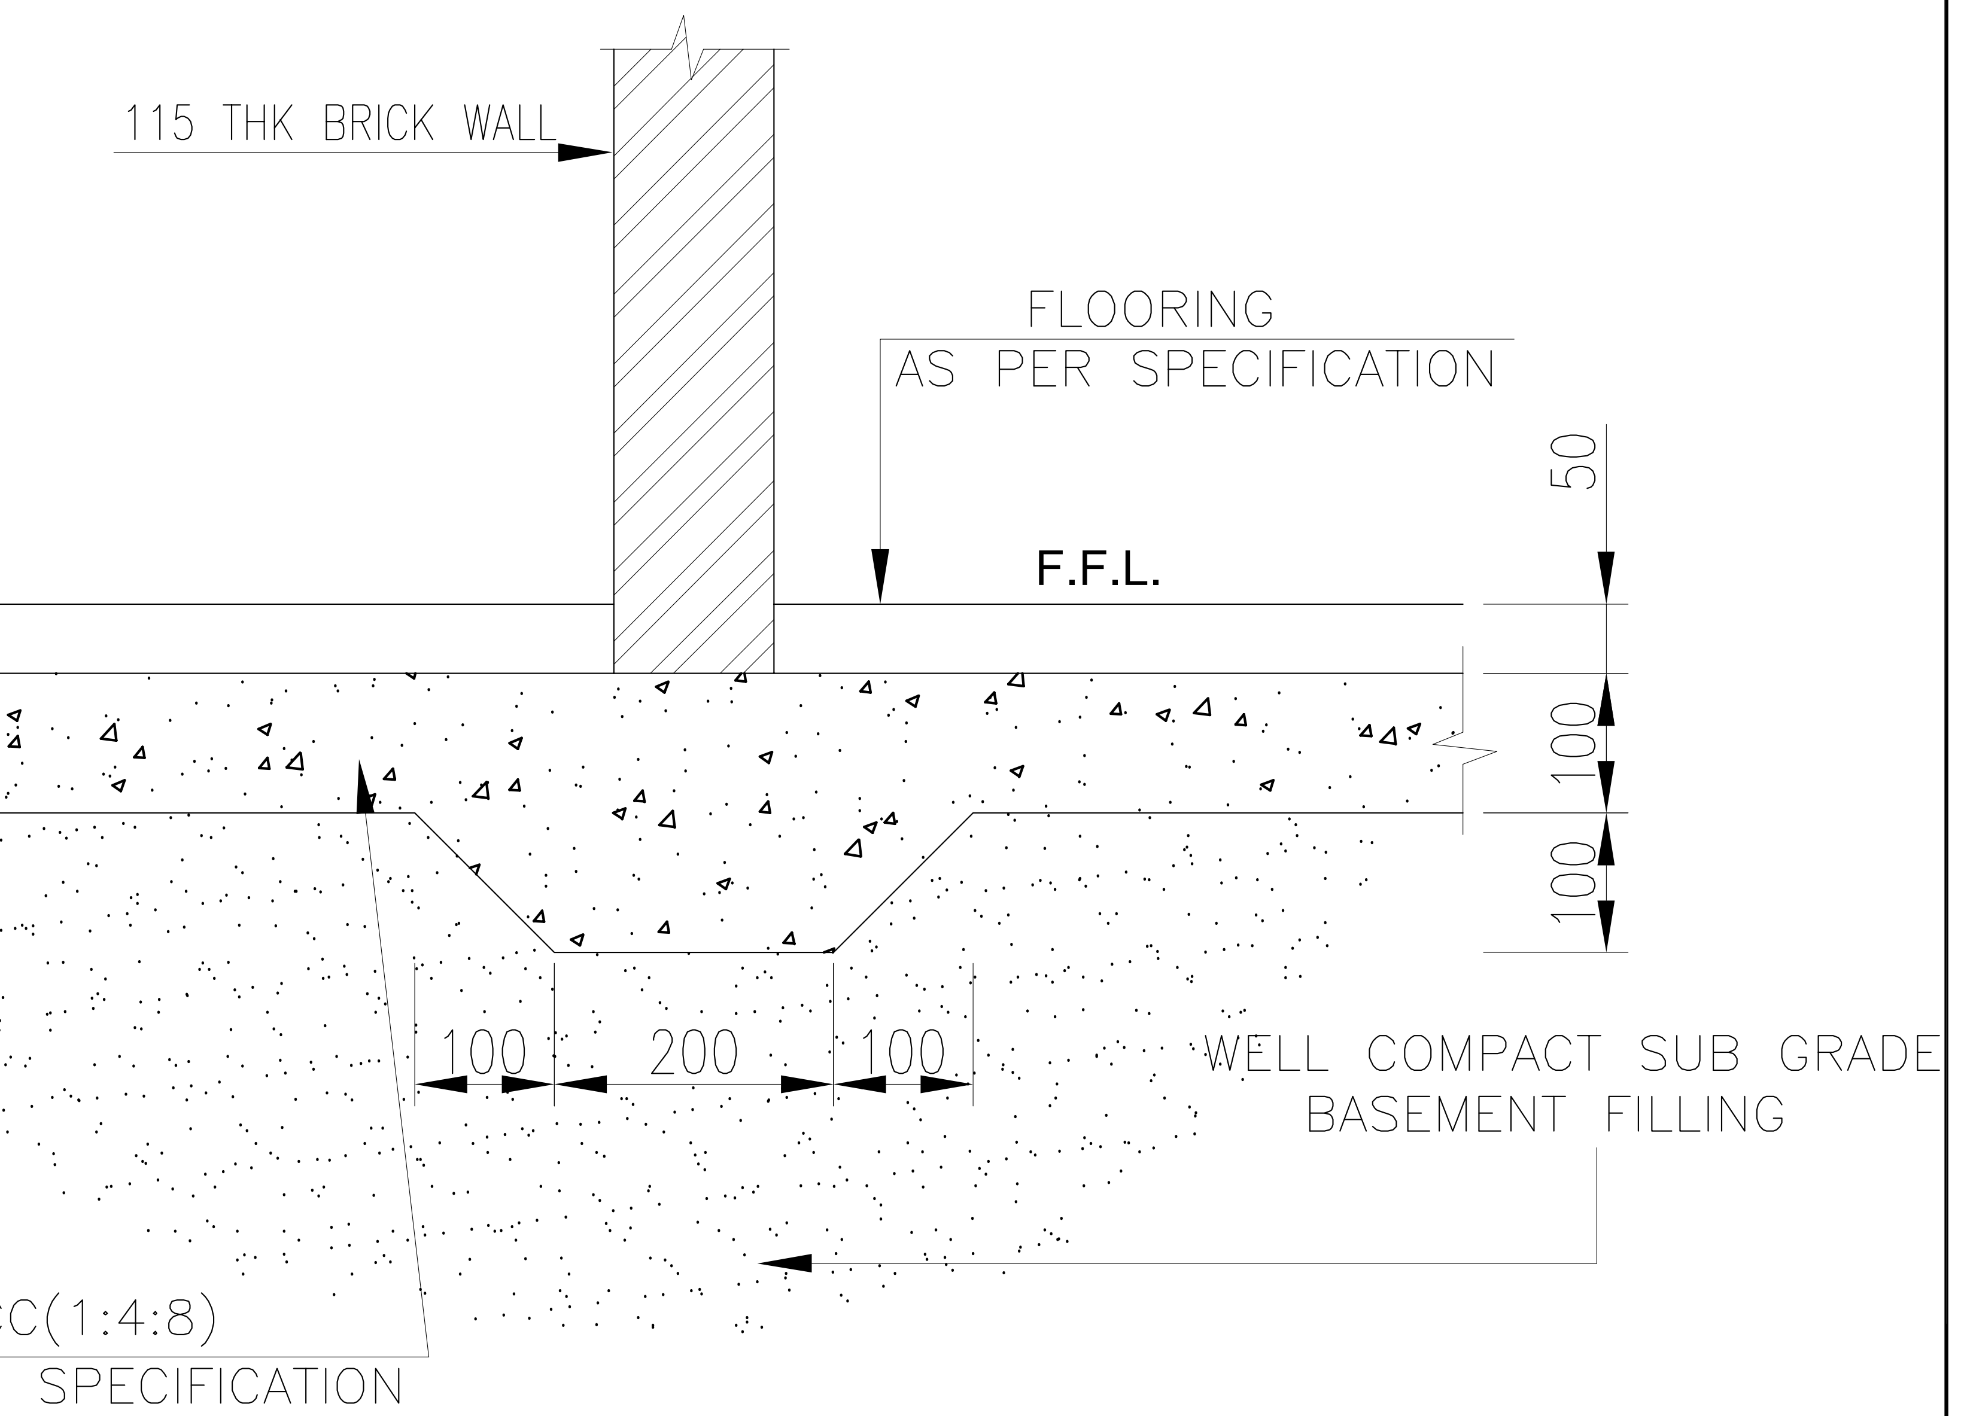
115 THK BRICK WALL
FLOORING
AS PER SPECIFICATION
50
F.F.L.
100
100
100
200
100
WELL COMPACT SUB GRADE
BASEMENT FILLING
PCC(1:4:8)
AS PER SPECIFICATION

FOUNDATION DETAIL UNDER
115mm THICK BRICK WALL

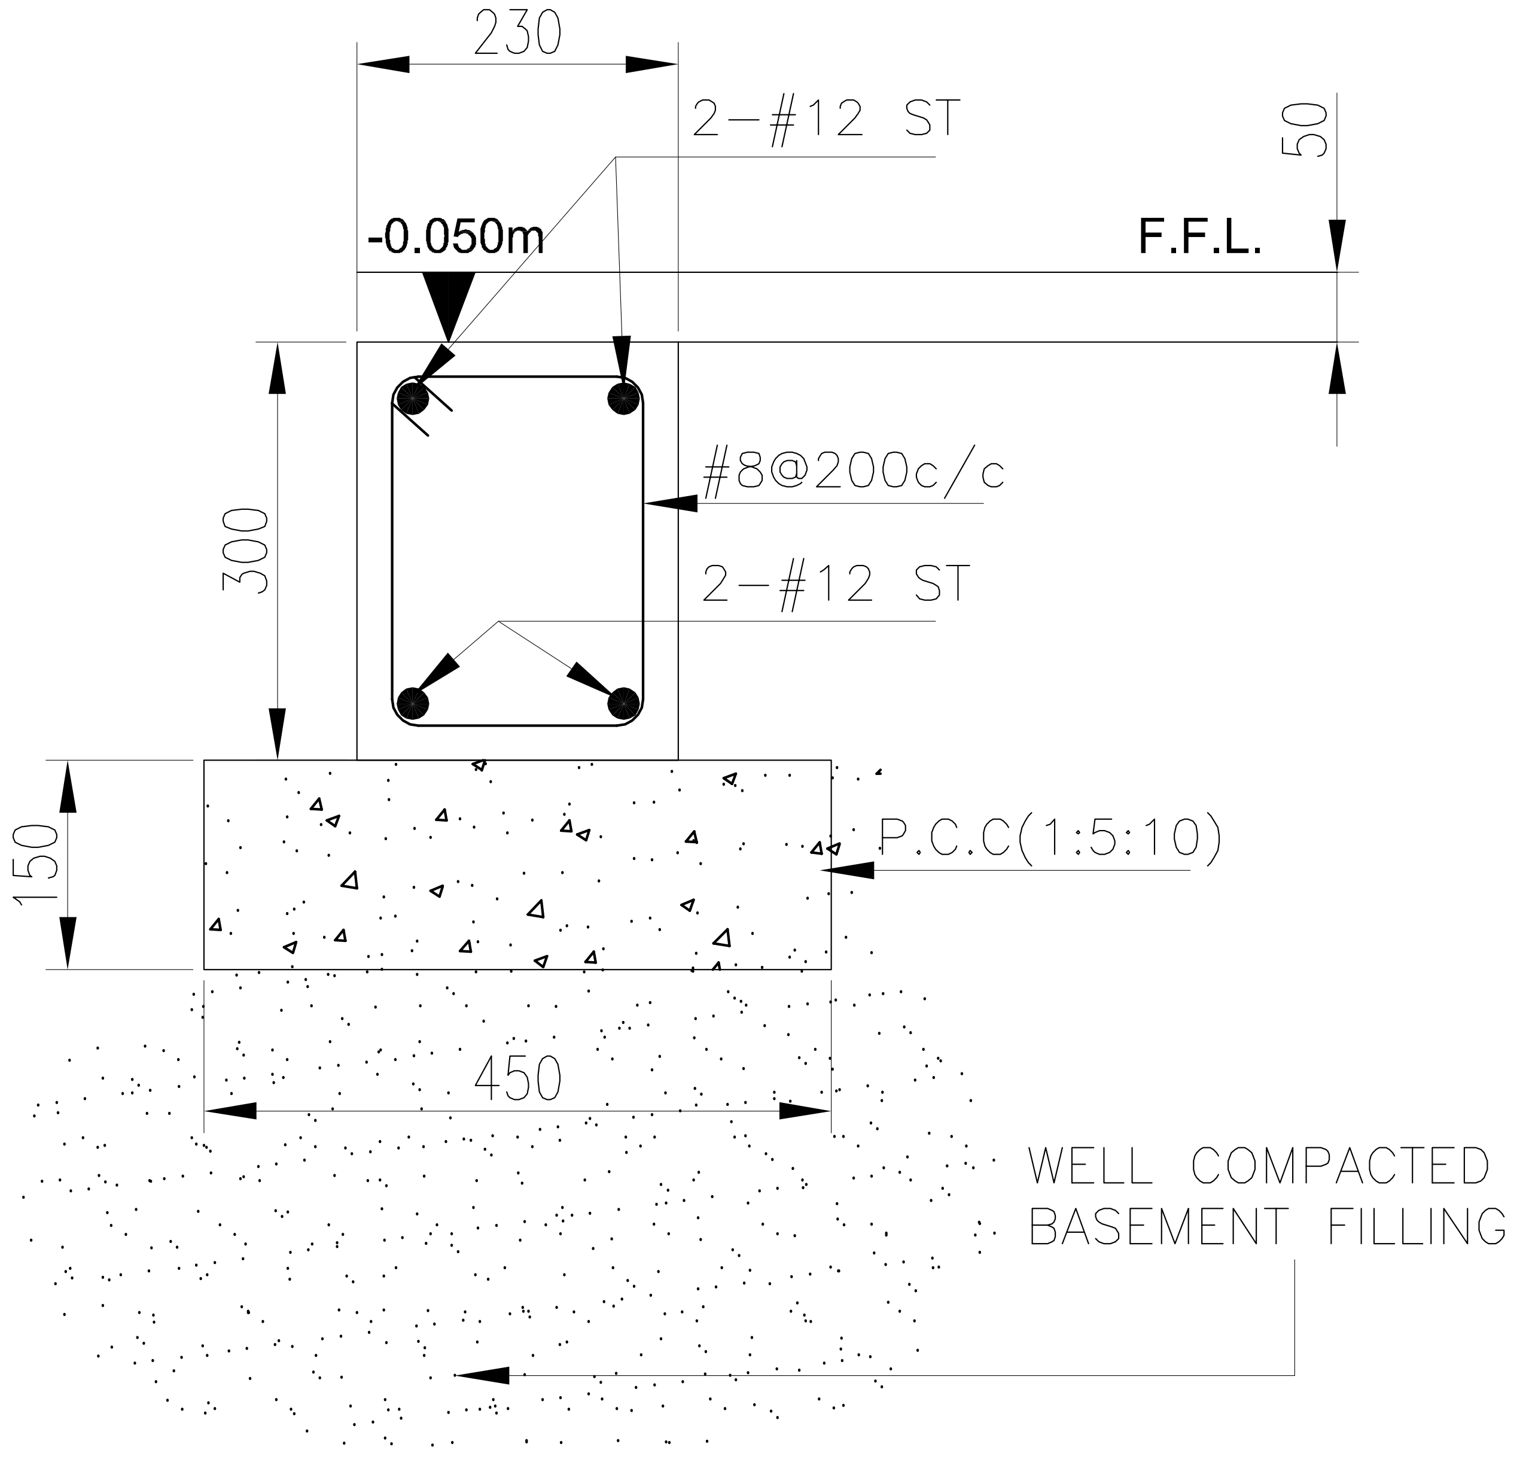
230
2–#12 ST
50
-0.050m
F.F.L.
300
#8@200c/c
2–#12 ST
150
P.C.C(1:5:10)
450
WELL COMPACTED
BASEMENT FILLING

IPB1

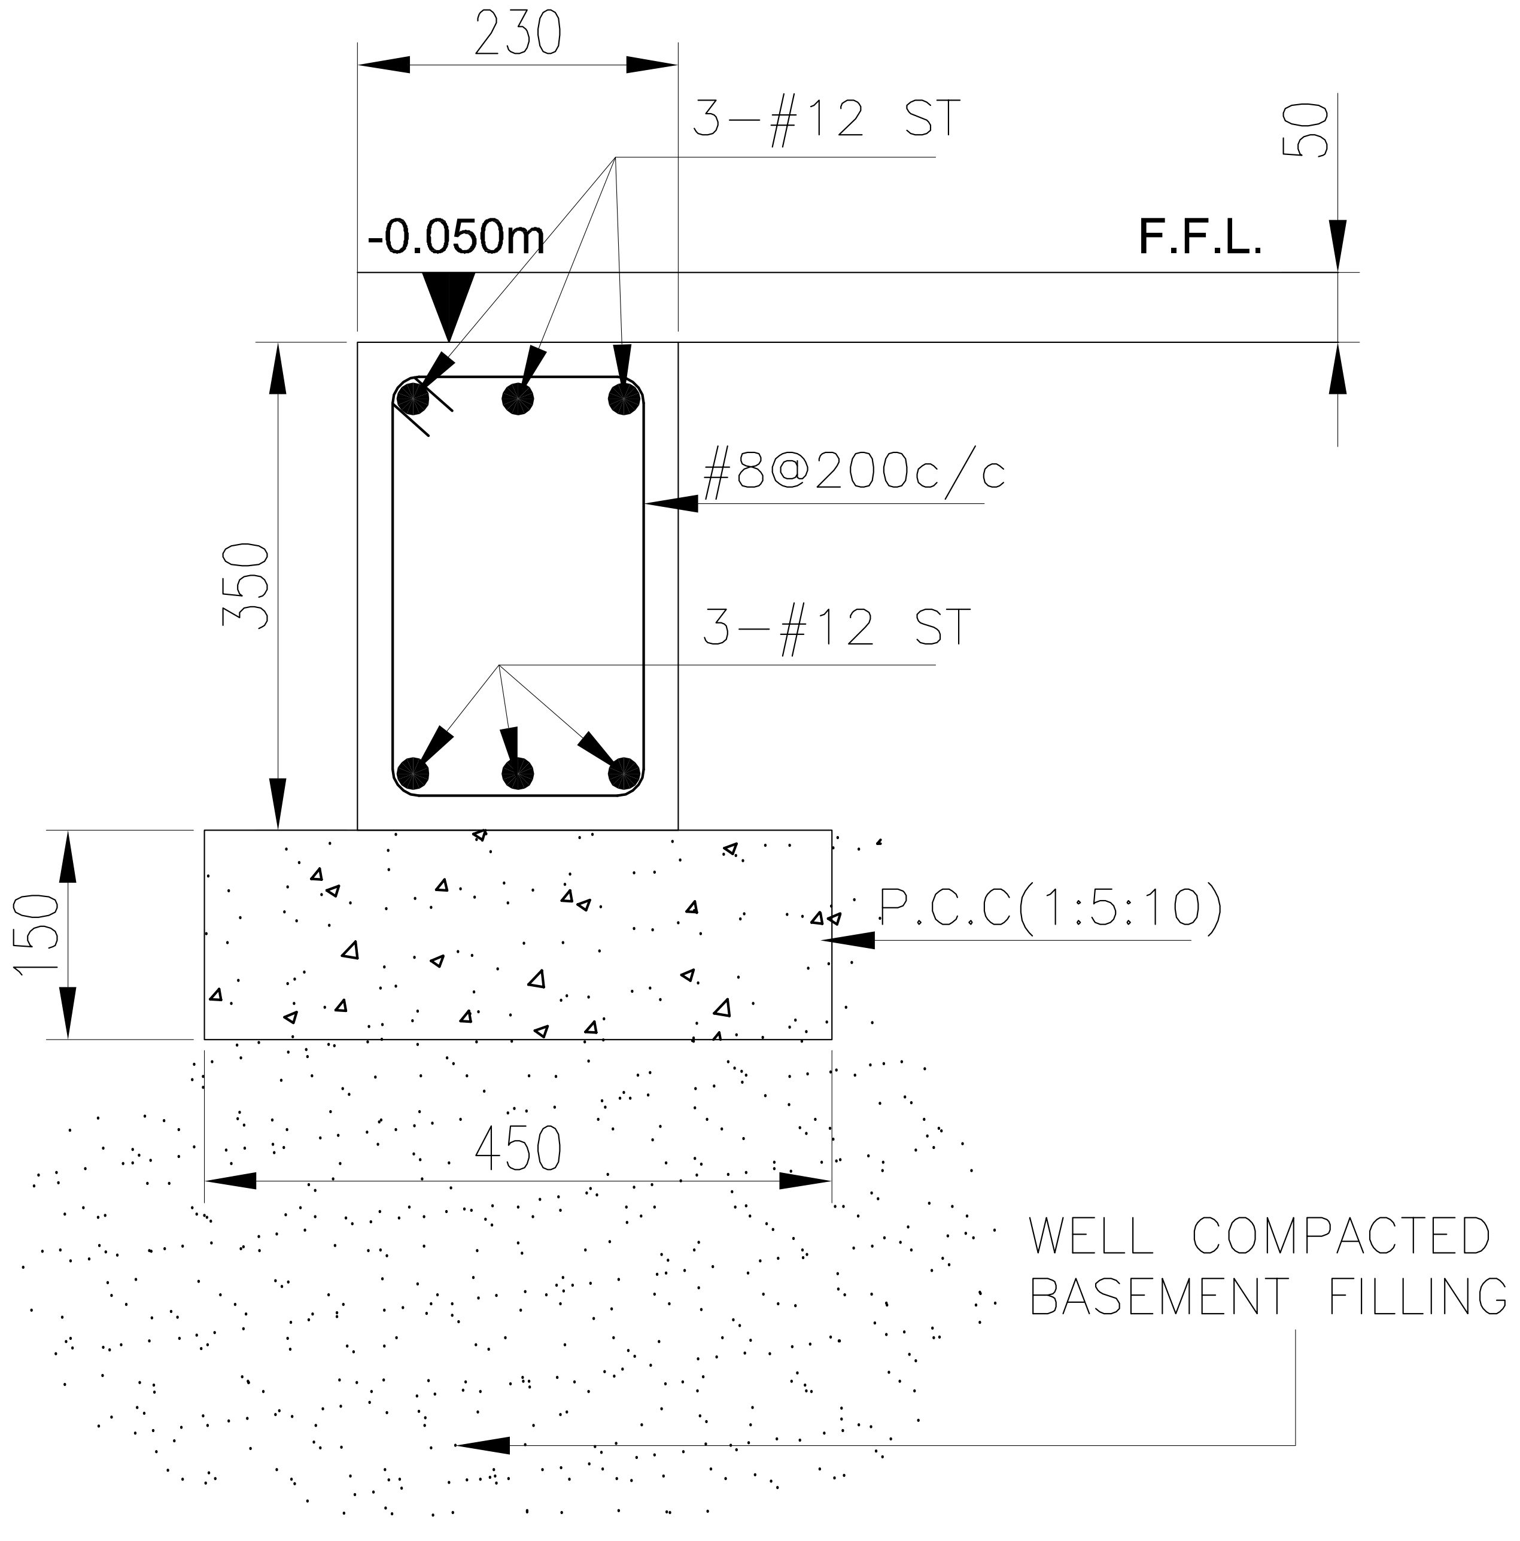
230
3–#12 ST
50
-0.050m
F.F.L.
350
#8@200c/c
3–#12 ST
150
P.C.C(1:5:10)
450
WELL COMPACTED
BASEMENT FILLING

IPB2

- THIS DRAWING SHALL BE READ IN CONJUNCTION WITH ALL RELEVANT ARCHITECTURAL, STRUCTURAL AND SERVICES DRAWINGS. ANY DISCREPANCY NOTICED SHALL BE BROUGHT TO THE ATTENTION OF THE CONSULTANTS AND RESOLVED AS SOON AS POSSIBLE BUT ALWAYS PRIOR TO

ARCHITECTURAL CONSULTANT:

also.
design
a little story of design

STRUCTURAL& MEP CONSULTANTS

JASHRITHA ASSOCIATES
AND MEP PLANNERS
4th FLOOR(4B), HIG 129, KPHB COLONY, KUKATPALLY,
(SUB BRANCH:PR NAGAR ERRAGADDA.)
HYDERABAD 500072, TELANGANA, INDIA
Phone : 9700441106.
E-mail : jashreyansh.consultatns@gmail.com
& jashritha.mep@gmail.com

PROJECT:

ANKURA HOMES_THE WOODS
AT KEESARAGUTTA

DRAWING TITLE:

1625_EAST VILLA
PLINTH BEAM DETAILS

DESIGN ENGG : AJAY	APPROVED :
SCALE : NTS	DRAWN : PK
DATE : 19-09-2026	CHECKED : PRADEEP
DRAWING NO: SD-04	REV.NO:

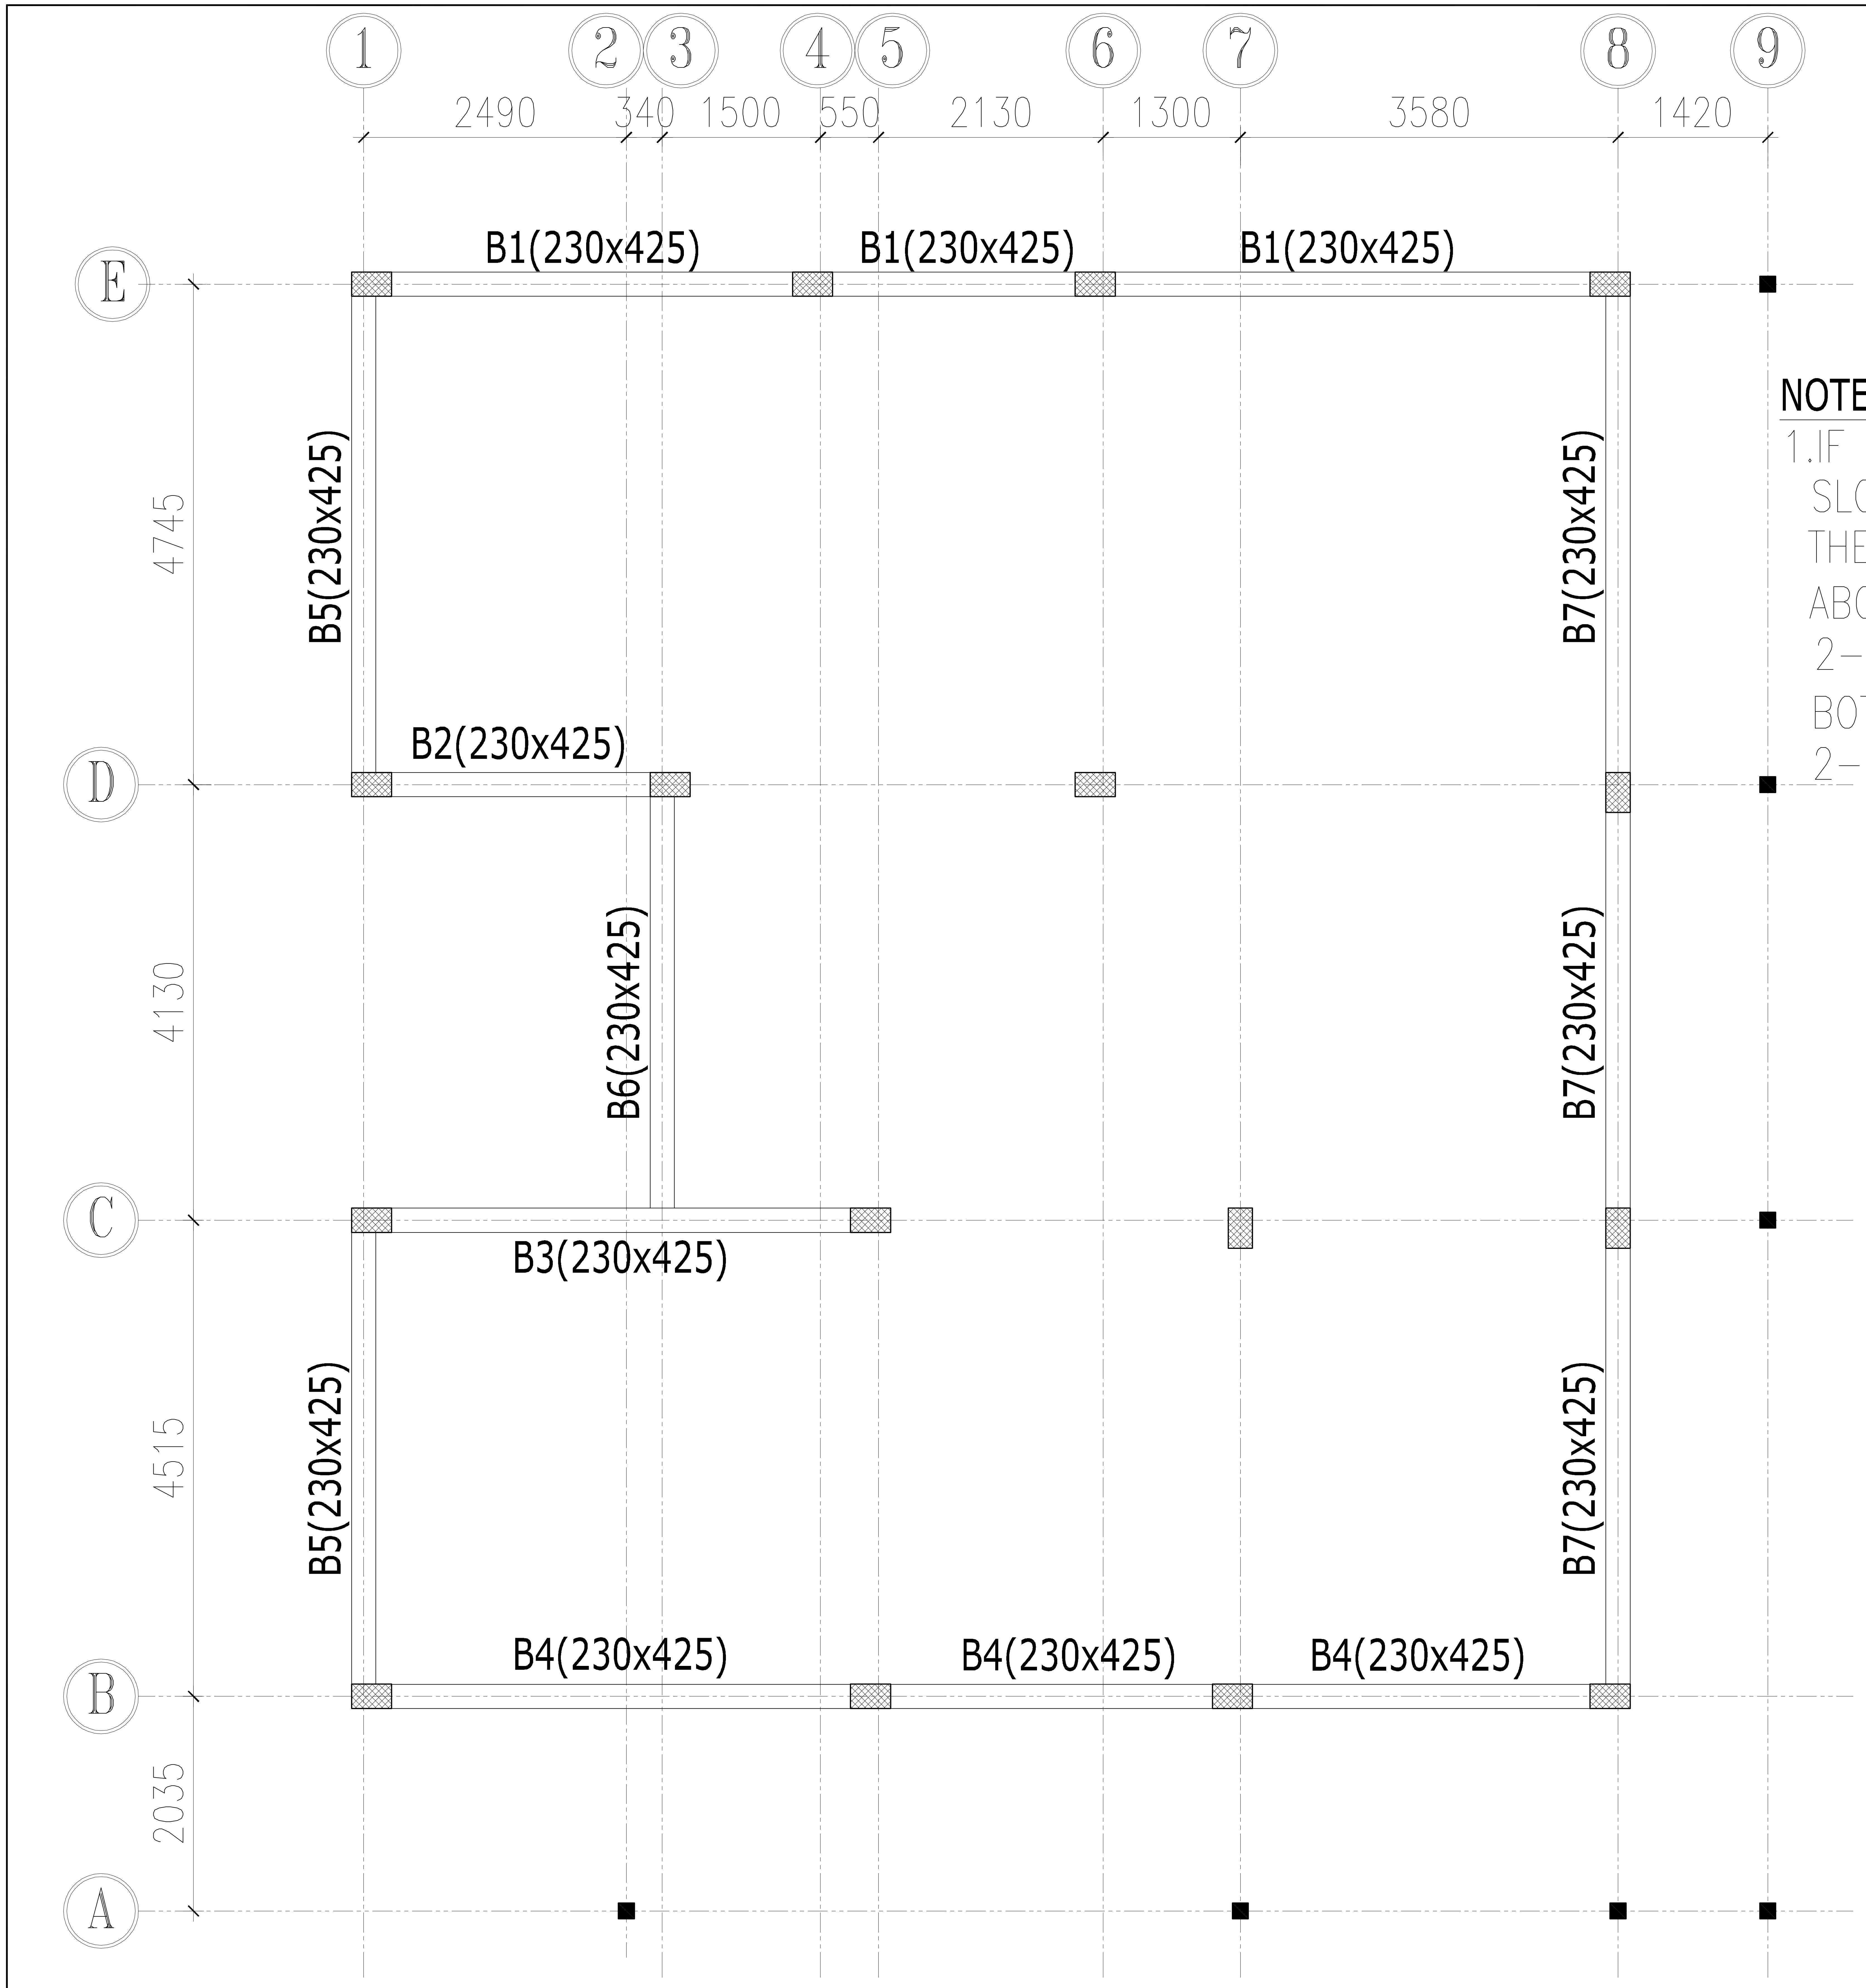
1
2
3
4
5
6
7
8
9
2490
340
1500
550
2130
1300
3580
1420
E
D
C
B
A
4745
4130
4515
2035
B1(230x425)
B1(230x425)
B1(230x425)
B5(230x425)
B2(230x425)
B6(230x425)
B3(230x425)
B5(230x425)
B4(230x425)
B4(230x425)
B4(230x425)
B7(230x425)
B7(230x425)
B7(230x425)

NOTE:

1.IF YOU WANT ANY INTERNAL BEAMS FOR SLOPED ROOF STRUCTURE PLEASE MAINTAIN THE STEEL 2-#16(Top&Bottom) UPTO 3.5M
ABOVE 3.5M SPAN MAINTAIN TOP STEEL
2-#16 ST+ 2-#12 EXT @ SUPPORTS
BOTTOM STEEL
2-#16 ST+ 2-#12 EXT @ MID SPAN

- THIS DRAWING SHALL BE READ IN CONJUNCTION WITH ALL RELEVANT ARCHITECTURAL, STRUCTURAL AND SERVICES DRAWINGS. ANY DISCREPANCY NOTICED SHALL BE BROUGHT TO THE ATTENTION OF THE CONSULTANTS AND RESOLVED AS SOON AS POSSIBLE BUT ALWAYS PRIOR TO

DIRECTION:

ARCHITECTURAL CONSULTANT:

also.
design
a little story of design

STRUCTURAL& MEP CONSULTANTS

JASHRITHA ASSOCIATES
AND MEP PLANNERS
4th FLOOR(4B), HIG 129, KPHB COLONY, KUKATPALLY,
(SUB BRANCH:PR NAGAR ERRAGADDA.)
HYDERABAD 500072, TELANGANA, INDIA
Phone : 9700441106.
E-mail : jashreyansh.consultatns@gmail.com
& jashritha.mep@gmail.com

PROJECT:

ANKURA HOMES_THE WOODS
AT KEESARAGUTTA

DRAWING TITLE:

1625_EAST VILLA
ROOF BEAM LAYOUT

DESIGN ENGG : AJAY	APPROVED :
SCALE : NTS	DRAWN : PK
DATE : 23-09-2026	CHECKED : PRADEEP

DRAWING NO: SD-05
REV.NO: 01

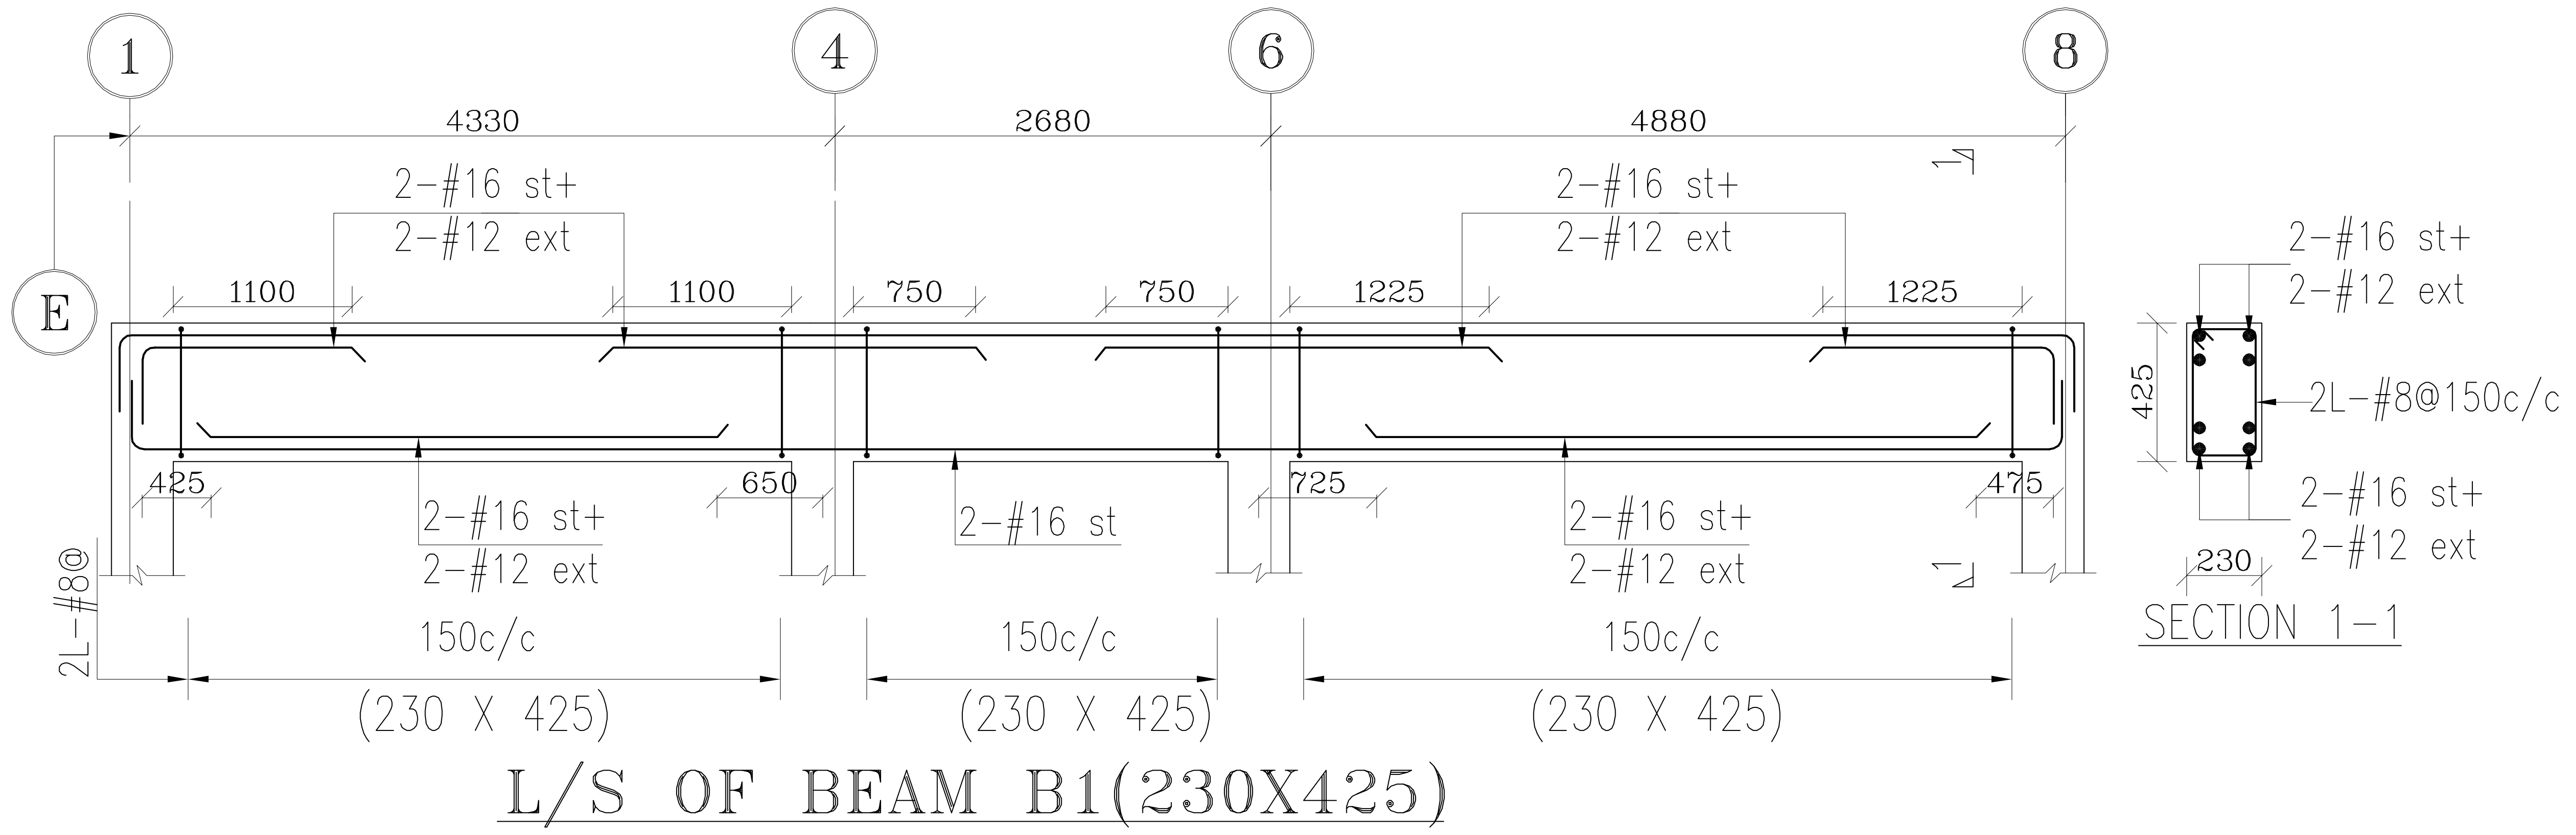
1
4
6
8
E
4330
2680
4880
2-#16 st+
2-#12 ext
1100
1100
750
750
1225
1225
425
650
725
475
2-#16 st
2L-#8@
150c/c
(230 X 425)
1
425
230
2L-#8@150c/c
SECTION 1-1

L/S OF BEAM B1(230X425)

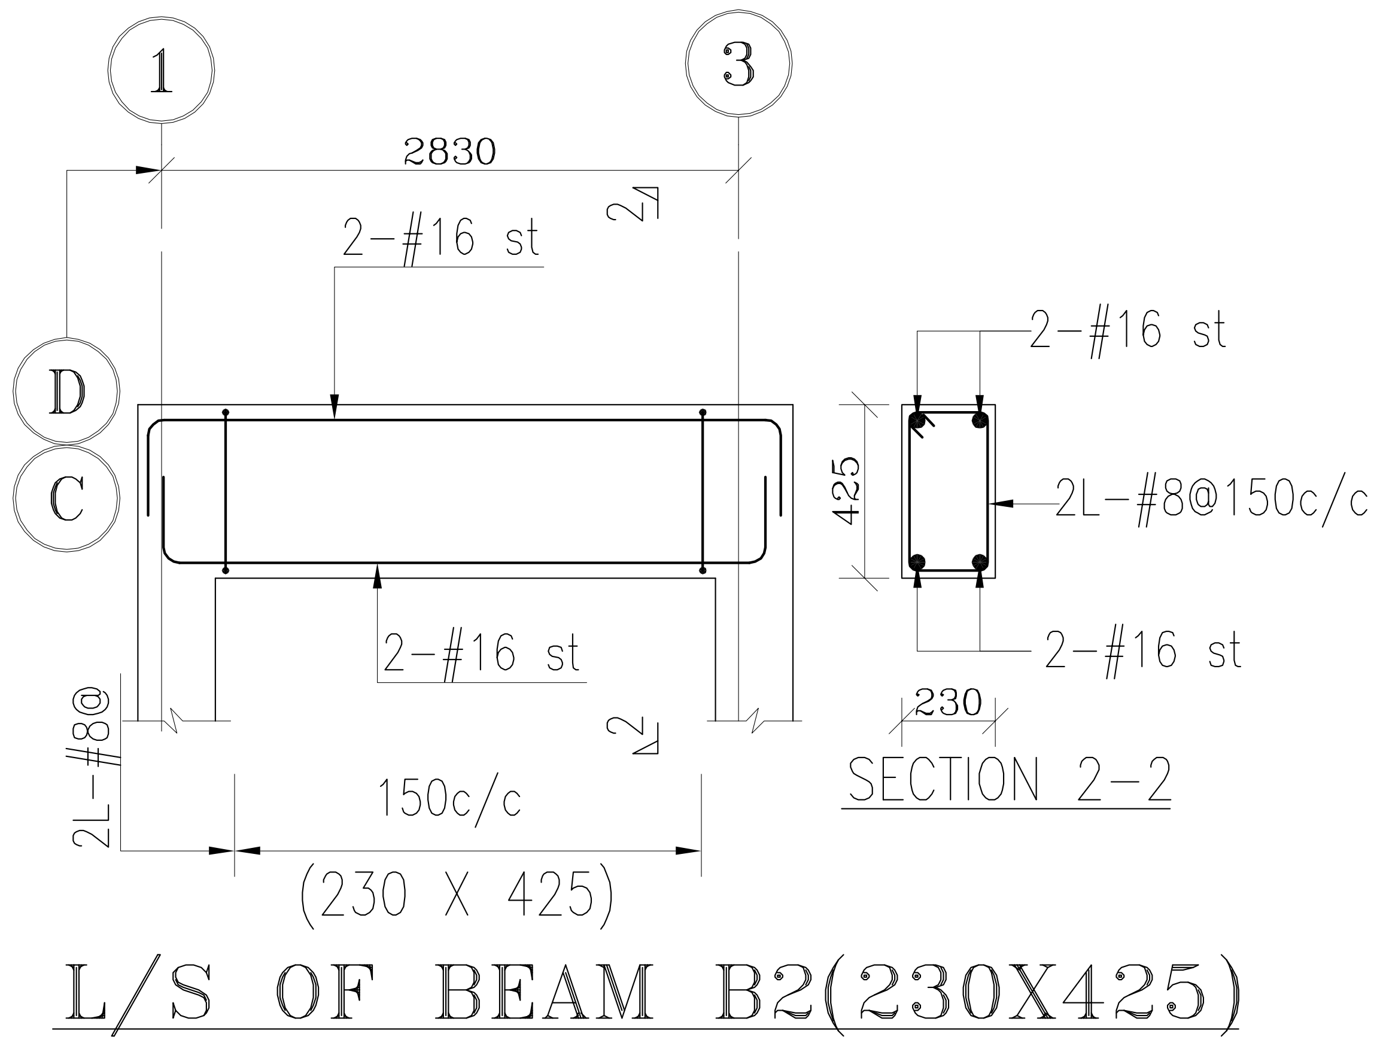
1
3
D
C
2830
2-#16 st
2
2L-#8@
150c/c
(230 X 425)
425
230
2L-#8@150c/c
SECTION 2-2

L/S OF BEAM B2(230X425)

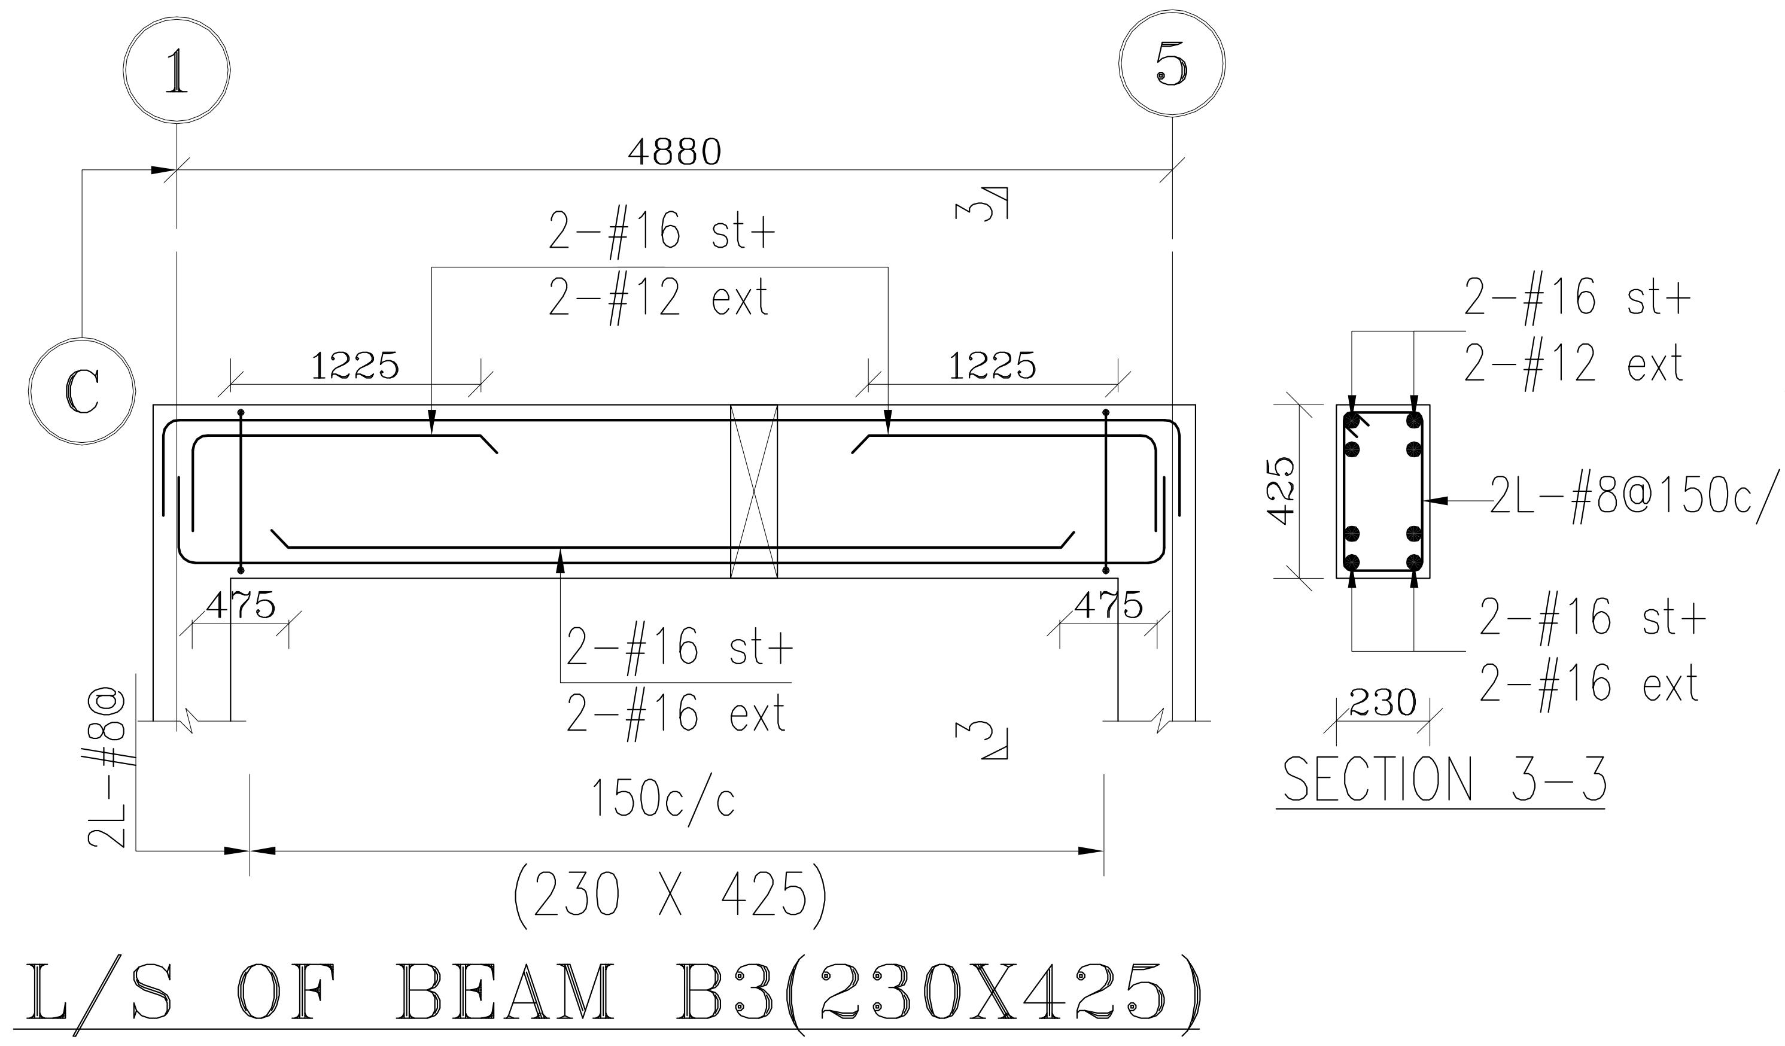
1
5
C
4880
2-#16 st+
2-#12 ext
1225
1225
475
475
2-#16 st+
2-#16 ext
3
2L-#8@
150c/c
(230 X 425)
425
230
2L-#8@150c/c
SECTION 3-3

L/S OF BEAM B3(230X425)

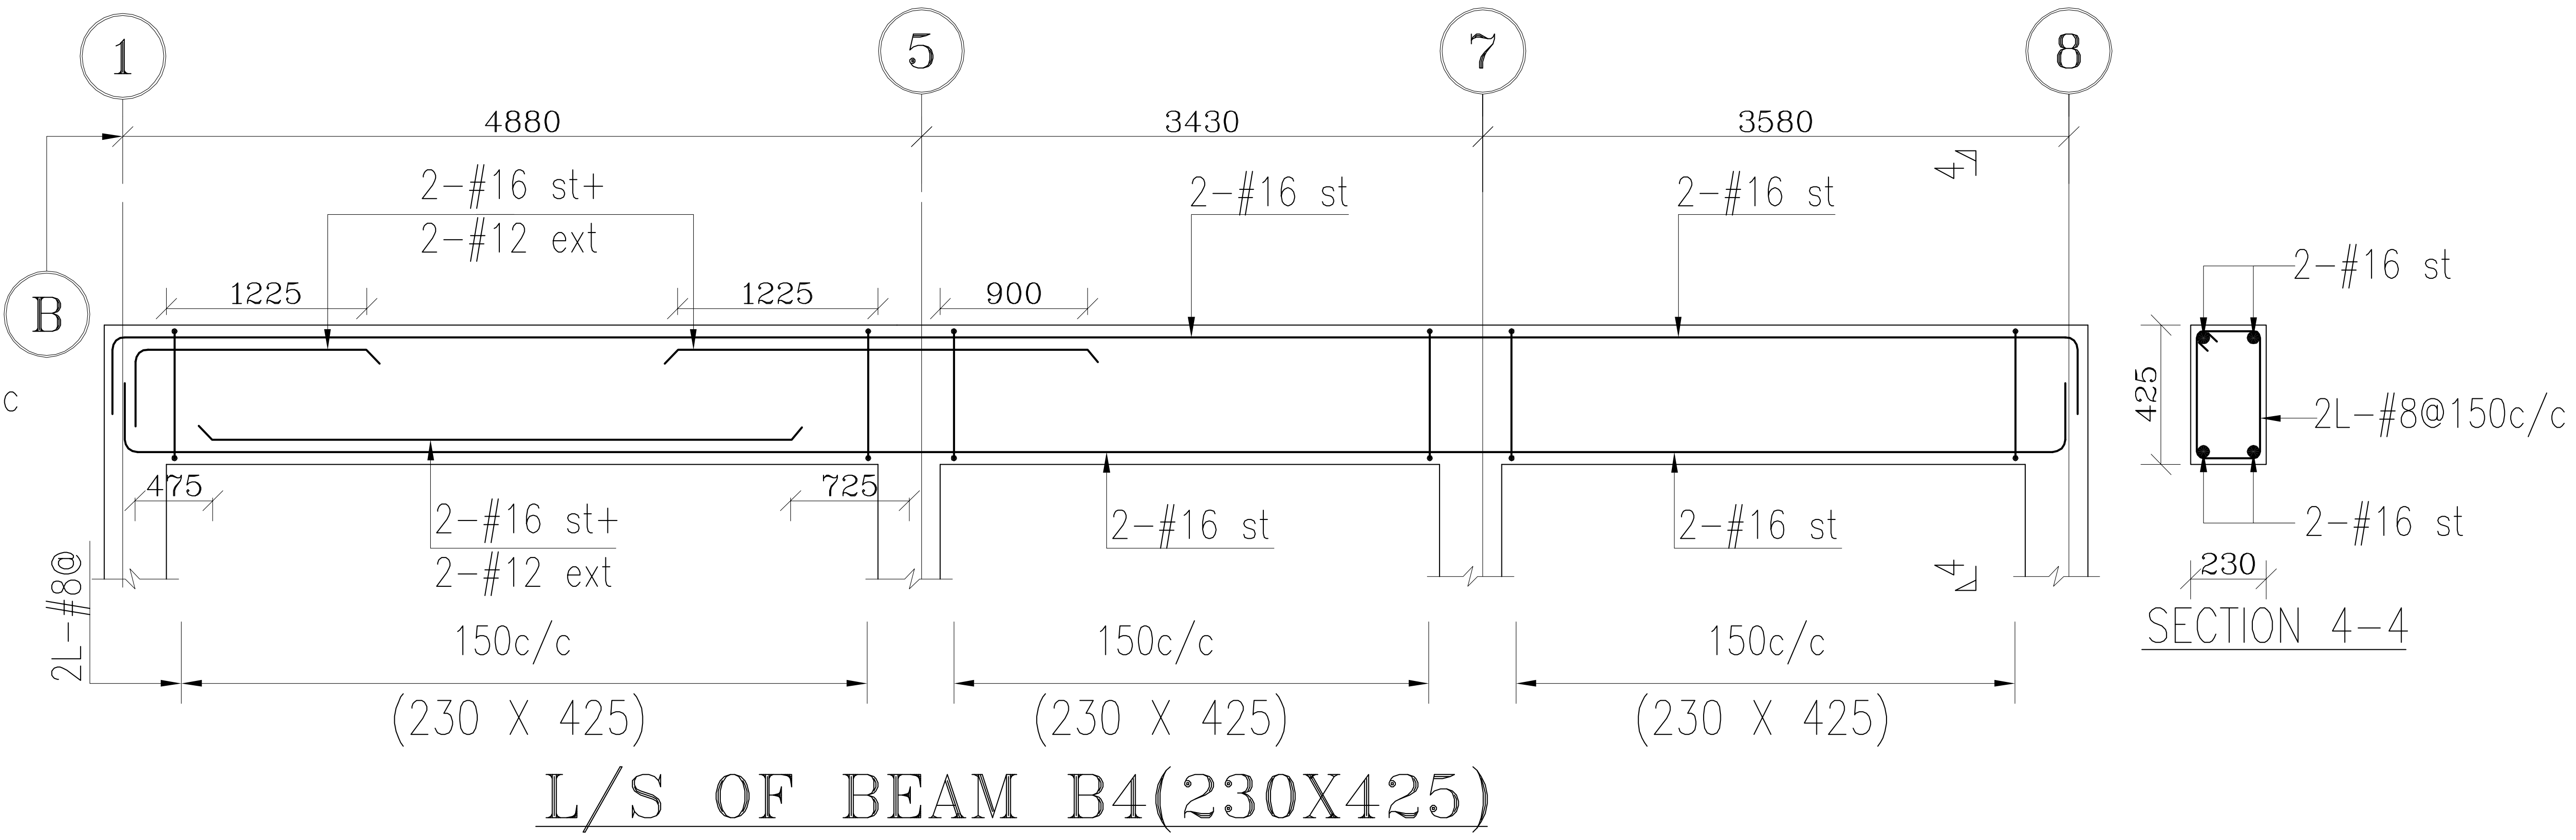
1
5
7
8
B
4880
3430
3580
2-#16 st+
2-#12 ext
2-#16 st
1225
1225
900
475
725
4
2L-#8@
150c/c
(230 X 425)
425
230
2L-#8@150c/c
SECTION 4-4

L/S OF BEAM B4(230X425)

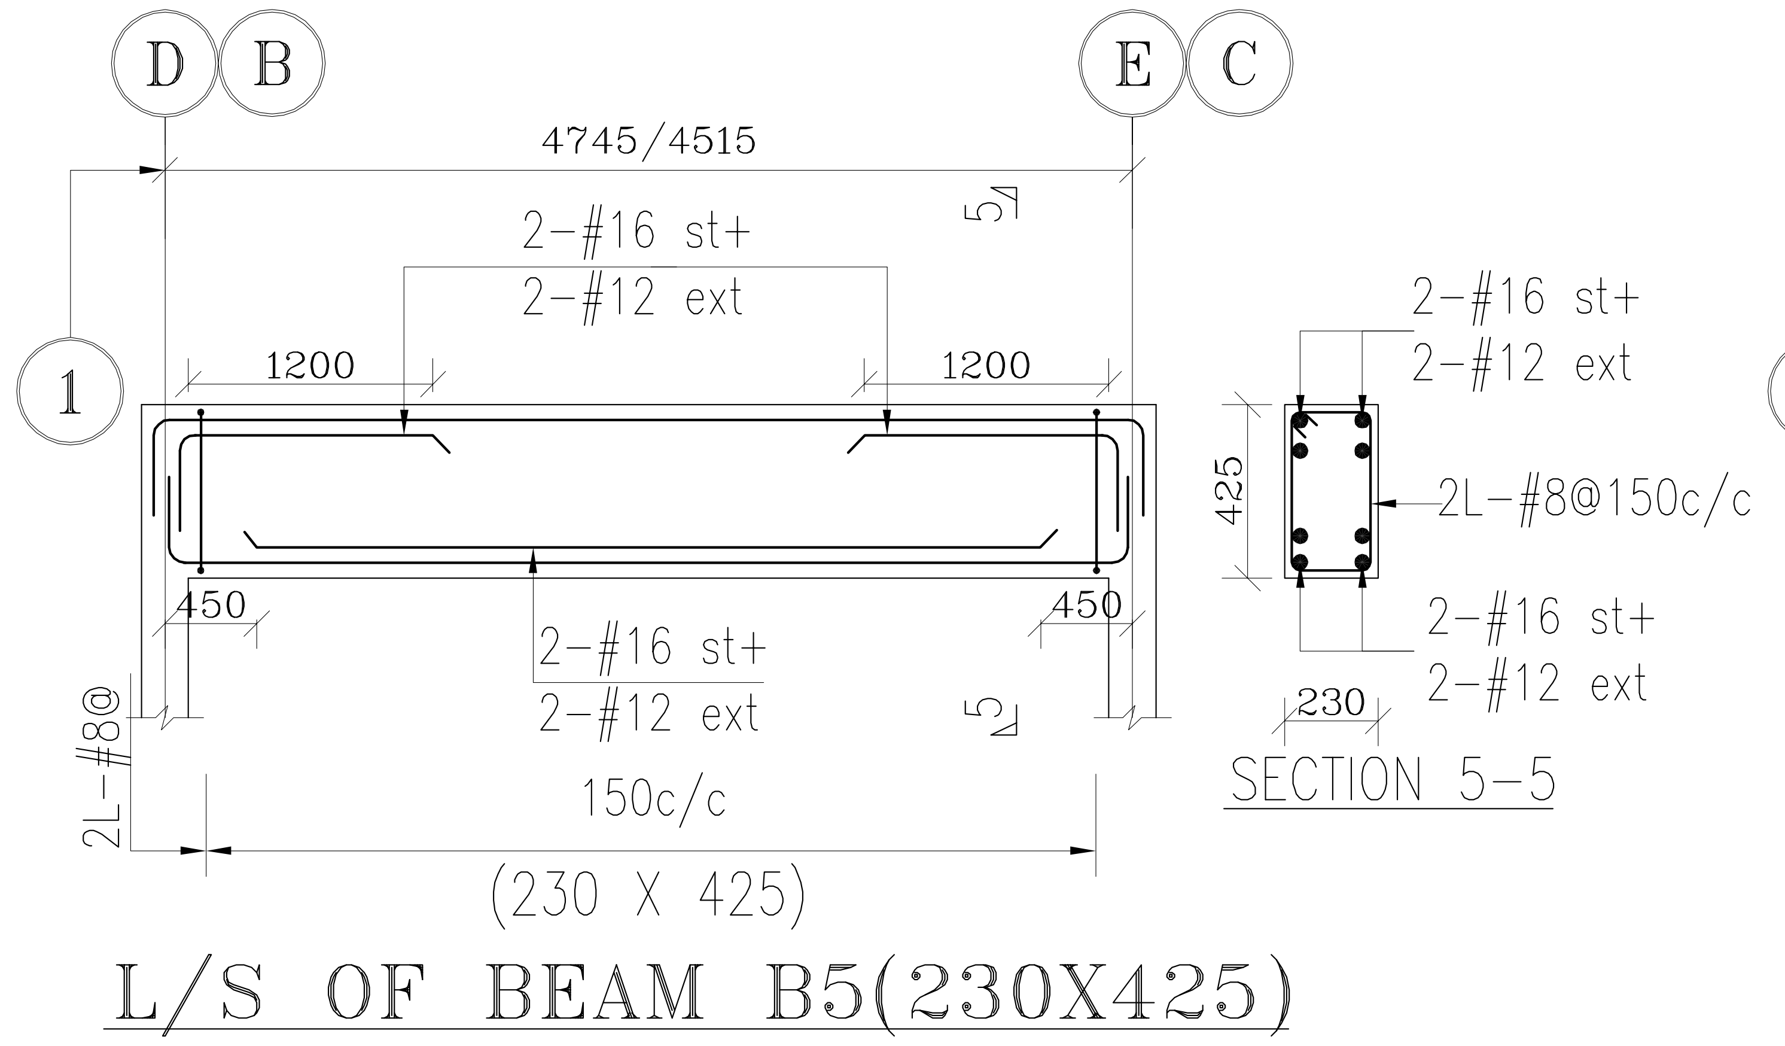
D
B
E
C
1
4745/4515
2-#16 st+
2-#12 ext
1200
1200
450
450
5
2L-#8@
150c/c
(230 X 425)
425
230
2L-#8@150c/c
SECTION 5-5

L/S OF BEAM B5(230X425)

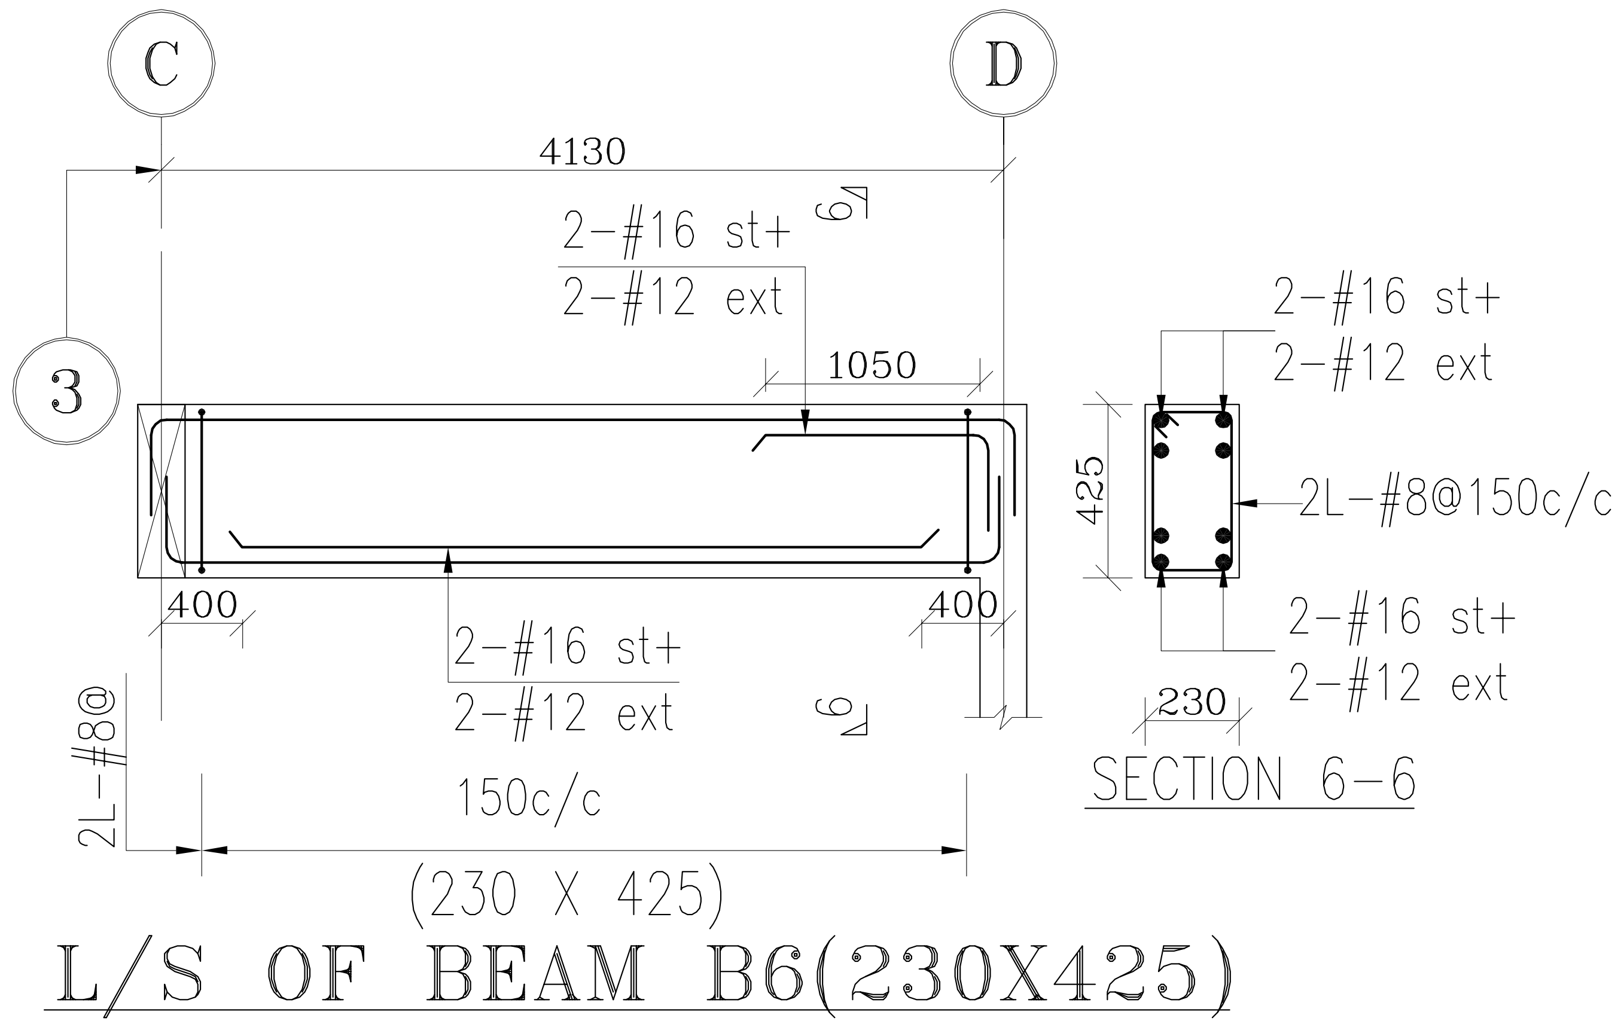
C
D
3
4130
2-#16 st+
2-#12 ext
1050
400
400
6
2L-#8@
150c/c
(230 X 425)
425
230
2L-#8@150c/c
SECTION 6-6

L/S OF BEAM B6(230X425)

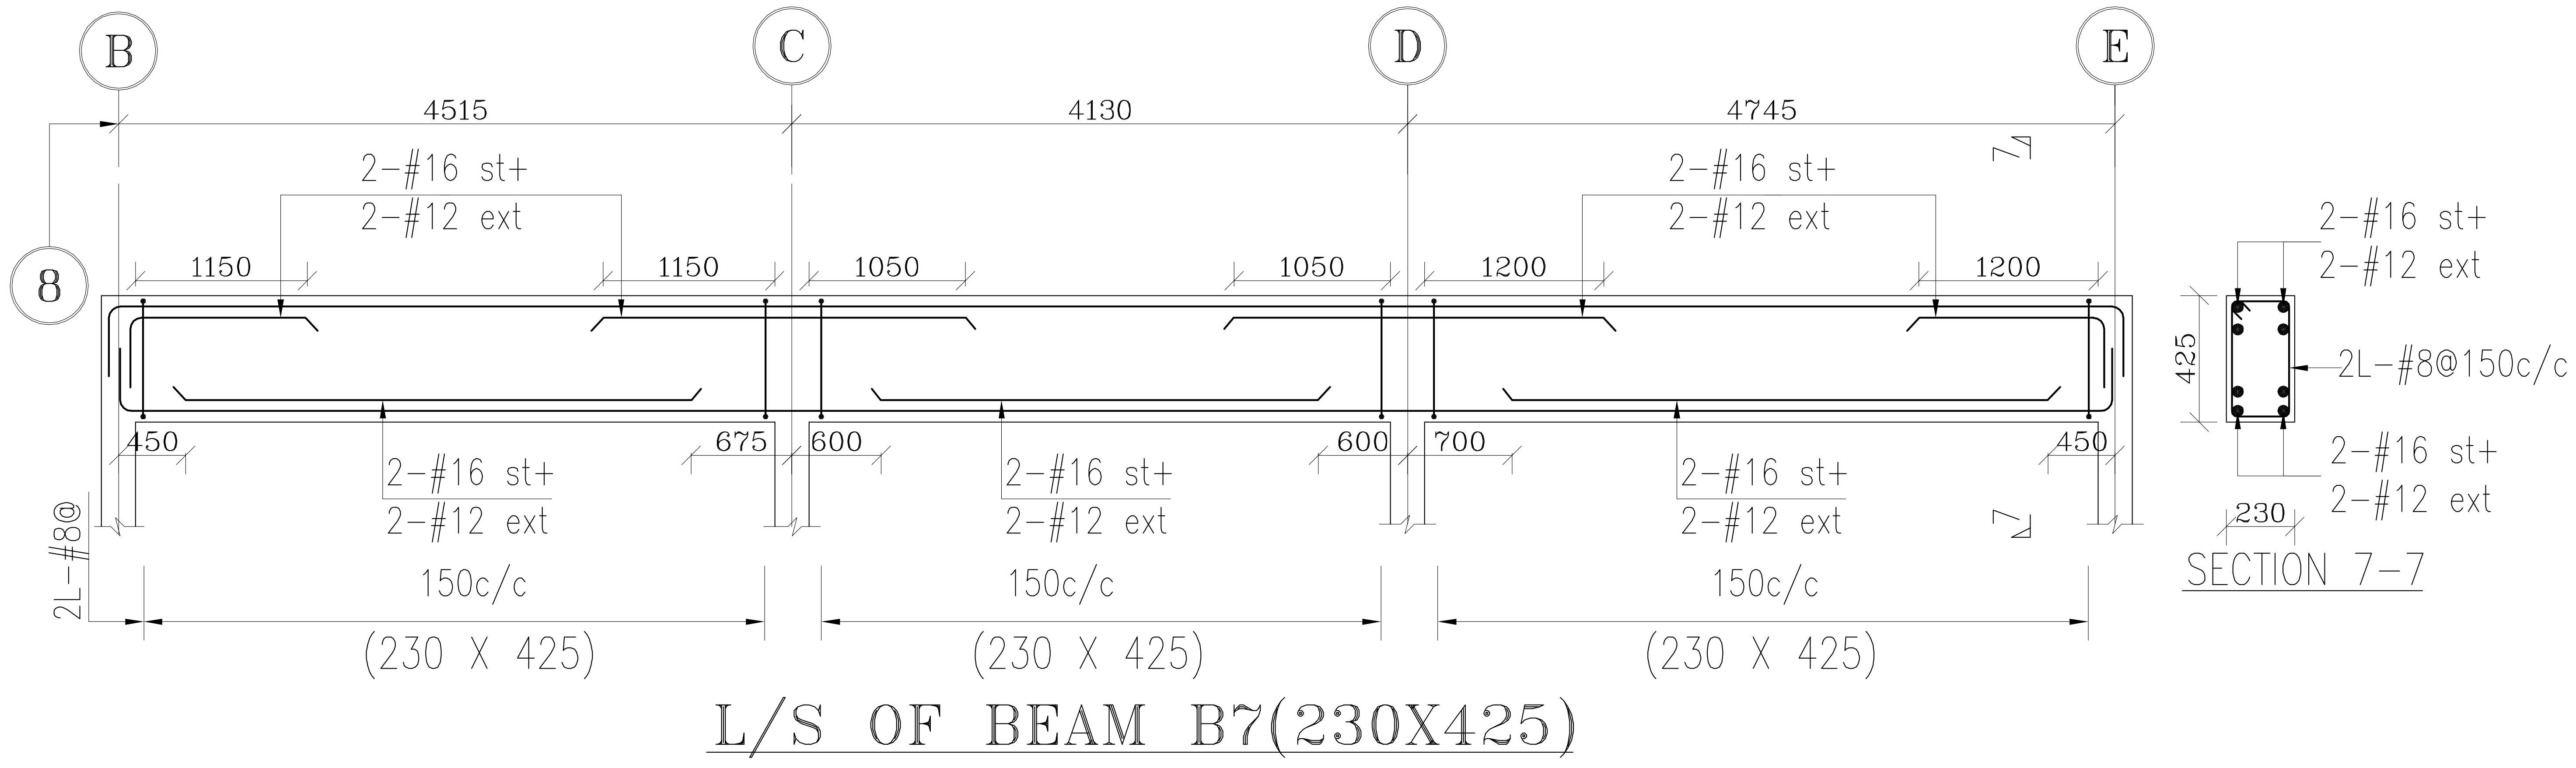
B
C
D
E
8
4515
4130
4745
2-#16 st+
2-#12 ext
1150
1150
1050
1050
1200
1200
450
675
600
600
700
450
7
2L-#8@
150c/c
(230 X 425)
425
230
2L-#8@150c/c
SECTION 7-7

L/S OF BEAM B7(230X425)

- THIS DRAWING SHALL BE READ IN CONJUNCTION WITH ALL RELEVANT ARCHITECTURAL, STRUCTURAL AND SERVICES DRAWINGS. ANY DISCREPANCY NOTICED SHALL BE BROUGHT TO THE ATTENTION OF THE CONSULTANTS AND RESOLVED AS SOON AS POSSIBLE BUT ALWAYS PRIOR TO

DIRECTION:

N

ARCHITECTURAL CONSULTANT:

also.
design
a little story of design

STRUCTURAL& MEP CONSULTANTS

JASHRITHA ASSOCIATES
AND MEP PLANNERS
4th FLOOR(4B), HIG 129, KPHB COLONY, KUKATPALLY,
(SUB BRANCH:PR NAGAR ERRAGADDA.)
HYDERABAD 500072, TELANGANA, INDIA
Phone : 9700441106.
E-mail : jashreyansh.consultatns@gmail.com
& jashritha.mep@gmail.com

PROJECT:

ANKURA HOMES_THE WOODS
AT KEESARAGUTTA

DRAWING TITLE:

1625_EAST VILLA
ROOF BEAM DETAILS

DESIGN ENGG : AJAY	APPROVED :
SCALE : NTS	DRAWN : PK
DATE : 23-09-2026	CHECKED : PRADEEP
DRAWING NO: SD-06	REV.NO: 01