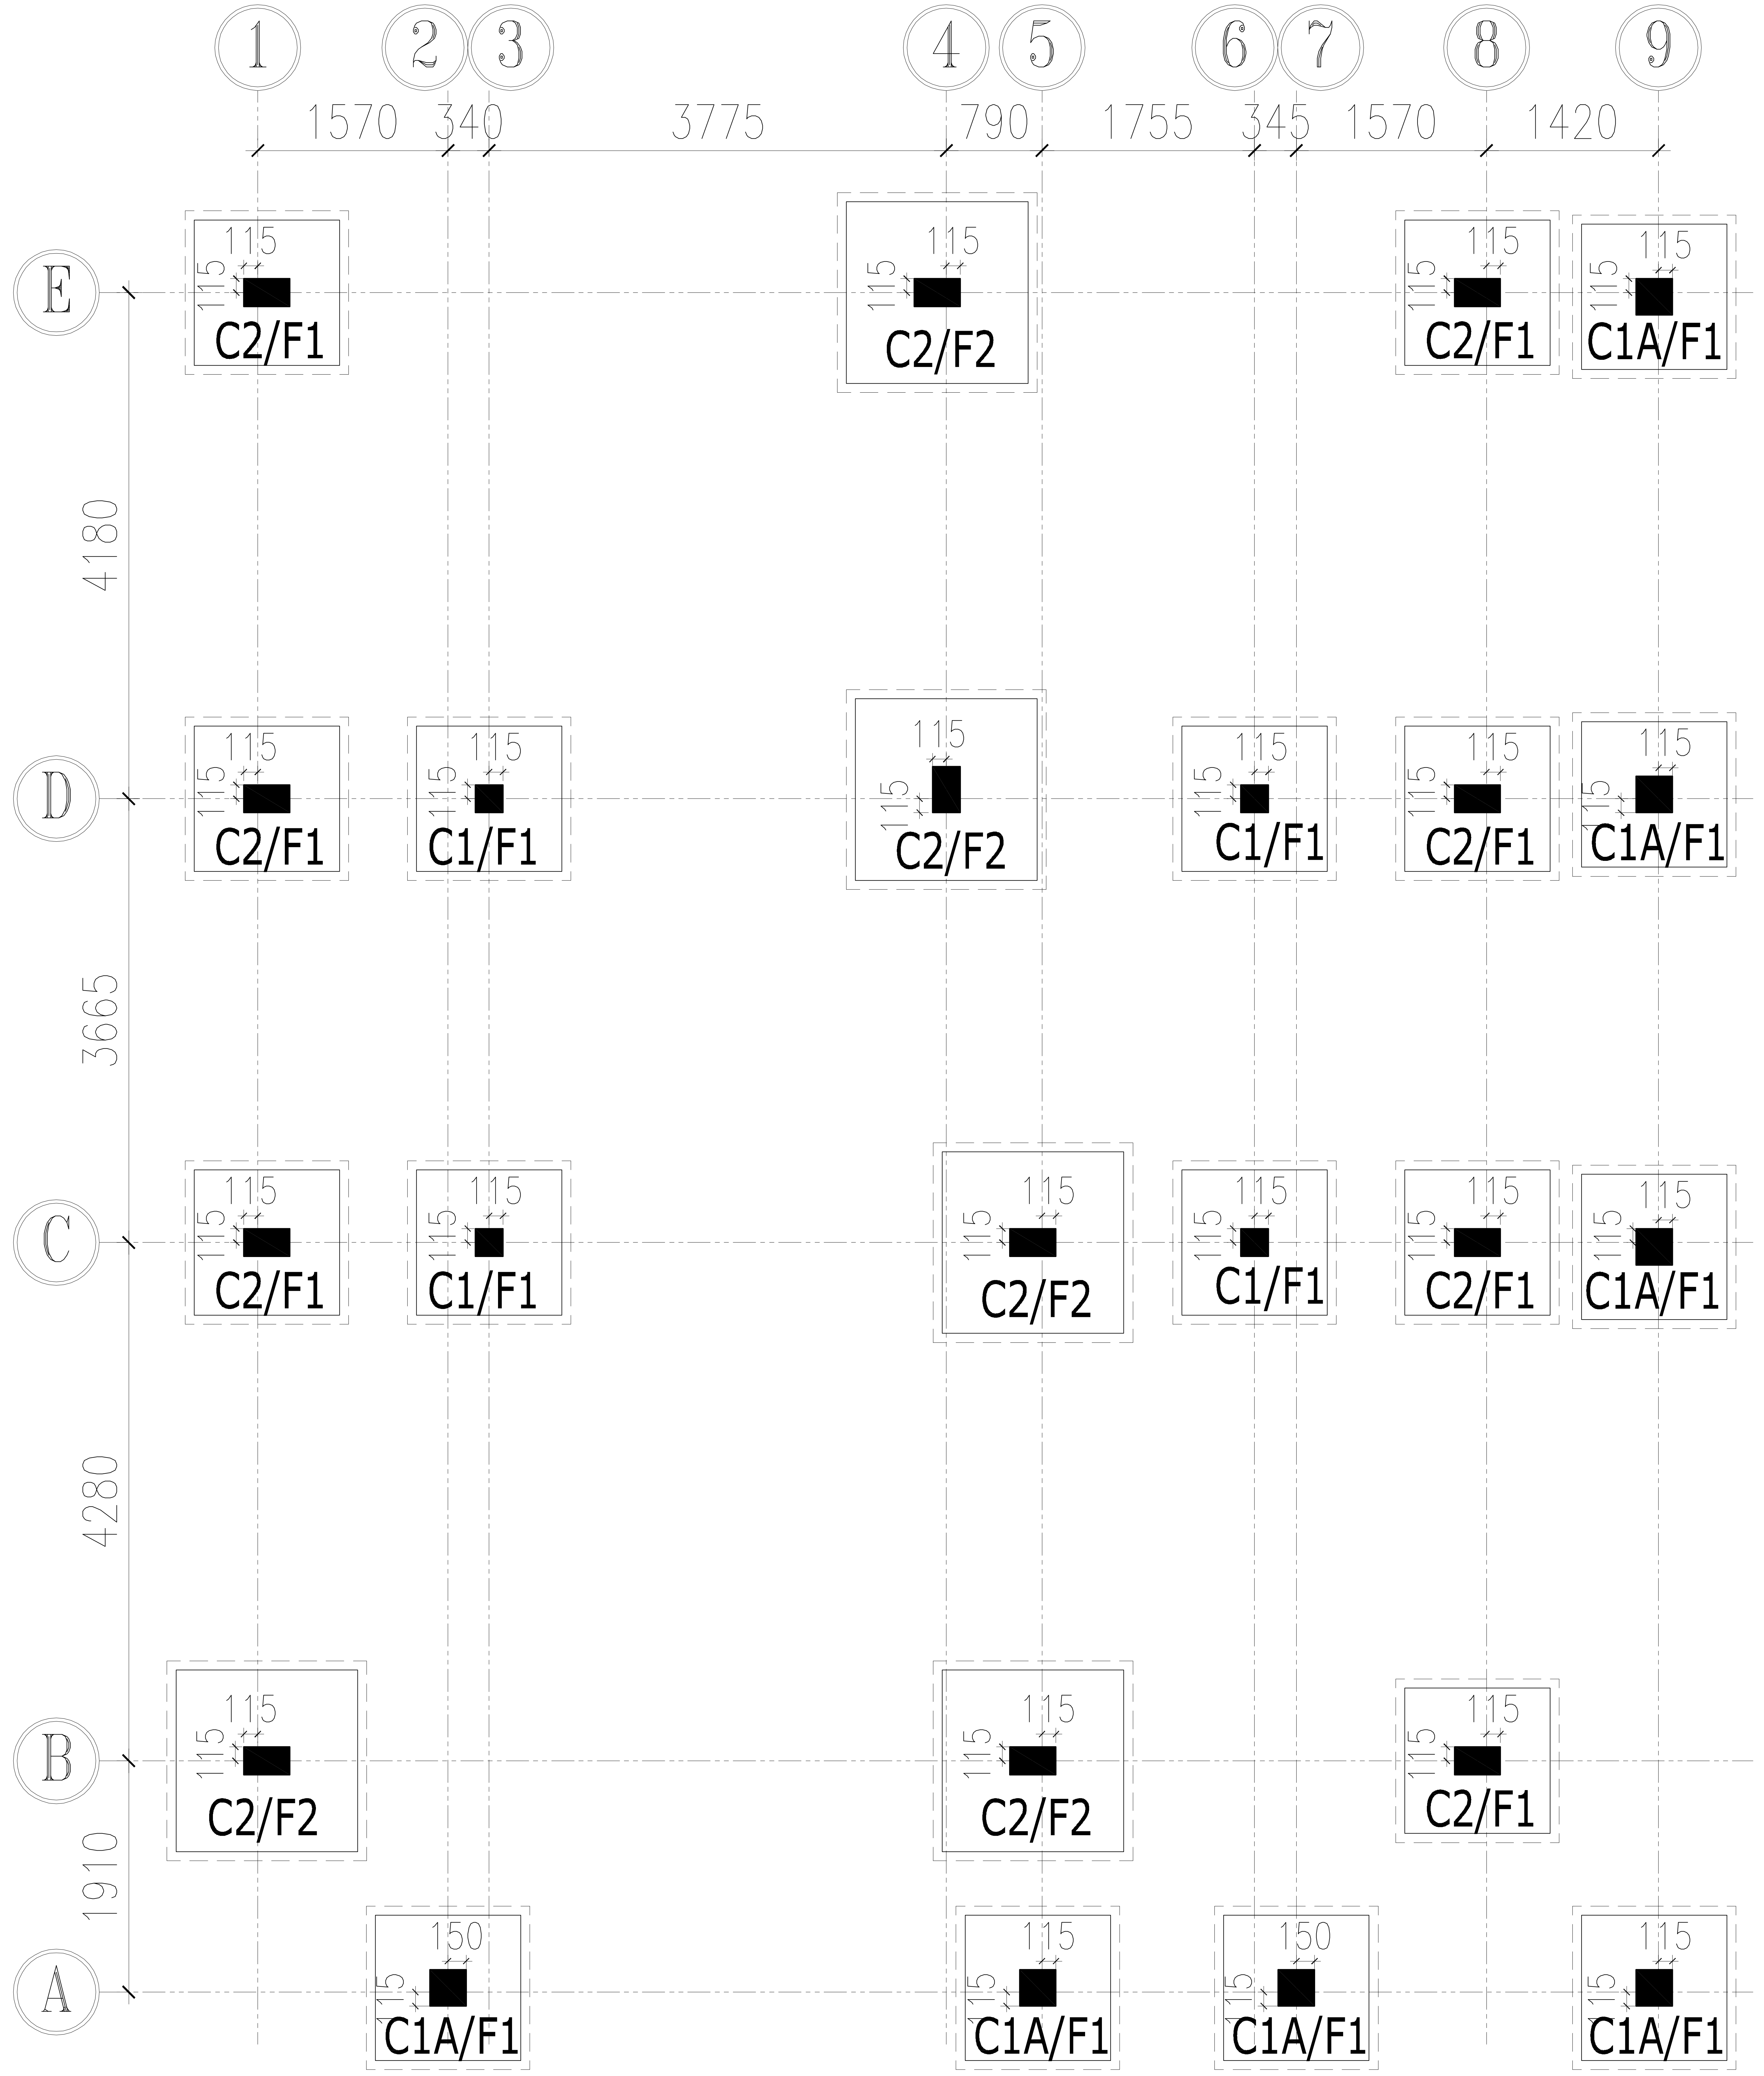

- THIS DRAWING SHALL BE READ IN CONJUNCTION WITH ALL RELEVANT ARCHITECTURAL, STRUCTURAL AND SERVICES DRAWINGS. ANY DISCREPANCY NOTICED SHALL BE BROUGHT TO THE ATTENTION OF THE CONSULTANTS AND RESOLVED AS SOON AS POSSIBLE BUT ALWAYS PRIOR TO

DIRECTION:

N

ARCHITECTURAL CONSULTANT:

also. design

a little story of design

STRUCTURAL& MEP CONSULTANTS

JASHRITHA ASSOCIATES
AND MEP PLANNERS
4th FLOOR(4B), HIG 129, KPHB COLONY, KUKATPALLY,
(SUB BRANCH:PR NAGAR ERRAGADDA.)
HYDERABAD 500072, TELANGANA, INDIA
Phone : 9700441106.
E-mail : jashreyansh.consultatns@gmail.com
& jashritha.mep@gmail.com

PROJECT:

ANKURA HOMES_THE WOODS
AT KEESARAGUTTA

DRAWING TITLE:

1215_EAST VILLA
MARKING PLAN

DESIGN ENGG :	AJAY	APPROVED :	
SCALE :	NTS	DRAWN : PK	
DATE :	07-10-2026	CHECKED : PRADEEP	
DRAWING NO:	SD-01	REV.NO:	01

COLUMN SCHEDULE

COLUMN ID	GRADE OF CONCRETE	COLUMN SIZE UPTO GROUND FLOOR ROOF	REFERENCE SECTION
C1	M - 25	230 x 230 #12 -4Nos	A1
C1A	M - 25	300 x 300 #12 -4Nos	A1
C2	M - 25	230 x 380 #16 -4Nos + #12 -4Nos	A2

ARRANGEMENT OF TIES, LINKS & MAIN BARS IN COLUMN

4 BARS ARRANGEMENT	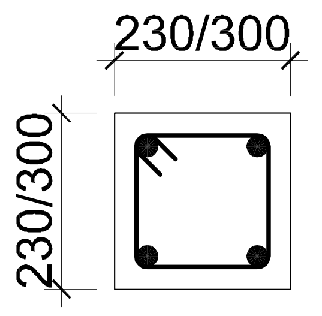 4 EQUAL DIA (A1)	8 BARS ARRANGEMENT	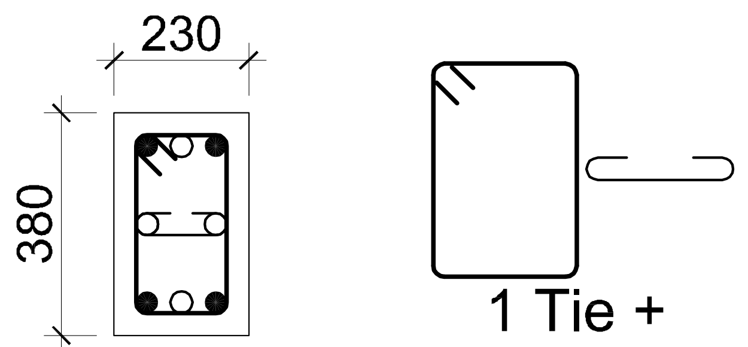 • 4 LARGER DIA ○ 4 LARGER DIA (A2) 1 Tie + 1 Link #8 @150c/c

FLAT FOOTING SCHEDULE:

GROUP	MIX	SIZE	DEPTH	BOTTOM REINFORCEMENT PARALLEL TO	
				SHORTER DIRECTION	LONGER DIRECTION
F1	M - 25	1200 x 1200	375	#10 -10 NOS	#10 -10 NOS
F2	M - 25	1500 x 1500	400	#10 -15 NOS	#10 -15 NOS

GENERAL NOTES:

1. DO NOT SCALE THIS DRAWING. FOLLOW FIGURED DIMENSIONS ONLY.
2. ALL DIMENSIONS ARE IN MM ONLY AND LEVELS ARE IN METERS UNLESS SPECIFIED.
3. S.B.C OF SOIL IS CONSIDERED AS 270 KN/M^2 @ 2.0M DEPTH
4. USE VIBRATED REINFORCED CONCRETE CONFORMING TO IS:456-2000. THE GRADES FOR DIFFERENT COMPONENTS ARE AS FOLLOWS

COMPONENT	FOOTING	COLUMNS	BEAMS	SLABS	WATER TANK SIDE WALLS
MIX	M25	M25	M25	M25	M25

5. GRADE OF STEEL SHALL BE Fe 500 CONFORMING TO IS:1786-85 & AMENDMENTS.
6. LAPS SHALL BE STAGGERED AND LAP LENGTHS ARE AS FOLLOWS.

MIX	M25
Ld	48 Dia

7. NOT MORE THAN 50% OF COLUMN REINFORCEMENT SHALL BE LAPPED AT A PARTICULAR LOCATION.
8. CLEAR COVERS ARE AS FOLLOWS

FOOTING TO MAIN BAR	COLUMN TO MAIN BAR	BEAMS TO STIRRUPS	SLABS TO MAIN BAR
50mm	40mm	20mm	20mm

9. CURING SHOULD BE DONE ATLEAST FOR 21 DAYS.
10. THIS DRAWING SHOULD BE READ IN CONJUNCTION WITH RELEVANT ARCHITECTURAL DRAWINGS.
11. STRIPPING TIME OF FORMWORK SHALL CONFORM TO CLAUSE 11.3 OF IS:456-2000.
12. FOR TIES,LINKS IN COLUMNS Y8-150mm c/c REFER COLUMN SCHEDULE DWG.
13. FOR EXACT LOCATION OF WALLS REFER RELEVANT ARCHITECTURAL DRAWINGS FOR NECESSARY DETAILS.
14. ANY DISCREPANCY FROM THE DRAWING SHALL BE BROUGHT TO THE NOTICE OF CONSULTANTS.
15. THE STRUCTURE IS DESIGNED FOR GROUND FLOOR ONLY

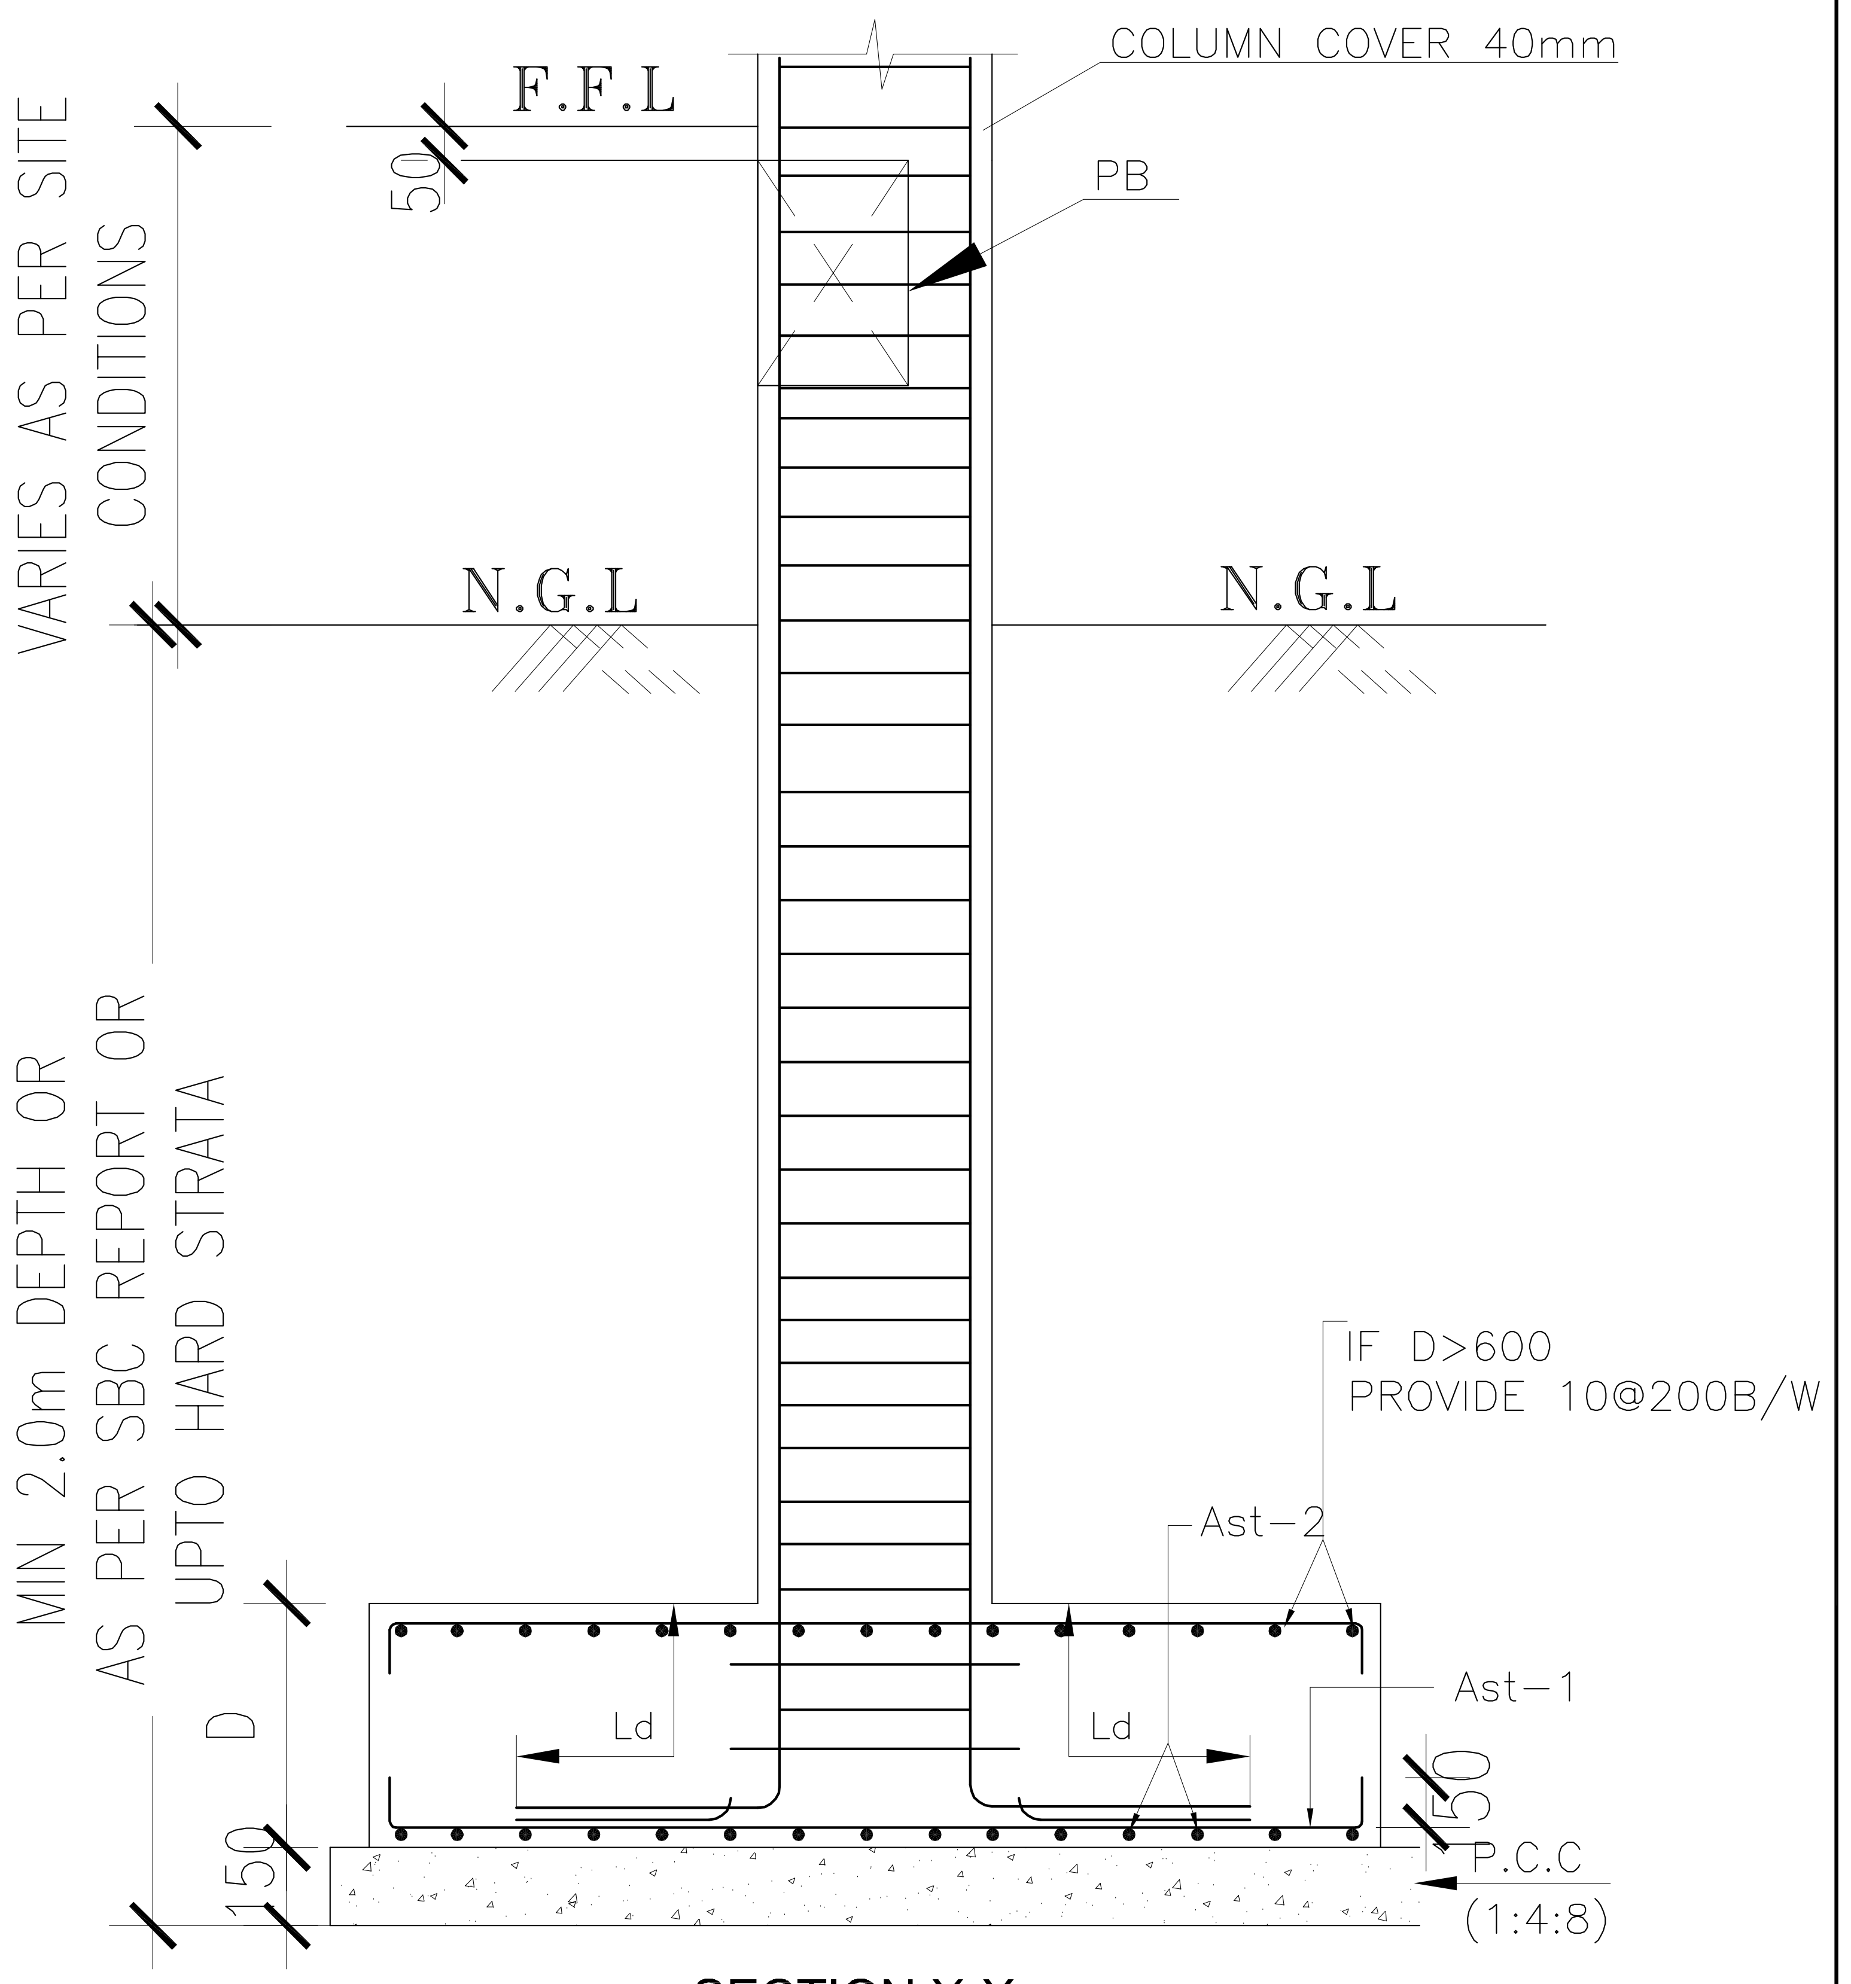
VARIES AS PER SITE CONDITIONS
F.F.L
50
COLUMN COVER 40mm
PB
N.G.L
N.G.L
MIN 2.0m DEPTH OR AS PER SBC REPORT OR UPTO HARD STRATA
IF D>600 PROVIDE 10@200B/W
Ast-2
Ast-1
Ld
Ld
D
150
50
P.C.C (1:4:8)

SECTION X-X

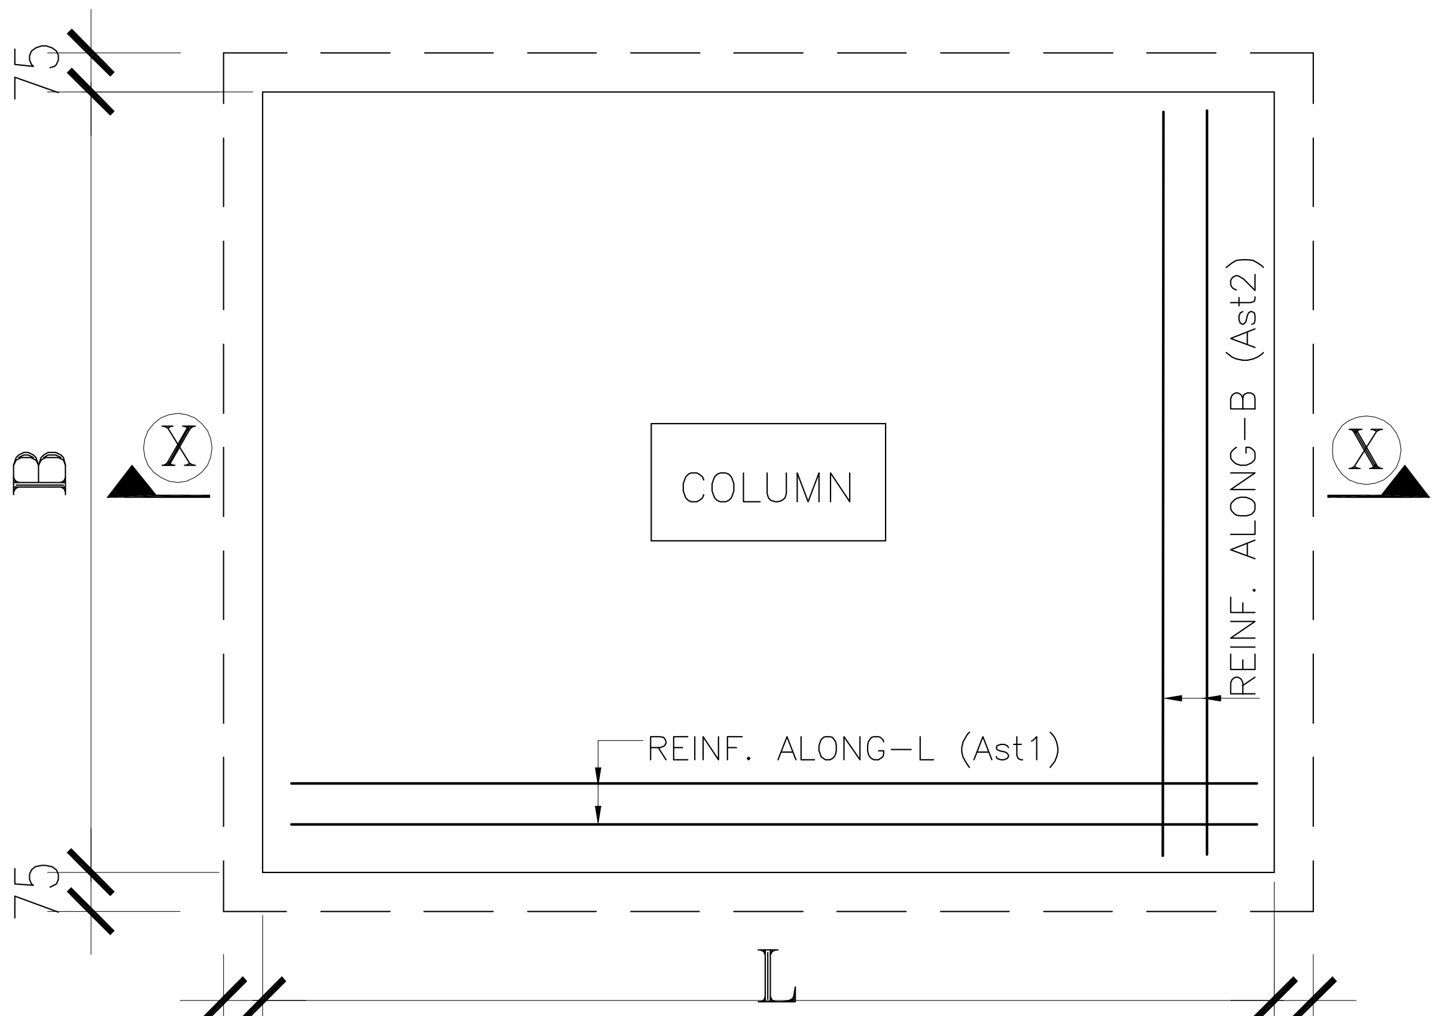

TYPICAL FOOTING PLAN

- THIS DRAWING SHALL BE READ IN CONJUNCTION WITH ALL RELEVANT ARCHITECTURAL, STRUCTURAL AND SERVICES DRAWINGS. ANY DISCREPANCY NOTICED SHALL BE BROUGHT TO THE ATTENTION OF THE CONSULTANTS AND RESOLVED AS SOON AS POSSIBLE BUT ALWAYS PRIOR TO

ARCHITECTURAL CONSULTANT:

also. design
a little story of design

STRUCTURAL& MEP CONSULTANTS

JASHRITHA ASSOCIATES
AND MEP PLANNERS
4th FLOOR(4B), HIG 129, KPHB COLONY, KUKATPALLY,
(SUB BRANCH:PR NAGAR ERRAGADDA.)
HYDERABAD 500072, TELANGANA, INDIA
Phone : 9700441106.
E-mail : jashreyansh.consultatns@gmail.com
& jashritha.mep@gmail.com

PROJECT:

ANKURA HOMES_THE WOODS
AT KEESARAGUTTA

DRAWING TITLE:

1215_EAST VILLA
COLUMN & FOOTING
SCHEDULE

DESIGN ENGG : AJAY	APPROVED :
SCALE : NTS	DRAWN : PK
DATE : 07-10-2026	CHECKED : PRADEEP

DRAWING NO: SD-02 REV.NO: 01

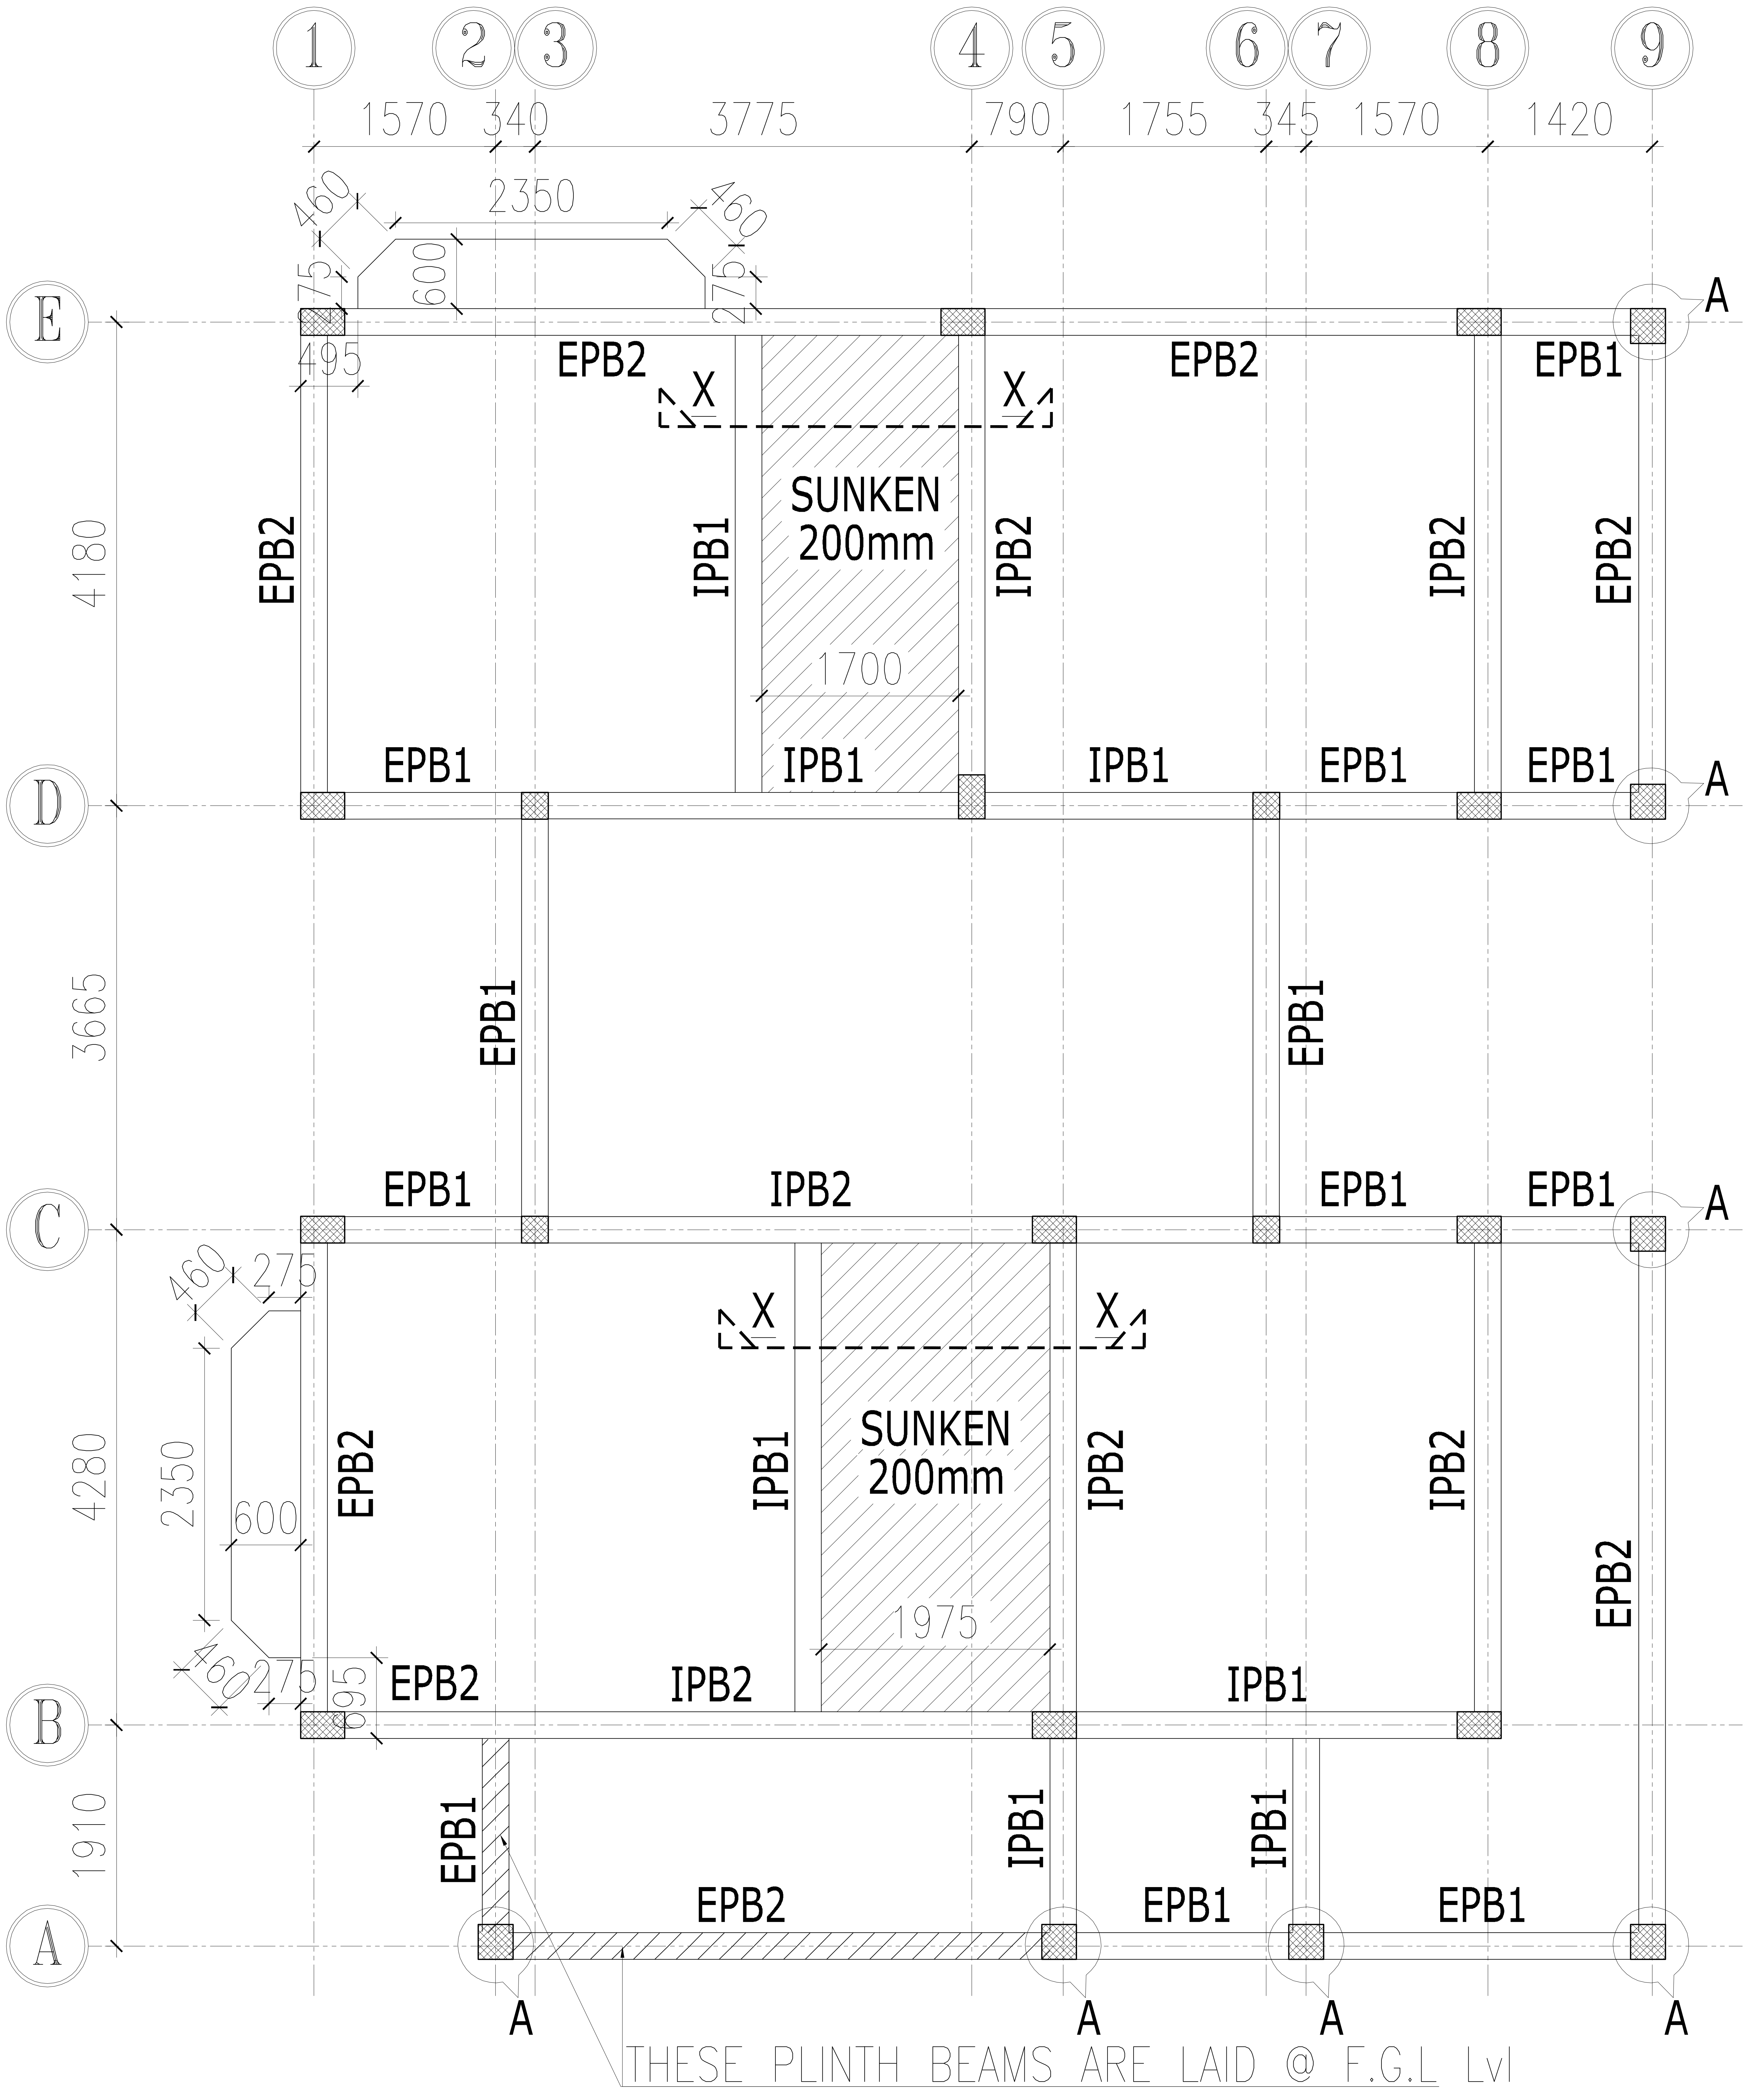

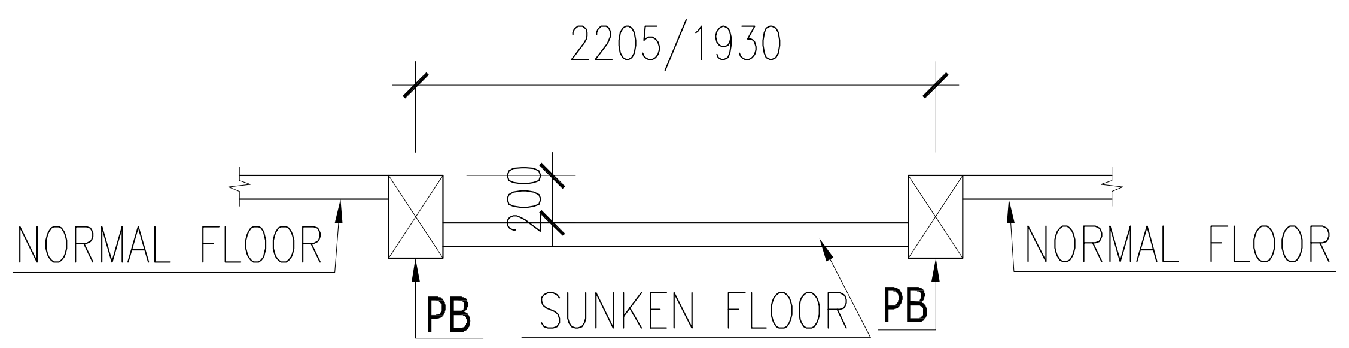

SECTION X-X

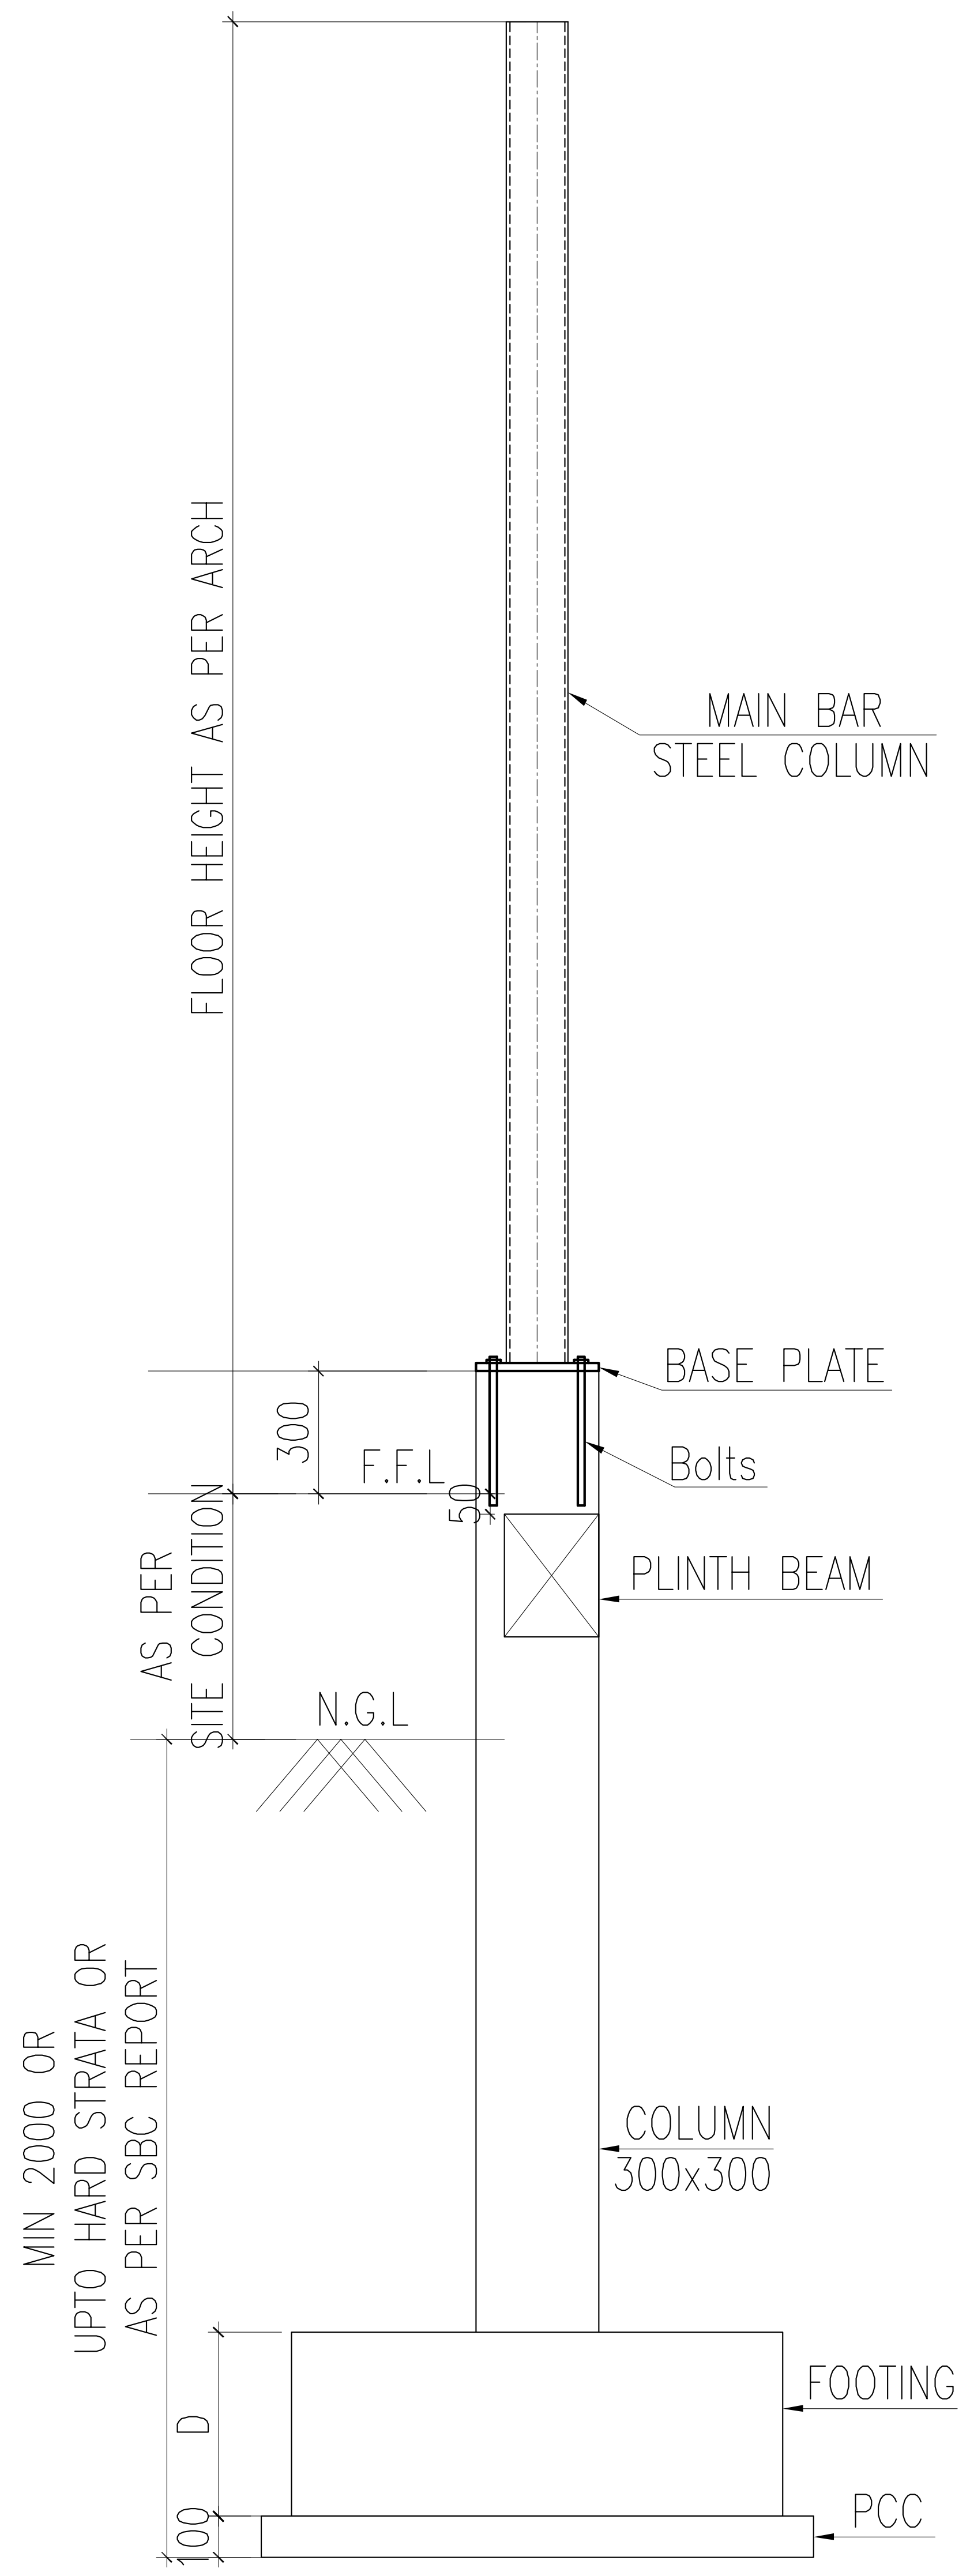

DETAIL-A

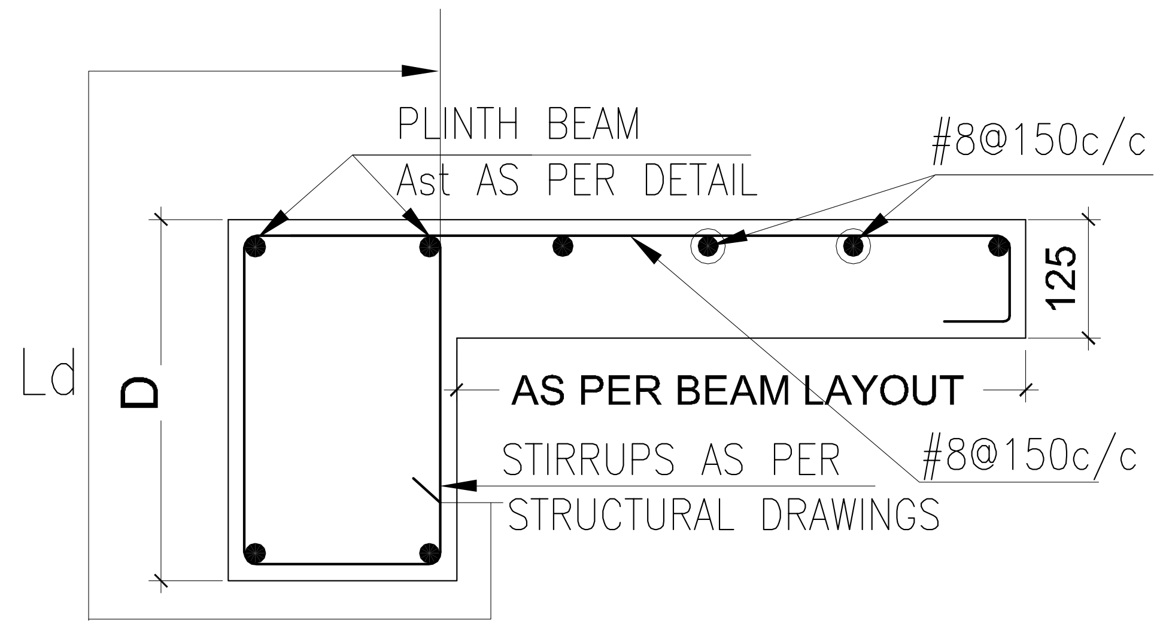

TYPICAL
SLAB PROJECTION DETAILS

- THIS DRAWING SHALL BE READ IN CONJUNCTION WITH ALL RELEVANT ARCHITECTURAL, STRUCTURAL AND SERVICES DRAWINGS. ANY DISCREPANCY NOTICED SHALL BE BROUGHT TO THE ATTENTION OF THE CONSULTANTS AND RESOLVED AS SOON AS POSSIBLE BUT ALWAYS PRIOR TO

DIRECTION:

N

ARCHITECTURAL CONSULTANT:

also.
design
a little story of design

STRUCTURAL& MEP CONSULTANTS

JASHRITHA ASSOCIATES
AND MEP PLANNERS
4th FLOOR(4B), HIG 129, KPHB COLONY, KUKATPALLY,
(SUB BRANCH:PR NAGAR ERRAGADDA.)
HYDERABAD 500072, TELANGANA, INDIA
Phone : 9700441106.
E-mail : jashreyansh.consultatns@gmail.com
& jashritha.mep@gmail.com

PROJECT:

ANKURA HOMES_THE WOODS
AT KEESARAGUTTA

DRAWING TITLE:

1215_EAST VILLA
PLINTH BEAM LAYOUT

DESIGN ENGG : AJAY	APPROVED :
SCALE : NTS	DRAWN : PK
DATE : 07-10-2026	CHECKED : PRADEEP

DRAWING NO:	SD-03	REV.NO:	01

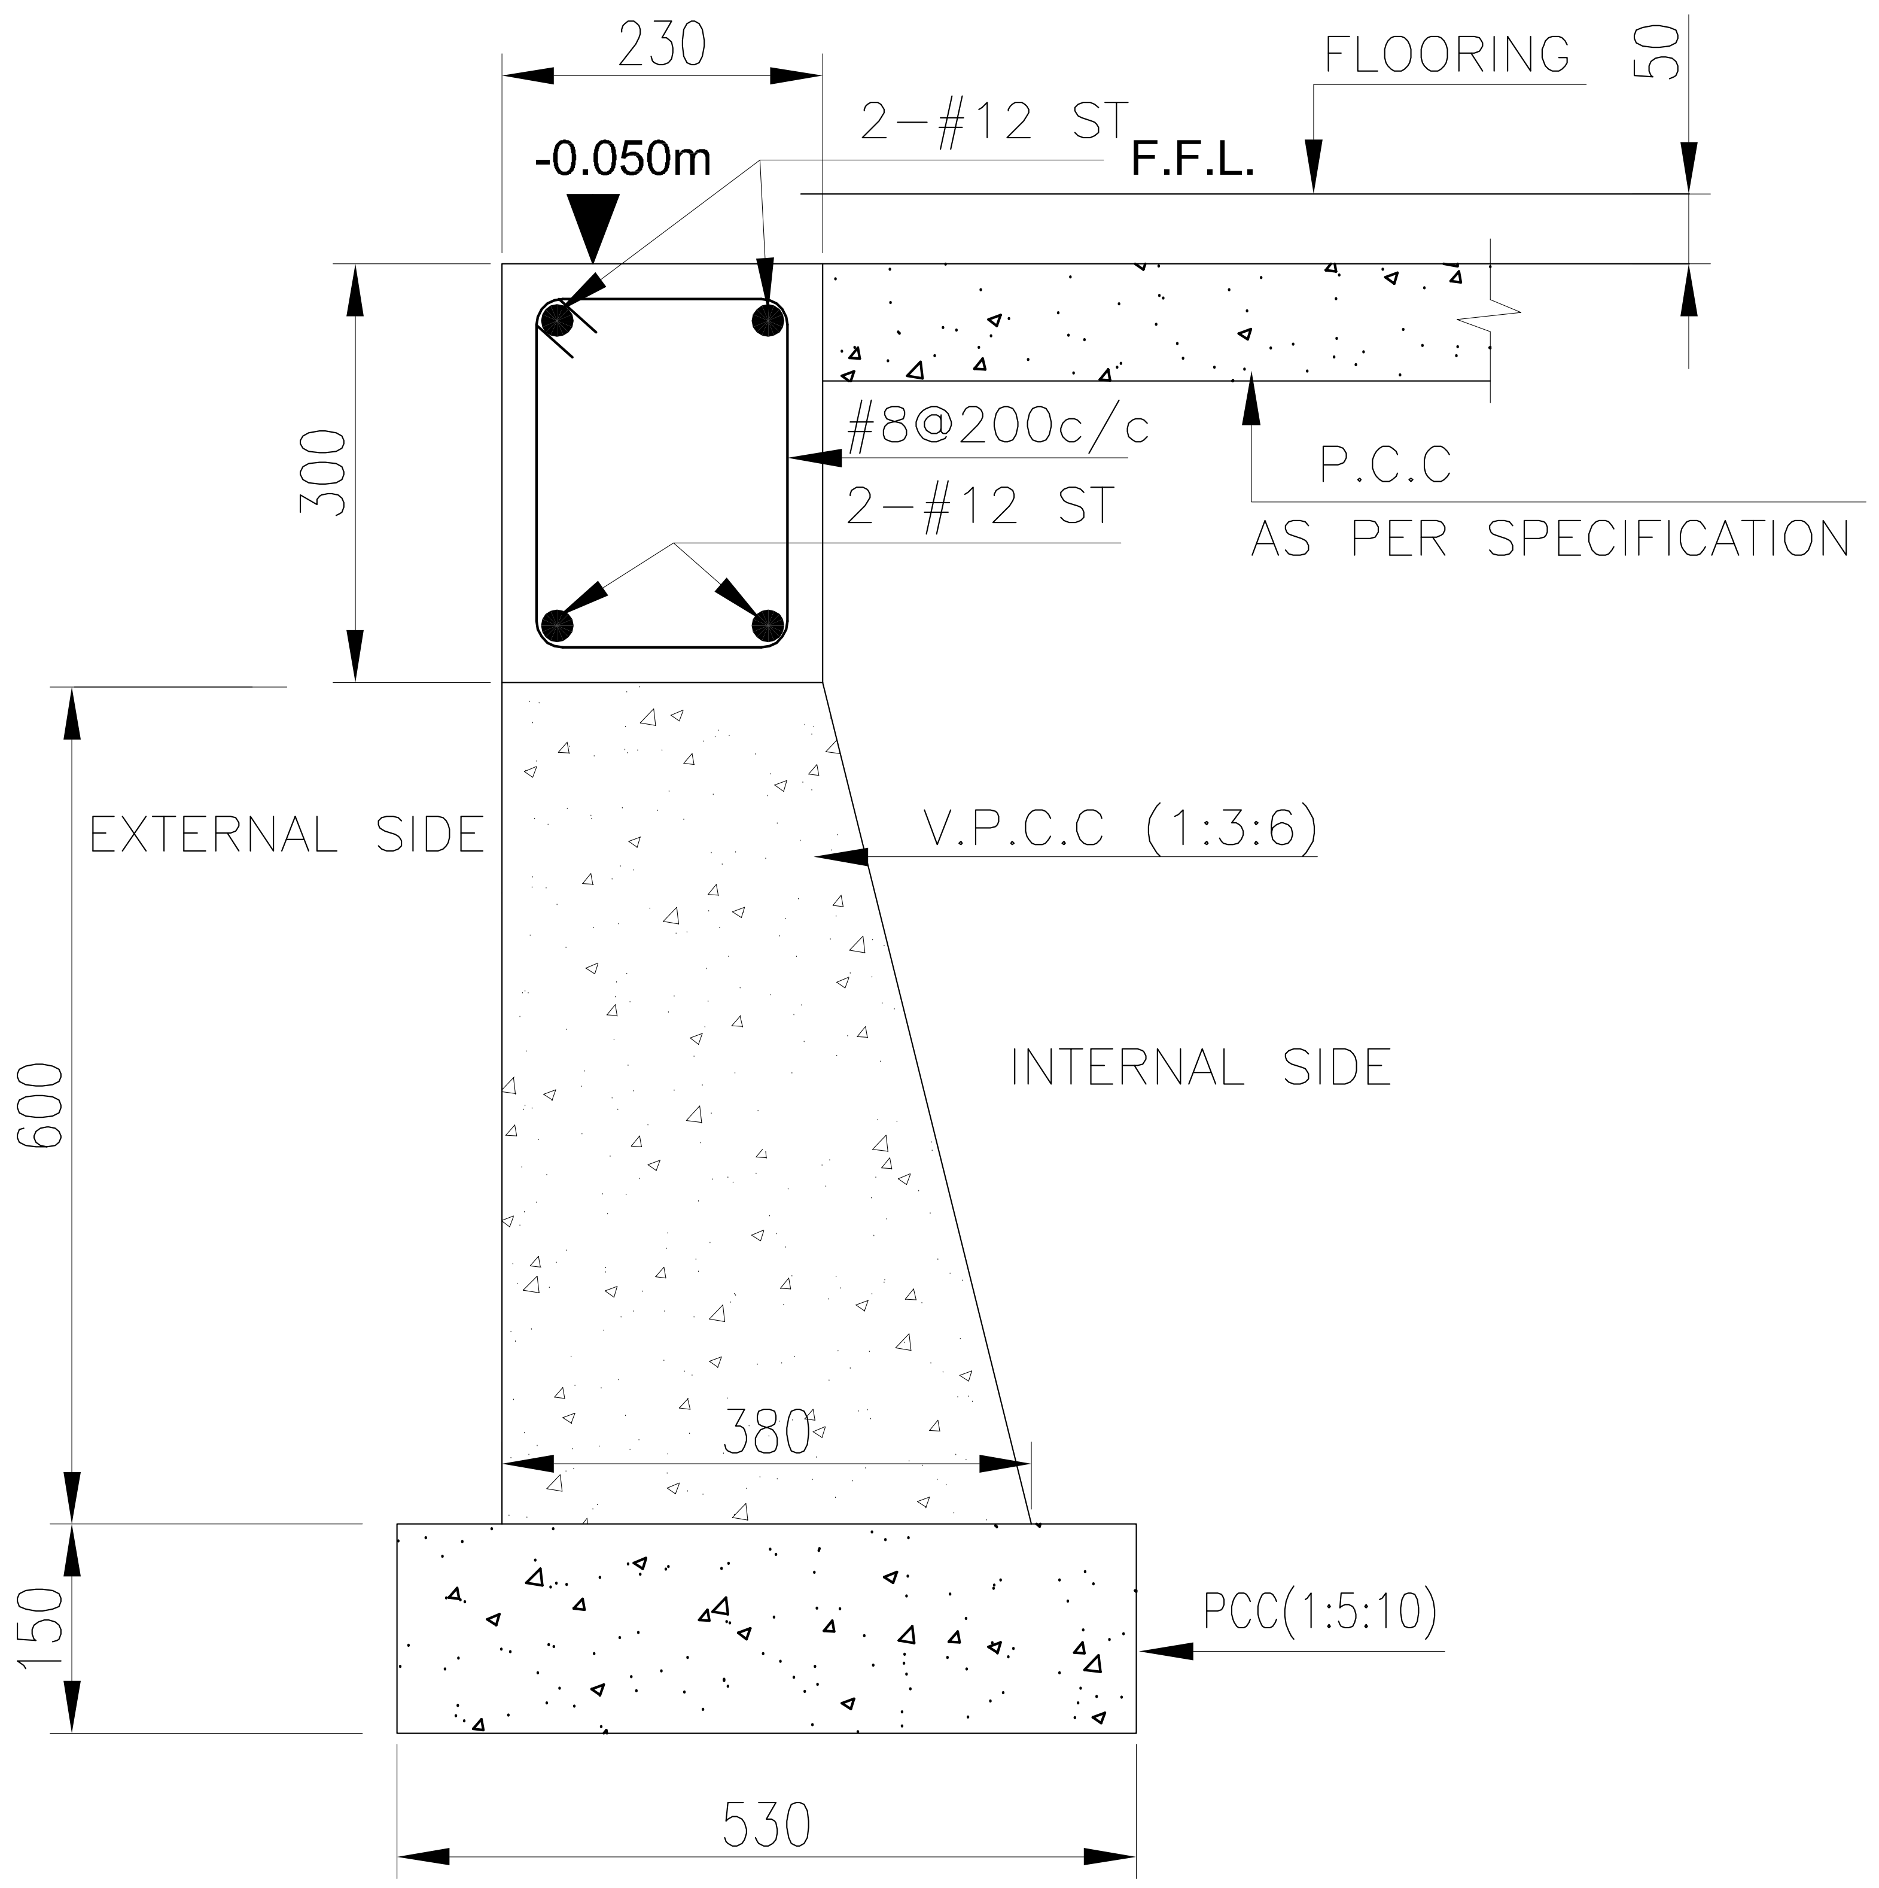

EPB1

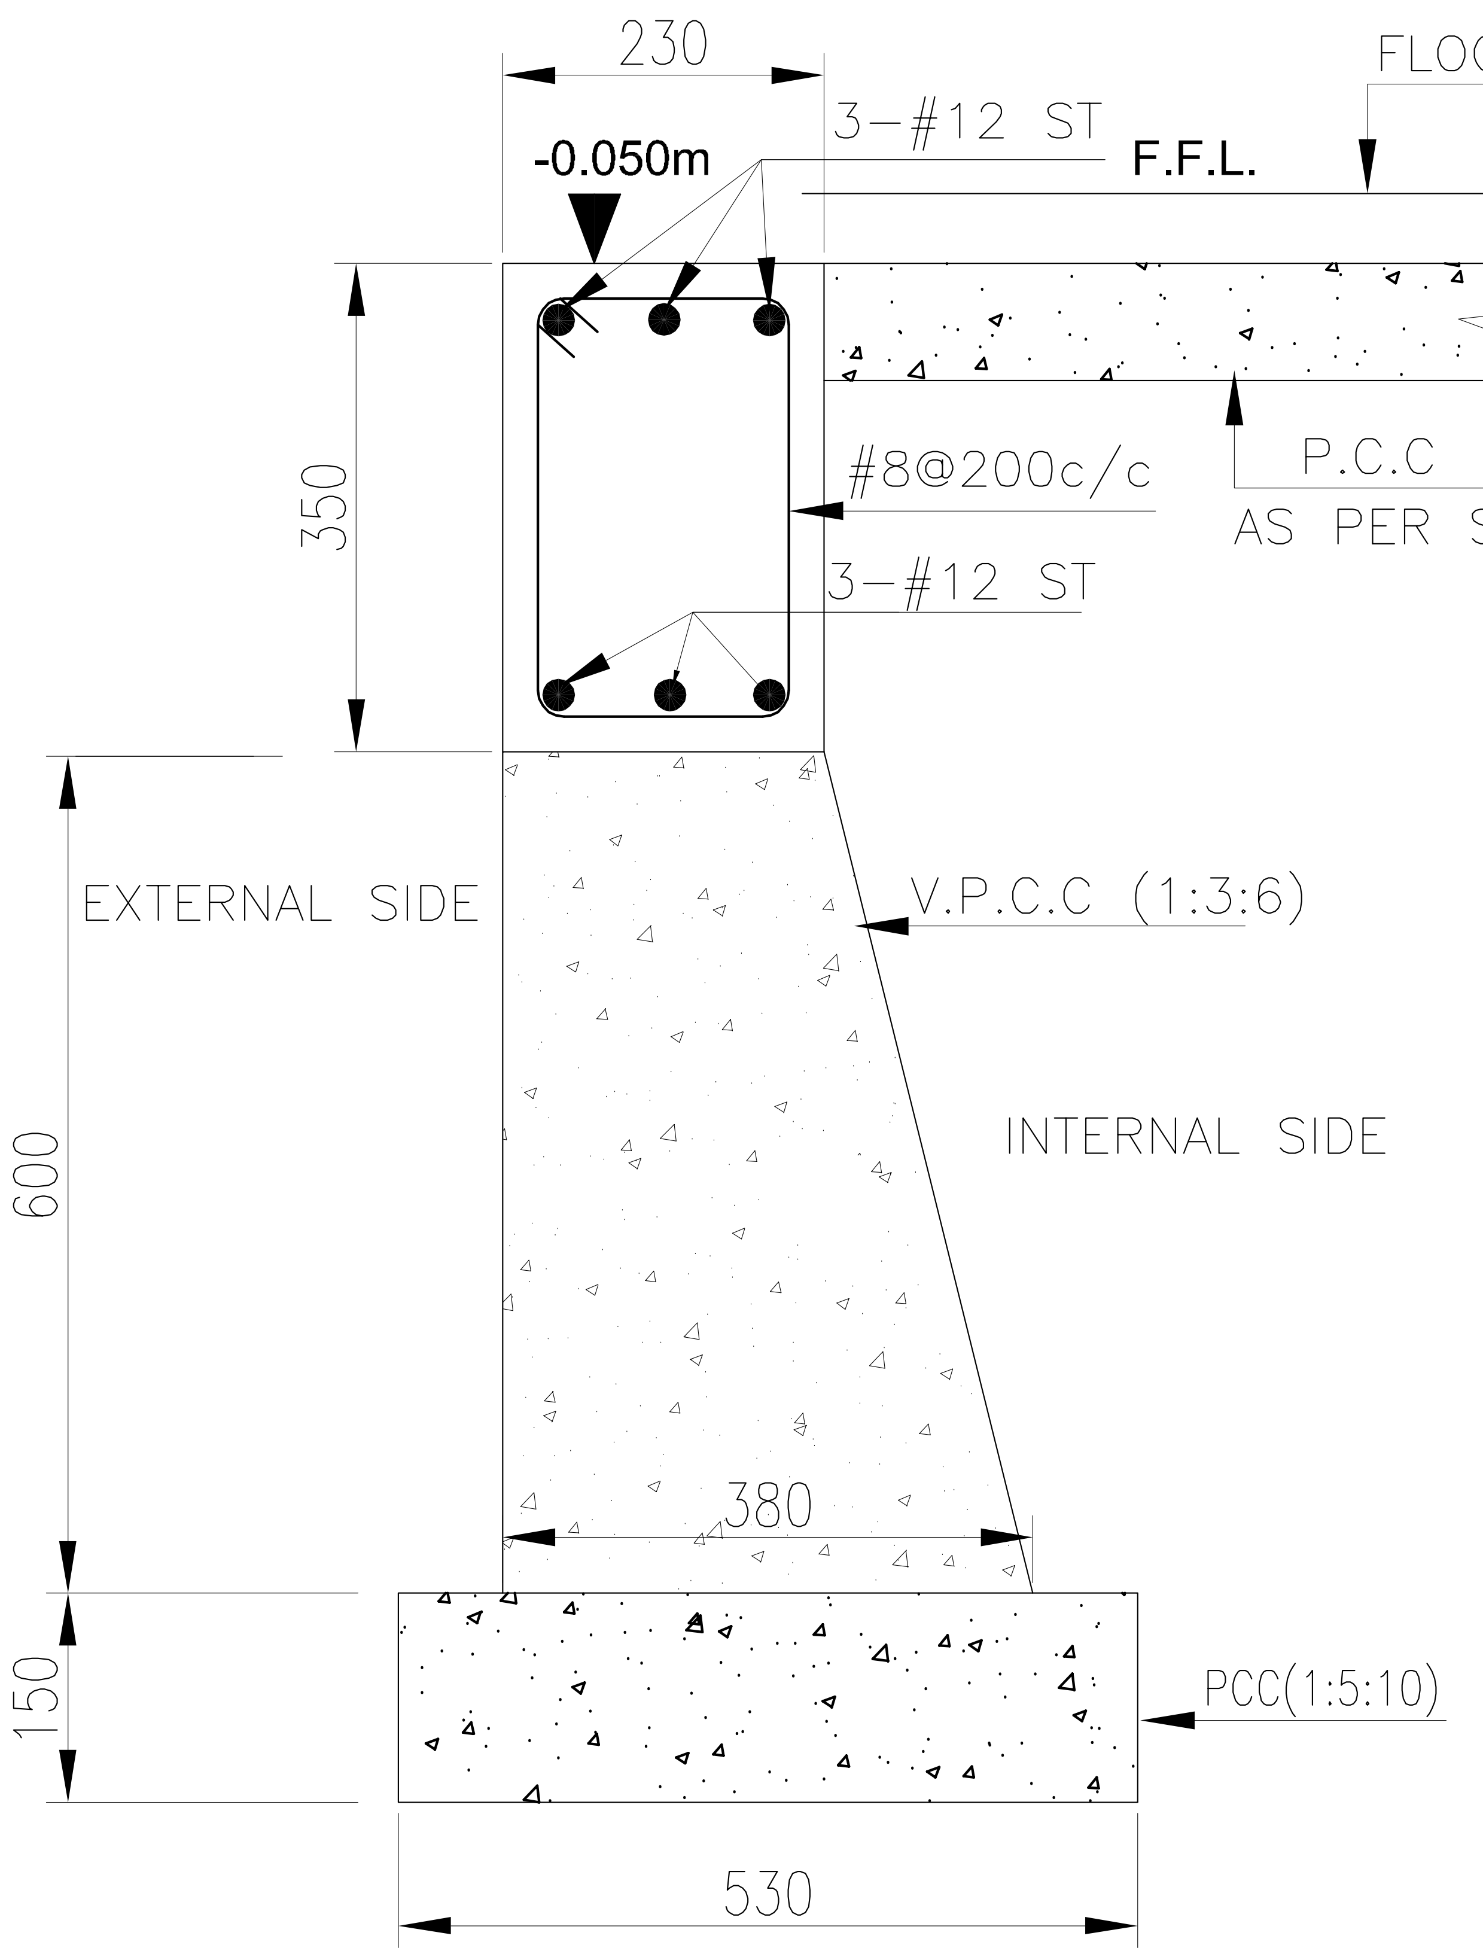

EPB2

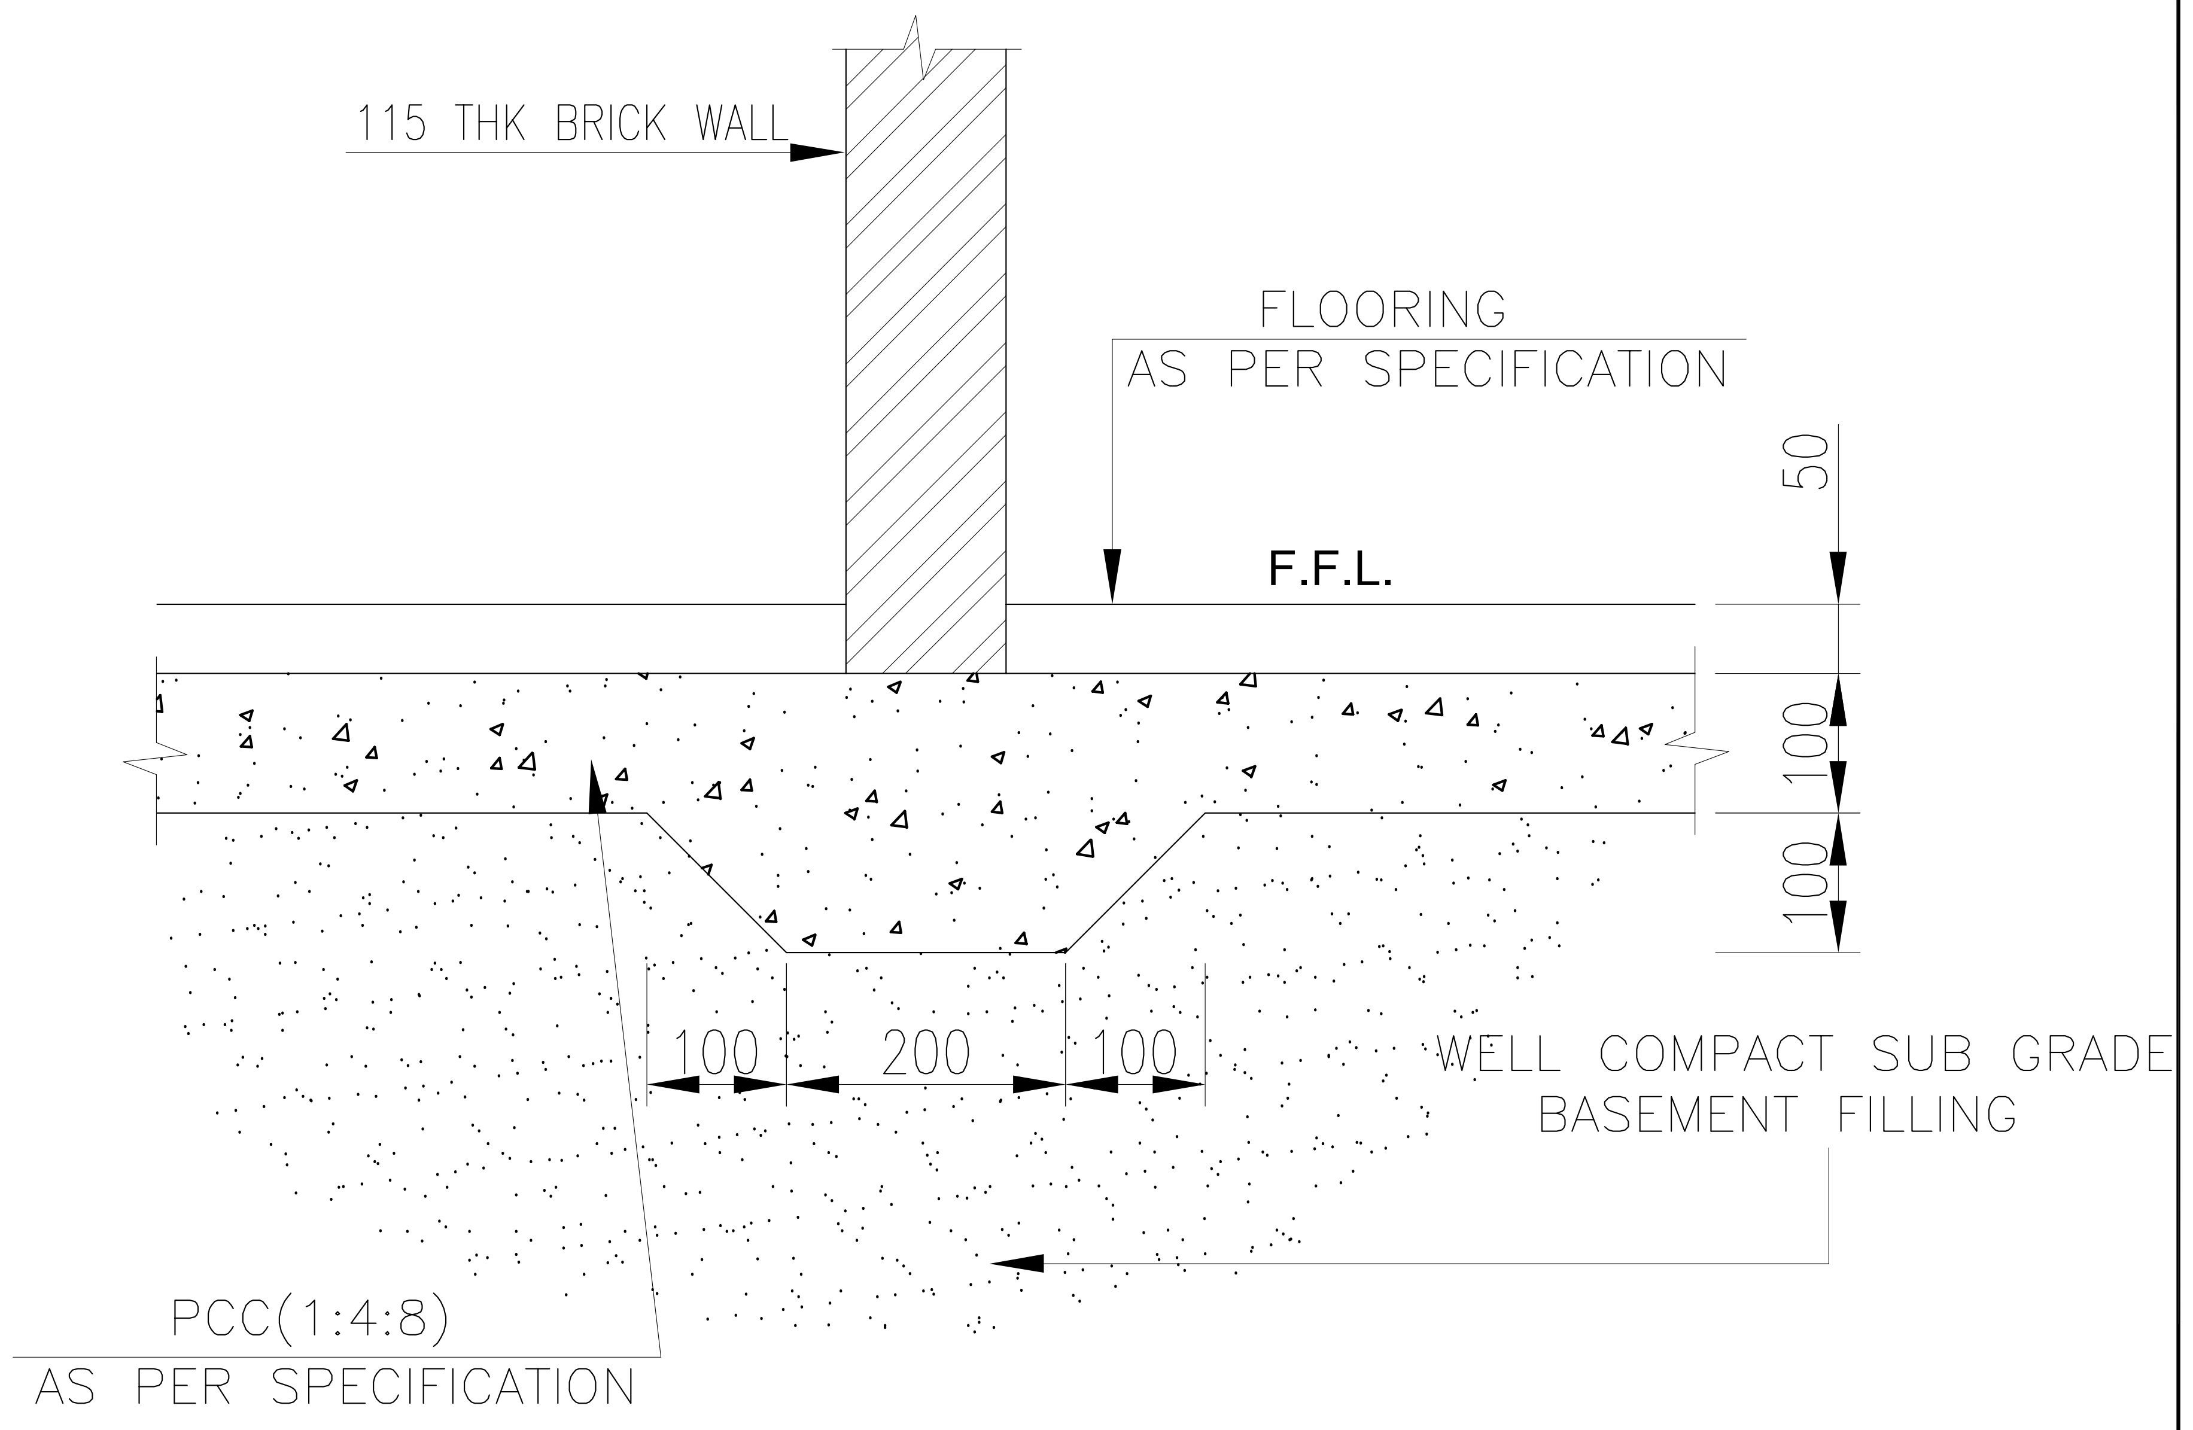

FOUNDATION DETAIL UNDER 115mm THICK BRICK WALL

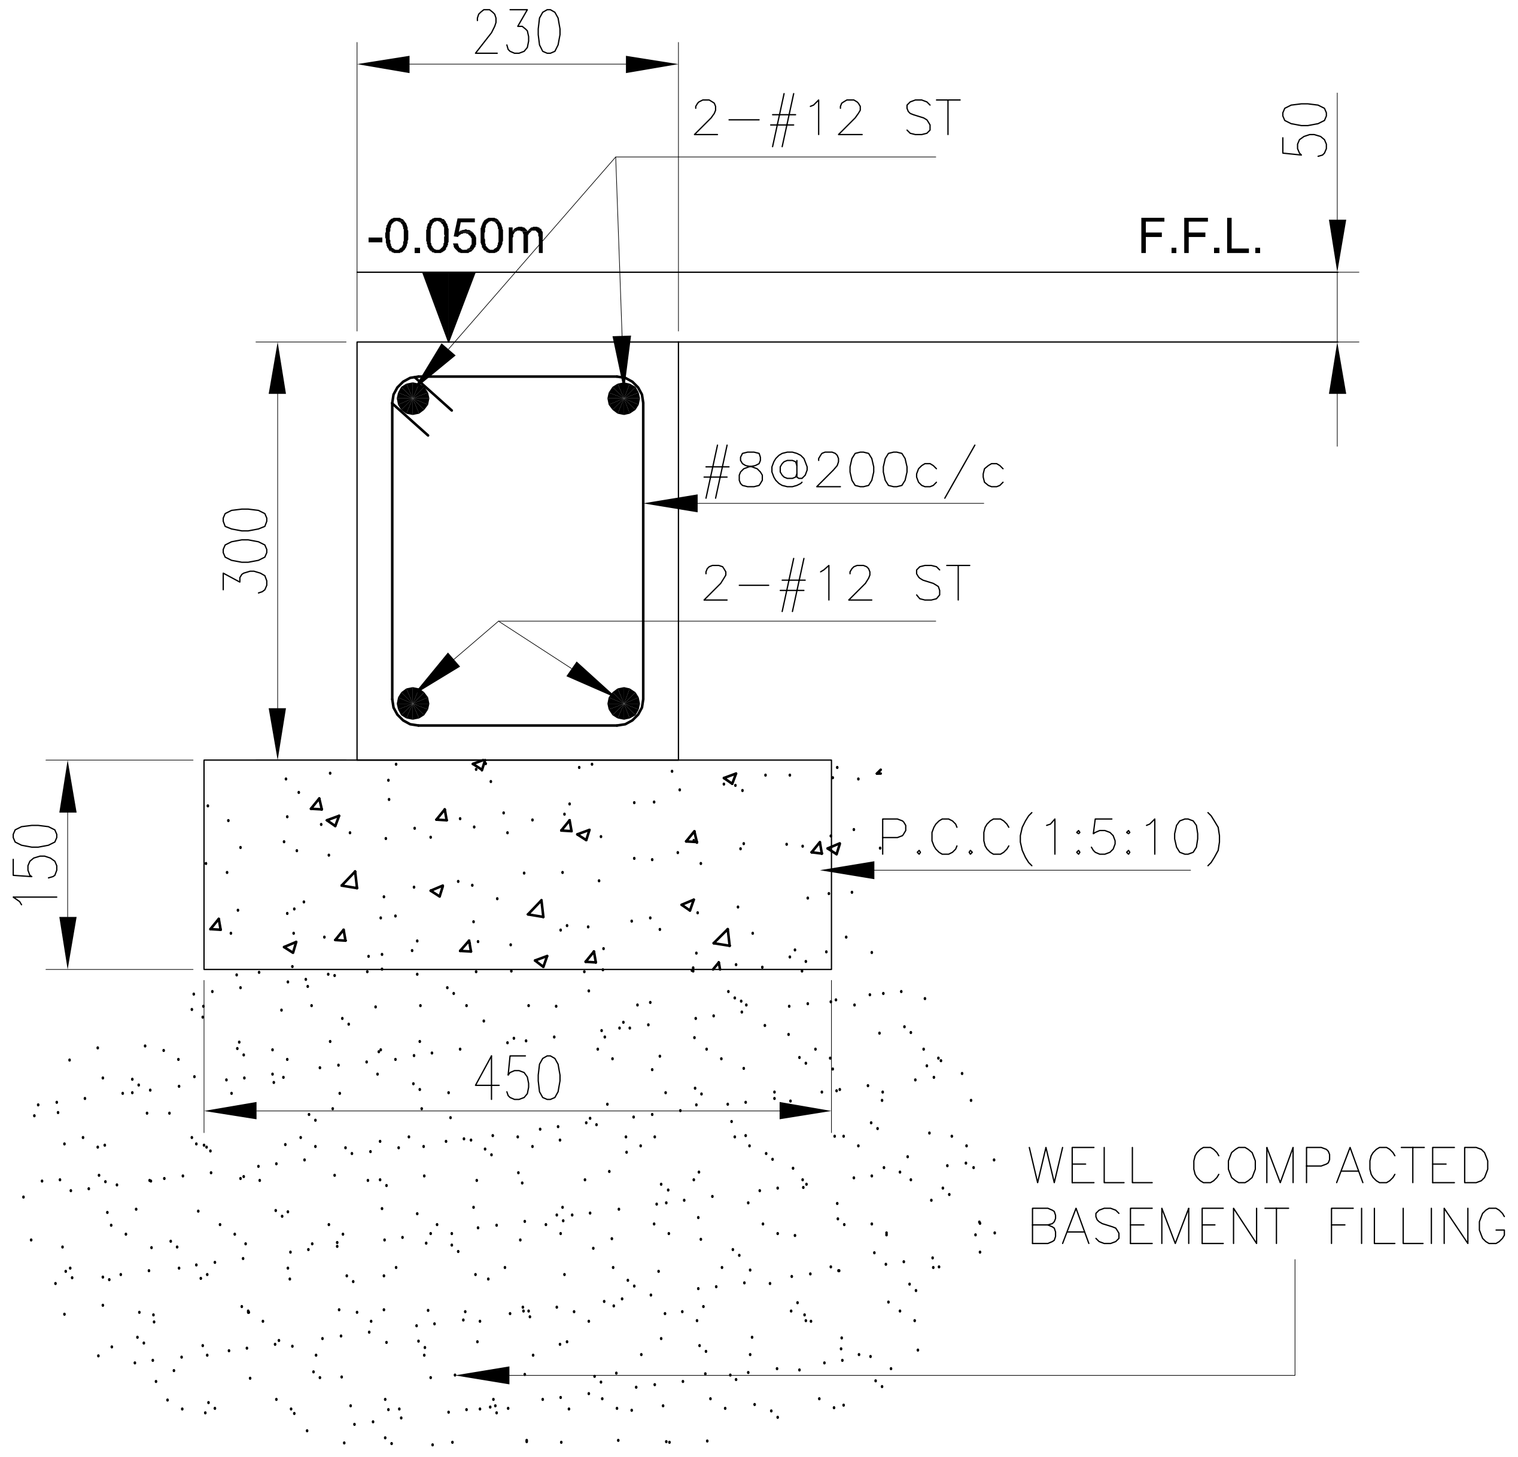

IPB1

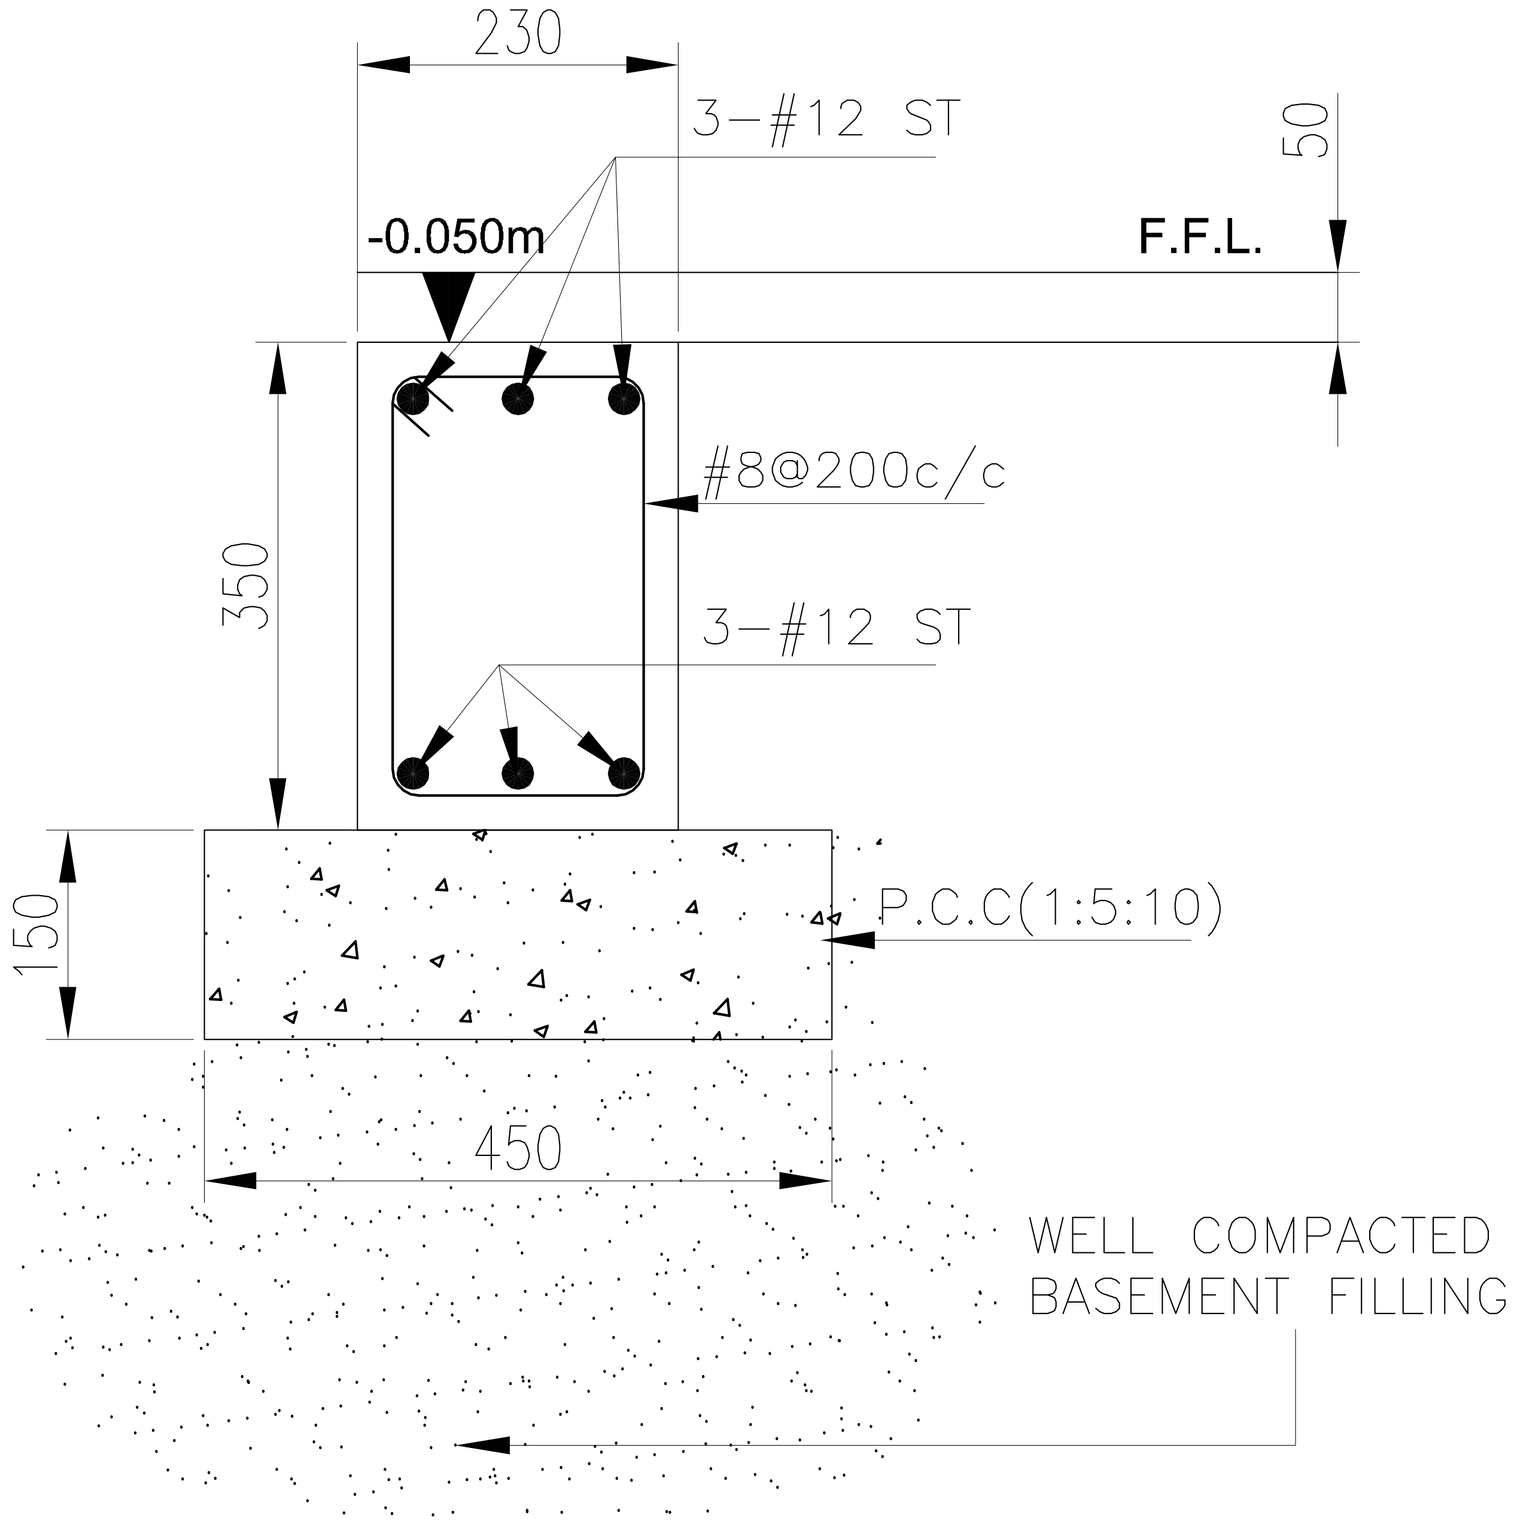

IPB2

- THIS DRAWING SHALL BE READ IN CONJUNCTION WITH ALL RELEVANT ARCHITECTURAL, STRUCTURAL AND SERVICES DRAWINGS. ANY DISCREPANCY NOTICED SHALL BE BROUGHT TO THE ATTENTION OF THE CONSULTANTS AND RESOLVED AS SOON AS POSSIBLE BUT ALWAYS PRIOR TO

ARCHITECTURAL CONSULTANT:

also. design
a little story of design

STRUCTURAL& MEP CONSULTANTS

JASHRITHA ASSOCIATES
AND MEP PLANNERS
4th FLOOR(4B), HIG 129, KPHB COLONY, KUKATPALLY,
(SUB BRANCH:PR NAGAR ERRAGADDA.)
HYDERABAD 500072, TELANGANA, INDIA
Phone : 9700441106.
E-mail : jashreyansh.consultatns@gmail.com
& jashritha.mep@gmail.com

PROJECT:

ANKURA HOMES_THE WOODS
AT KEESARAGUTTA

DRAWING TITLE:

1215_EAST VILLA
PLINTH BEAM DETAILS

DESIGN ENGG : AJAY	APPROVED :
SCALE : NTS	DRAWN : PK
DATE : 23-09-2026	CHECKED : PRADEEP

DRAWING NO: SD-04
REV.NO:

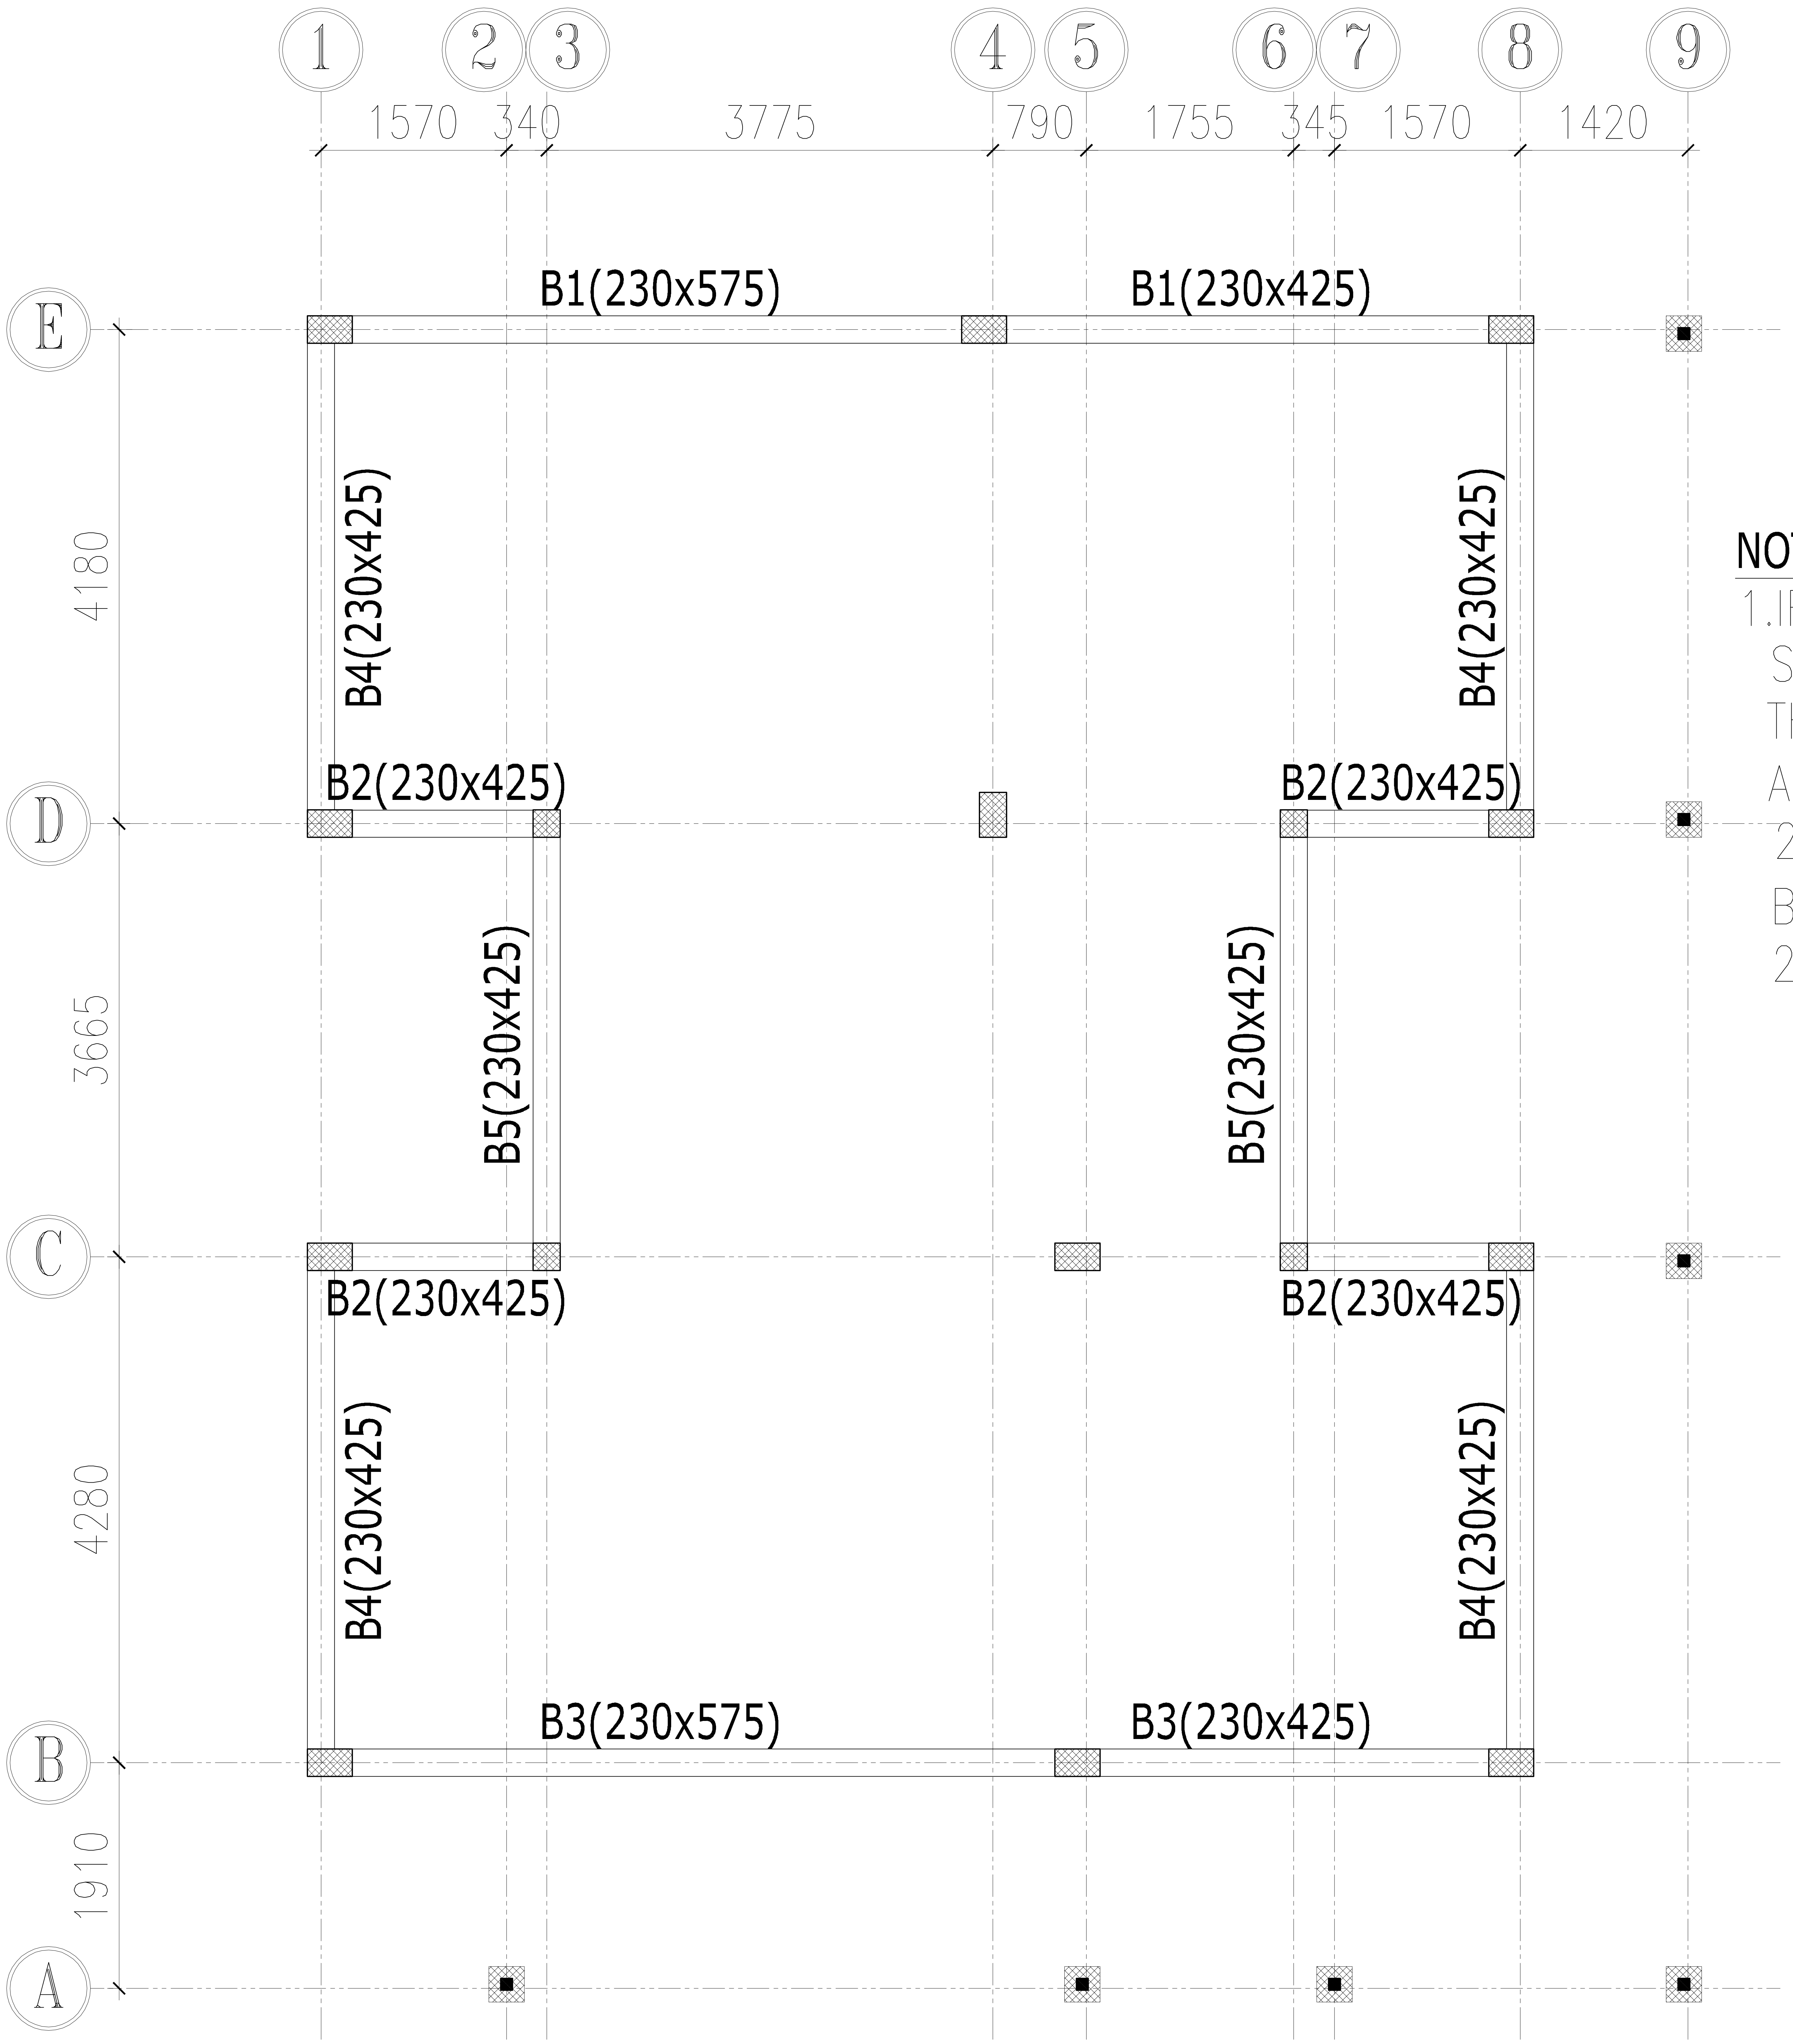

NOTE:

1.IF YOU WANT ANY INTERNAL BEAMS FOR SLOPED ROOF STRUCTURE PLEASE MAINTAIN THE STEEL 2-#16(Top&Bottom) UPTO 3.5M
ABOVE 3.5M SPAN MAINTAIN TOP STEEL
2-#16 ST+ 2-#12 EXT @ SUPPORTS
BOTTOM STEEL
2-#16 ST+ 2-#12 EXT @ MID SPAN

- THIS DRAWING SHALL BE READ IN CONJUNCTION WITH ALL RELEVANT ARCHITECTURAL, STRUCTURAL AND SERVICES DRAWINGS. ANY DISCREPANCY NOTICED SHALL BE BROUGHT TO THE ATTENTION OF THE CONSULTANTS AND RESOLVED AS SOON AS POSSIBLE BUT ALWAYS PRIOR TO

DIRECTION:

N

ARCHITECTURAL CONSULTANT:

also.
design
a little story of design

STRUCTURAL& MEP CONSULTANTS

JASHRITHA ASSOCIATES
AND MEP PLANNERS
4th FLOOR(4B), HIG 129, KPHB COLONY, KUKATPALLY,
(SUB BRANCH:PR NAGAR ERRAGADDA.)
HYDERABAD 500072, TELANGANA, INDIA
Phone : 9700441106.
E-mail : jashreyansh.consultatns@gmail.com
& jashritha.mep@gmail.com

PROJECT:

ANKURA HOMES_THE WOODS
AT KEESARAGUTTA

DRAWING TITLE:

1215_EAST VILLA
ROOF BEAM LAYOUT

DESIGN ENGG : AJAY	APPROVED :
SCALE : NTS	DRAWN : PK
DATE : 07-10-2026	CHECKED : PRADEEP

DRAWING NO: SD-05
REV.NO: 01

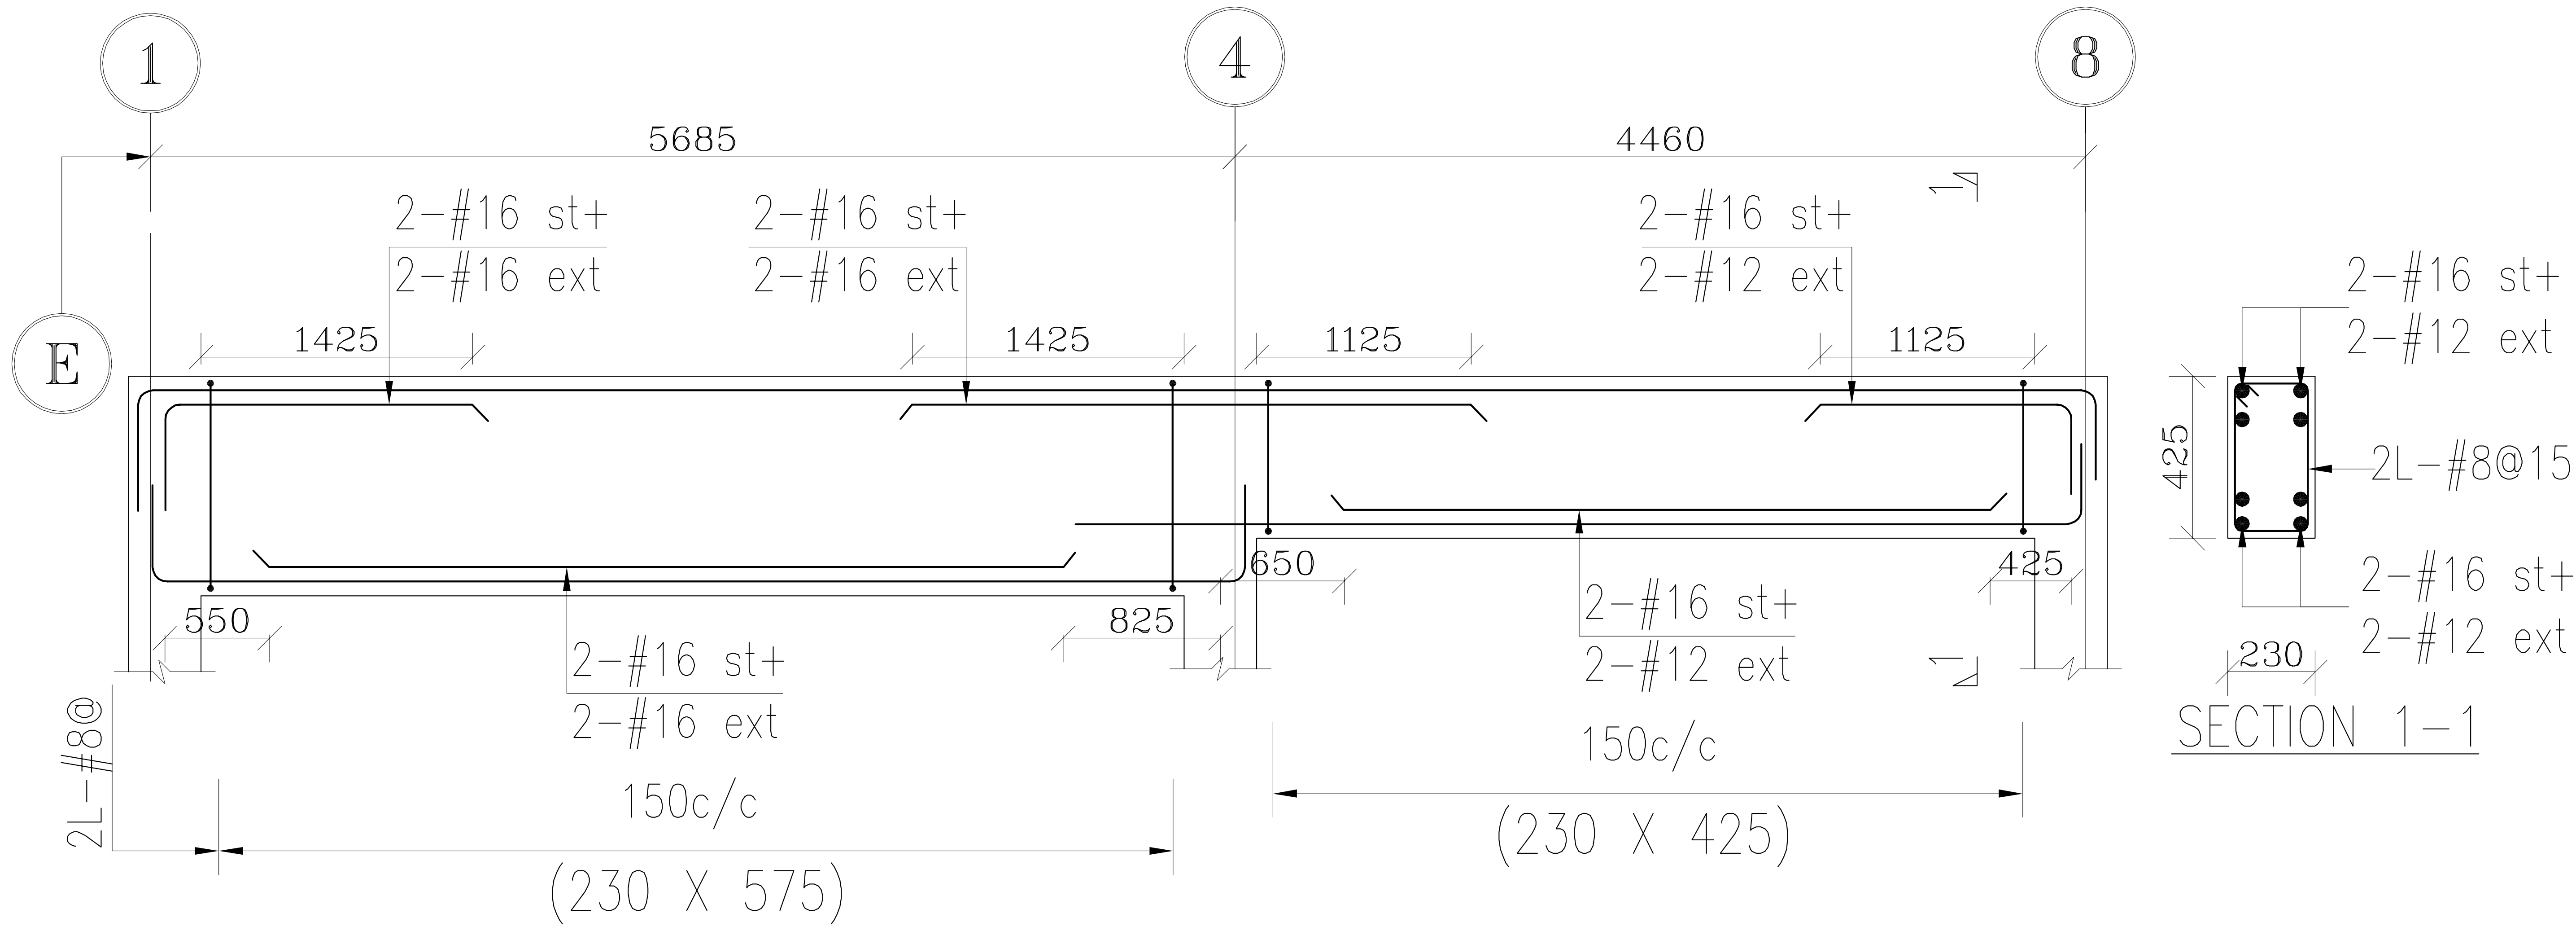

L/S OF BEAM B1(230X575/425)

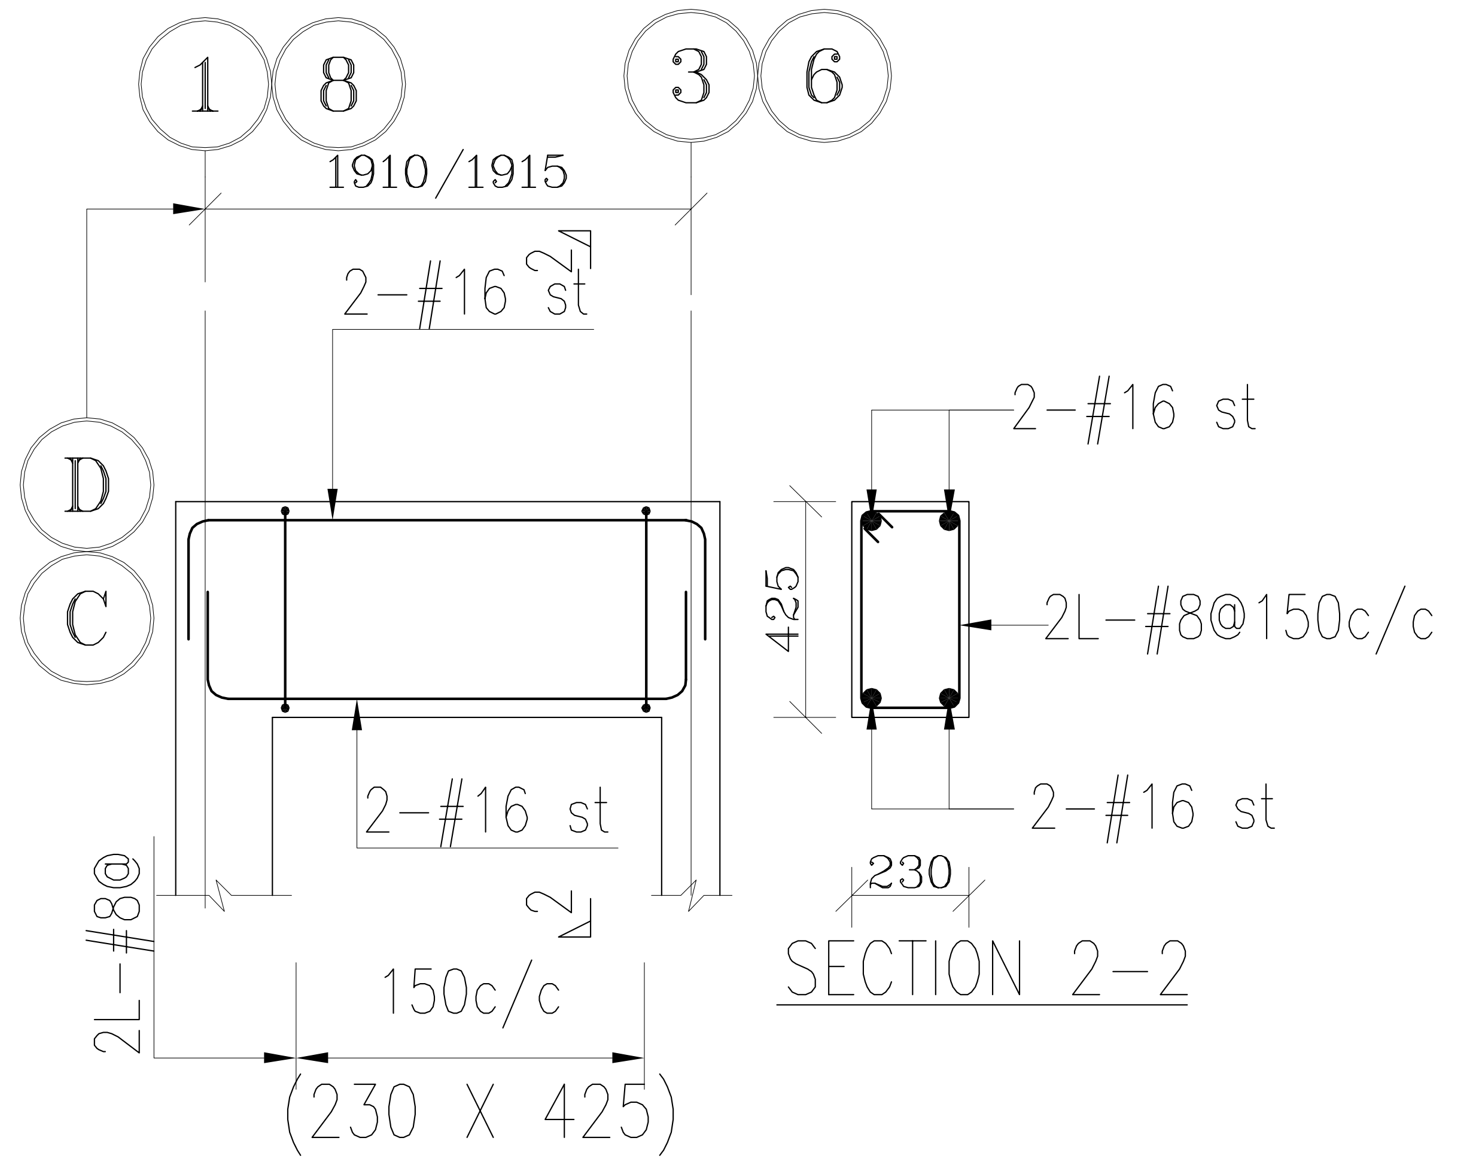

L/S OF BEAM B2(230X425)

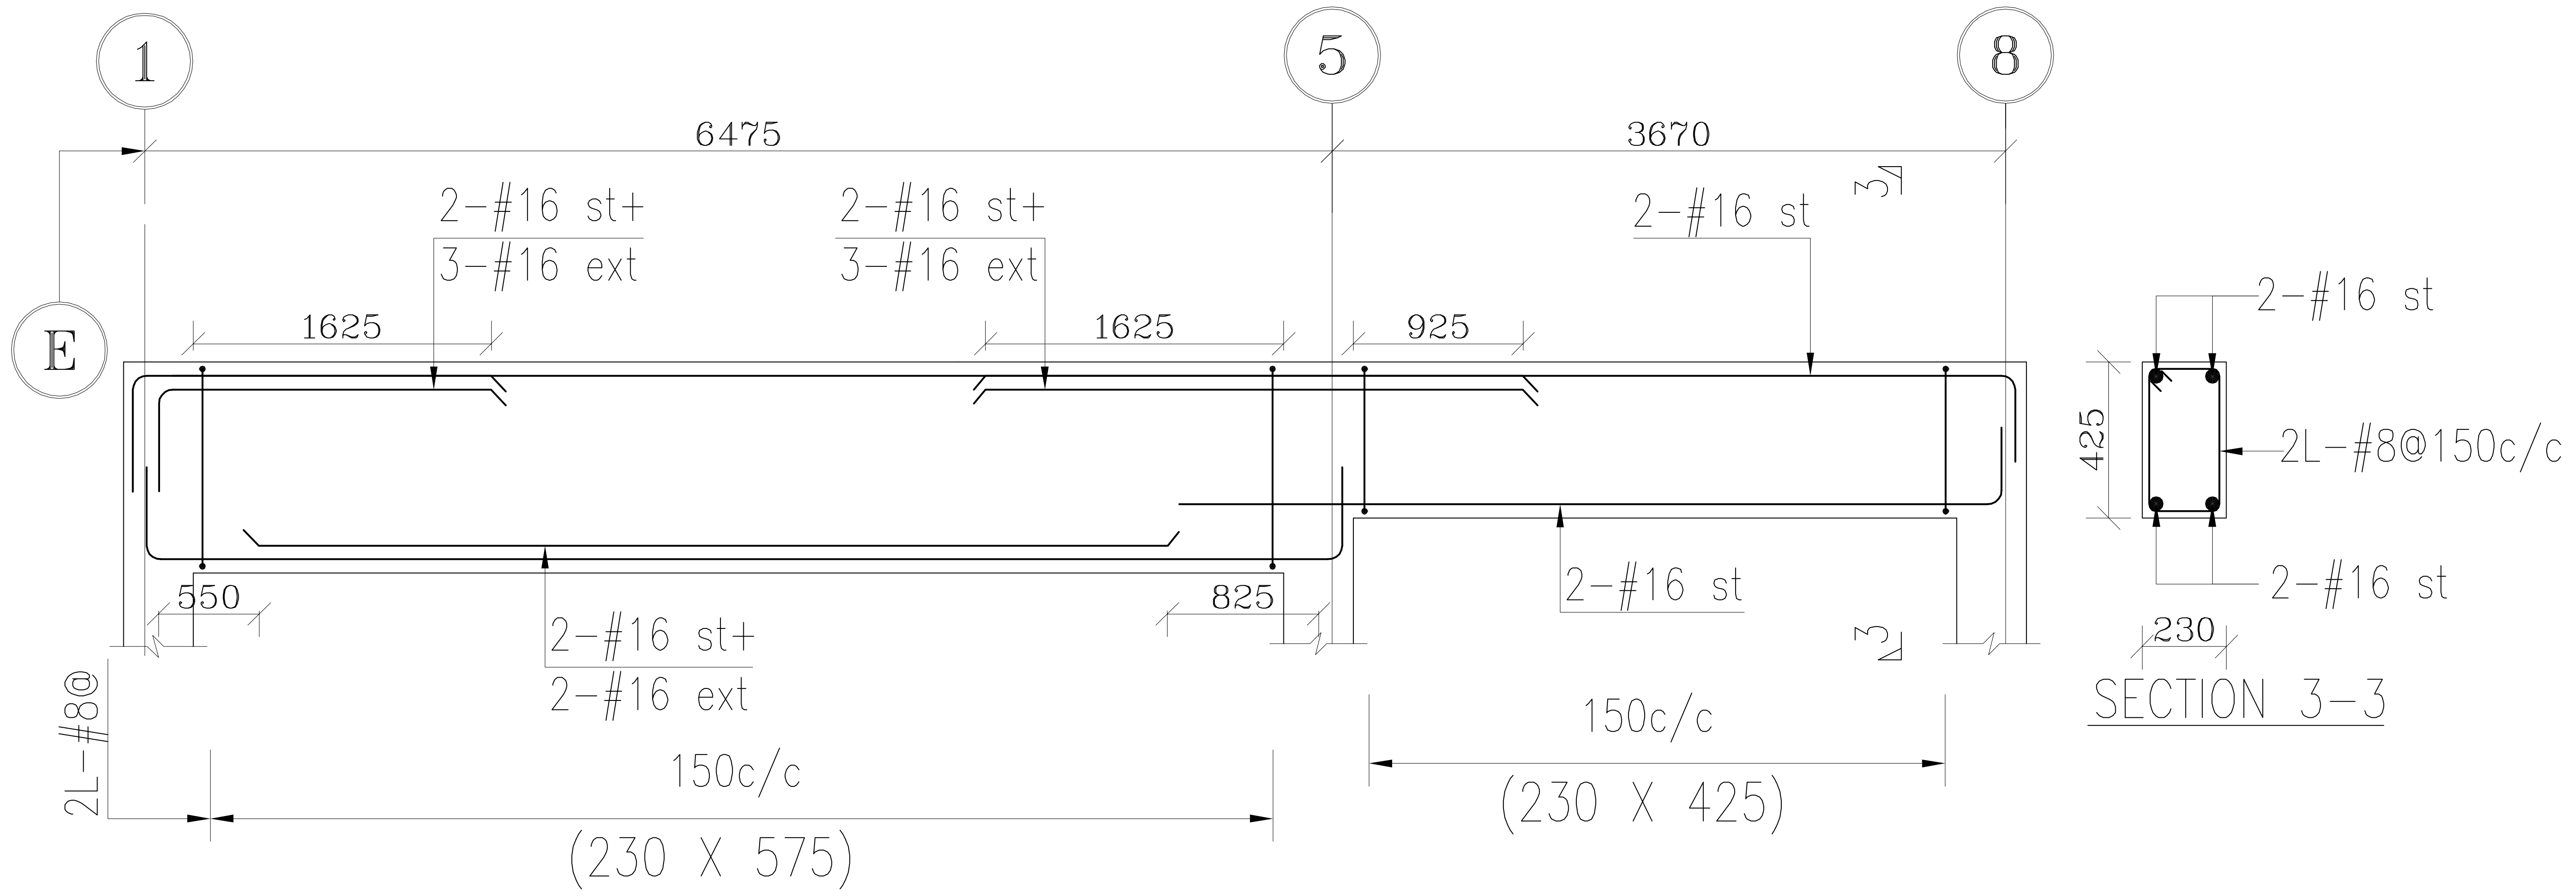

L/S OF BEAM B3(230X575/425)

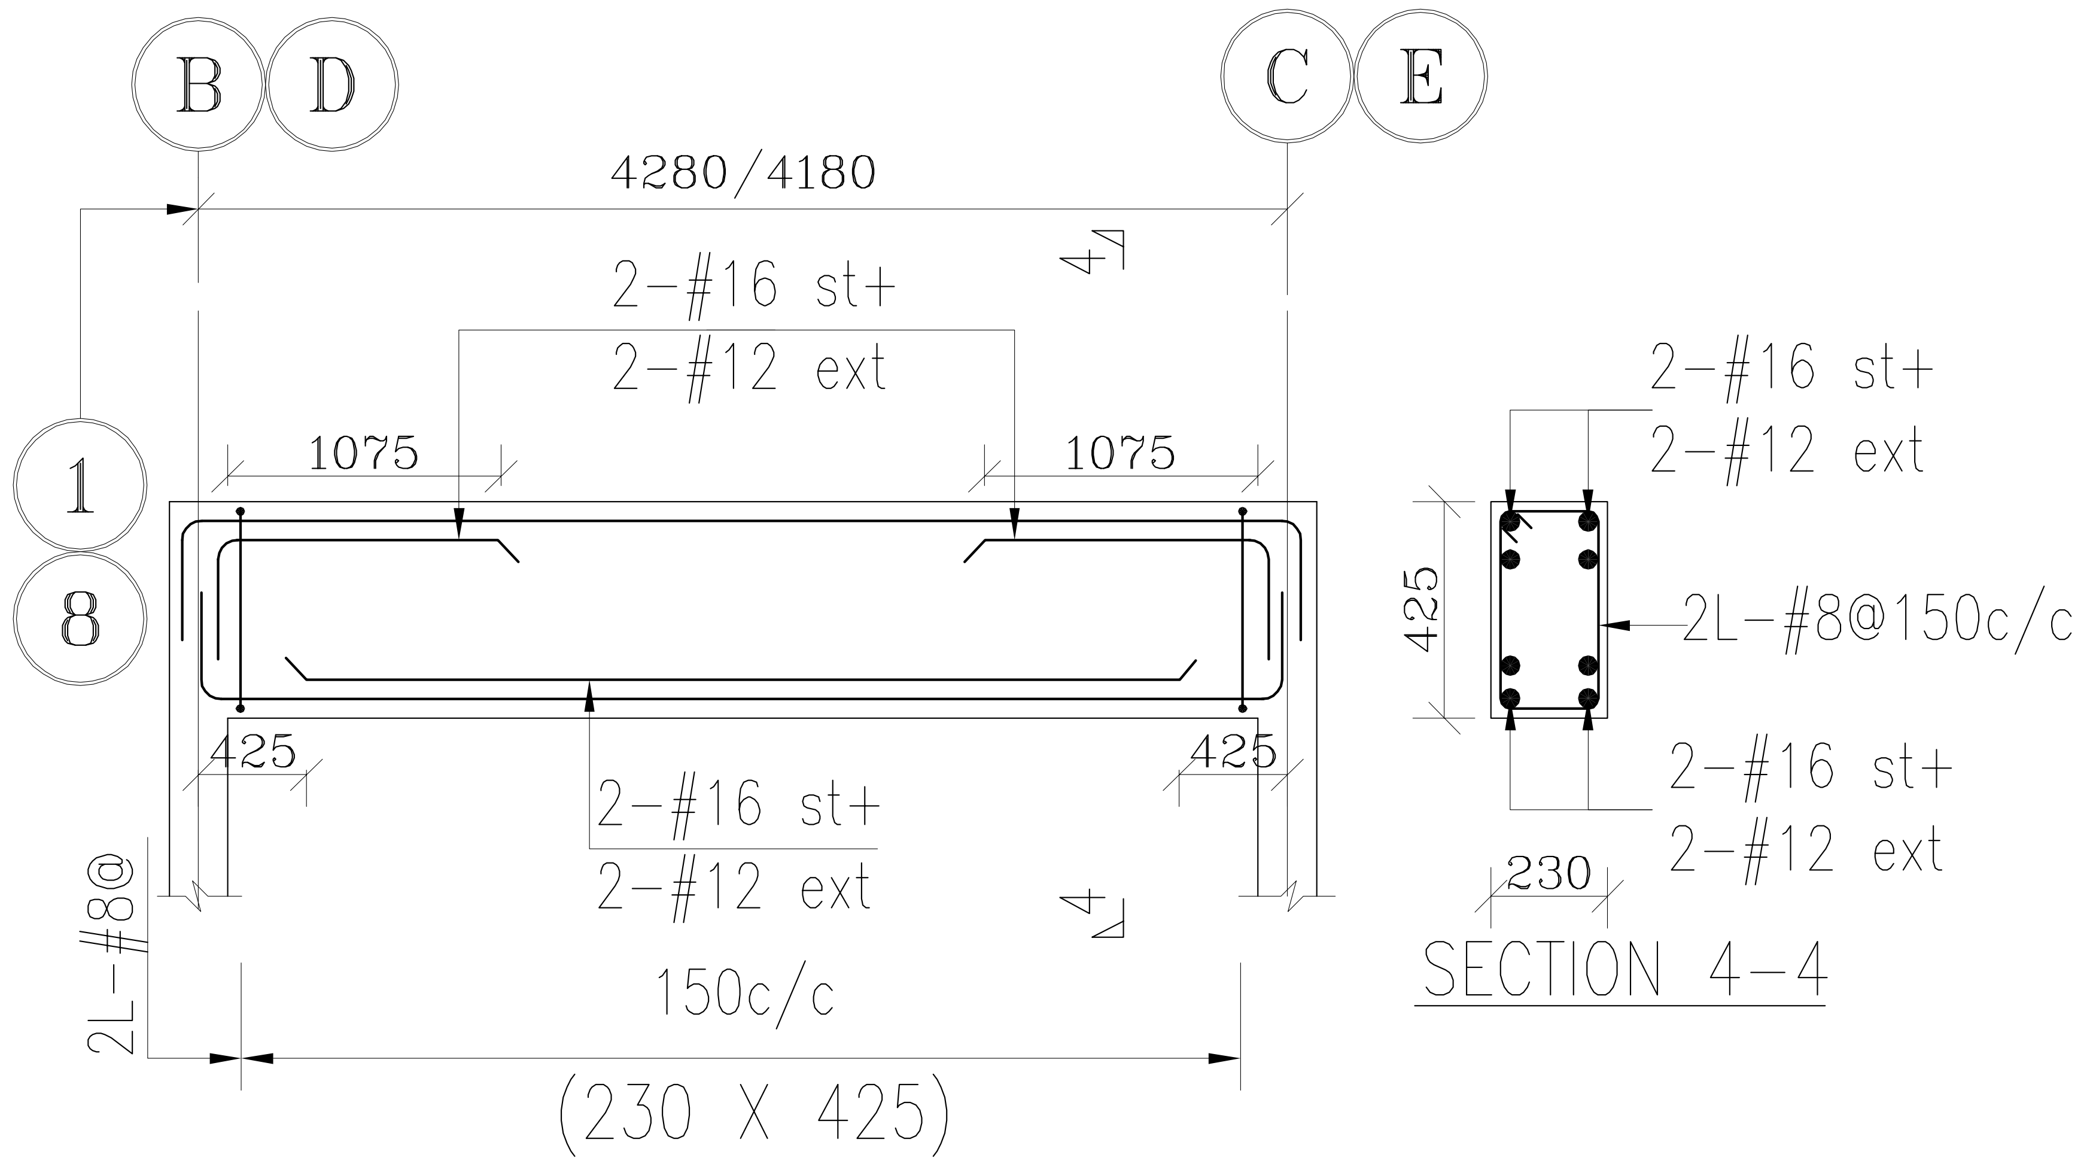

L/S OF BEAM B4(230X425)

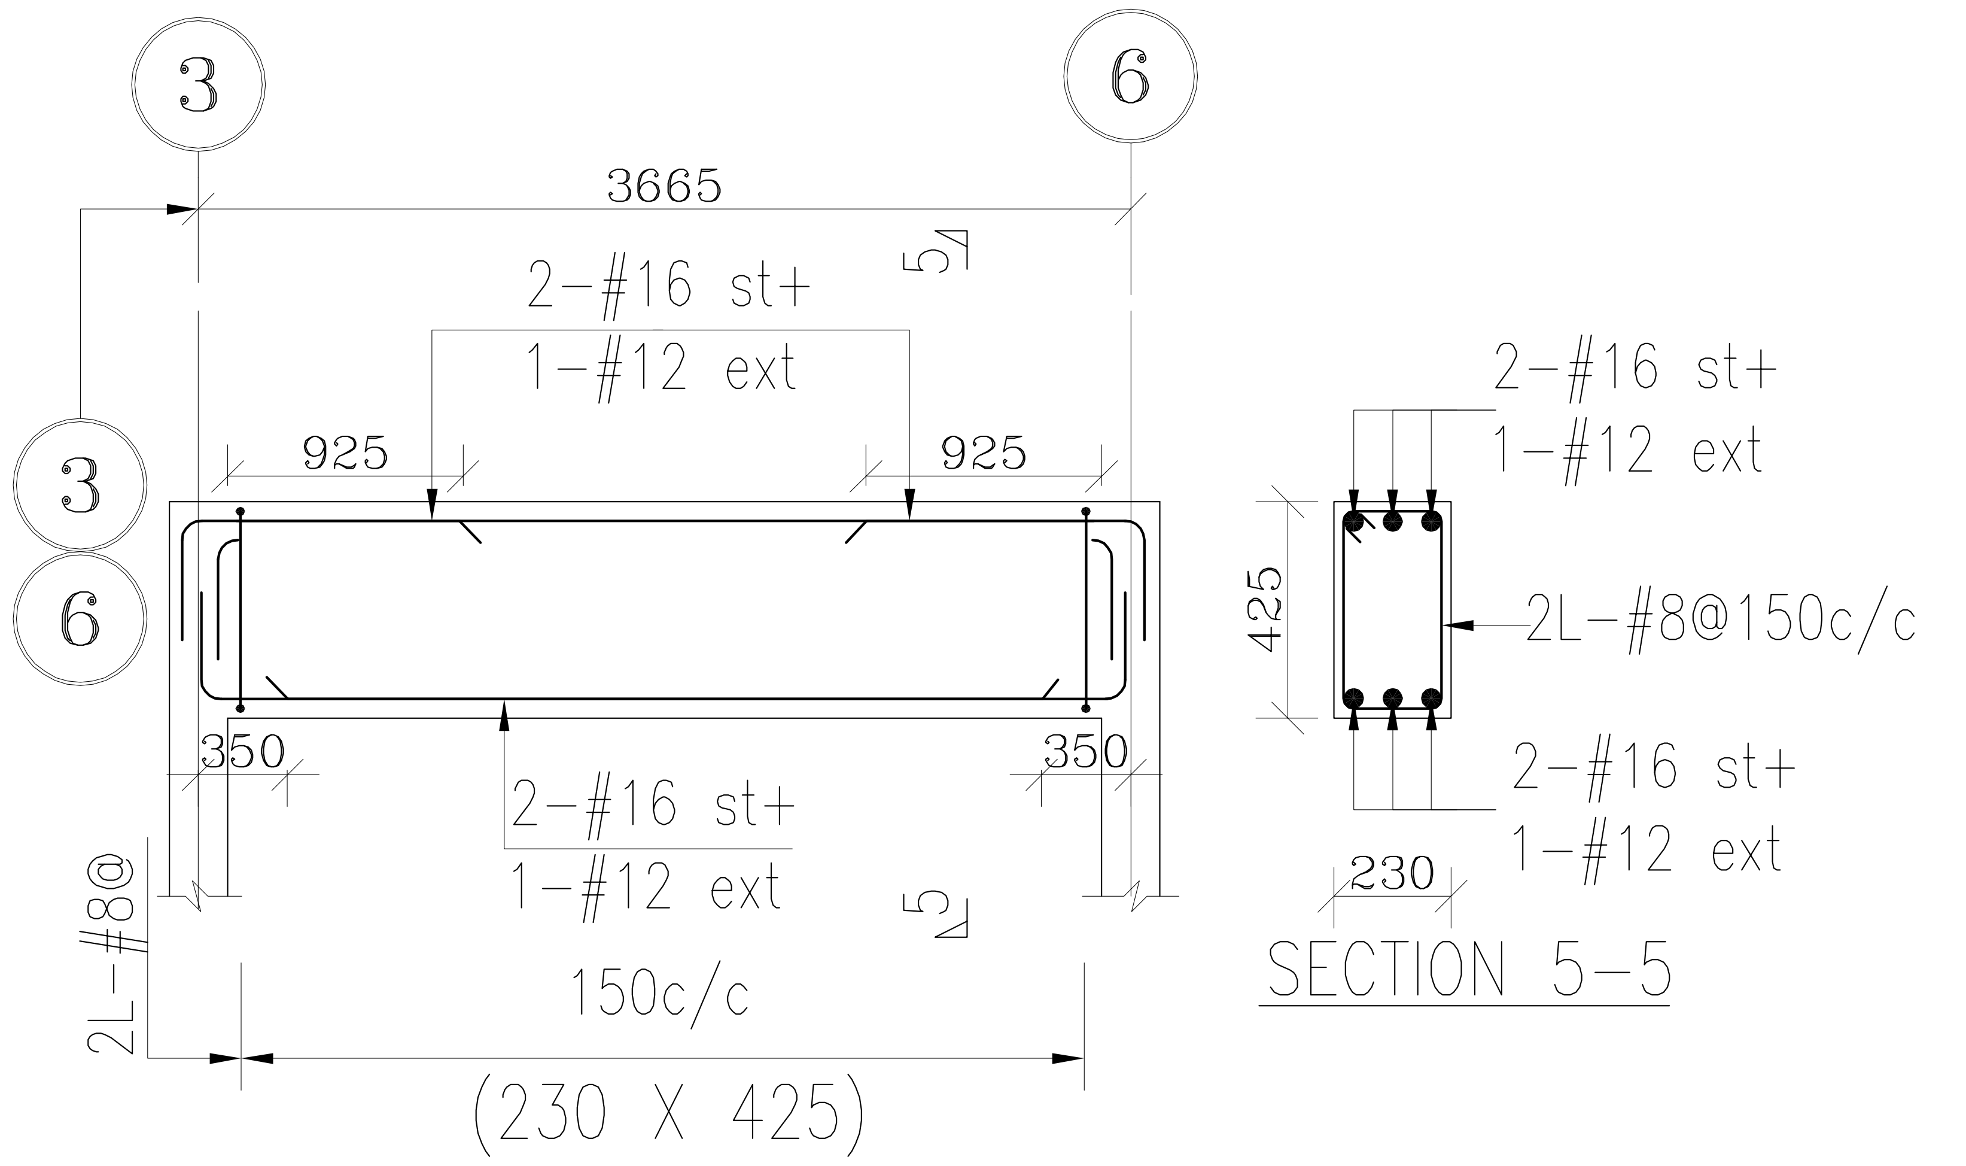

L/S OF BEAM B5(230X425)

- THIS DRAWING SHALL BE READ IN CONJUNCTION WITH ALL RELEVANT ARCHITECTURAL, STRUCTURAL AND SERVICES DRAWINGS. ANY DISCREPANCY NOTICED SHALL BE BROUGHT TO THE ATTENTION OF THE CONSULTANTS AND RESOLVED AS SOON AS POSSIBLE BUT ALWAYS PRIOR TO

DIRECTION:

N

ARCHITECTURAL CONSULTANT:

also. design
a little story of design

STRUCTURAL& MEP CONSULTANTS

JASHRITHA ASSOCIATES
AND MEP PLANNERS
4th FLOOR(4B), HIG 129, KPHB COLONY, KUKATPALLY,
(SUB BRANCH:PR NAGAR ERRAGADDA.)
HYDERABAD 500072, TELANGANA, INDIA
Phone : 9700441106.
E-mail : jashreyansh.consultatns@gmail.com
& jashritha.mep@gmail.com

PROJECT:

ANKURA HOMES_THE WOODS
AT KEESARAGUTTA

DRAWING TITLE:

1215_EAST VILLA
ROOF BEAM DETAILS

DESIGN ENGG : AJAY	APPROVED :
SCALE : NTS	DRAWN : PK
DATE : 23-09-2026	CHECKED : PRADEEP

DRAWING NO: SD-06 REV.NO: