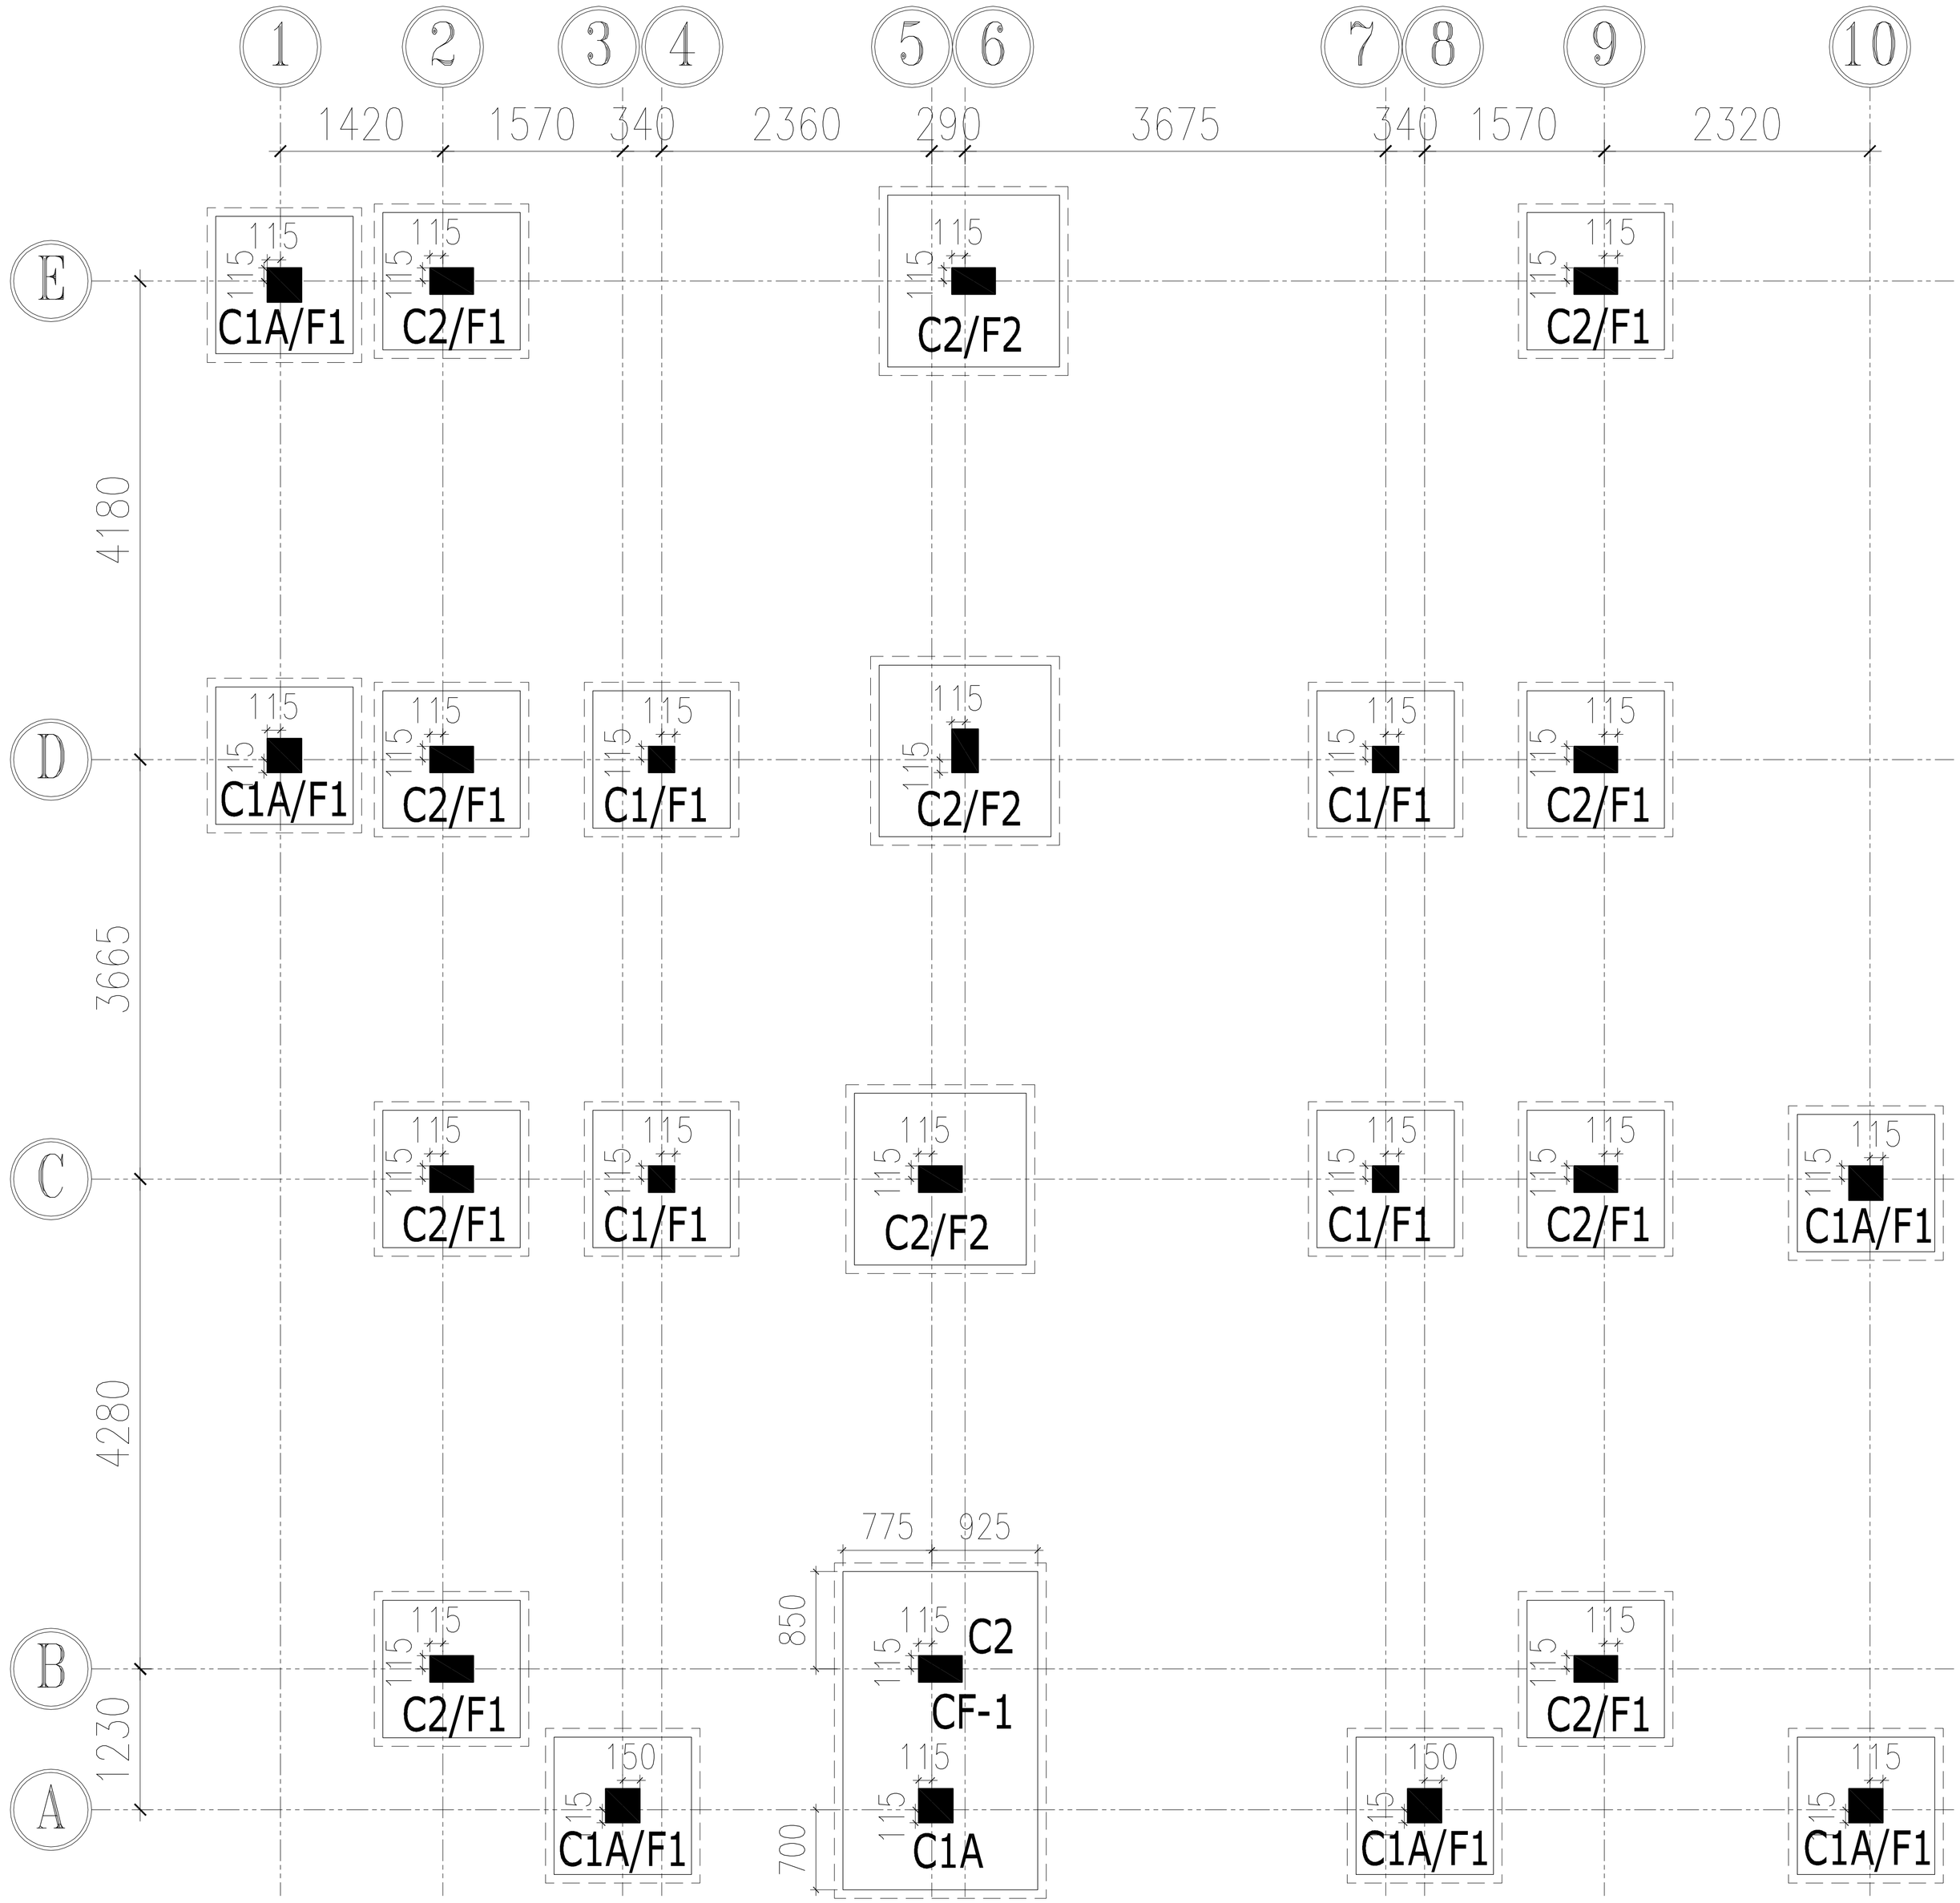


- THIS DRAWING SHALL BE READ IN CONJUNCTION WITH ALL RELEVANT ARCHITECTURAL, STRUCTURAL AND SERVICES DRAWINGS. ANY DISCREPANCY NOTICED SHALL BE BROUGHT TO THE ATTENTION OF THE CONSULTANTS AND RESOLVED AS SOON AS POSSIBLE BUT ALWAYS PRIOR TO

DIRECTION:

N

ARCHITECTURAL CONSULTANT:

also. design

STRUCTURAL& MEP CONSULTANTS

JASHRITHA ASSOCIATES
AND MEP PLANNERS
4th FLOOR#45, HIG 125, KPHB COLONY, KUKATPALLY,
(SUB BRANCH:PR NAGAR ERRAGADDA)
HYDERABAD 500072, TELANGANA, INDIA.
Phone : 9700441106,
E-mail# jashreyesh.consultants@gmail.com
& jashdhanu.mep@gmail.com

PROJECT:

ANKURA HOMES_THE WOODS
AT KEESARAGUTTA

DRAWING TITLE:

1215_WEST VILLA
MARKING PLAN




DESIGN ENGG : AJAY	APPROVED :
SCALE : NTS	DRAWN : PK
DATE : 07-10-2026	CHECKED : PRADEEP

DRAWING NO:	SD-01	REV.NO:	01

COLUMN SCHEDULE

COLUMN ID	GRADE OF CONCRETE	COLUMN SIZE UPTO GROUND FLOOR ROOF	REFERENCE SECTION
C1	M - 25	230 x 230 #12 -4Nos	A1
C1A	M - 25	300 x 300 #12 -4Nos	A1
C2	M - 25	230 x 380 #16 -4Nos + #12 -4Nos	A2

ARRANGEMENT OF TIES, LINKS & MAIN BARS IN COLUMN

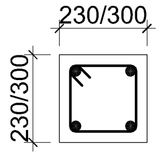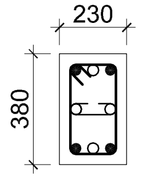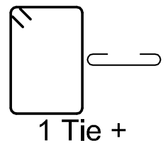4 BARS ARRANGEMENT		8 BARS ARRANGEMENT		
	 4 EQUAL DIA (A1)		 • 4 LARGER DIA ○ 4 LARGER DIA (A2)	 1 Tie + 1 Link #8 @150c/c

FLAT FOOTING SCHEDULE:

GROUP	MIX	SIZE	DEPTH	BOTTOM REINFORCEMENT PARALLEL TO	
				SHORTER DIRECTION	LONGER DIRECTION
F1	M - 25	1200 x 1200	375	#10 -10 NOS	#10 -10 NOS
F2	M - 25	1500 x 1500	400	#10 -15 NOS	#10 -15 NOS

COMBINED FOOTING SCHEDULE:

GROUP	MIX	SIZE	DEPTH	BOTTOM REINFORCEMENT	TOP REINFORCEMENT
				BOTH WAYS	BOTH WAYS
CF-1	M - 25	1700 x 2780	425	#10 -100 c/c	#10 -150 c/c

GENERAL NOTES:

1. DO NOT SCALE THIS DRAWING. FOLLOW FIGURED DIMENSIONS ONLY.
2. ALL DIMENSIONS ARE IN MM ONLY AND LEVELS ARE IN METERS UNLESS SPECIFIED.
3. S.B.C OF SOIL IS CONSIDERED AS 270 KN/M^2 @ 2.0M DEPTH
4. USE VIBRATED REINFORCED CONCRETE CONFORMING TO IS:456-2000. THE GRADES FOR DIFFERENT COMPONENTS ARE AS FOLLOWS

COMPONENT	FOOTING	COLUMNS	BEAMS	SLABS	WATER TANK SIDE WALLS
MIX	M25	M25	M25	M25	M25


5. GRADE OF STEEL SHALL BE Fe 500 CONFORMING TO IS:1786-85 & AMENDMENTS.
6. LAPS SHALL BE STAGGERED AND LAP LENGTHS ARE AS FOLLOWS.

MIX	M25
Ld	48 Dia


7. NOT MORE THAN 50% OF COLUMN REINFORCEMENT SHALL BE LAPPED AT A PARTICULAR LOCATION.
8. CLEAR COVERS ARE AS FOLLOWS

FOOTING TO MAIN BAR	COLUMN TO MAIN BAR	BEAMS TO STIRRUPS	SLABS TO MAIN BAR
50mm	40mm	20mm	20mm


9. CURING SHOULD BE DONE ATLEAST FOR 21 DAYS.
10. THIS DRAWING SHOULD BE READ IN CONJUNCTION WITH RELEVANT ARCHITECTURAL DRAWINGS.
11. STRIPPING TIME OF FORMWORK SHALL CONFORM TO CLAUSE 11.3 OF IS:456-2000.
12. FOR TIES,LINKS IN COLUMNS Y8-150mm c/c REFER COLUMN SCHEDULE DWG.
13. FOR EXACT LOCATION OF WALLS REFER RELEVANT ARCHITECTURAL DRAWINGS FOR NECESSARY DETAILS.
14. ANY DISCREPANCY FROM THE DRAWING SHALL BE BROUGHT TO THE NOTICE OF CONSULTANTS.
15. THE STRUCTURE IS DESIGNED FOR GROUND FLOOR ONLY

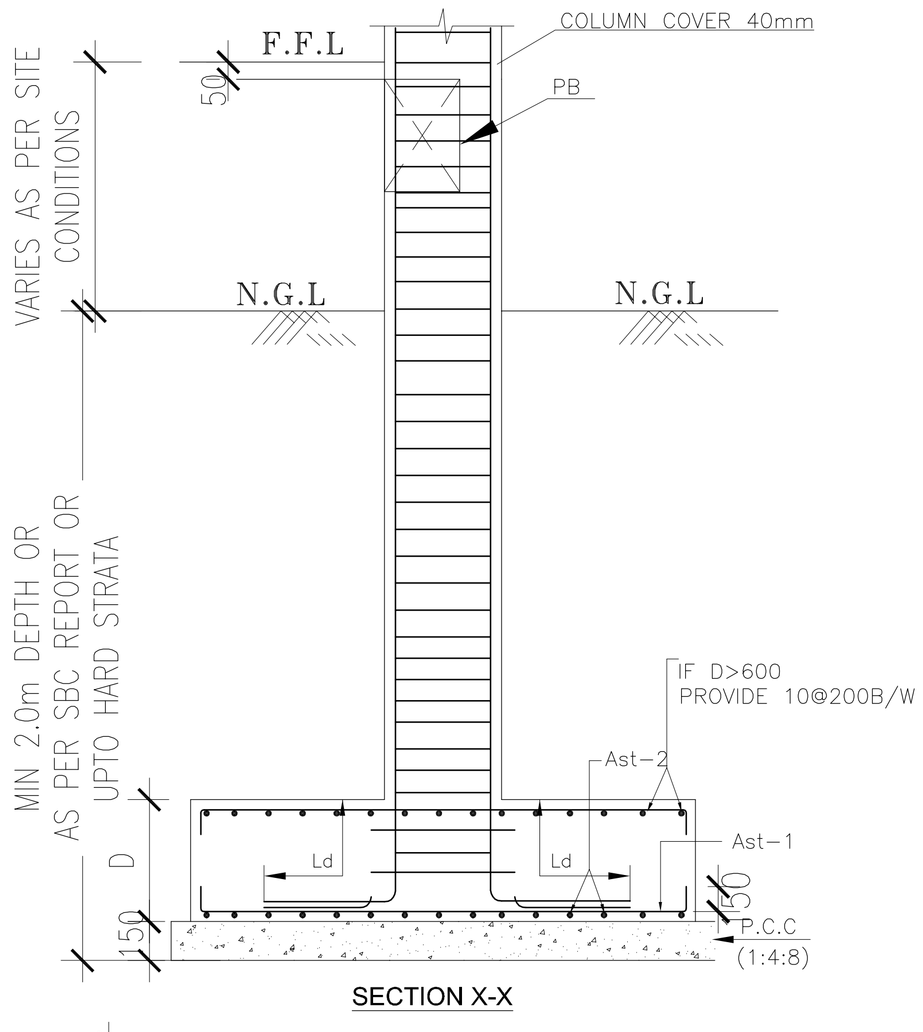

SECTION X-X

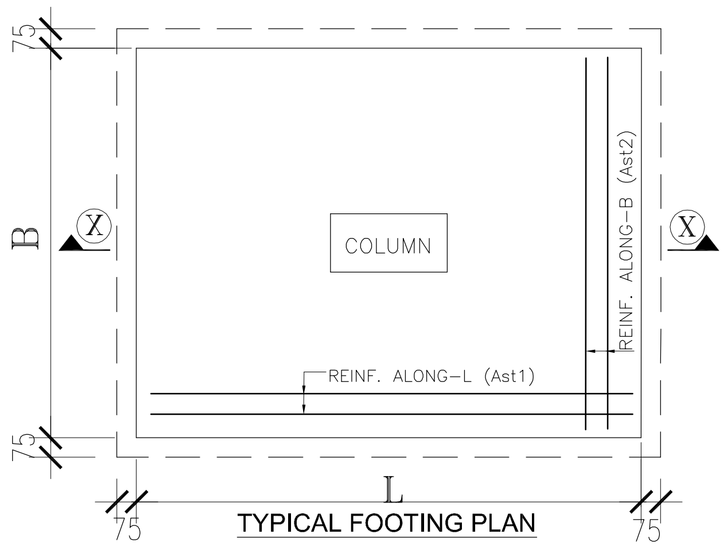

TYPICAL FOOTING PLAN

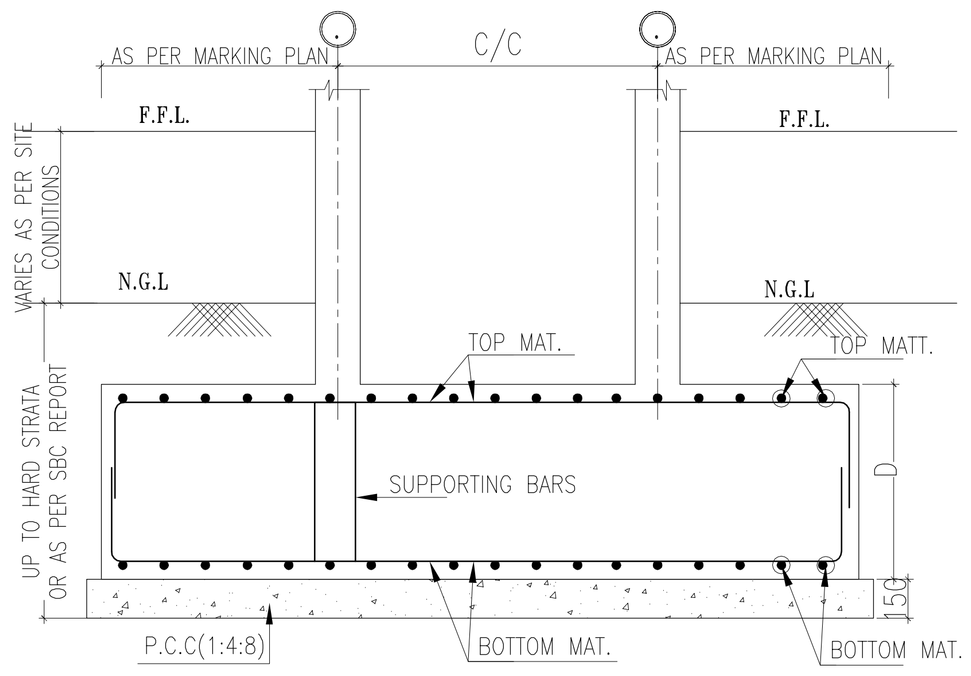

TYPICAL SECTION OF COMBINED FOOTING

- THIS DRAWING SHALL BE READ IN CONJUNCTION WITH ALL RELEVANT ARCHITECTURAL, STRUCTURAL AND SERVICES DRAWINGS. ANY DISCREPANCY NOTICED SHALL BE BROUGHT TO THE ATTENTION OF THE CONSULTANTS AND RESOLVED AS SOON AS POSSIBLE BUT ALWAYS PRIOR TO

ARCHITECTURAL CONSULTANT:

also. design

STRUCTURAL& MEP CONSULTANTS

JASHRITHA ASSOCIATES
AND MEP PLANNERS
4th FLOOR#81, HIG 121,KPHB COLONY, KUKATPALLY,
(SUB BRANCH:SRI NAGAR ERRAGADDA)
HYDERABAD 500072, TELANGANA,INDIA.
Phone : 9700441106,
E-mail:jashreyesh.consultants@gmail.com
& jashritha.mep@gmail.com


PROJECT:


ANKURA HOMES_THE WOODS
AT KEESARAGUTTA

DRAWING TITLE:


1215_WEST VILLA
COLUMN & FOOTING
SCHEDULE

DESIGN ENGG : AJAY	APPROVED :
SCALE : NTS	DRAWN : PK
DATE : 07-10-2026	CHECKED : PRADEEP
DRAWING NO: SD-02	REV.NO: 01

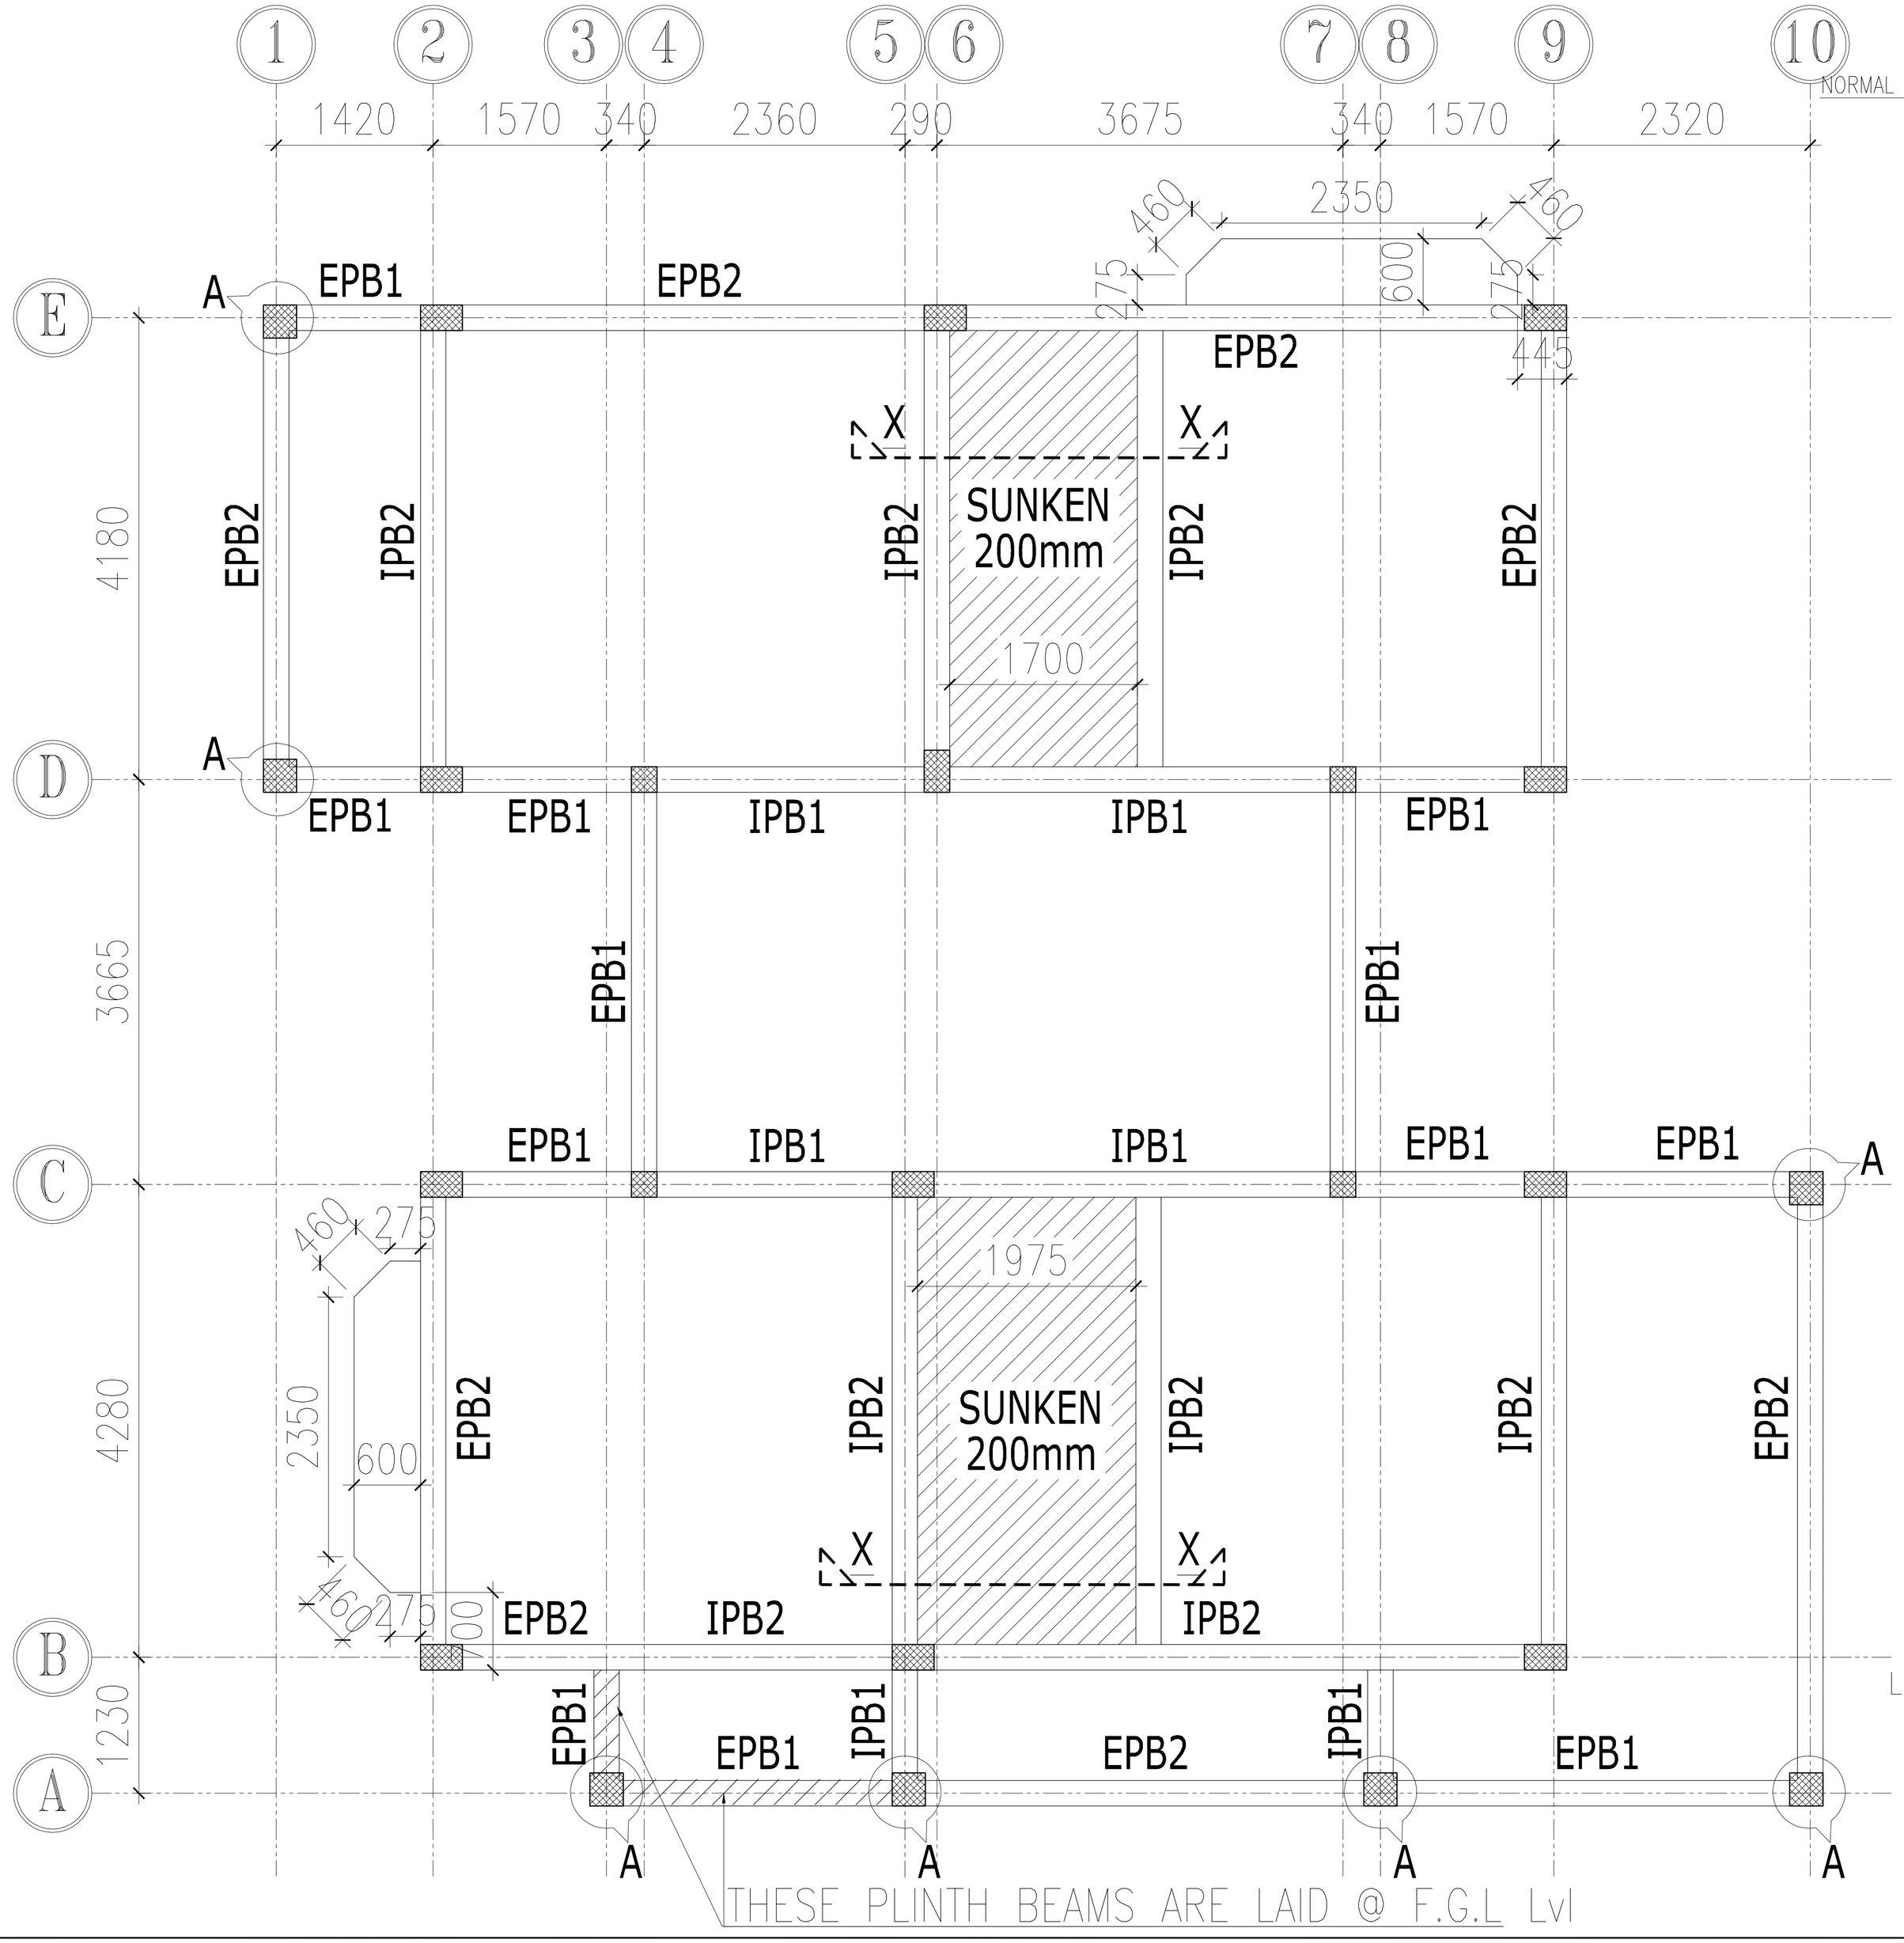


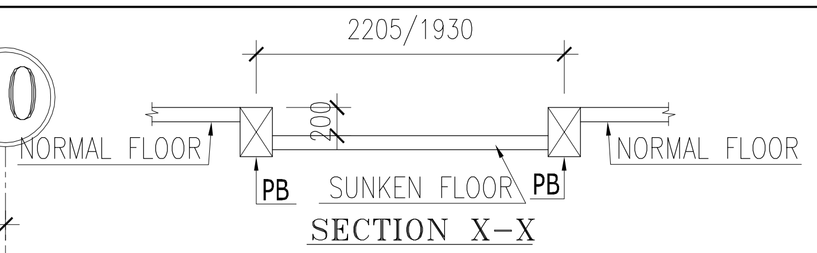

SECTION X–X

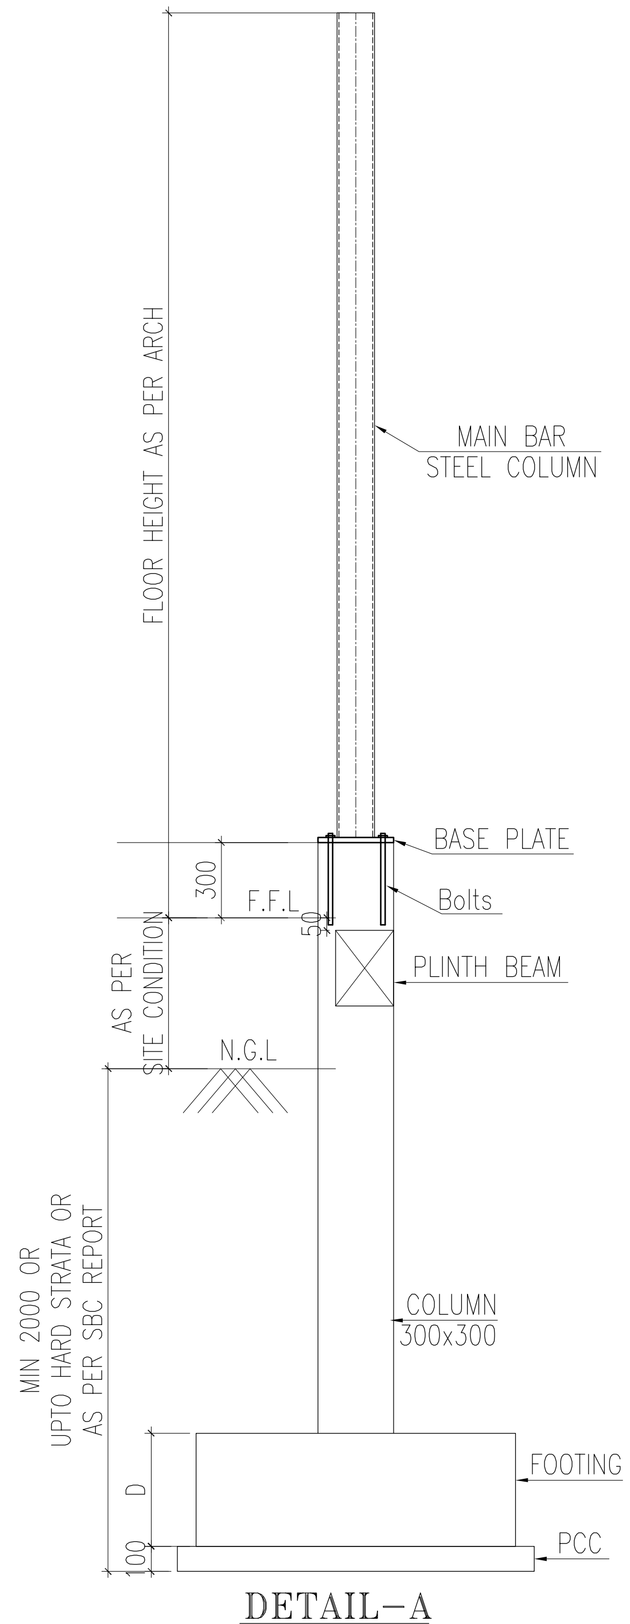

DETAIL–A

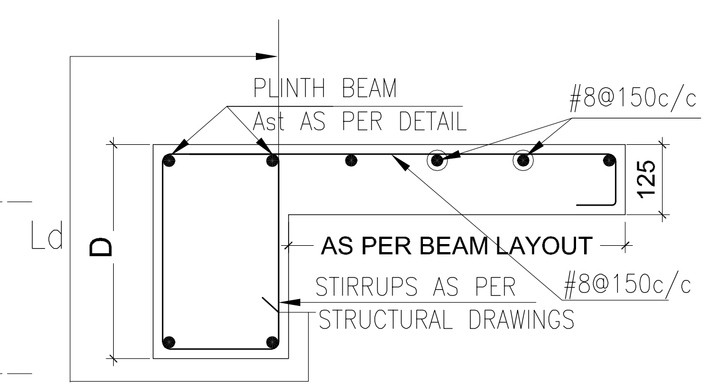

TYPICAL
SLAB PROJECTION DETAILS

- THIS DRAWING SHALL BE READ IN CONJUNCTION WITH ALL RELEVANT ARCHITECTURAL, STRUCTURAL AND SERVICES DRAWINGS. ANY DISCREPANCY NOTICED SHALL BE BROUGHT TO THE ATTENTION OF THE CONSULTANTS AND RESOLVED AS SOON AS POSSIBLE BUT ALWAYS PRIOR TO

DIRECTION:

ARCHITECTURAL CONSULTANT:

also. design

STRUCTURAL& MEP CONSULTANTS

JASHRITHA ASSOCIATES
AND MEP PLANNERS
4th FLOOR(MB), HB-129, NTHB COLONY, KUKATPALLY.
(SUB BRANCH)PB NAGAR ERRAGADDA,
HYDERABAD-500072, TELANGANA, INDIA.
Phone : 9700441106,
E-mail# jashmepsmch.consultants@gmail.com
& jashdhanumep@gmail.com


PROJECT:

ANKURA HOMES_THE WOODS
AT KEESARAGUTTA


DRAWING TITLE:

1215_WEST VILLA
PLINTH BEAM LAYOUT


DESIGN ENGG : AJAY	APPROVED :
SCALE : NTS	DRAWN : PK
DATE : 07-10-2026	CHECKED : PRADEEP
DRAWING NO: SD-03	REV.NO: 01

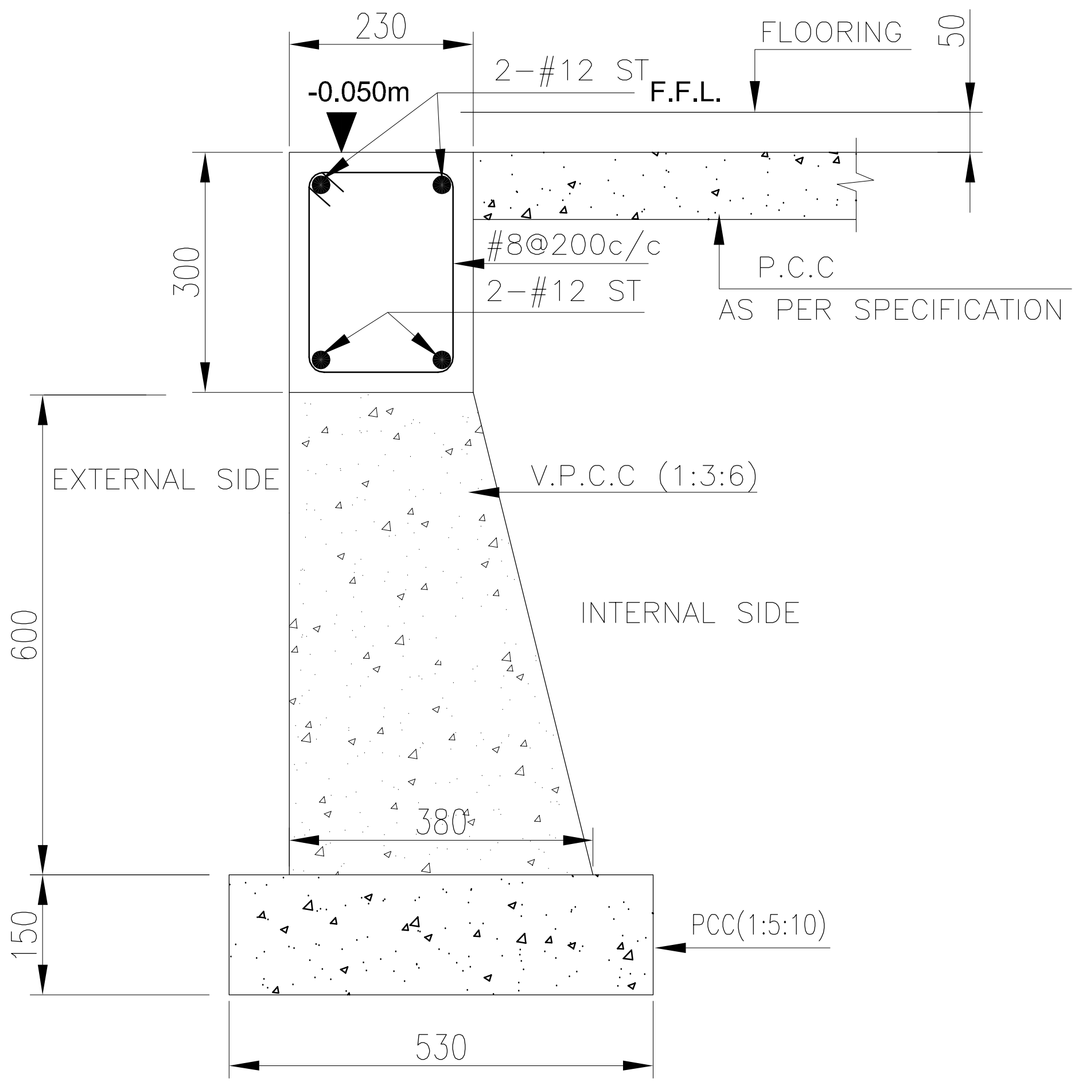


EPB1

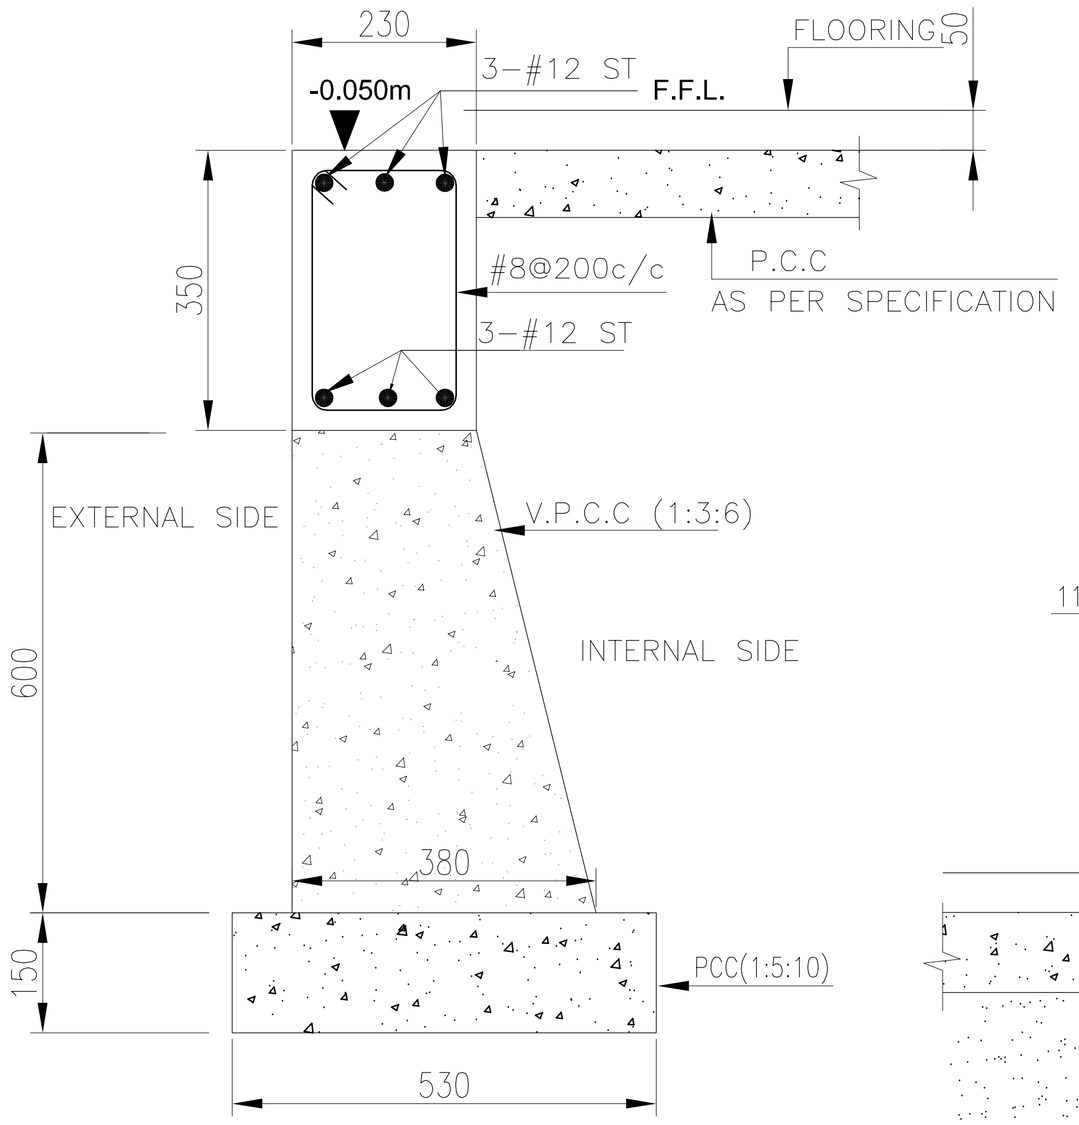


EPB2

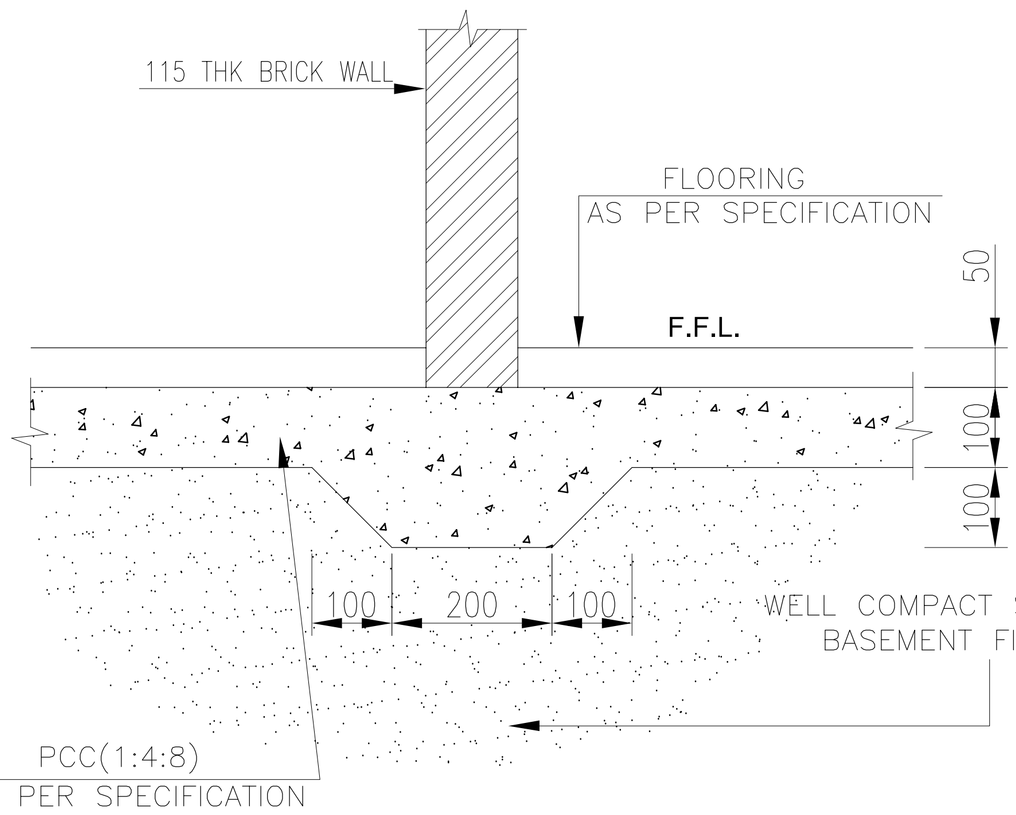

FOUNDATION DETAIL UNDER
115mm THICK BRICK WALL

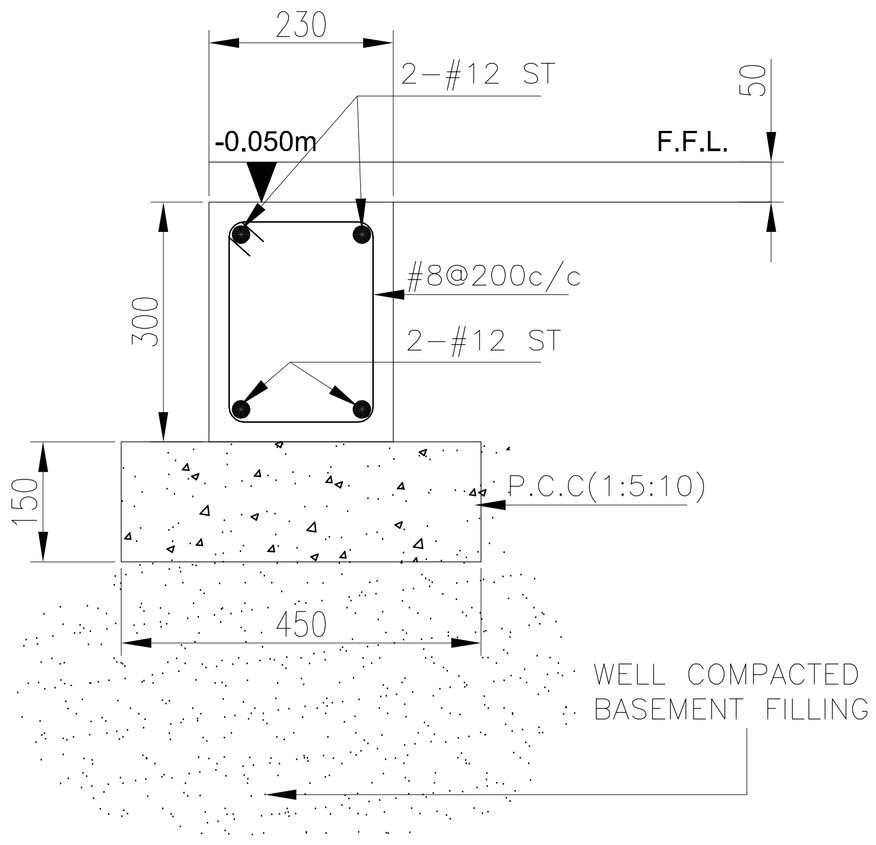

IPB1

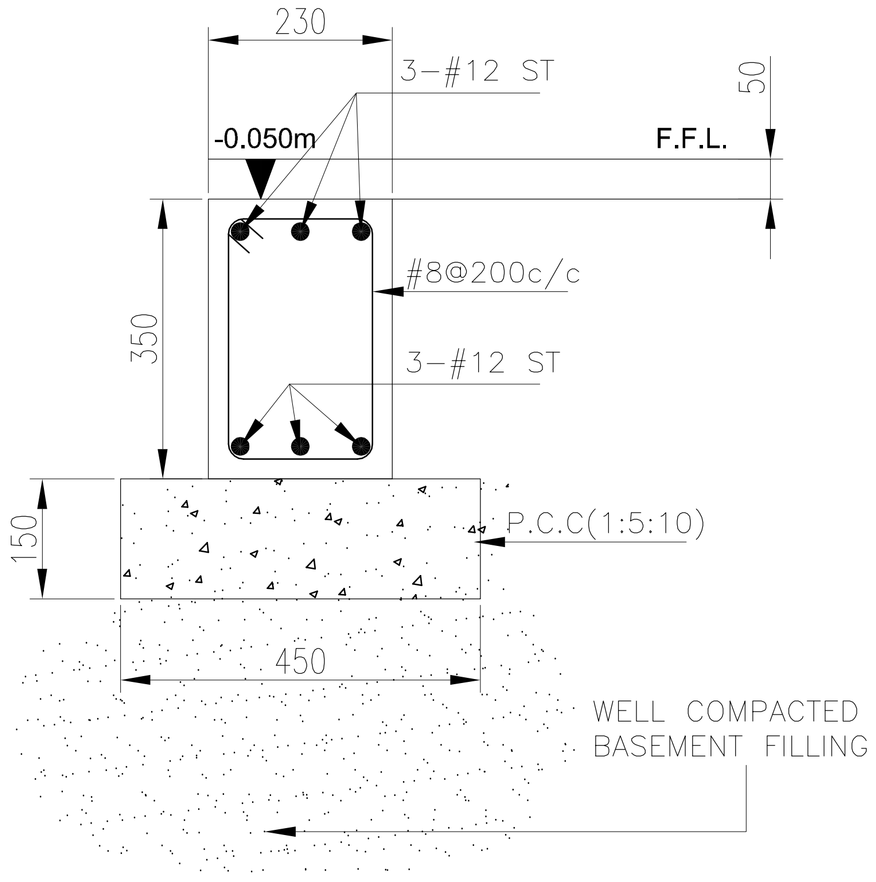

IPB2

- THIS DRAWING SHALL BE READ IN CONJUNCTION WITH ALL RELEVANT ARCHITECTURAL, STRUCTURAL AND SERVICES DRAWINGS. ANY DISCREPANCY NOTICED SHALL BE BROUGHT TO THE ATTENTION OF THE CONSULTANTS AND RESOLVED AS SOON AS POSSIBLE BUT ALWAYS PRIOR TO

ARCHITECTURAL CONSULTANT:

also. design

STRUCTURAL& MEP CONSULTANTS

JASHRITHA ASSOCIATES
AND MEP PLANNERS
4th FLOOR#B1-120,KPHB COLONY, KUKATPALLY.
(SUB BRANCH:PR NAGAR ERRAGADDA)
HYDERABAD 500072, TELANGANA, INDIA.
Phone : 9700441106,
E-mail:(jashreyesh.consultants@gmail.com
& jash@hu.mep@gmail.com

PROJECT:


ANKURA HOMES_THE WOODS
AT KEESARAGUTTA

DRAWING TITLE:

1215_WEST VILLA
PLINTH BEAM DETAILS

DESIGN ENGG : AJAY	APPROVED :
SCALE : NTS	DRAWN : PK
DATE : 26-09-2026	CHECKED : PRADEEP

DRAWING NO: SD-04 REV.NO:

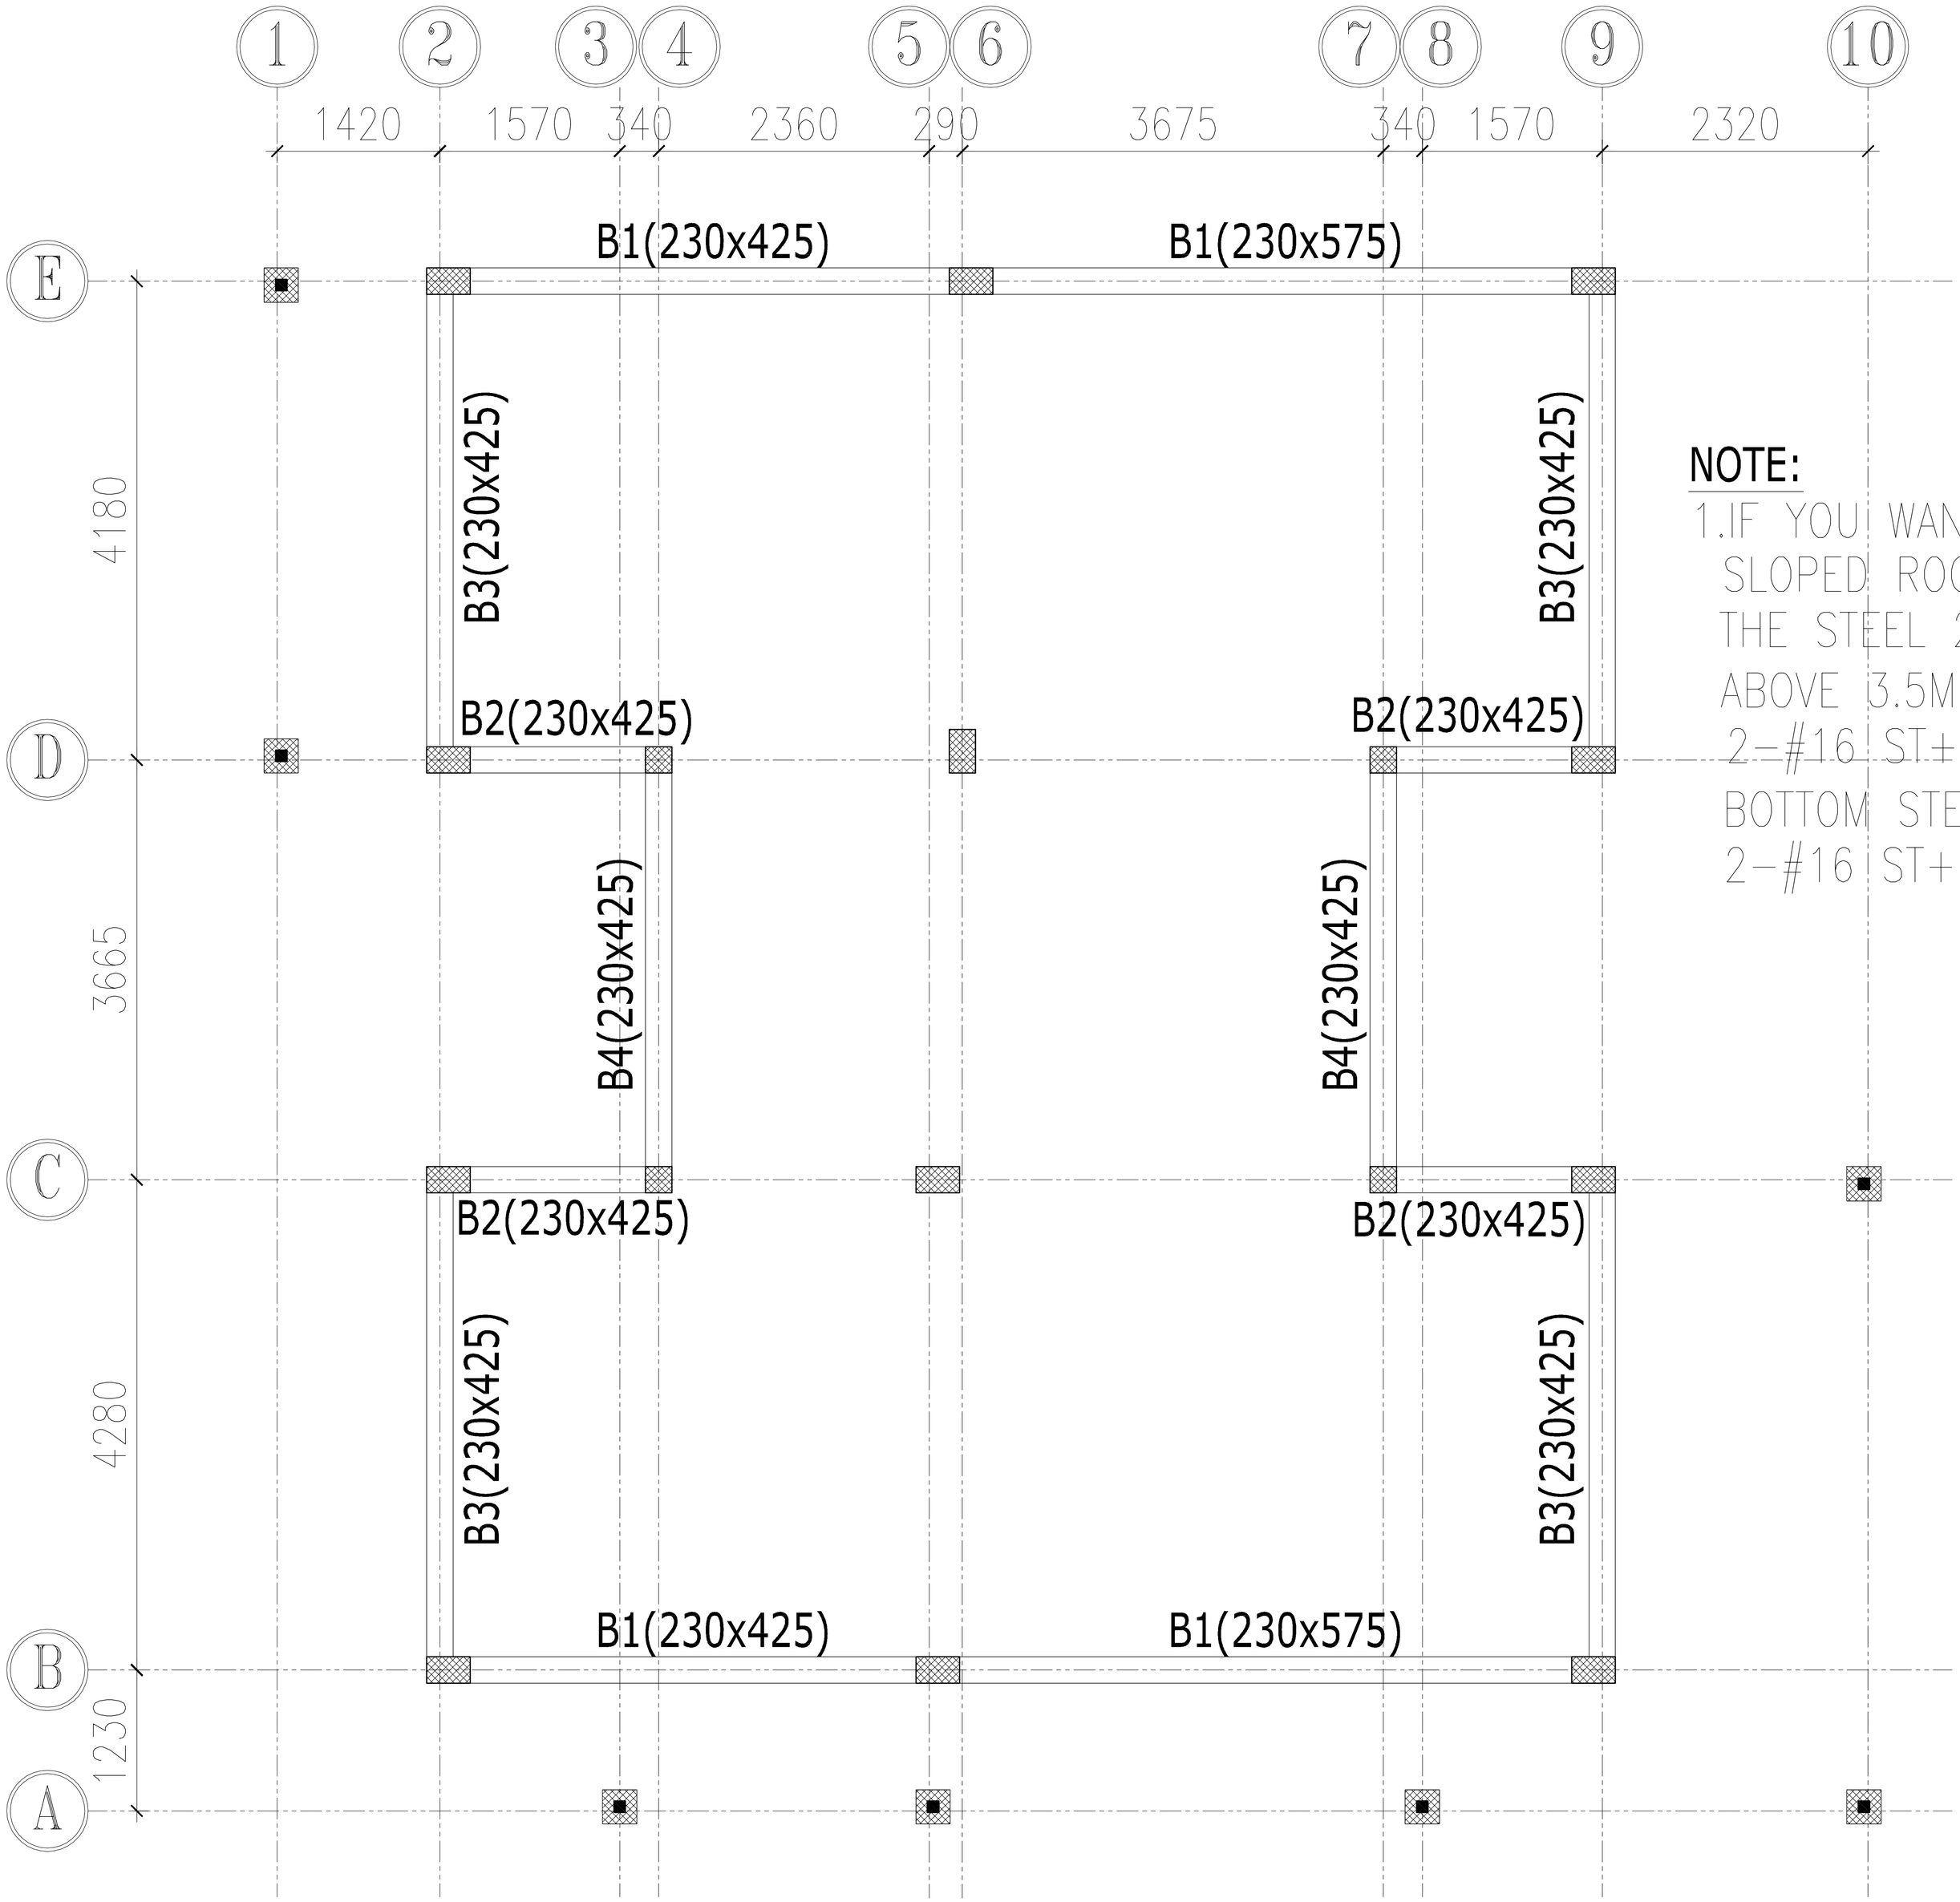

NOTE:

1. IF YOU WANT ANY INTERNAL BEAMS FOR SLOPED ROOF STRUCTURE PLEASE MAINTAIN THE STEEL 2-#16(Top&Bottom) UPTO 3.5M ABOVE 3.5M SPAN MAINTAIN TOP STEEL 2-#16 ST+ 2-#12 EXT @ SUPPORTS BOTTOM STEEL 2-#16 ST+ 2-#12 EXT @ MID SPAN

- THIS DRAWING SHALL BE READ IN CONJUNCTION WITH ALL RELEVANT ARCHITECTURAL, STRUCTURAL AND SERVICES DRAWINGS. ANY DISCREPANCY NOTICED SHALL BE BROUGHT TO THE ATTENTION OF THE CONSULTANTS AND RESOLVED AS SOON AS POSSIBLE BUT ALWAYS PRIOR TO

DIRECTION:

ARCHITECTURAL CONSULTANT:

also. design

STRUCTURAL& MEP CONSULTANTS

JASHRITHA ASSOCIATES
AND MEP PLANNERS
4th FLOOR#EL-483 125 KPHB COLONY, KUKATPALLY,
(SUB BRANCH)PRINAGAR ERRAGADDA)
HYDERABAD 500072, TELANGANA, INDIA.
Phone : 9700441106,
E-mail# jashreyestructconsultants@gmail.com
& jashdhanmep@gmail.com

PROJECT:


ANKURA HOMES_THE WOODS
AT KEESARAGUTTA

DRAWING TITLE:


1215_WEST VILLA
ROOF BEAM LAYOUT


DESIGN ENGG : AJAY	APPROVED :
SCALE : NTS	DRAWN : PK
DATE : 07-10-2026	CHECKED : PRADEEP

DRAWING NO:	SD-05	REV.NO:	01

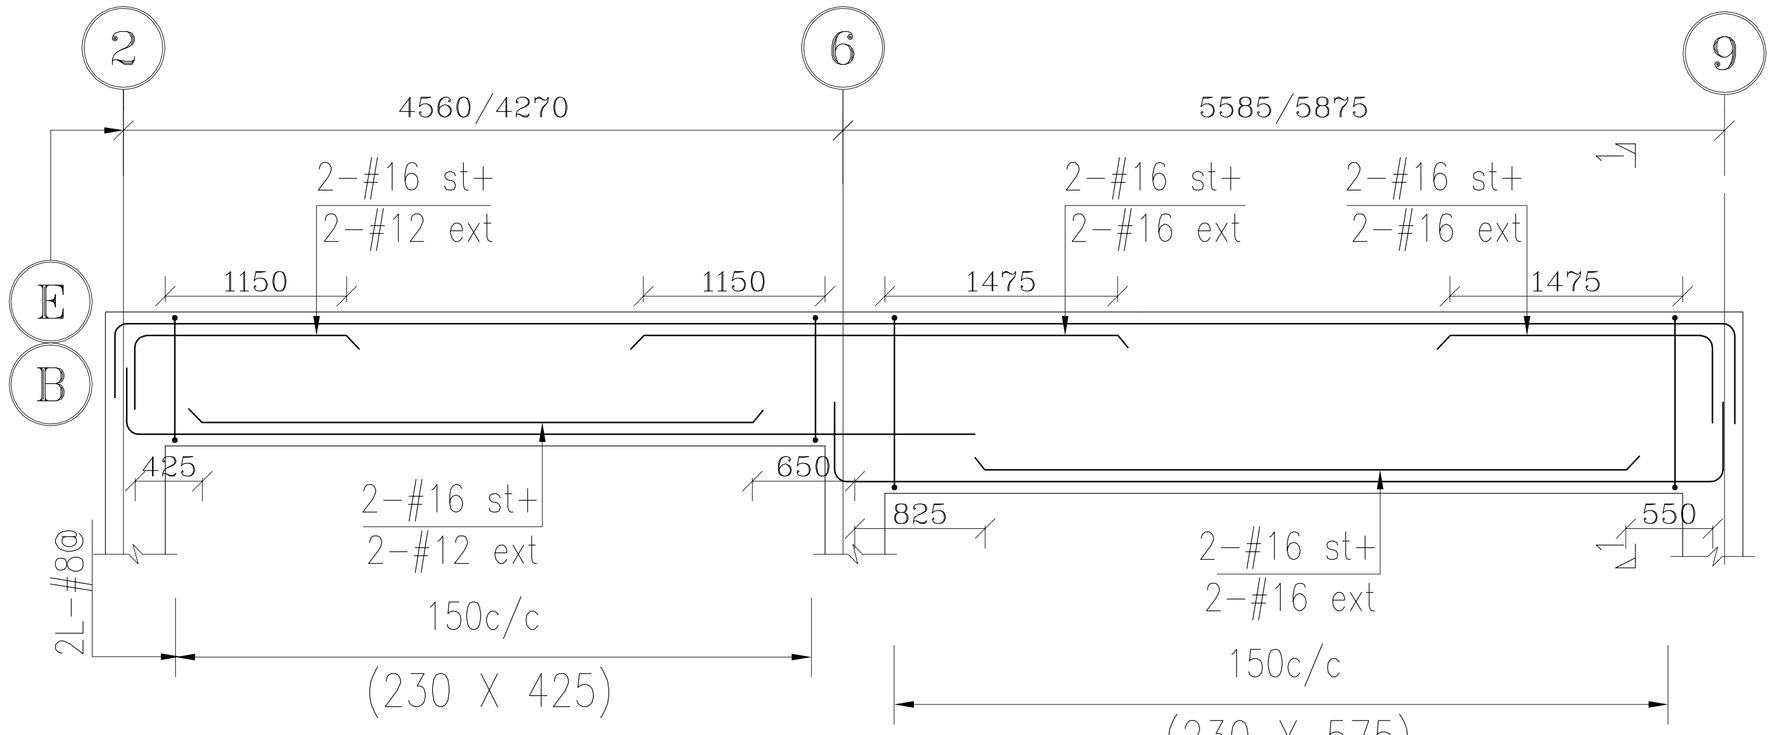


L/S OF BEAM B1(230X425/575)

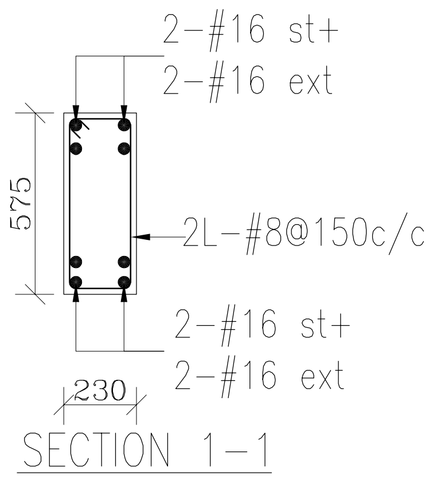


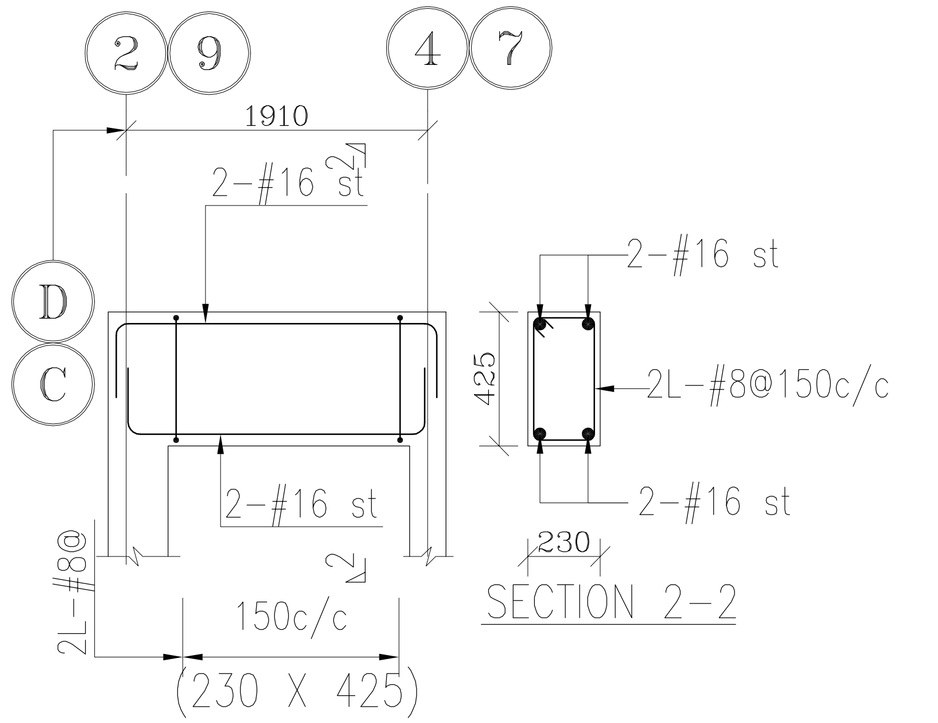

L/S OF BEAM B2(230X425)

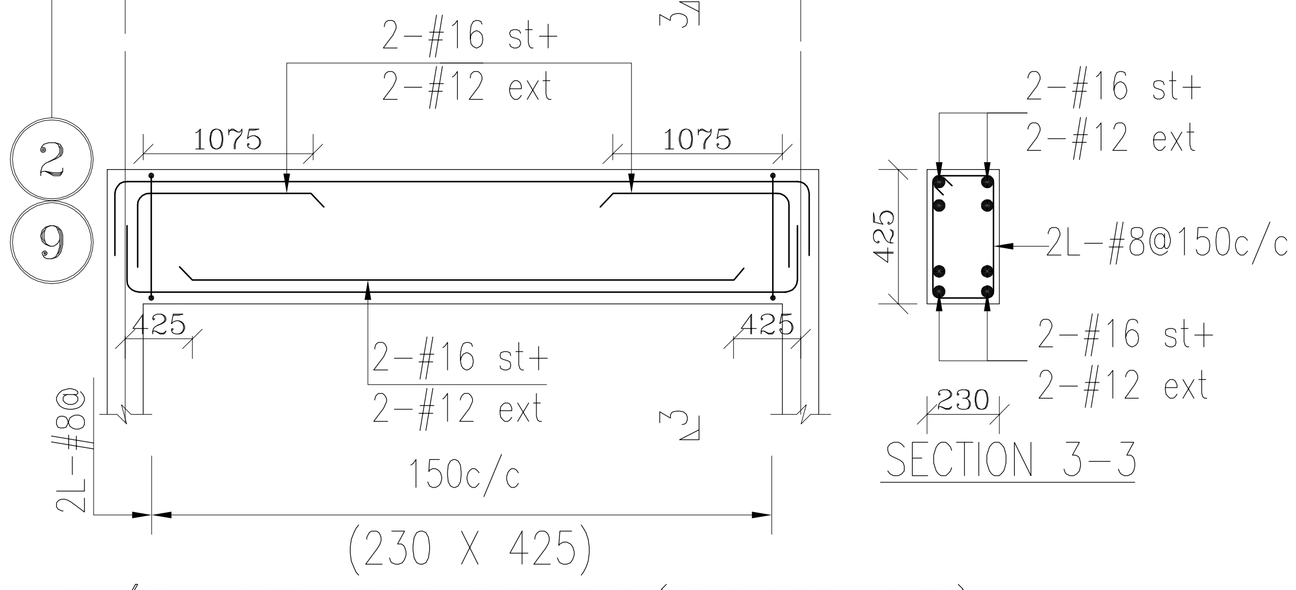

L/S OF BEAM B3(230X425)

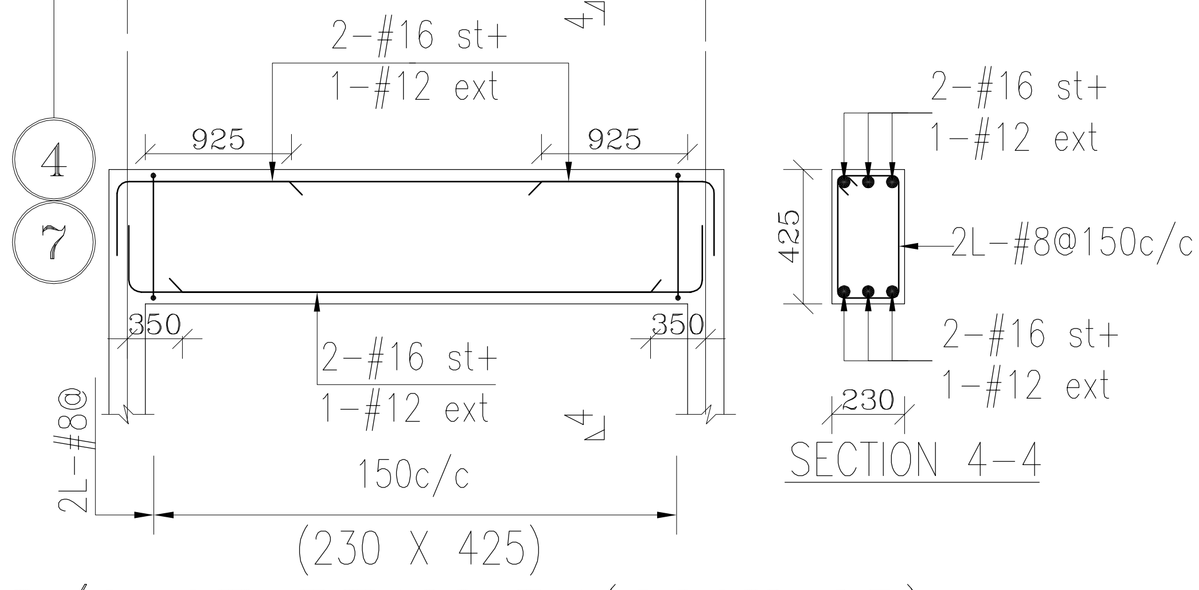

L/S OF BEAM B4(230X425)

- THIS DRAWING SHALL BE READ IN CONJUNCTION WITH ALL RELEVANT ARCHITECTURAL, STRUCTURAL AND SERVICES DRAWINGS. ANY DISCREPANCY NOTICED SHALL BE BROUGHT TO THE ATTENTION OF THE CONSULTANTS AND RESOLVED AS SOON AS POSSIBLE BUT ALWAYS PRIOR TO

DIRECTION:

ARCHITECTURAL CONSULTANT:

also. design

STRUCTURAL& MEP CONSULTANTS

JASHRITHA ASSOCIATES
AND MEP PLANNERS
4th FLOOR(BB), HIG 125, KPHB COLONY, KUKATPALLY,
(SUB BRANCH OF PH NAGAR ERRAGADDA)
HYDERABAD-500072, TELANGANA, INDIA.
Phone : 9705641105,
E-mail# jashreyansh.consultants@gmail.com
& Jashritha.mep@gmail.com

PROJECT:

ANKURA HOMES_THE WOODS
AT KEESARAGUTTA

DRAWING TITLE:

1215_WEST VILLA
ROOF BEAM DETAILS

DESIGN ENGG : AJAY	APPROVED :
SCALE : NTS	DRAWN : PK
DATE : 26-09-2026	CHECKED : PRADEEP

DRAWING NO:	SD-06	REV.NO: