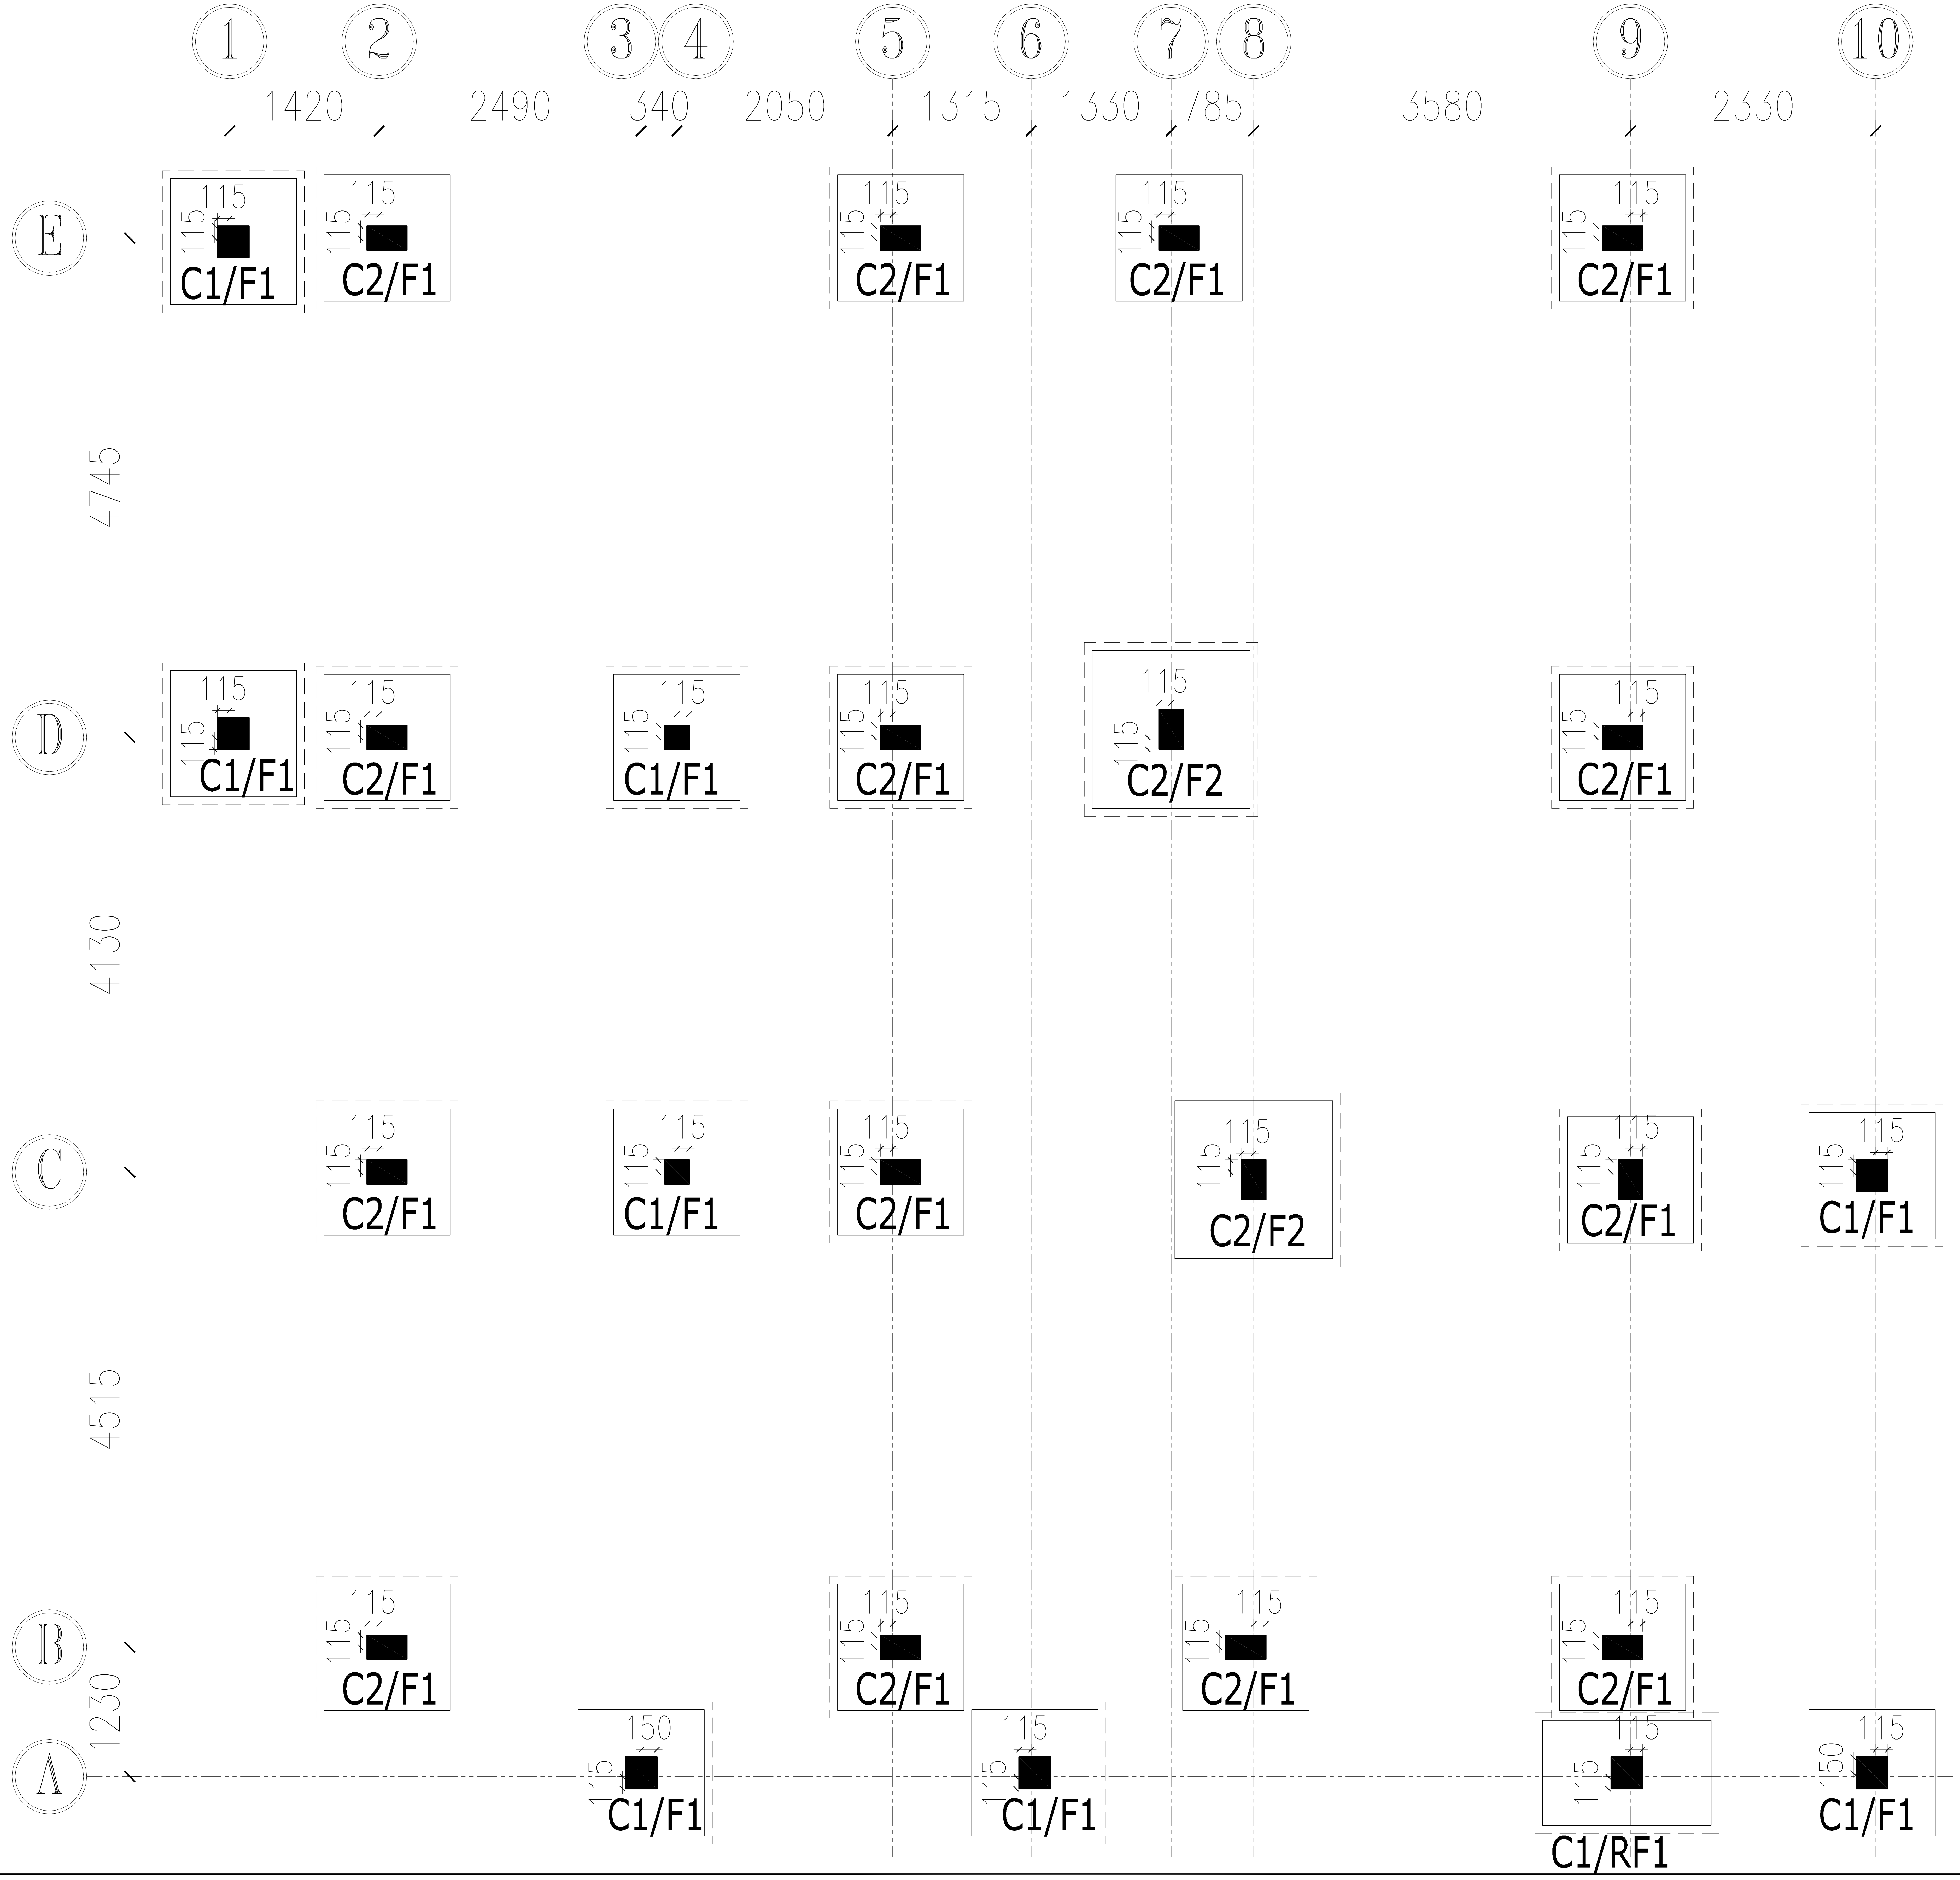
1
2
3
4
5
6
7
8
9
10
1420
2490
340
2050
1315
1330
785
3580
2330
E
D
C
B
A
4745
4130
4515
1230
115
C1/F1
C2/F1
C2/F2
C1/RF1
150

- THIS DRAWING SHALL BE READ IN CONJUNCTION WITH ALL RELEVANT ARCHITECTURAL, STRUCTURAL AND SERVICES DRAWINGS. ANY DISCREPANCY NOTICED SHALL BE BROUGHT TO THE ATTENTION OF THE CONSULTANTS AND RESOLVED AS SOON AS POSSIBLE BUT ALWAYS PRIOR TO

DIRECTION:

N

ARCHITECTURAL CONSULTANT:

also.
design
a little story of design

STRUCTURAL& MEP CONSULTANTS

JASHRITHA ASSOCIATES
AND MEP PLANNERS
4th FLOOR(4B), HIG 129, KPHB COLONY, KUKATPALLY,
(SUB BRANCH:PR NAGAR ERRAGADDA.)
HYDERABAD 500072, TELANGANA, INDIA
Phone : 9700441106.
E-mail : jashreyansh.consultatns@gmail.com
& jashritha.mep@gmail.com

PROJECT:

ANKURA HOMES_THE WOODS
AT KEESARAGUTTA

DRAWING TITLE:

1625_WEST VILLA
MARKING PLAN

DESIGN ENGG : AJAY	APPROVED :
SCALE : NTS	DRAWN : PK
DATE : 07-10-2026	CHECKED : PRADEEP
DRAWING NO: SD-01	REV.NO: 01

COLUMN SCHEDULE

COLUMN ID	GRADE OF CONCRETE	COLUMN SIZE	REFERENCE SECTION
C1	M - 25	300 x 300 #12 -4Nos	A1
C2	M - 25	230 x 380 #16 -4Nos + #12 -4Nos	A2

ARRANGEMENT OF TIES, LINKS & MAIN BARS IN COLUMN

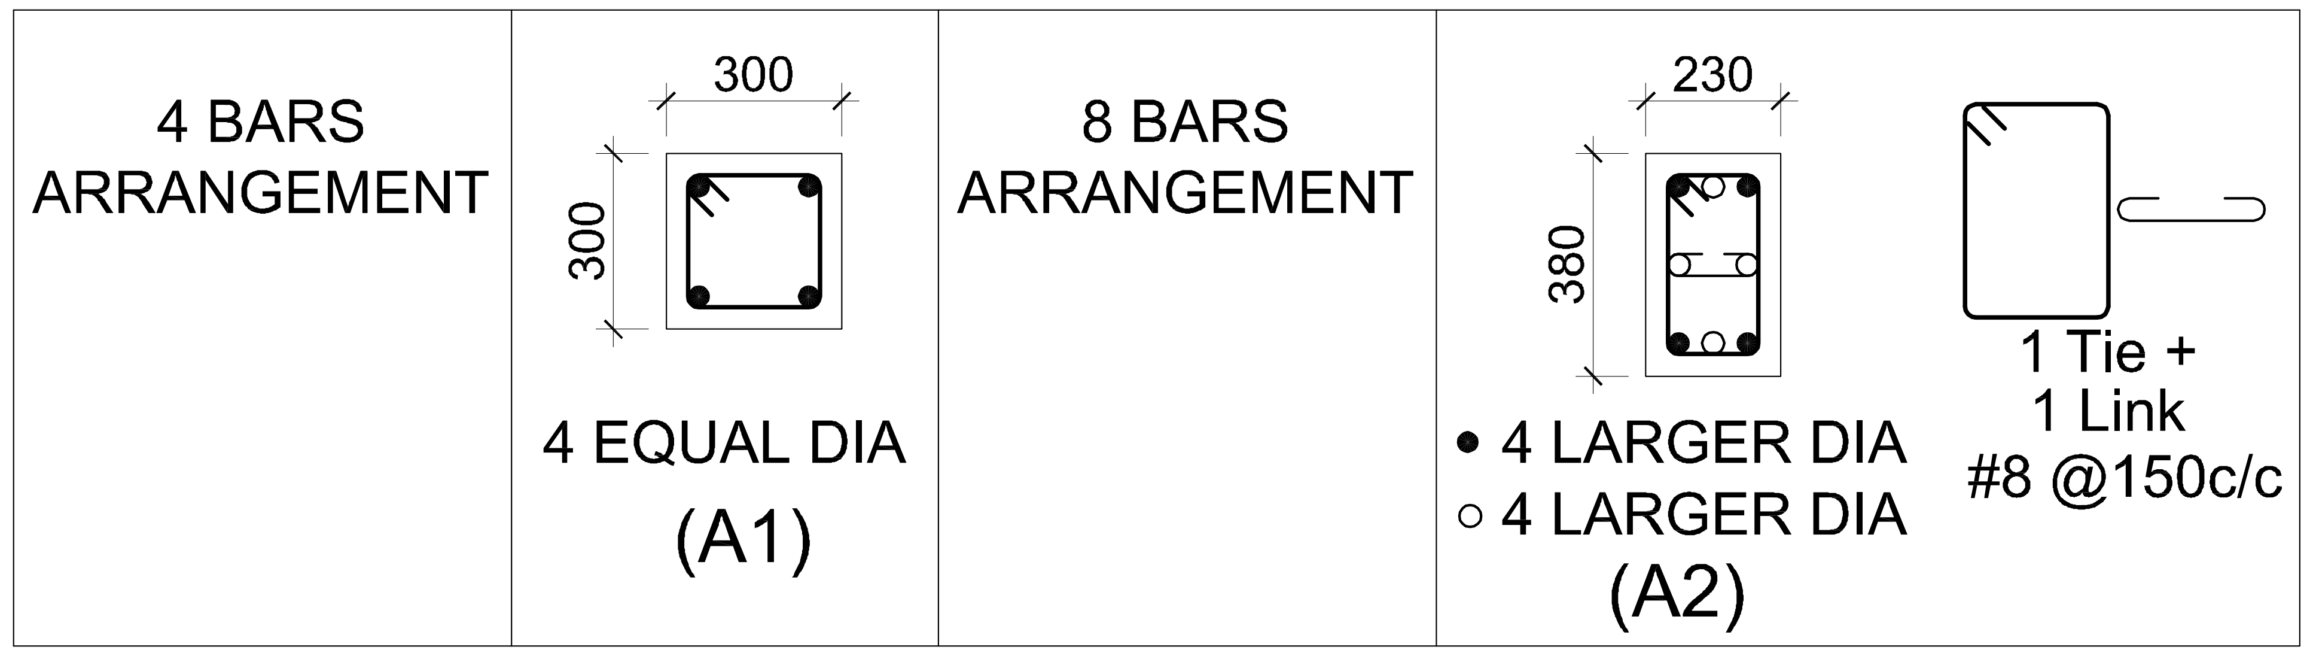
4 BARS ARRANGEMENT
300
300
4 EQUAL DIA
(A1)
8 BARS ARRANGEMENT
230
380
● 4 LARGER DIA
○ 4 LARGER DIA
(A2)
1 Tie +
1 Link
#8 @150c/c

FLAT FOOTING SCHEDULE:

GROUP	MIX	SIZE	DEPTH	BOTTOM REINFORCEMENT PARALLEL TO	
				SHORTER DIRECTION	LONGER DIRECTION
F1	M - 25	1200 x 1200	375	#10 -10 NOS	#10 -10 NOS
F2	M - 25	1500 x 1500	400	#10 -15 NOS	#10 -15 NOS
RF1	M - 25	1600 x 1000	400	#10 -16 NOS	#10 - 8 NOS

GENERAL NOTES:

1. DO NOT SCALE THIS DRAWING. FOLLOW FIGURED DIMENSIONS ONLY.
2. ALL DIMENSIONS ARE IN MM ONLY AND LEVELS ARE IN METERS UNLESS SPECIFIED.
3. S.B.C OF SOIL IS CONSIDERED AS 270 KN/M^2 @ 2.0M DEPTH
4. USE VIBRATED REINFORCED CONCRETE CONFORMING TO IS:456-2000. THE GRADES FOR DIFFERENT COMPONENTS ARE AS FOLLOWS

COMPONENT	FOOTING	COLUMNS	BEAMS	SLABS	WATER TANK SIDE WALLS
MIX	M25	M25	M25	M25	M25

5. GRADE OF STEEL SHALL BE Fe 500 CONFORMING TO IS:1786-85 & AMENDMENTS.
6. LAPS SHALL BE STAGGERED AND LAP LENGTHS ARE AS FOLLOWS.

MIX	M25
Ld	48 Dia

7. NOT MORE THAN 50% OF COLUMN REINFORCEMENT SHALL BE LAPPED AT A PARTICULAR LOCATION.
8. CLEAR COVERS ARE AS FOLLOWS

FOOTING TO MAIN BAR	COLUMN TO MAIN BAR	BEAMS TO STIRRUPS	SLABS TO MAIN BAR
50mm	40mm	20mm	20mm

9. CURING SHOULD BE DONE ATLEAST FOR 21 DAYS.
10. THIS DRAWING SHOULD BE READ IN CONJUNCTION WITH RELEVANT ARCHITECTURAL DRAWINGS.
11. STRIPPING TIME OF FORMWORK SHALL CONFORM TO CLAUSE 11.3 OF IS:456-2000.
12. FOR TIES,LINKS IN COLUMNS Y8-150mm c/c REFER COLUMN SCHEDULE DWG.
13. FOR EXACT LOCATION OF WALLS REFER RELEVANT ARCHITECTURAL DRAWINGS FOR NECESSARY DETAILS.
14. ANY DISCREPANCY FROM THE DRAWING SHALL BE BROUGHT TO THE NOTICE OF CONSULTANTS.
15. THE STRUCTURE IS DESIGNED FOR GROUND FLOOR ONLY

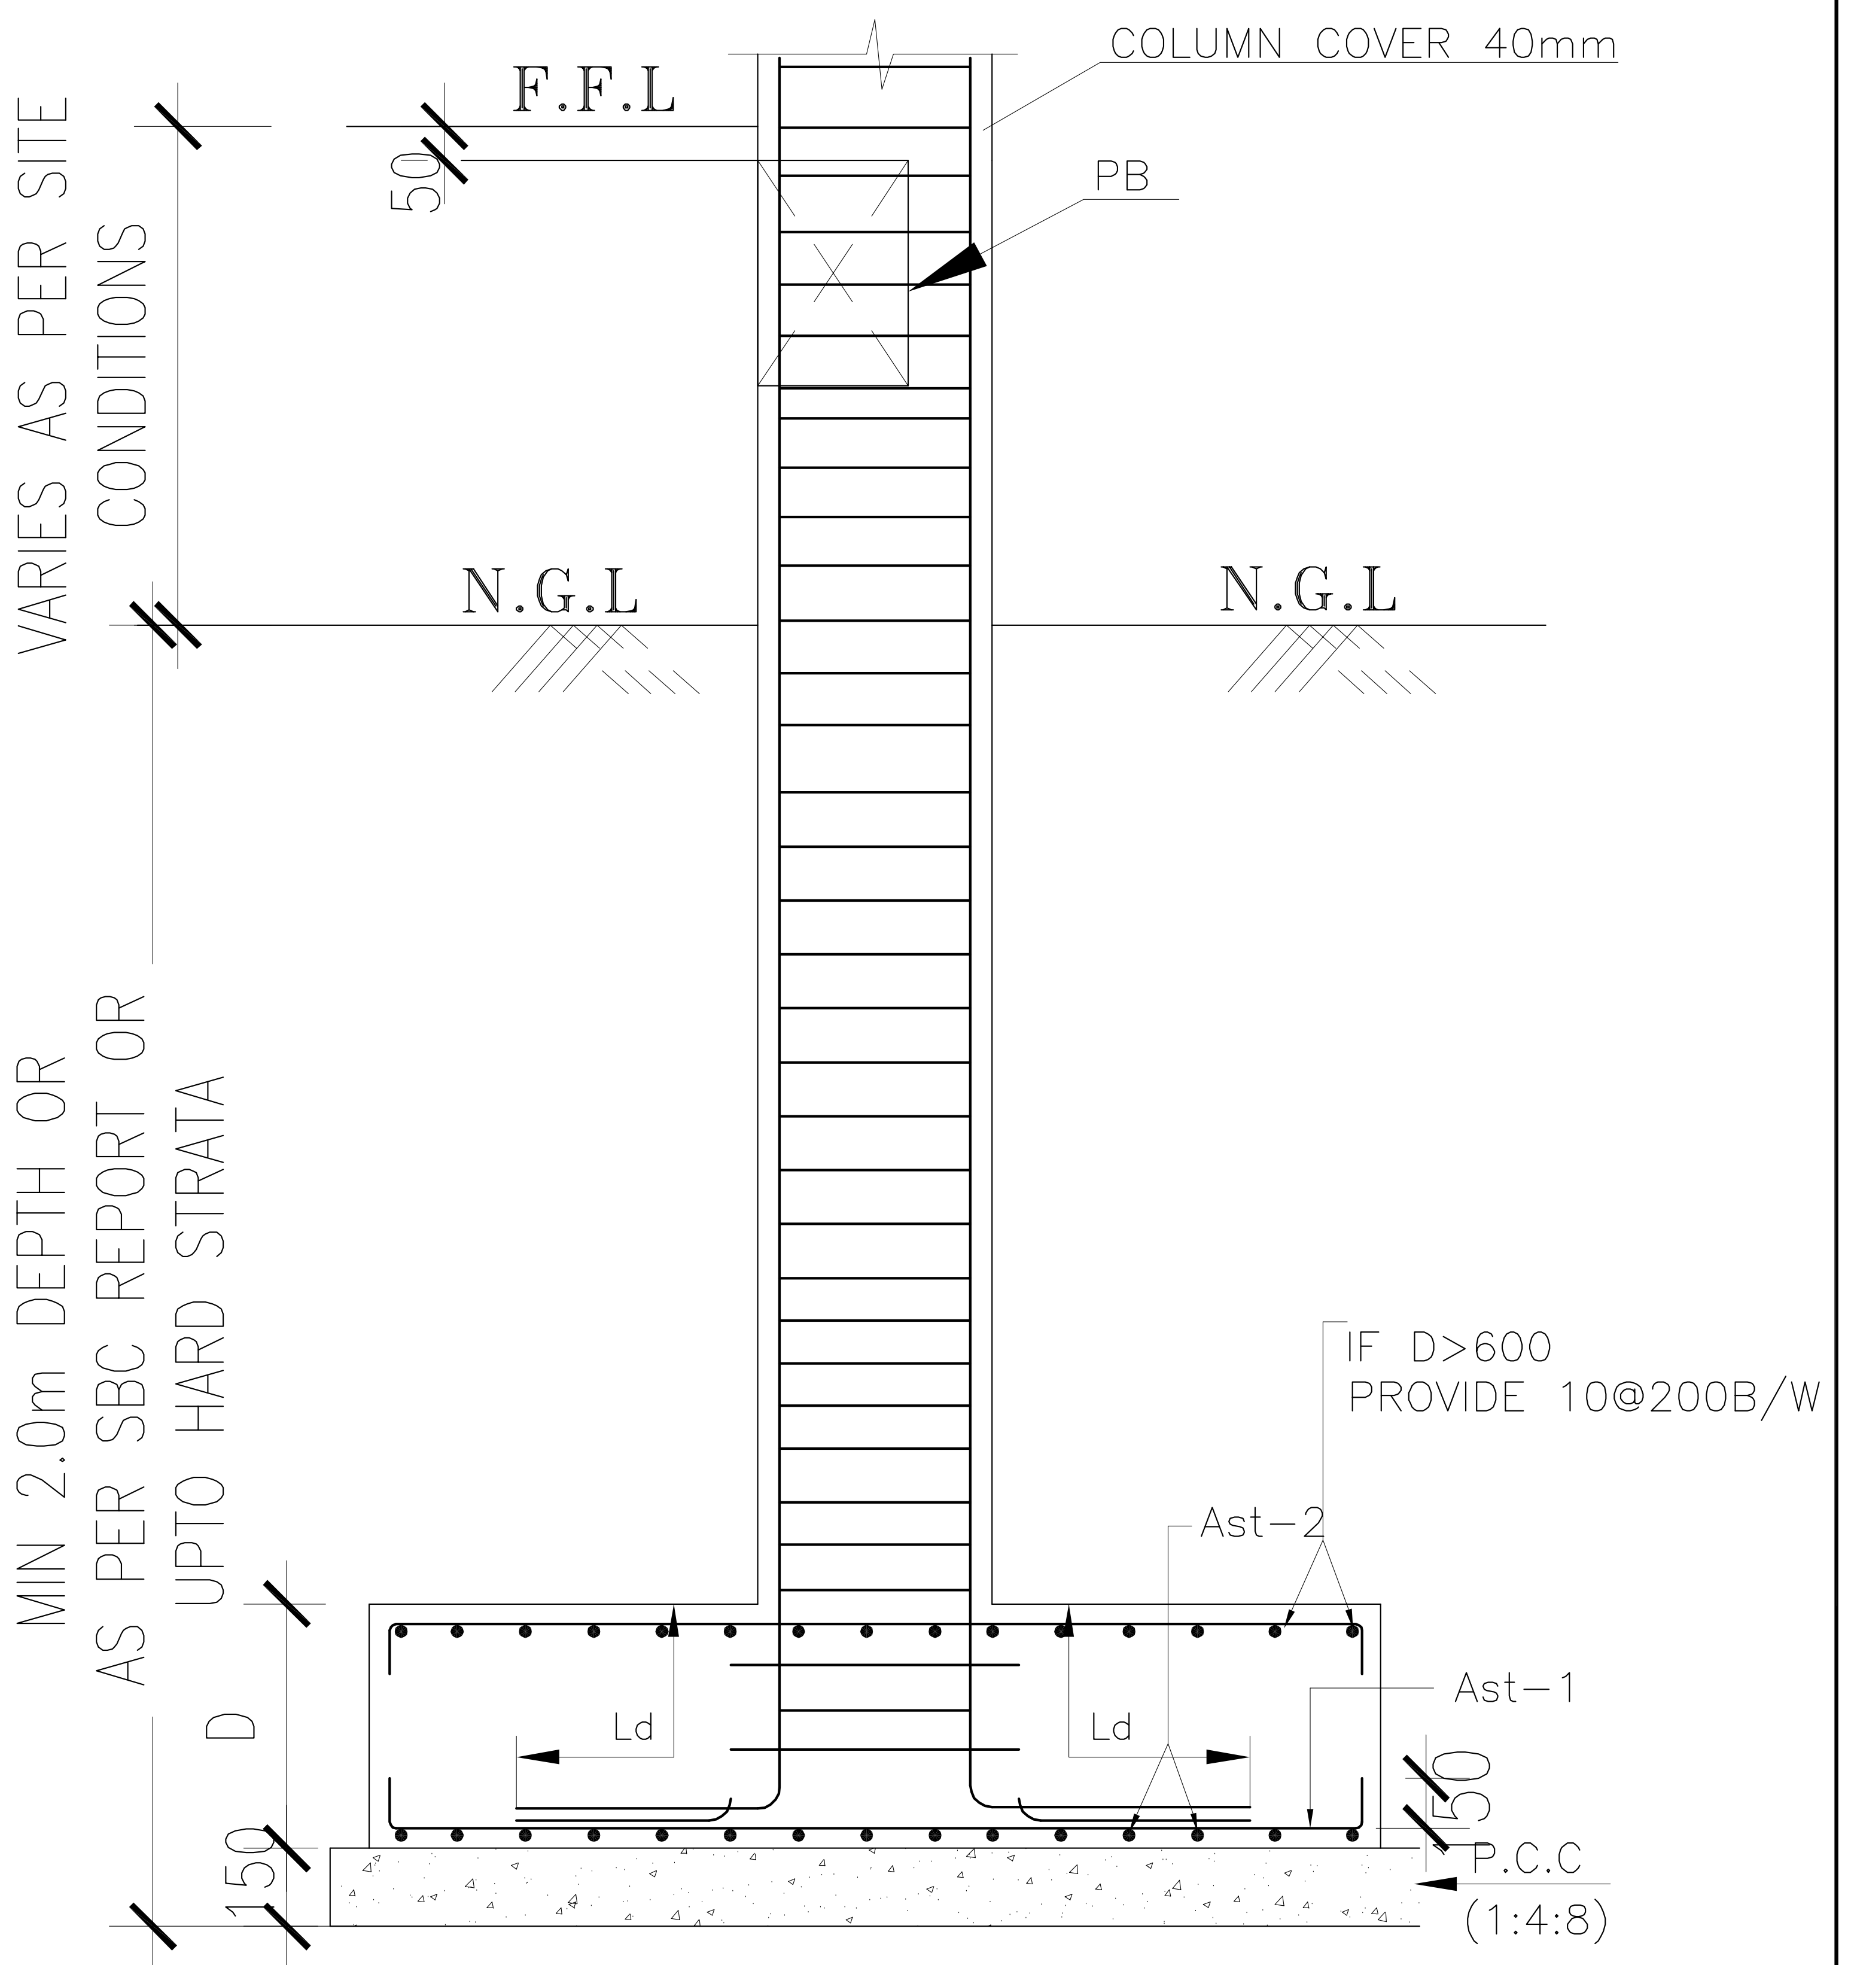
VARIES AS PER SITE CONDITIONS
MIN 2.0m DEPTH OR AS PER SBC REPORT OR UPTO HARD STRATA
F.F.L
50
COLUMN COVER 40mm
PB
N.G.L
N.G.L
IF D>600
PROVIDE 10@200B/W
Ast-2
Ast-1
Ld
Ld
D
150
50
P.C.C
(1:4:8)

SECTION X-X

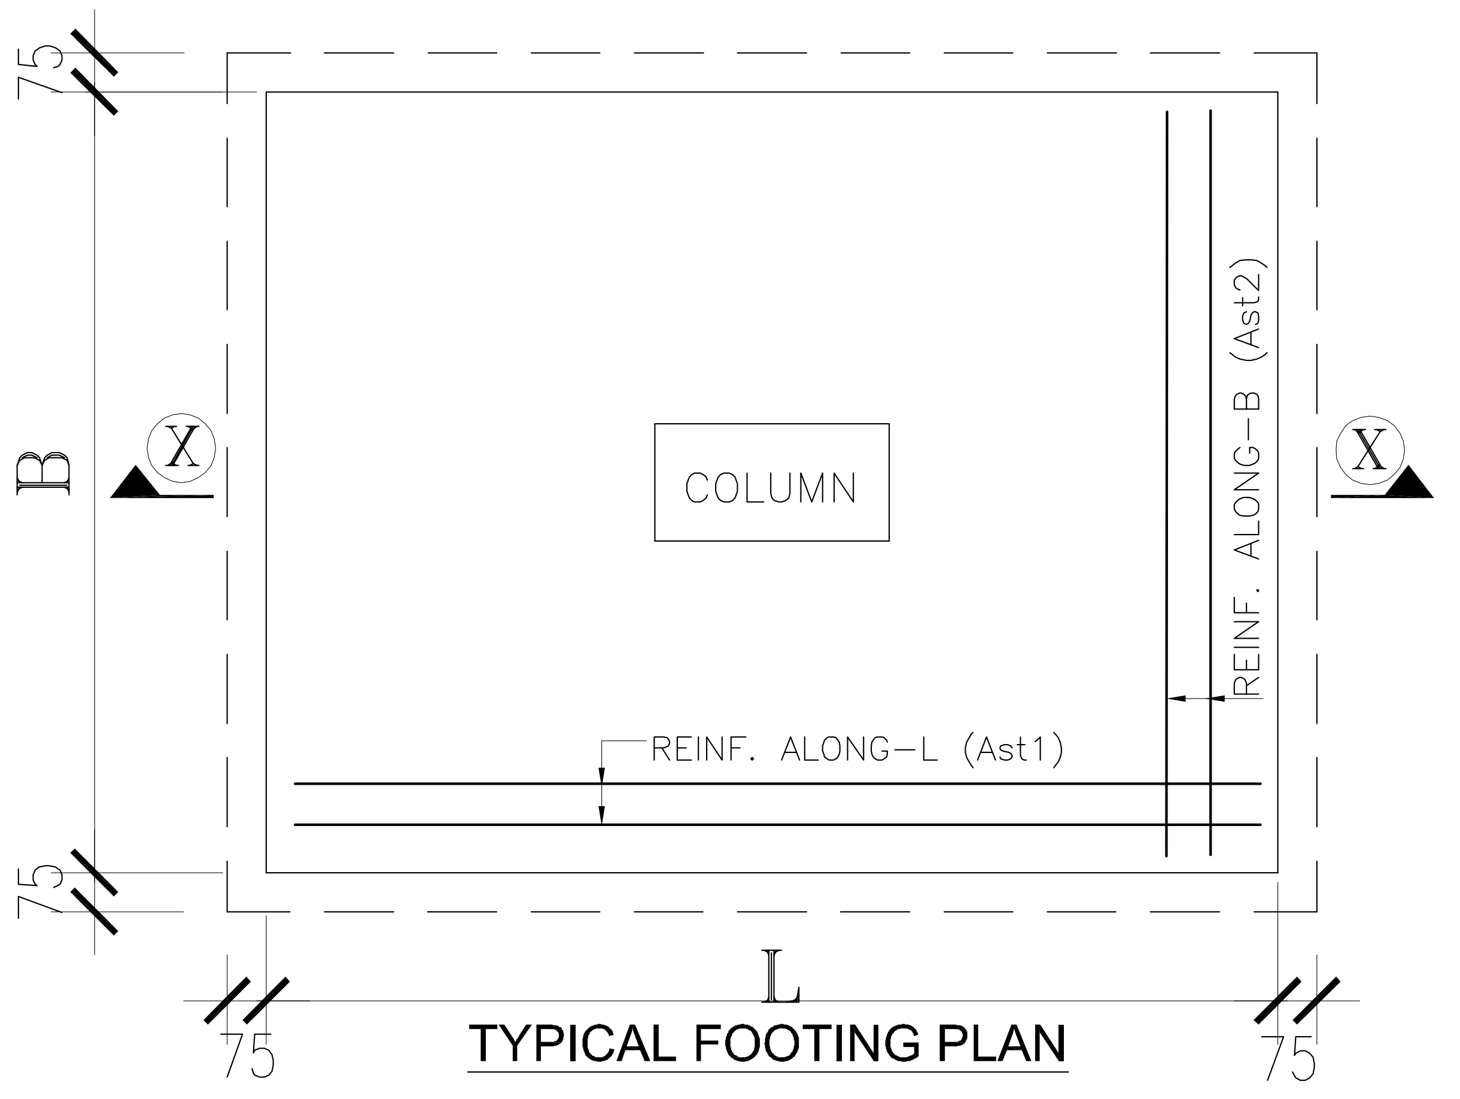
75
75
B
X
X
COLUMN
REINF. ALONG-B (Ast2)
REINF. ALONG-L (Ast1)
L
75
75

TYPICAL FOOTING PLAN

- THIS DRAWING SHALL BE READ IN CONJUNCTION WITH ALL RELEVANT ARCHITECTURAL, STRUCTURAL AND SERVICES DRAWINGS. ANY DISCREPANCY NOTICED SHALL BE BROUGHT TO THE ATTENTION OF THE CONSULTANTS AND RESOLVED AS SOON AS POSSIBLE BUT ALWAYS PRIOR TO

ARCHITECTURAL CONSULTANT:

also. design
a little story of design

STRUCTURAL& MEP CONSULTANTS

JASHRITHA ASSOCIATES
AND MEP PLANNERS
4th FLOOR(4B), HIG 129, KPHB COLONY, KUKATPALLY,
(SUB BRANCH:PR NAGAR ERRAGADDA.)
HYDERABAD 500072, TELANGANA, INDIA
Phone : 9700441106.
E-mail : jashreyansh.consultatns@gmail.com
& jashritha.mep@gmail.com

PROJECT:

ANKURA HOMES_THE WOODS
AT KEESARAGUTTA

DRAWING TITLE:

1625_WEST VILLA
COLUMN & FOOTING
SCHEDULE

DESIGN ENGG : AJAY	APPROVED :
SCALE : NTS	DRAWN : PK
DATE : 07-10-2026	CHECKED : PRADEEP
DRAWING NO: SD-02	REV.NO: 01

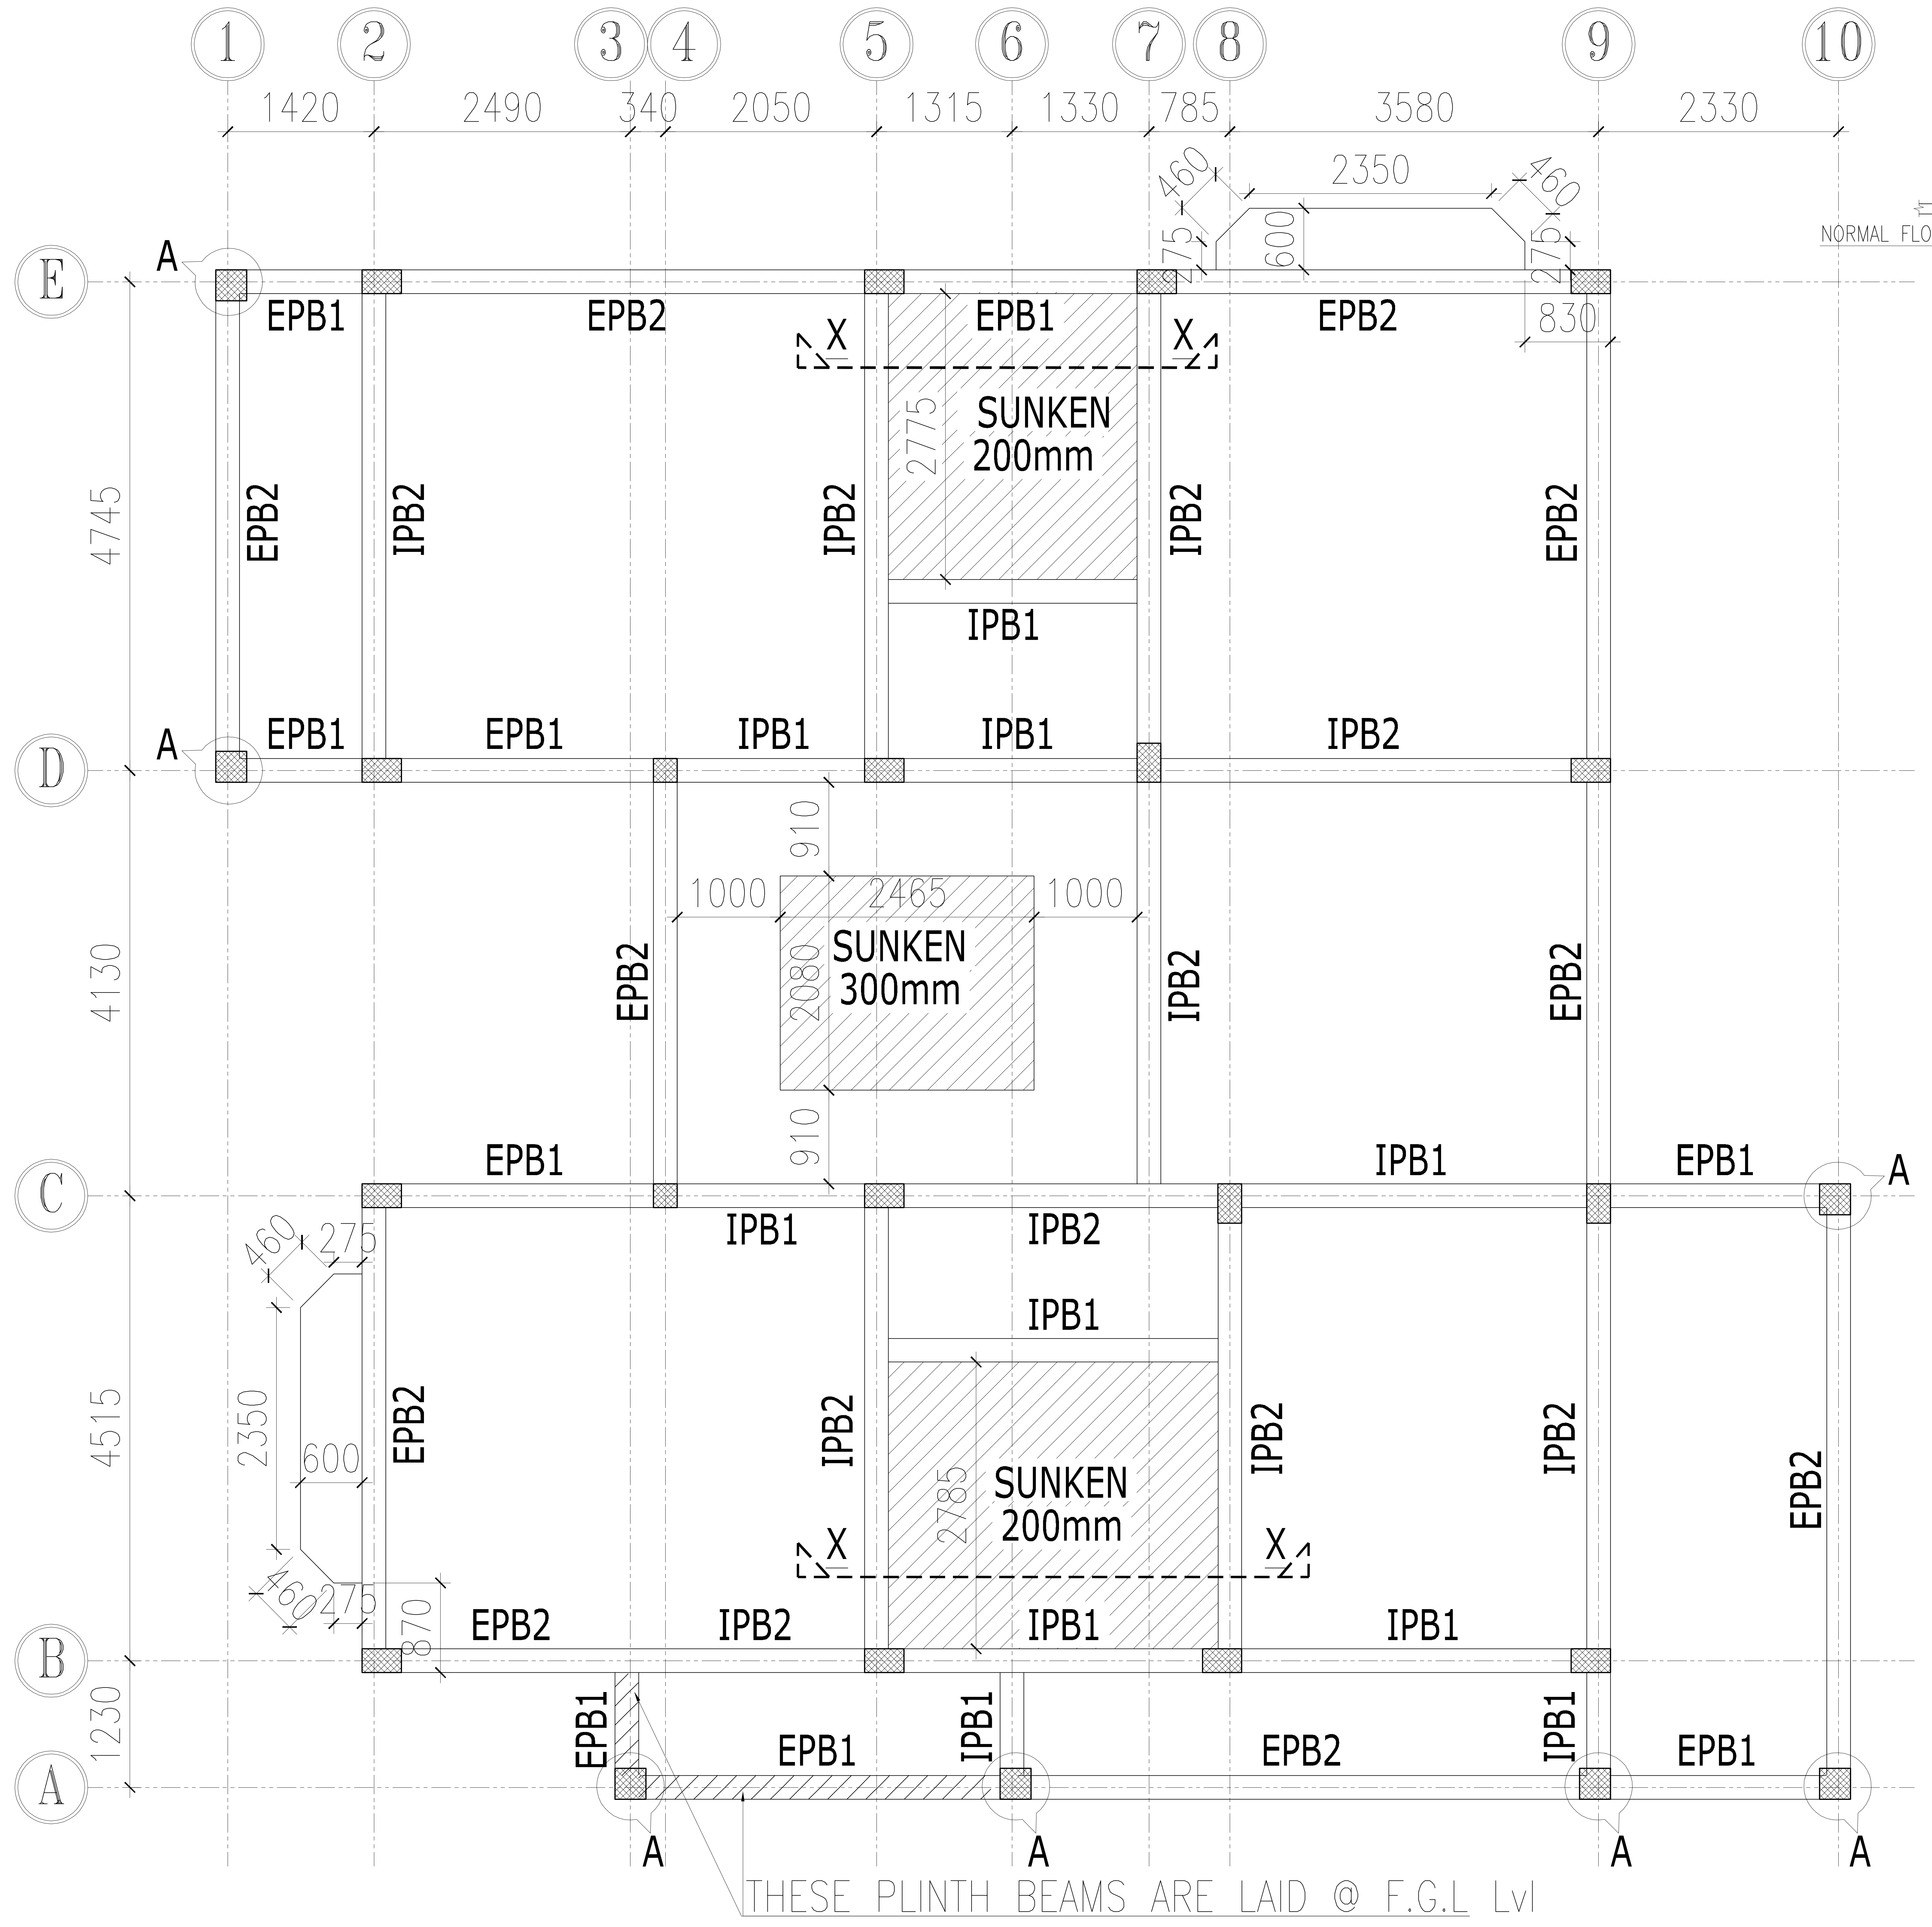
1
2
3
4
5
6
7
8
9
10
1420
2490
340
2050
1315
1330
785
3580
2330
E
D
C
B
A
4745
4130
4515
1230
A
A
A
A
A
A
A
EPB1
EPB2
EPB1
EPB2
X
X
SUNKEN
200mm
2775
EPB2
IPB2
IPB2
IPB2
EPB2
IPB1
460
2350
460
275
600
275
830
EPB1
EPB1
IPB1
IPB1
IPB2
910
1000
2465
1000
SUNKEN
300mm
2080
910
EPB2
IPB2
EPB2
EPB1
IPB1
EPB1
IPB1
IPB2
IPB1
460
275
2350
600
460
275
870
EPB2
IPB2
IPB2
SUNKEN
200mm
2785
IPB2
IPB2
EPB2
X
X
EPB2
IPB2
IPB1
IPB1
EPB1
EPB1
IPB1
EPB2
IPB1
EPB1
THESE PLINTH BEAMS ARE LAID @ F.G.L Lvl

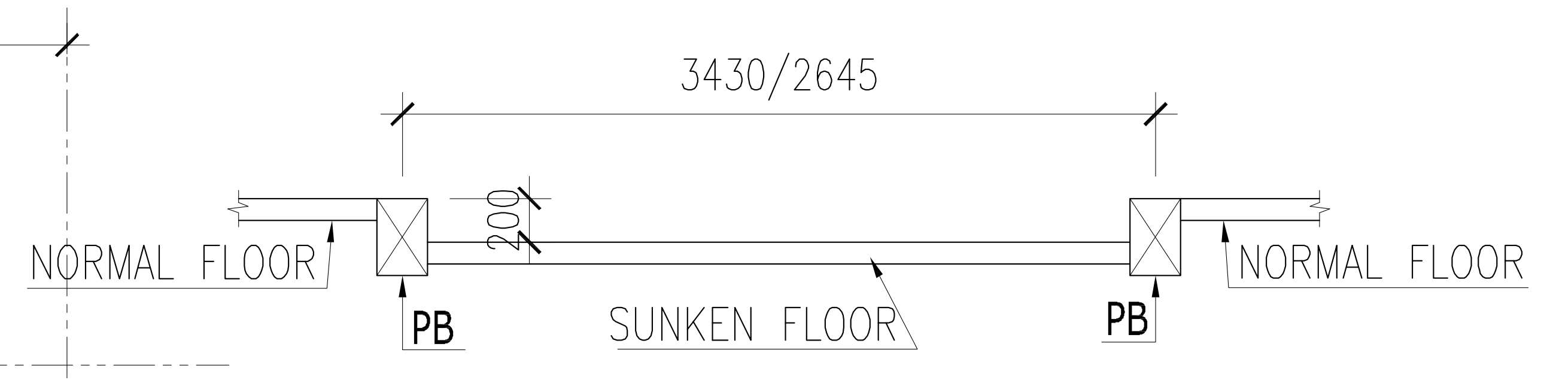
3430/2645
200
NORMAL FLOOR
PB
SUNKEN FLOOR
PB
NORMAL FLOOR

SECTION X-X

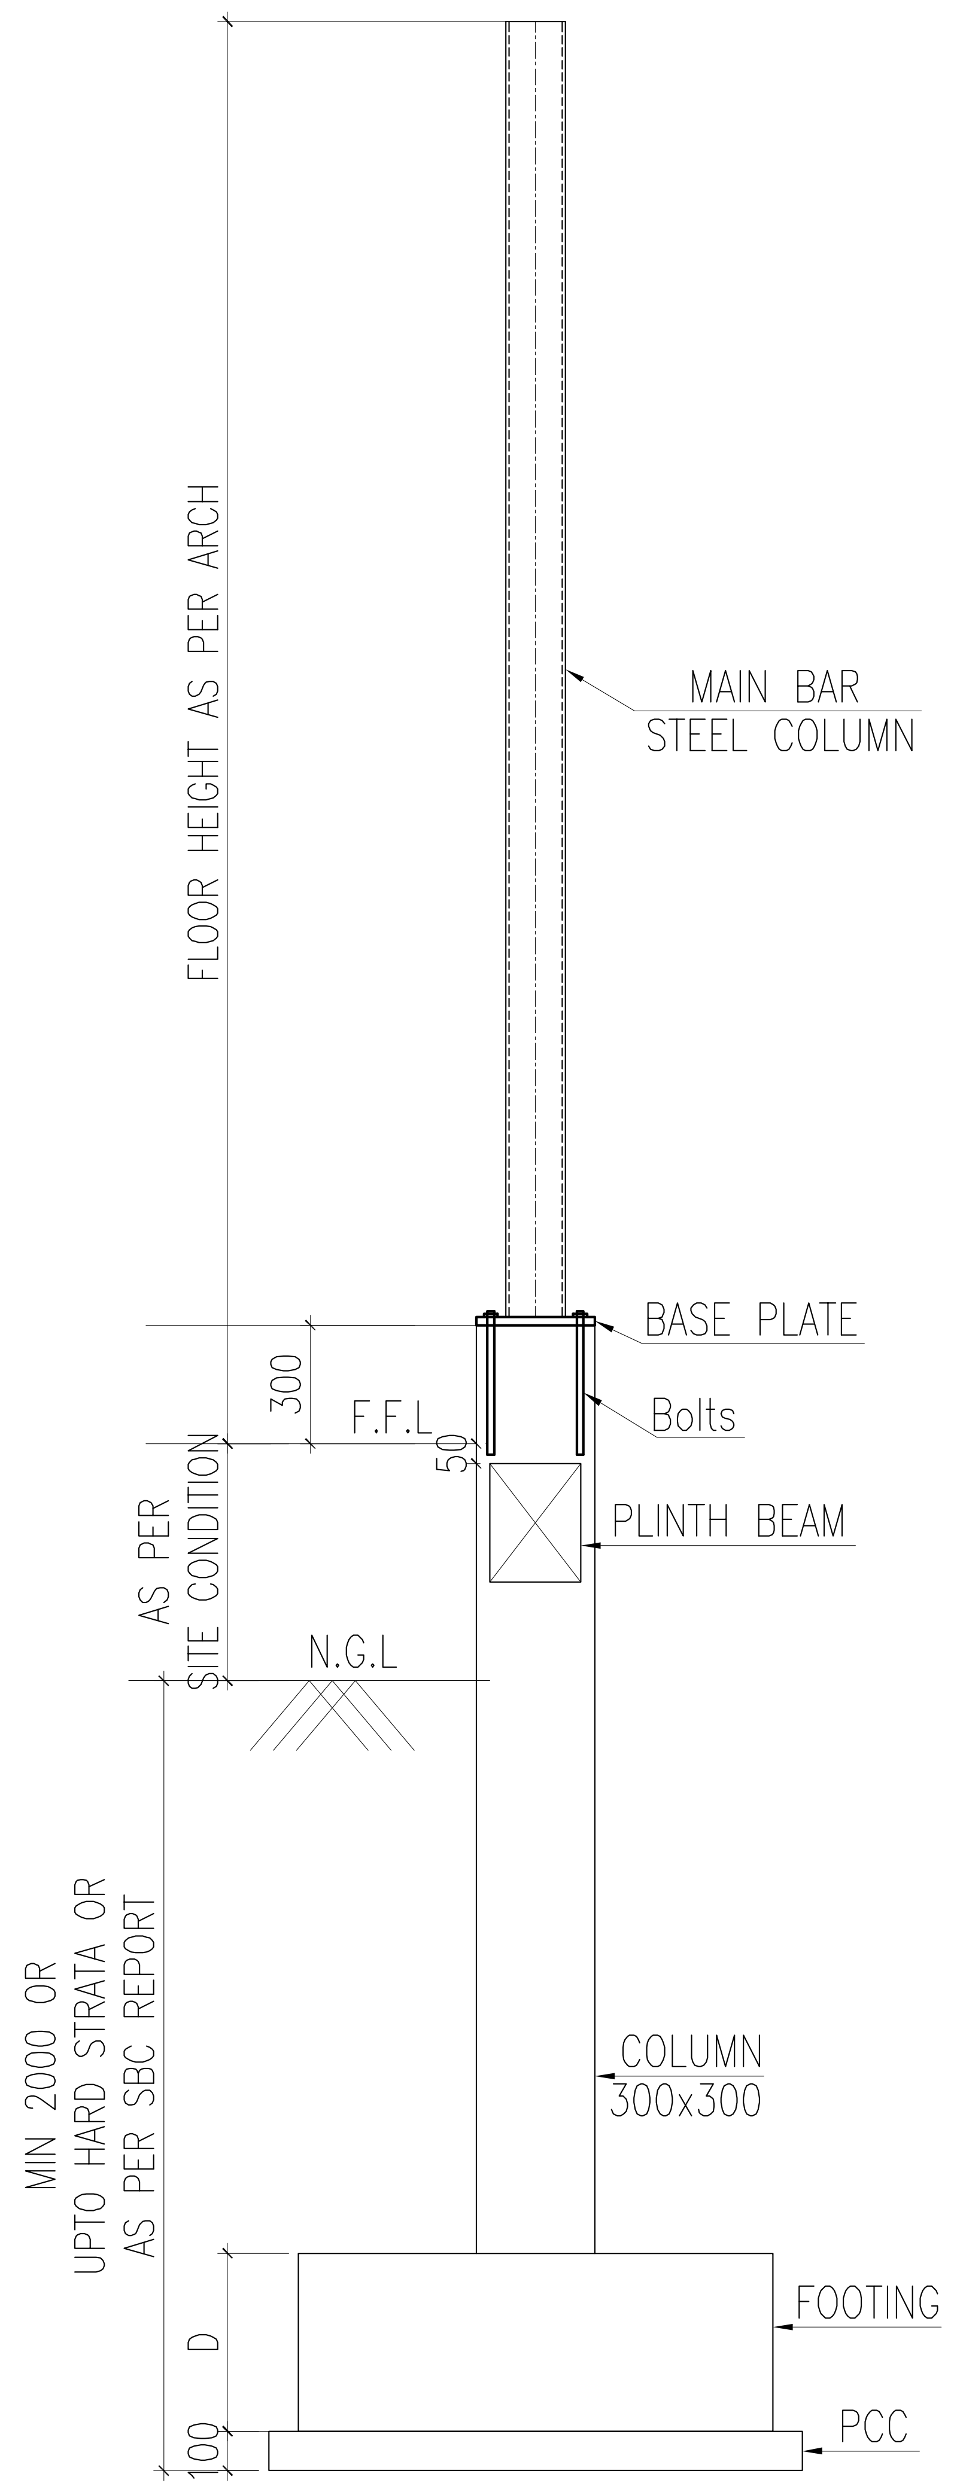
FLOOR HEIGHT AS PER ARCH
MAIN BAR
STEEL COLUMN
BASE PLATE
Bolts
PLINTH BEAM
300
F.F.L
50
AS PER
SITE CONDITION
N.G.L
MIN 2000 OR
UPTO HARD STRATA OR
AS PER SBC REPORT
COLUMN
300x300
FOOTING
PCC
D
100

DETAIL-A

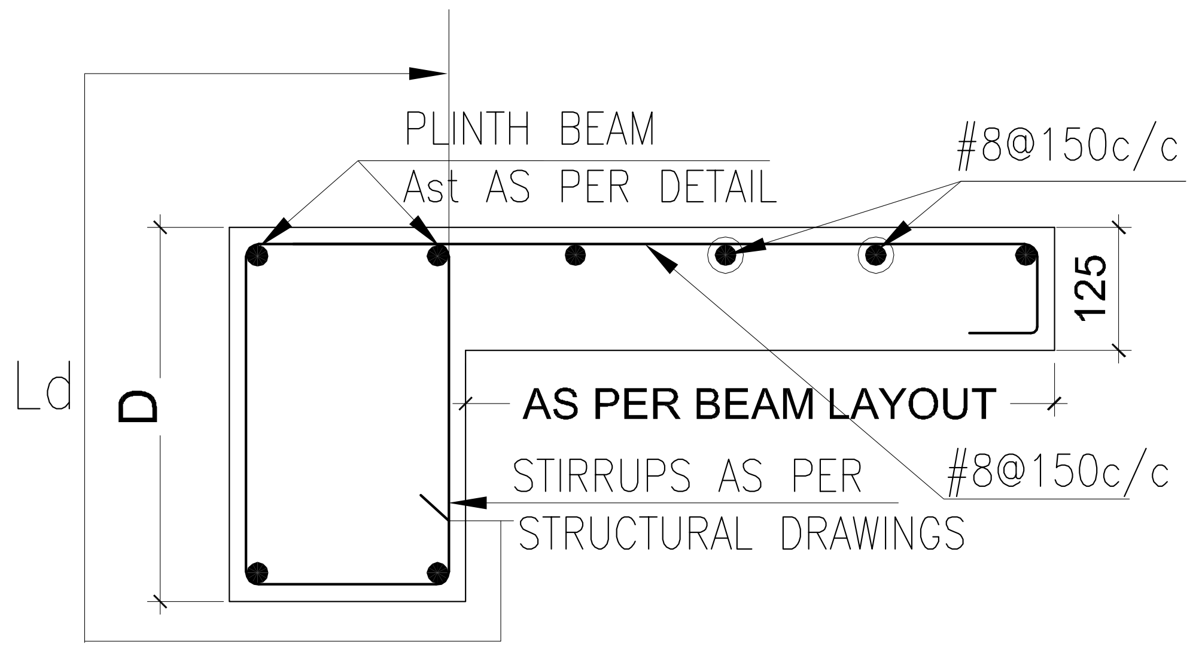
PLINTH BEAM
Ast AS PER DETAIL
#8@150c/c
125
Ld
D
AS PER BEAM LAYOUT
STIRRUPS AS PER
STRUCTURAL DRAWINGS
#8@150c/c

TYPICAL
SLAB PROJECTION DETAILS

- THIS DRAWING SHALL BE READ IN CONJUNCTION WITH ALL RELEVANT ARCHITECTURAL, STRUCTURAL AND SERVICES DRAWINGS. ANY DISCREPANCY NOTICED SHALL BE BROUGHT TO THE ATTENTION OF THE CONSULTANTS AND RESOLVED AS SOON AS POSSIBLE BUT ALWAYS PRIOR TO

DIRECTION:

N

ARCHITECTURAL CONSULTANT:

also.
design
a little story of design

STRUCTURAL& MEP CONSULTANTS

JASHRITHA ASSOCIATES
AND MEP PLANNERS
4th FLOOR(4B), HIG 129, KPHB COLONY, KUKATPALLY,
(SUB BRANCH:PR NAGAR ERRAGADDA.)
HYDERABAD 500072, TELANGANA, INDIA
Phone : 9700441106.
E-mail : jashreyansh.consultatns@gmail.com
& jashritha.mep@gmail.com

PROJECT:

ANKURA HOMES_THE WOODS
AT KEESARAGUTTA

DRAWING TITLE:

1625_WEST VILLA
PLINTH BEAM LAYOUT

DESIGN ENGG : AJAY	APPROVED :
SCALE : NTS	DRAWN : PK
DATE : 07-10-2026	CHECKED : PRADEEP
DRAWING NO: SD-03	REV.NO: 01

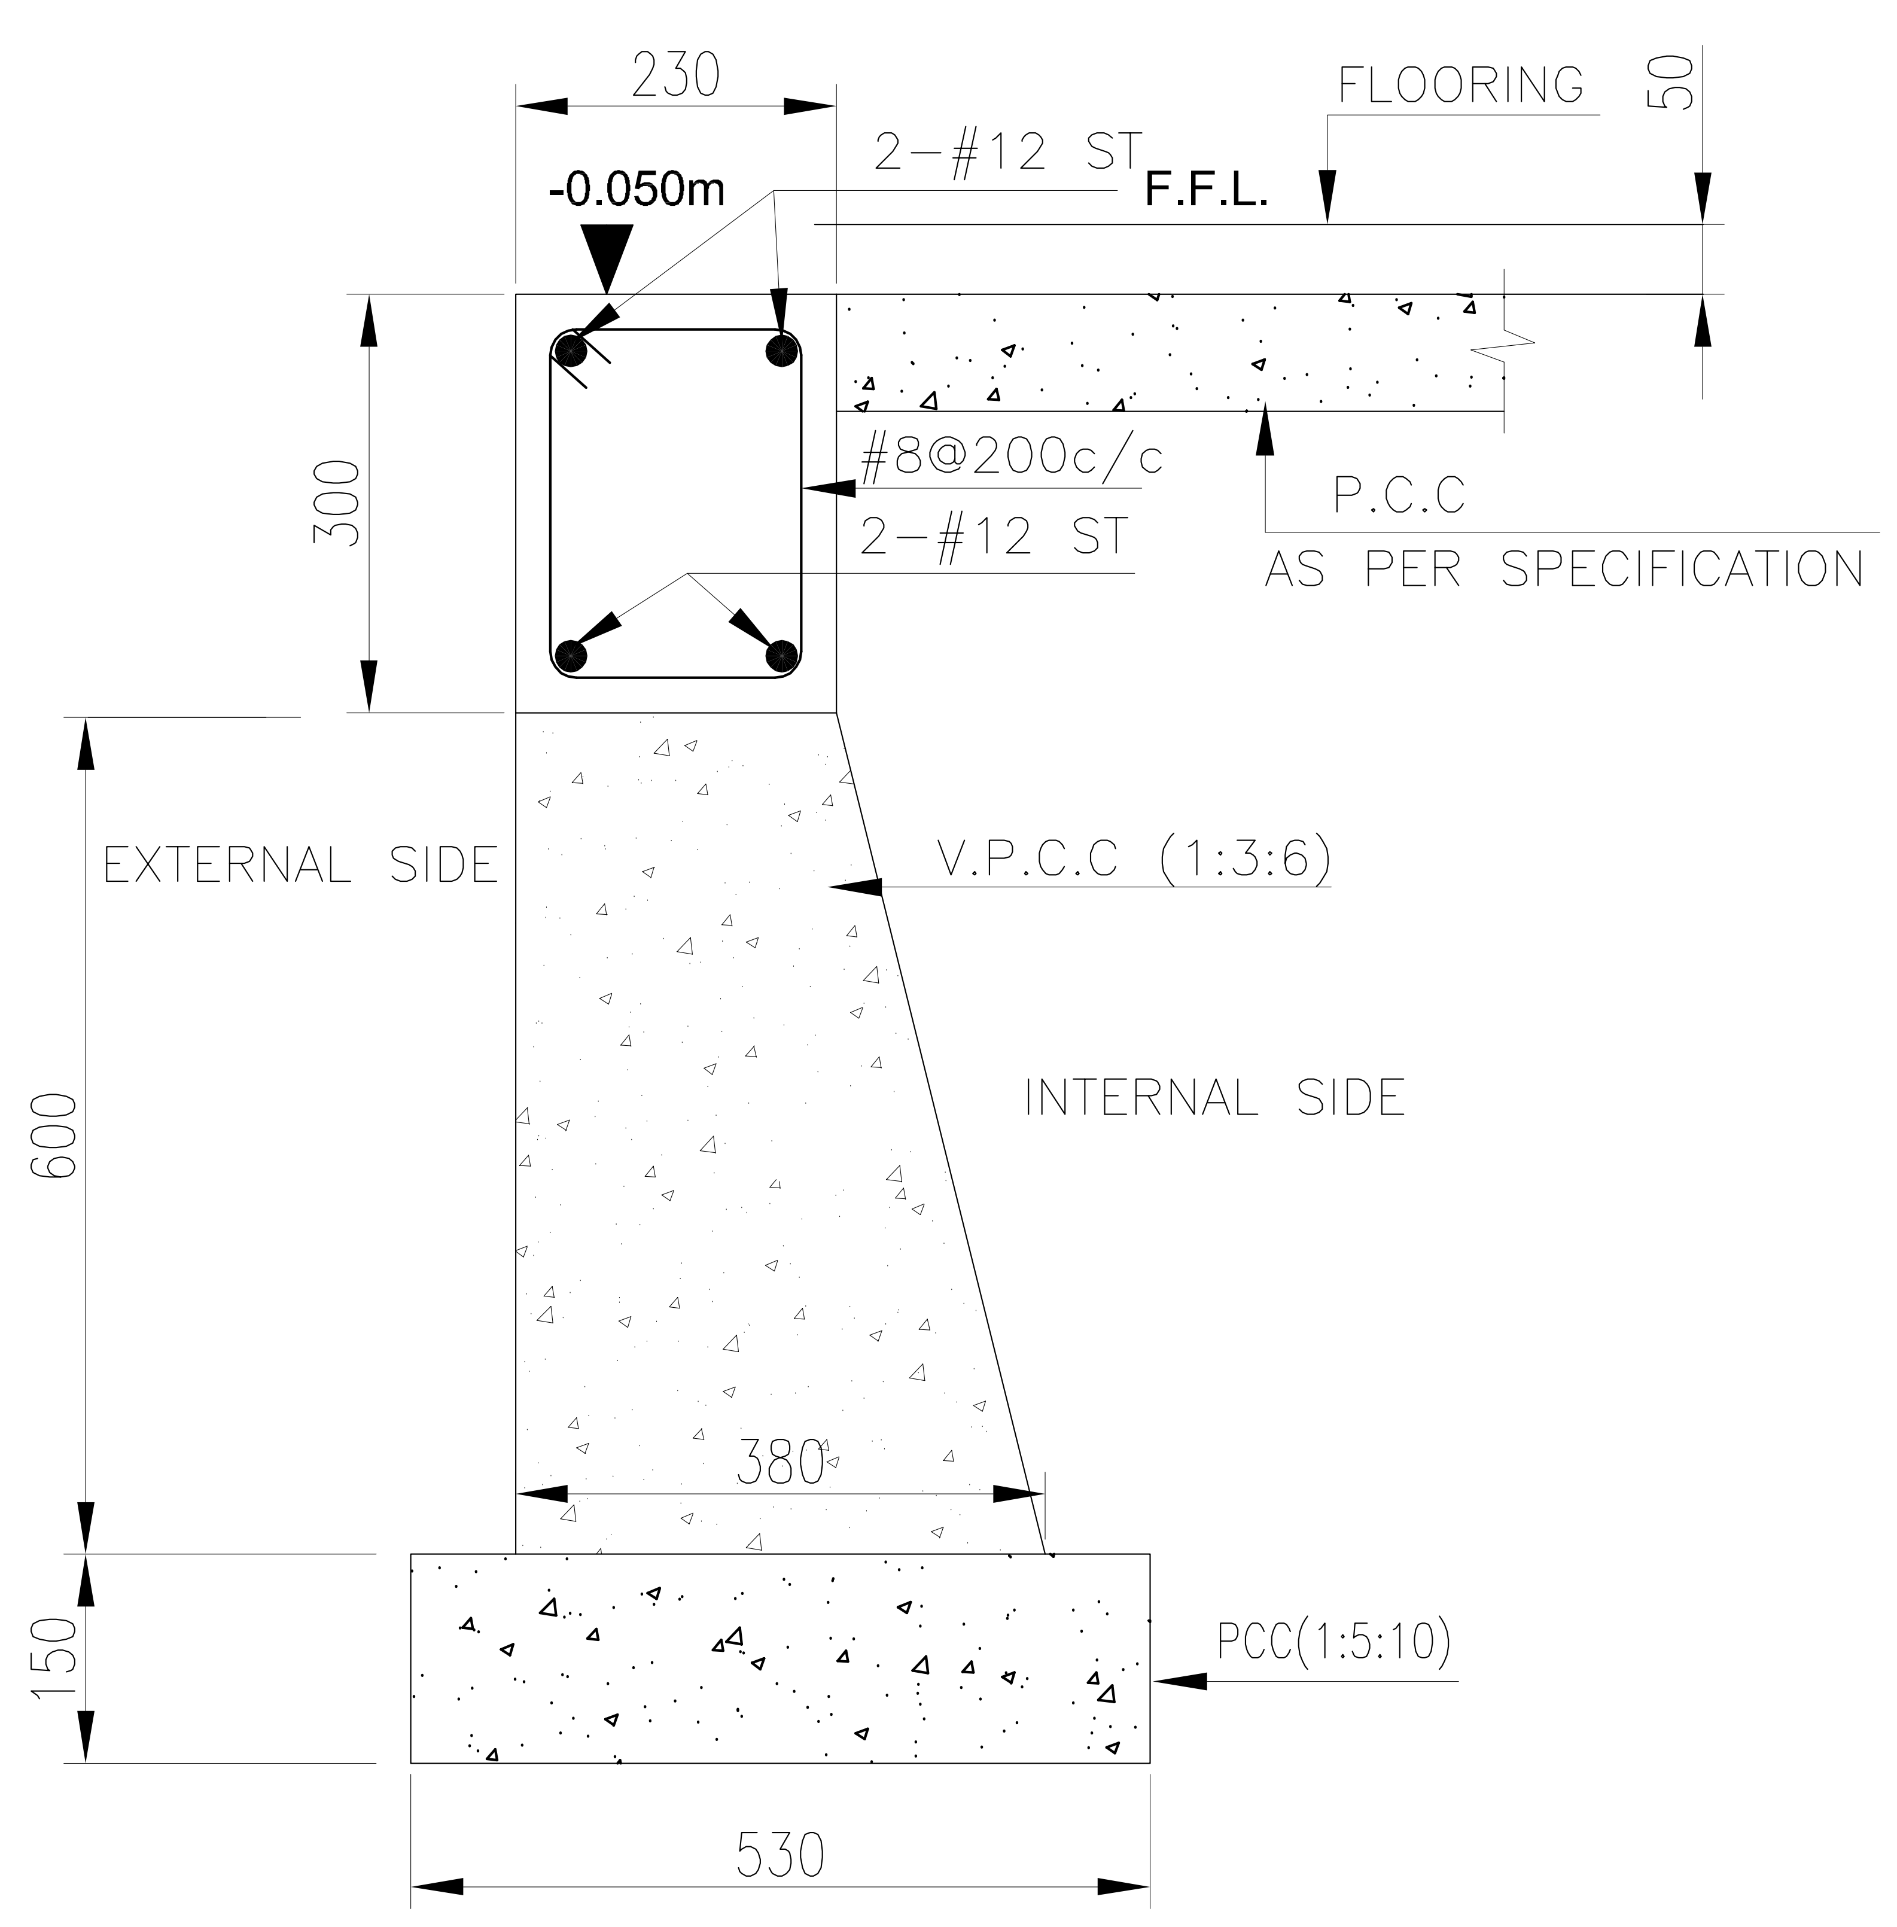
230
-0.050m
2-#12 ST
F.F.L.
FLOORING
50
300
#8@200c/c
2-#12 ST
P.C.C
AS PER SPECIFICATION
EXTERNAL SIDE
V.P.C.C (1:3:6)
INTERNAL SIDE
600
380
150
PCC(1:5:10)
530

EPB1

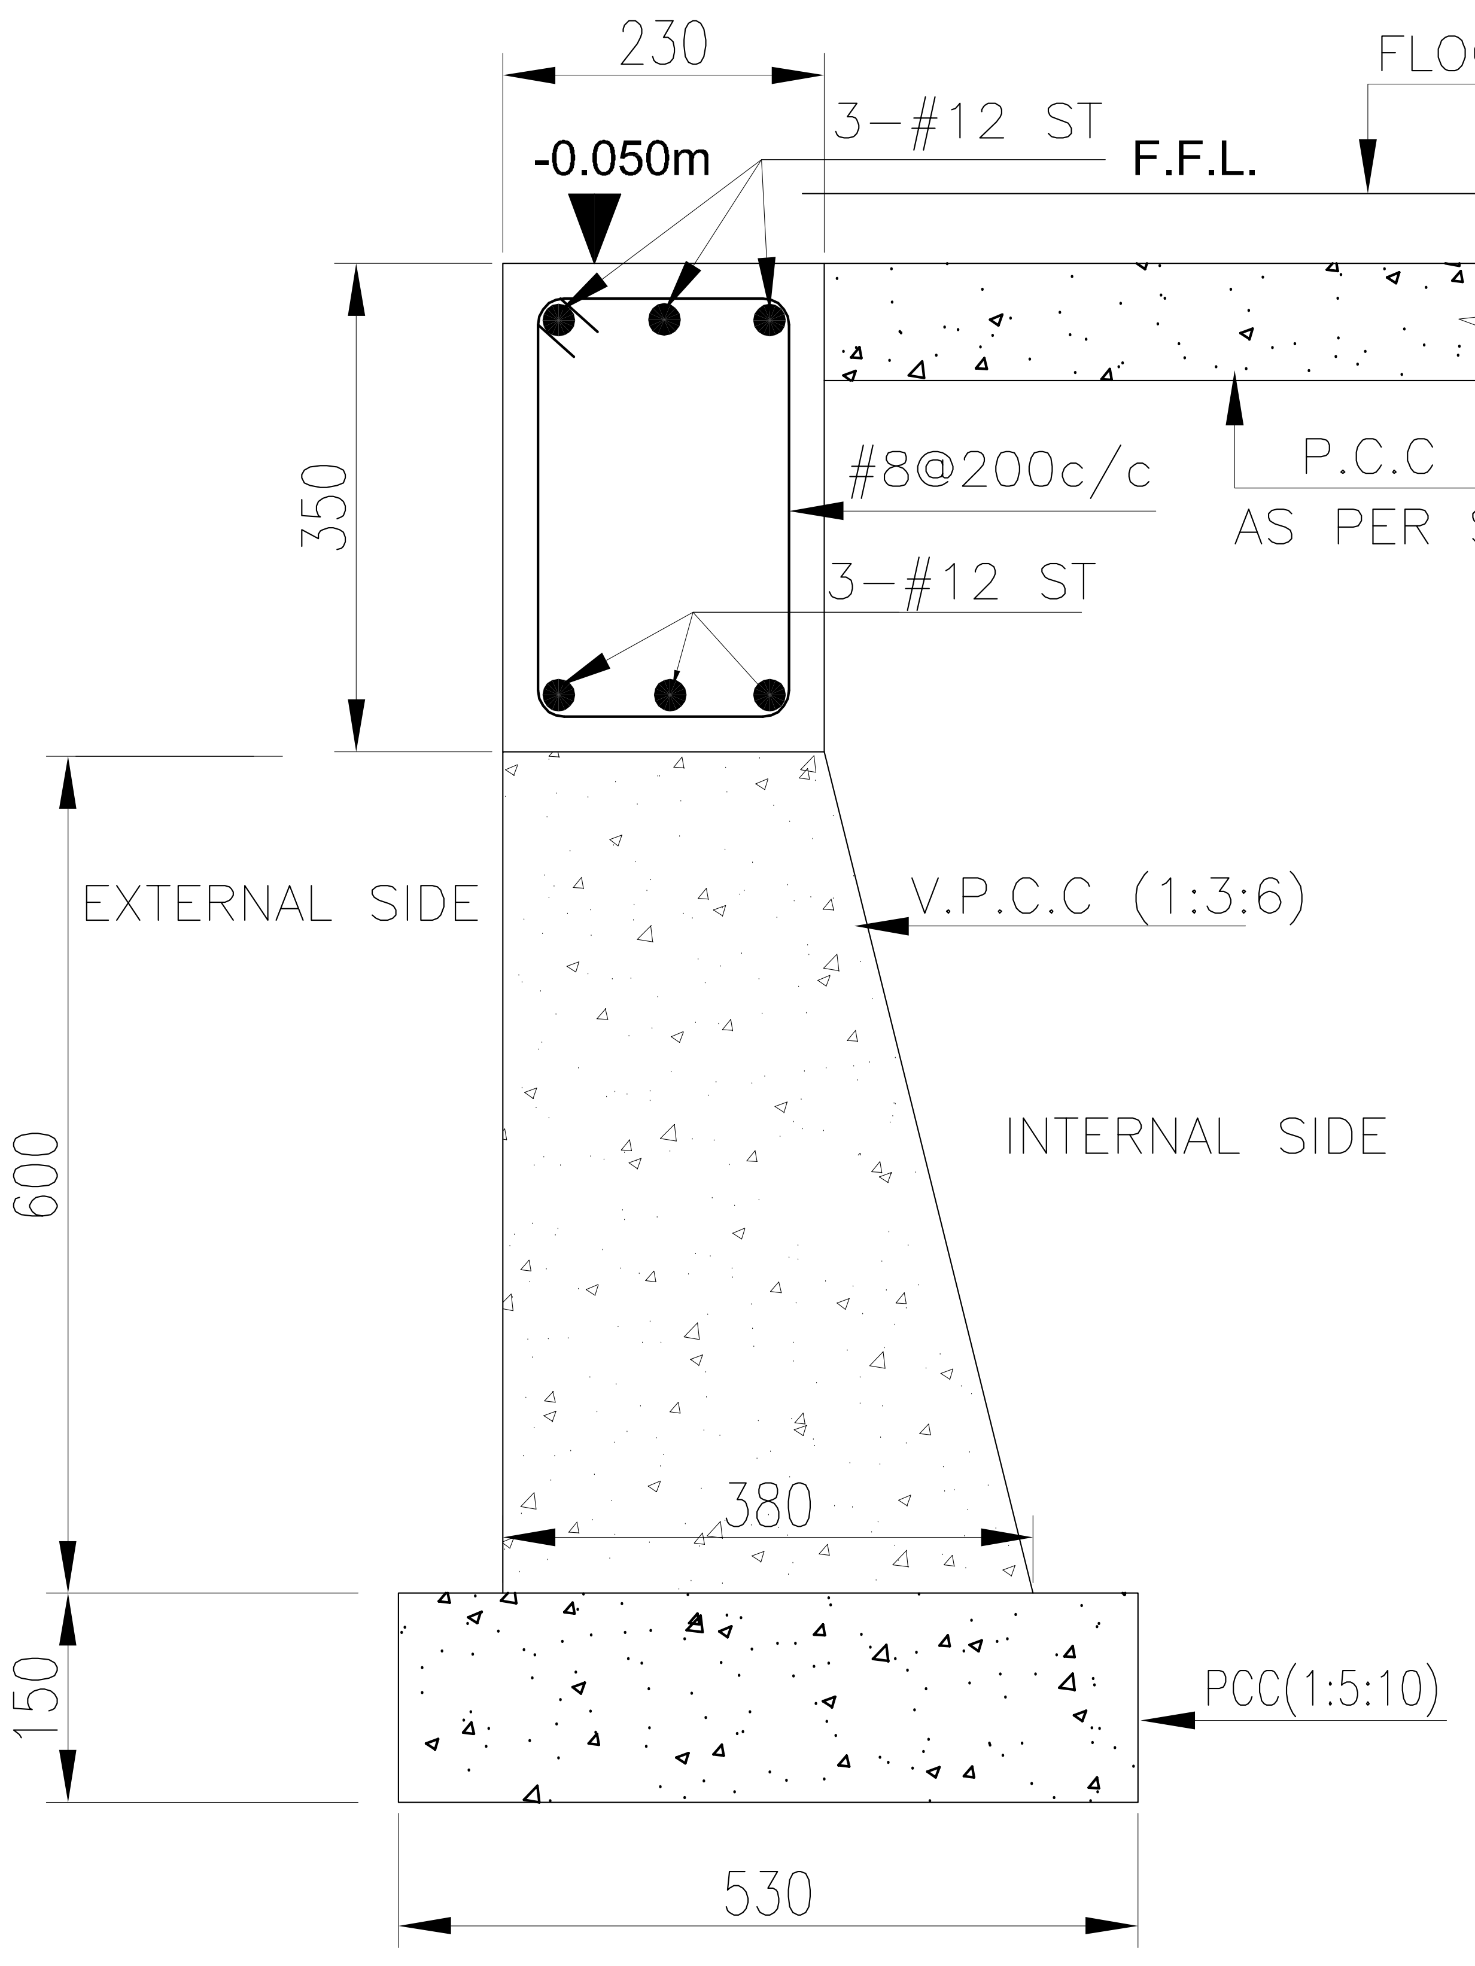
230
-0.050m
3-#12 ST
F.F.L.
FLOORING
50
350
#8@200c/c
3-#12 ST
P.C.C
AS PER SPECIFICATION
EXTERNAL SIDE
V.P.C.C (1:3:6)
INTERNAL SIDE
600
380
150
PCC(1:5:10)
530

EPB2

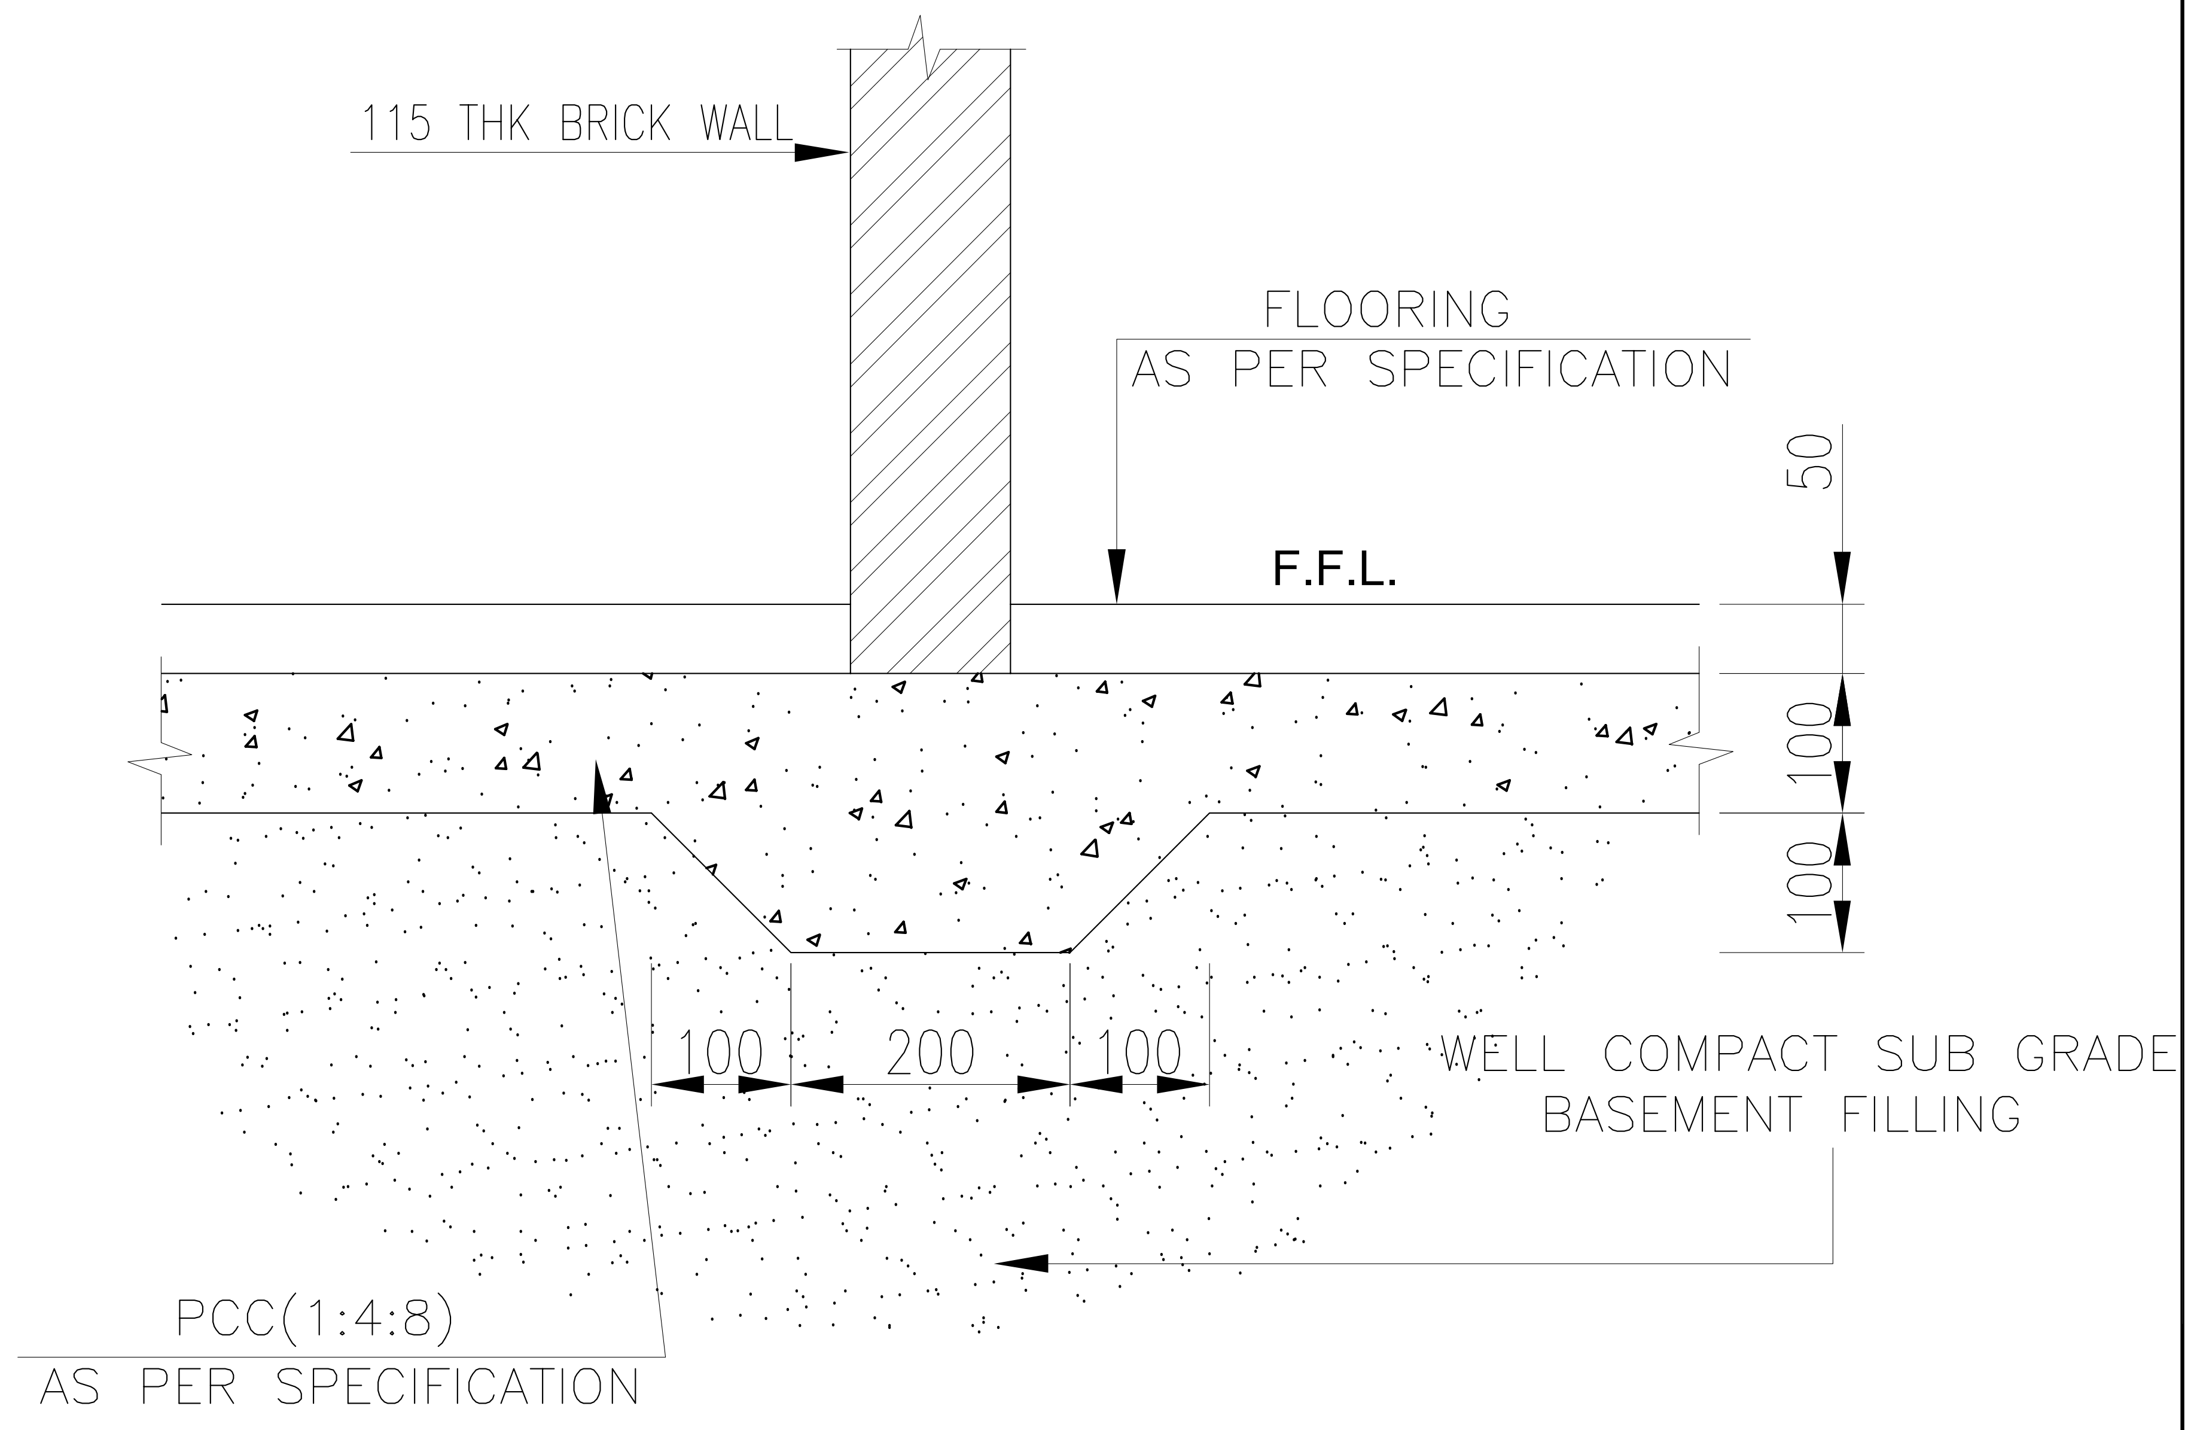
115 THK BRICK WALL
FLOORING
AS PER SPECIFICATION
50
F.F.L.
100
100
100
200
100
WELL COMPACT SUB GRADE
BASEMENT FILLING
PCC(1:4:8)
AS PER SPECIFICATION

FOUNDATION DETAIL UNDER 115mm THICK BRICK WALL

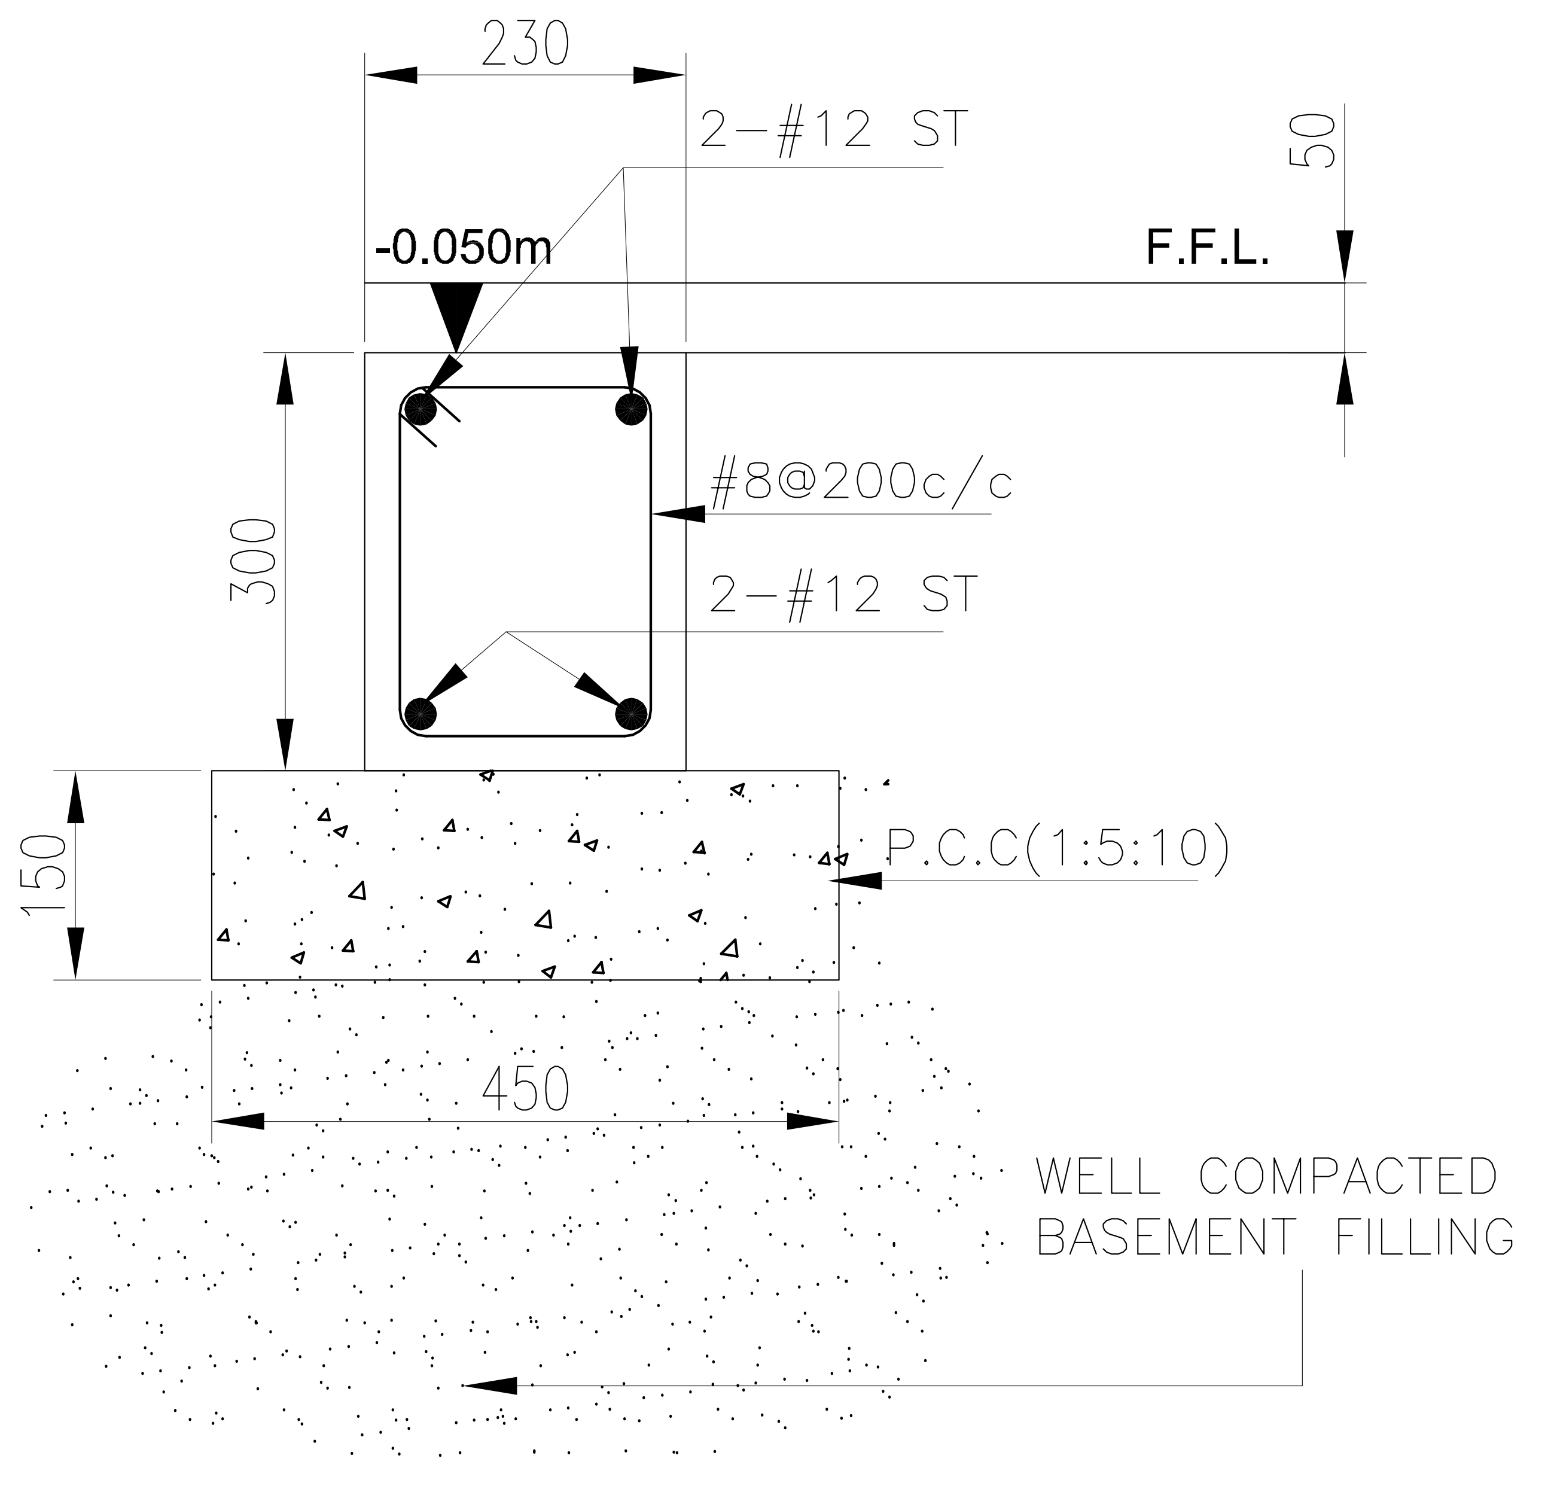
230
2-#12 ST
50
-0.050m
F.F.L.
300
#8@200c/c
2-#12 ST
150
P.C.C(1:5:10)
450
WELL COMPACTED
BASEMENT FILLING

IPB1

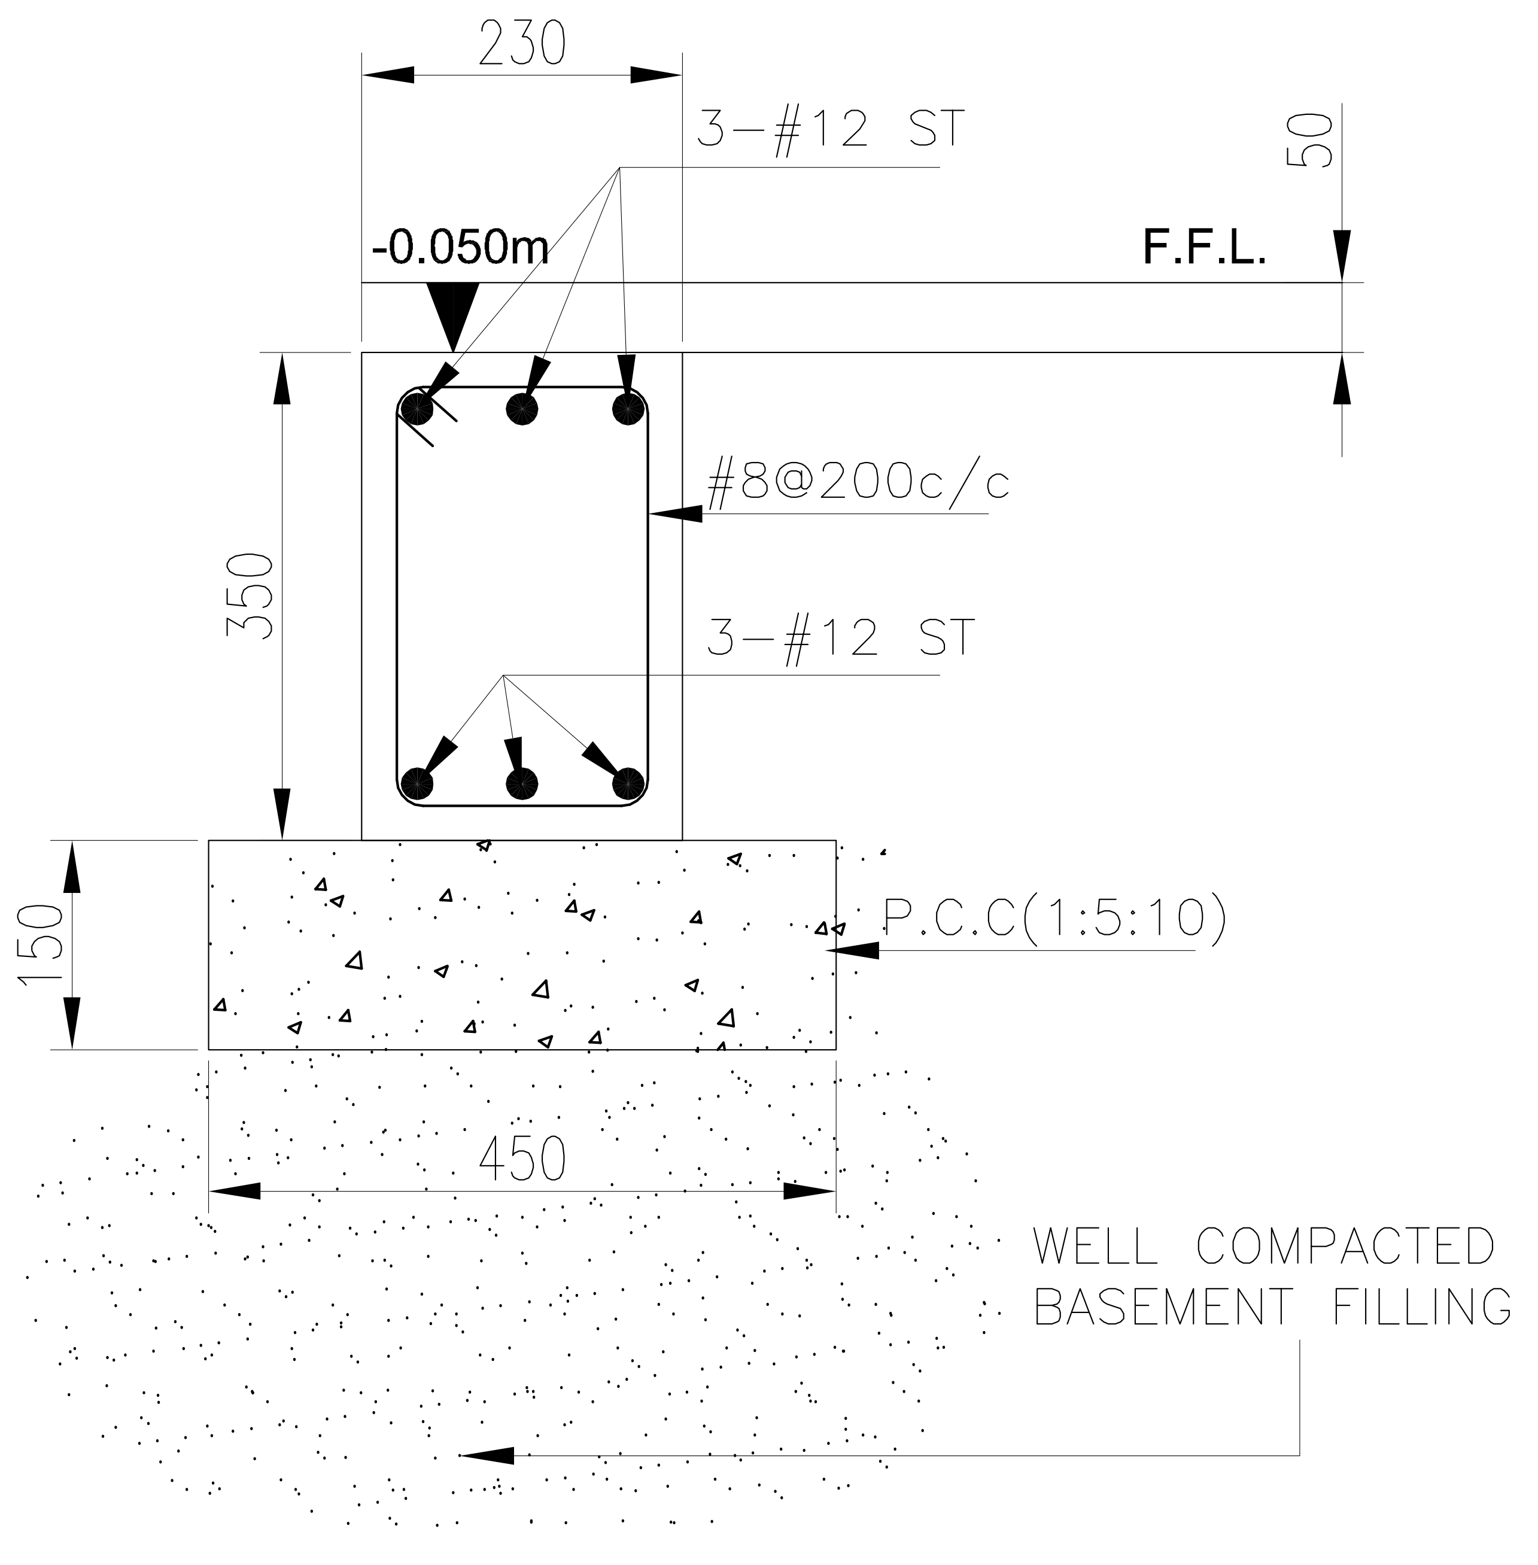
230
3-#12 ST
50
-0.050m
F.F.L.
350
#8@200c/c
3-#12 ST
150
P.C.C(1:5:10)
450
WELL COMPACTED
BASEMENT FILLING

IPB2

- THIS DRAWING SHALL BE READ IN CONJUNCTION WITH ALL RELEVANT ARCHITECTURAL, STRUCTURAL AND SERVICES DRAWINGS. ANY DISCREPANCY NOTICED SHALL BE BROUGHT TO THE ATTENTION OF THE CONSULTANTS AND RESOLVED AS SOON AS POSSIBLE BUT ALWAYS PRIOR TO

ARCHITECTURAL CONSULTANT:

also. design
a little story of design

STRUCTURAL& MEP CONSULTANTS

JASHRITHA ASSOCIATES
AND MEP PLANNERS
4th FLOOR(4B), HIG 129, KPHB COLONY, KUKATPALLY,
(SUB BRANCH:PR NAGAR ERRAGADDA.)
HYDERABAD 500072, TELANGANA, INDIA
Phone : 9700441106.
E-mail : jashreyansh.consultatns@gmail.com
& jashritha.mep@gmail.com

PROJECT:

ANKURA HOMES_THE WOODS
AT KEESARAGUTTA

DRAWING TITLE:

1625_WEST VILLA
PLINTH BEAM DETAILS

DESIGN ENGG : AJAY	APPROVED :
SCALE : NTS	DRAWN : PK
DATE : 25-09-2026	CHECKED : PRADEEP

DRAWING NO: SD-04
REV.NO:

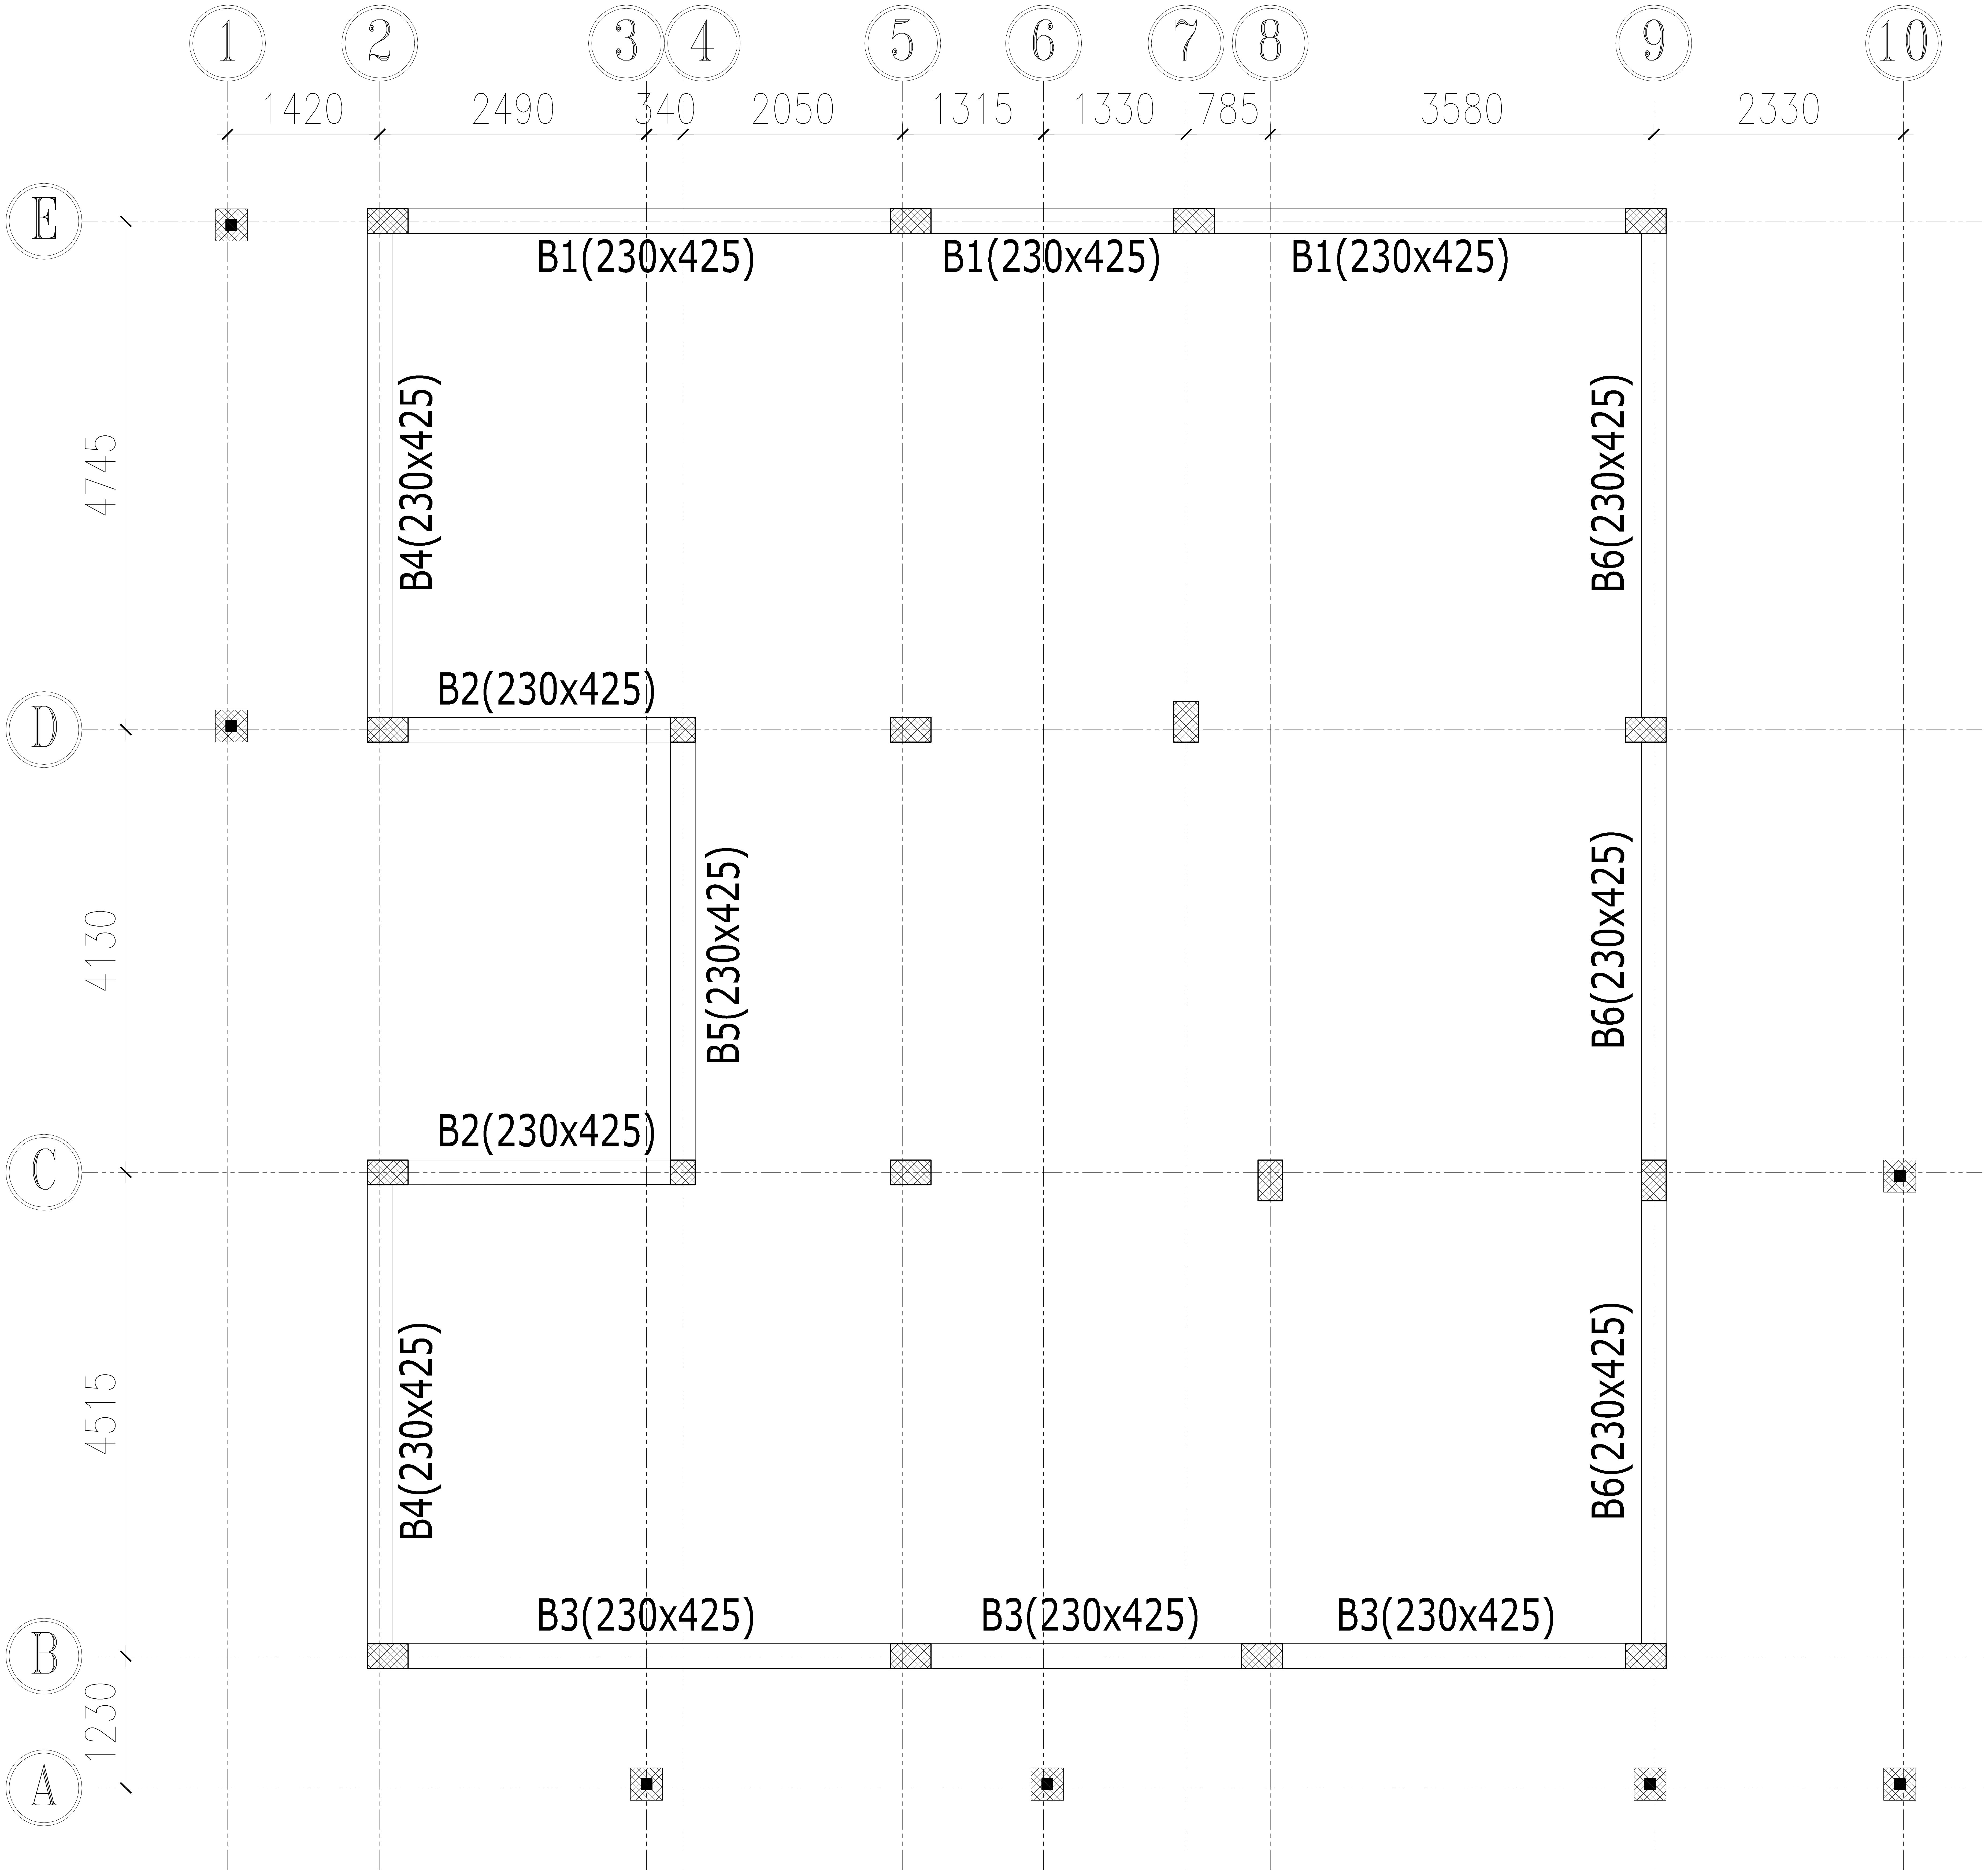
1
2
3
4
5
6
7
8
9
10
1420
2490
340
2050
1315
1330
785
3580
2330
E
D
C
B
A
4745
4130
4515
1230
B1(230x425)
B1(230x425)
B1(230x425)
B4(230x425)
B6(230x425)
B2(230x425)
B5(230x425)
B6(230x425)
B2(230x425)
B4(230x425)
B6(230x425)
B3(230x425)
B3(230x425)
B3(230x425)

- THIS DRAWING SHALL BE READ IN CONJUNCTION WITH ALL RELEVANT ARCHITECTURAL, STRUCTURAL AND SERVICES DRAWINGS. ANY DISCREPANCY NOTICED SHALL BE BROUGHT TO THE ATTENTION OF THE CONSULTANTS AND RESOLVED AS SOON AS POSSIBLE BUT ALWAYS PRIOR TO

DIRECTION:

N

ARCHITECTURAL CONSULTANT:

also.
design
a little story of design

STRUCTURAL& MEP CONSULTANTS

JASHRITHA ASSOCIATES
AND MEP PLANNERS
4th FLOOR(4B), HIG 129, KPHB COLONY, KUKATPALLY,
(SUB BRANCH:PR NAGAR ERRAGADDA.)
HYDERABAD 500072, TELANGANA, INDIA
Phone : 9700441106.
E-mail : jashreyansh.consultatns@gmail.com
& jashritha.mep@gmail.com

PROJECT:

ANKURA HOMES_THE WOODS
AT KEESARAGUTTA

DRAWING TITLE:

1625_WEST VILLA
ROOF BEAM LAYOUT

DESIGN ENGG : AJAY	APPROVED :
SCALE : NTS	DRAWN : PK
DATE : 07-10-2026	CHECKED : PRADEEP

DRAWING NO: SD-05
REV.NO: 01

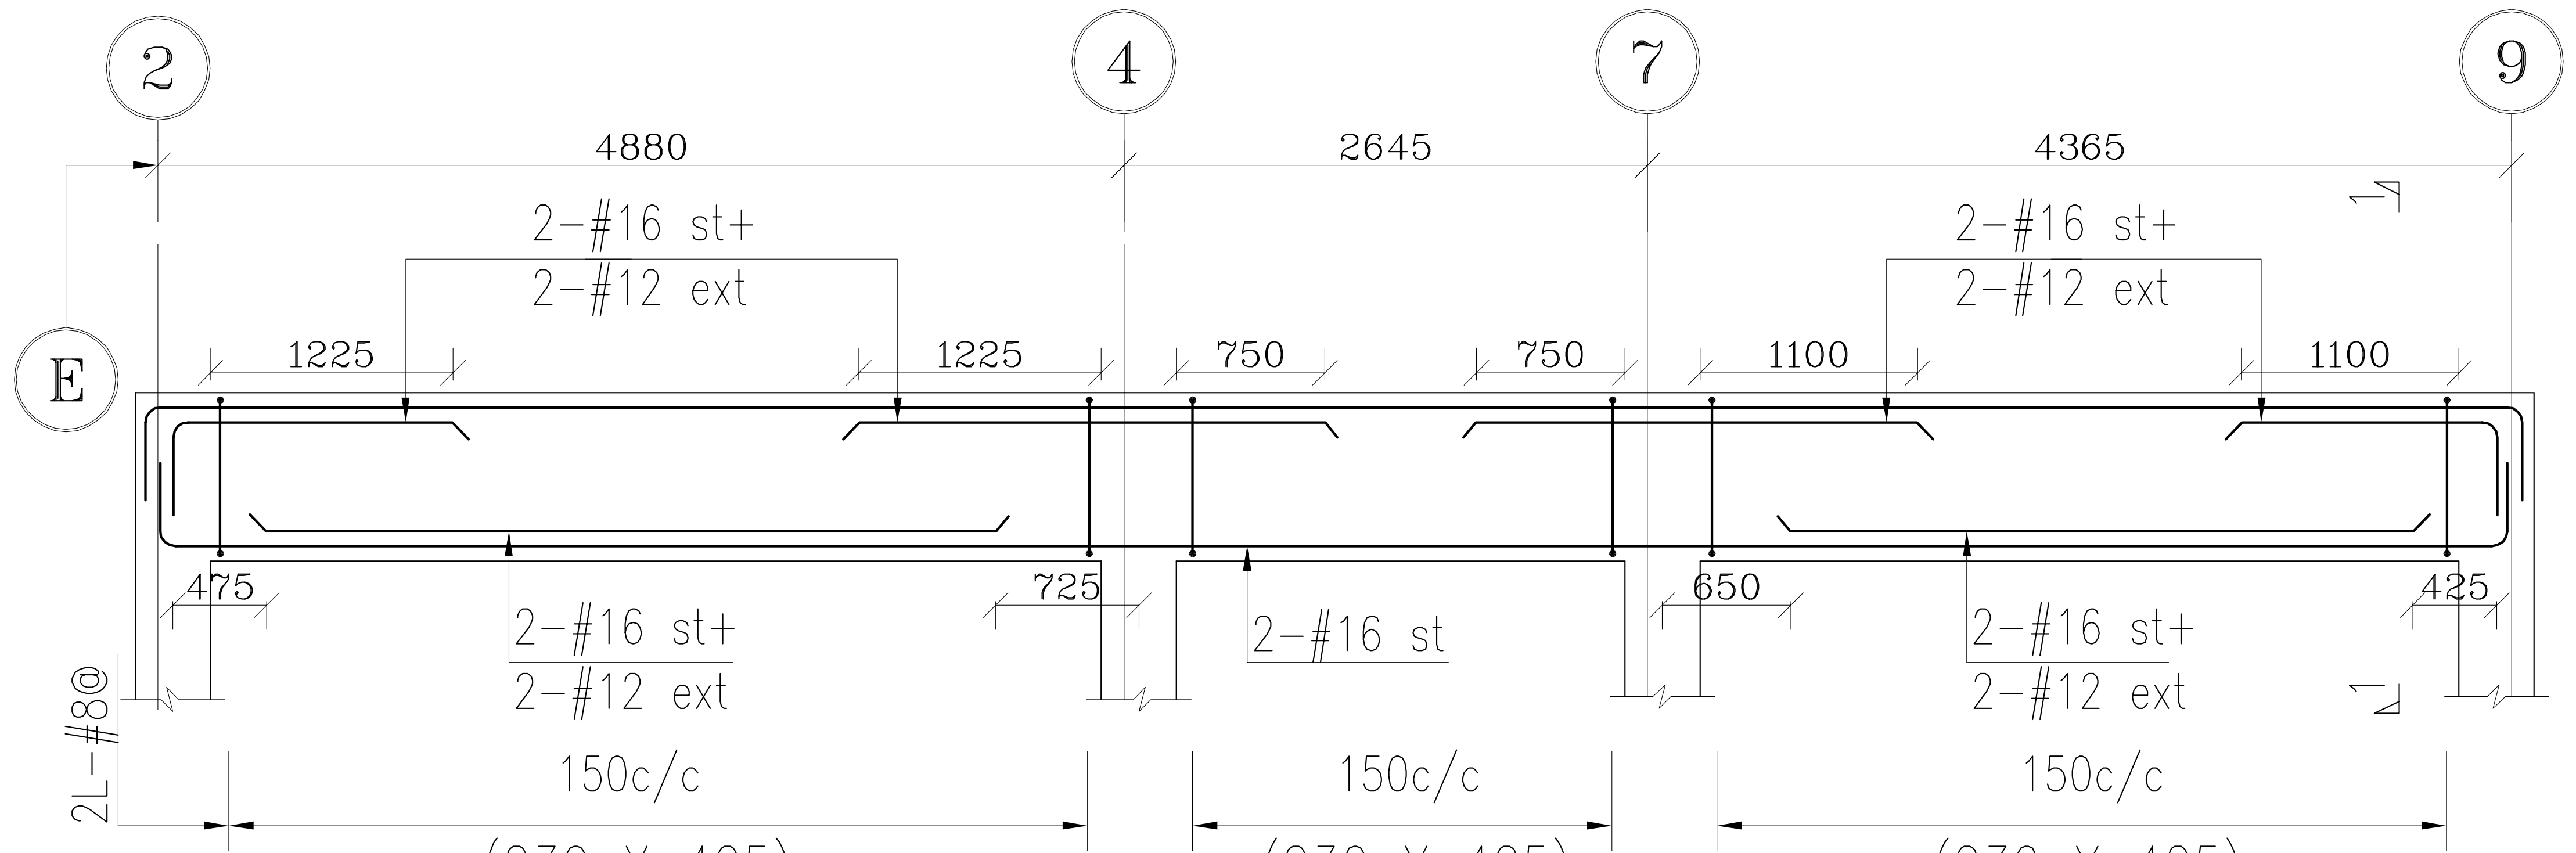
2
4
7
9
E
4880
2645
4365
2-#16 st+
2-#12 ext
1225
1225
750
750
1100
1100
475
725
650
425
2-#16 st
2L-#8@
150c/c
(230 X 425)
1
1

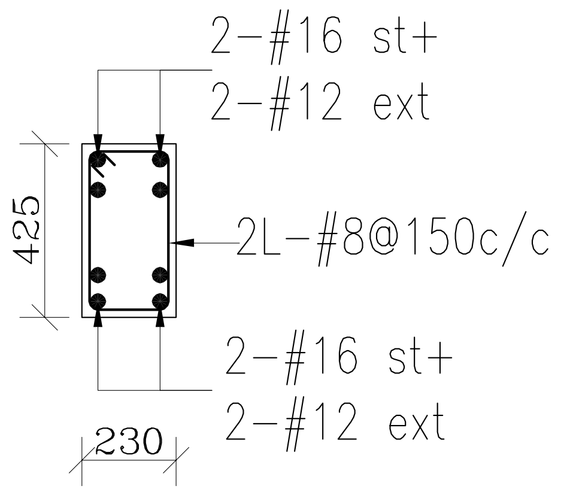
2-#16 st+
2-#12 ext
425
2L-#8@150c/c
2-#16 st+
2-#12 ext
230

SECTION 1-1

L/S OF BEAM B1(230X425)

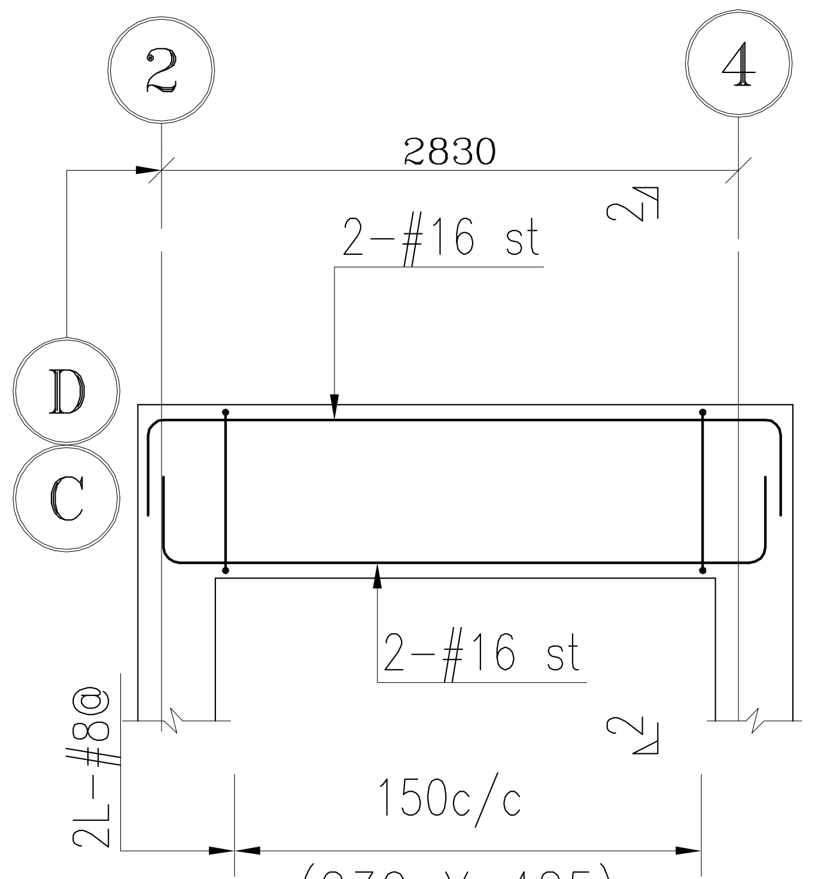
2
4
D
C
2830
2-#16 st
2L-#8@
150c/c
(230 X 425)
2
2

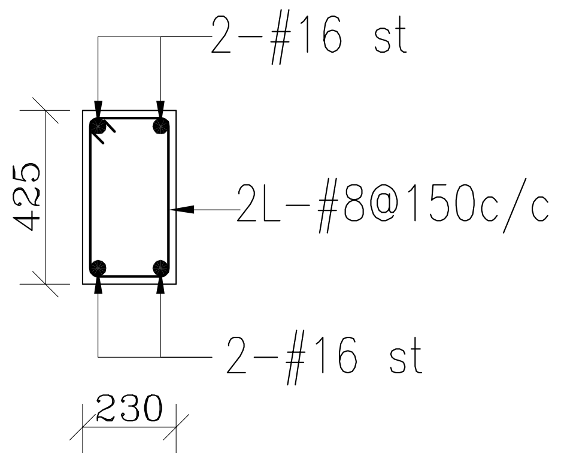
2-#16 st
425
2L-#8@150c/c
2-#16 st
230

SECTION 2-2

L/S OF BEAM B2(230X425)

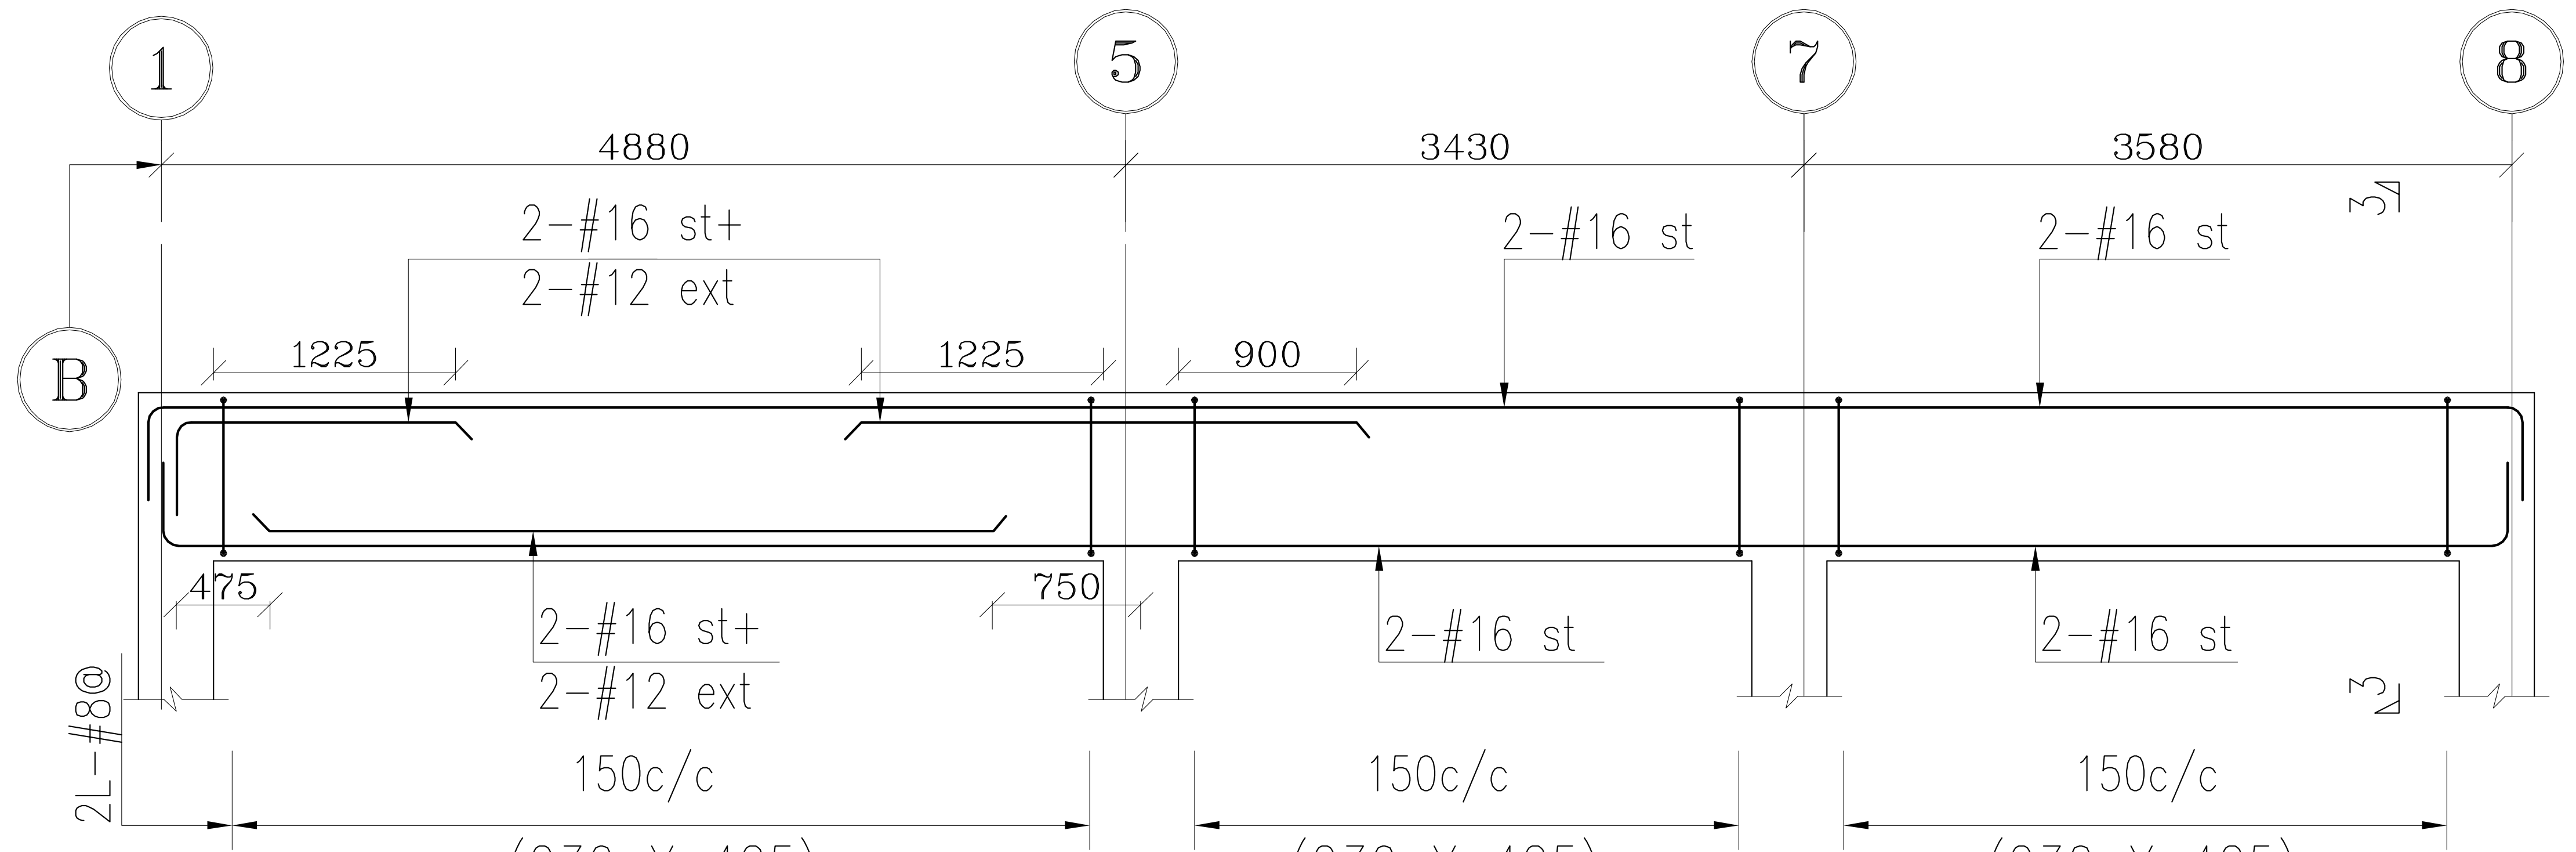
1
5
7
8
B
4880
3430
3580
2-#16 st+
2-#12 ext
2-#16 st
1225
1225
900
475
750
2L-#8@
150c/c
(230 X 425)
3
3

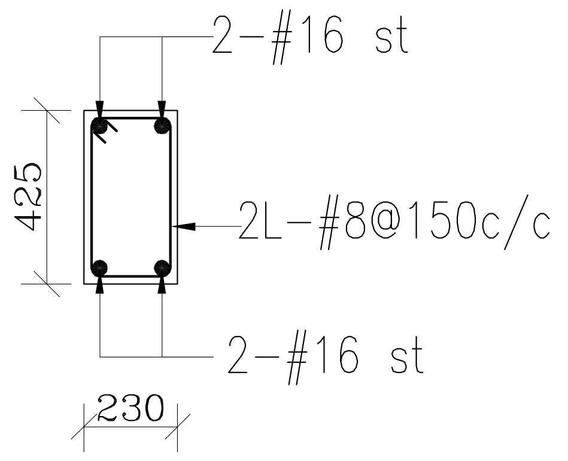
2-#16 st
425
2L-#8@150c/c
2-#16 st
230

SECTION 3-3

L/S OF BEAM B3(230X425)

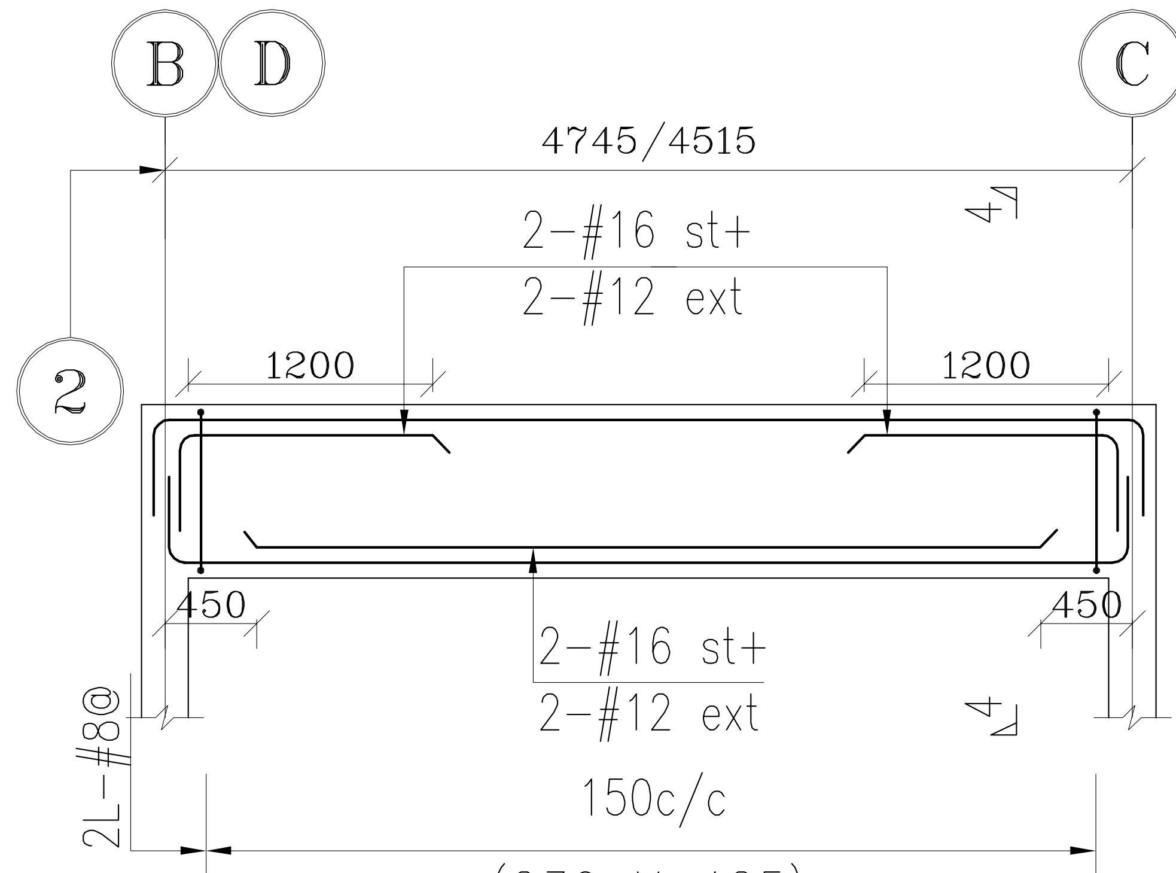
B
D
C
E
2
4745/4515
2-#16 st+
2-#12 ext
1200
1200
450
450
2L-#8@
150c/c
(230 X 425)
4
4

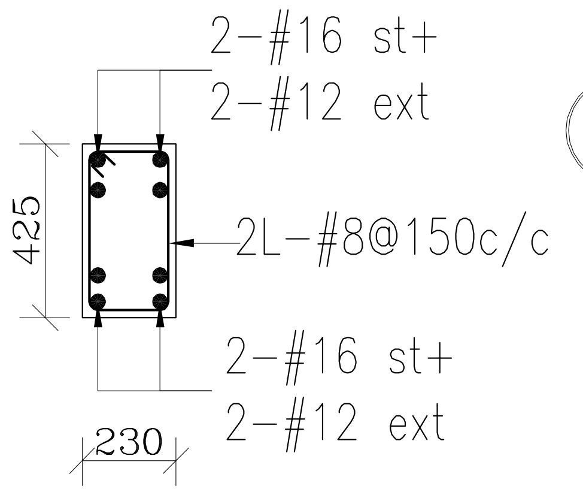
2-#16 st+
2-#12 ext
425
2L-#8@150c/c
2-#16 st+
2-#12 ext
230

SECTION 4-4

L/S OF BEAM B4(230X425)

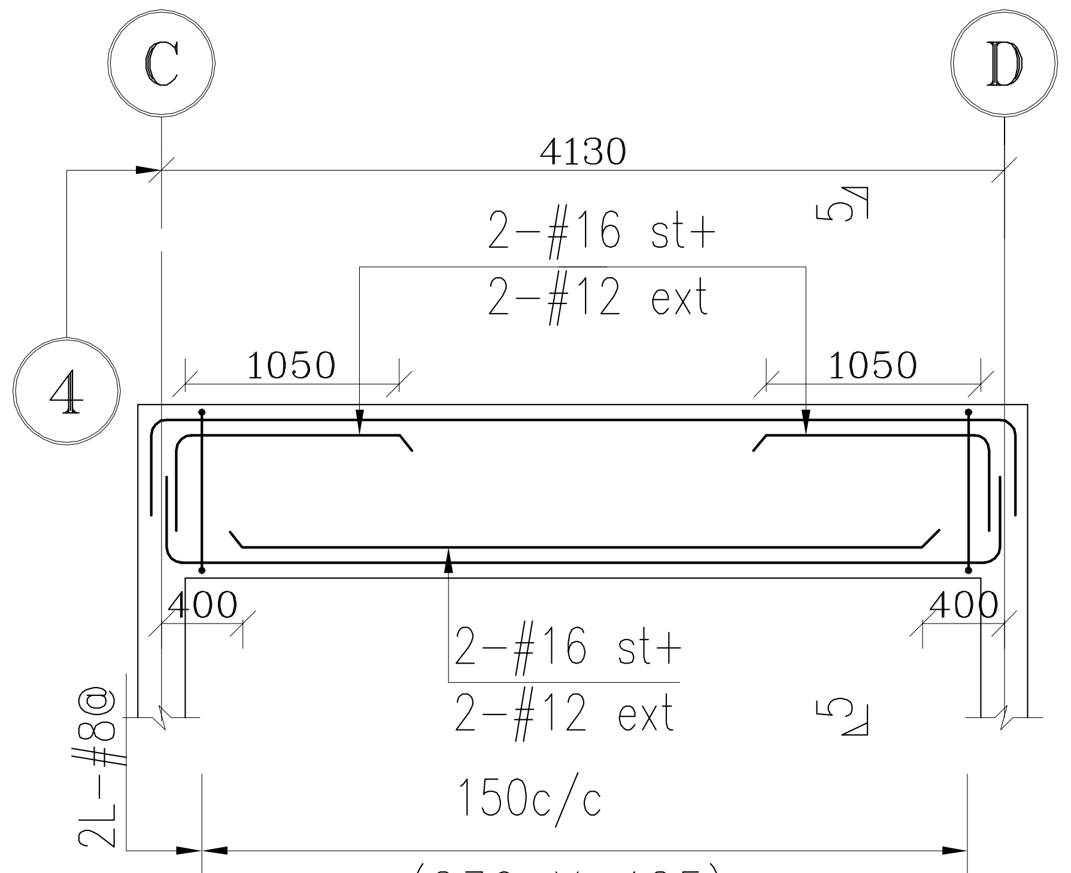
C
D
4
4130
2-#16 st+
2-#12 ext
1050
1050
400
400
2L-#8@
150c/c
(230 X 425)
5
5

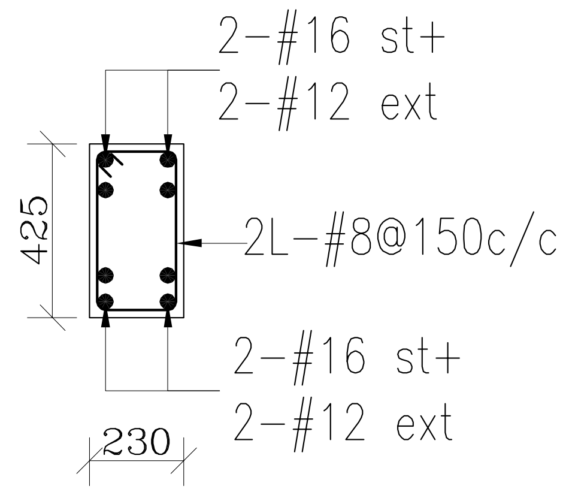
2-#16 st+
2-#12 ext
425
2L-#8@150c/c
2-#16 st+
2-#12 ext
230

SECTION 5-5

L/S OF BEAM B5(230X425)

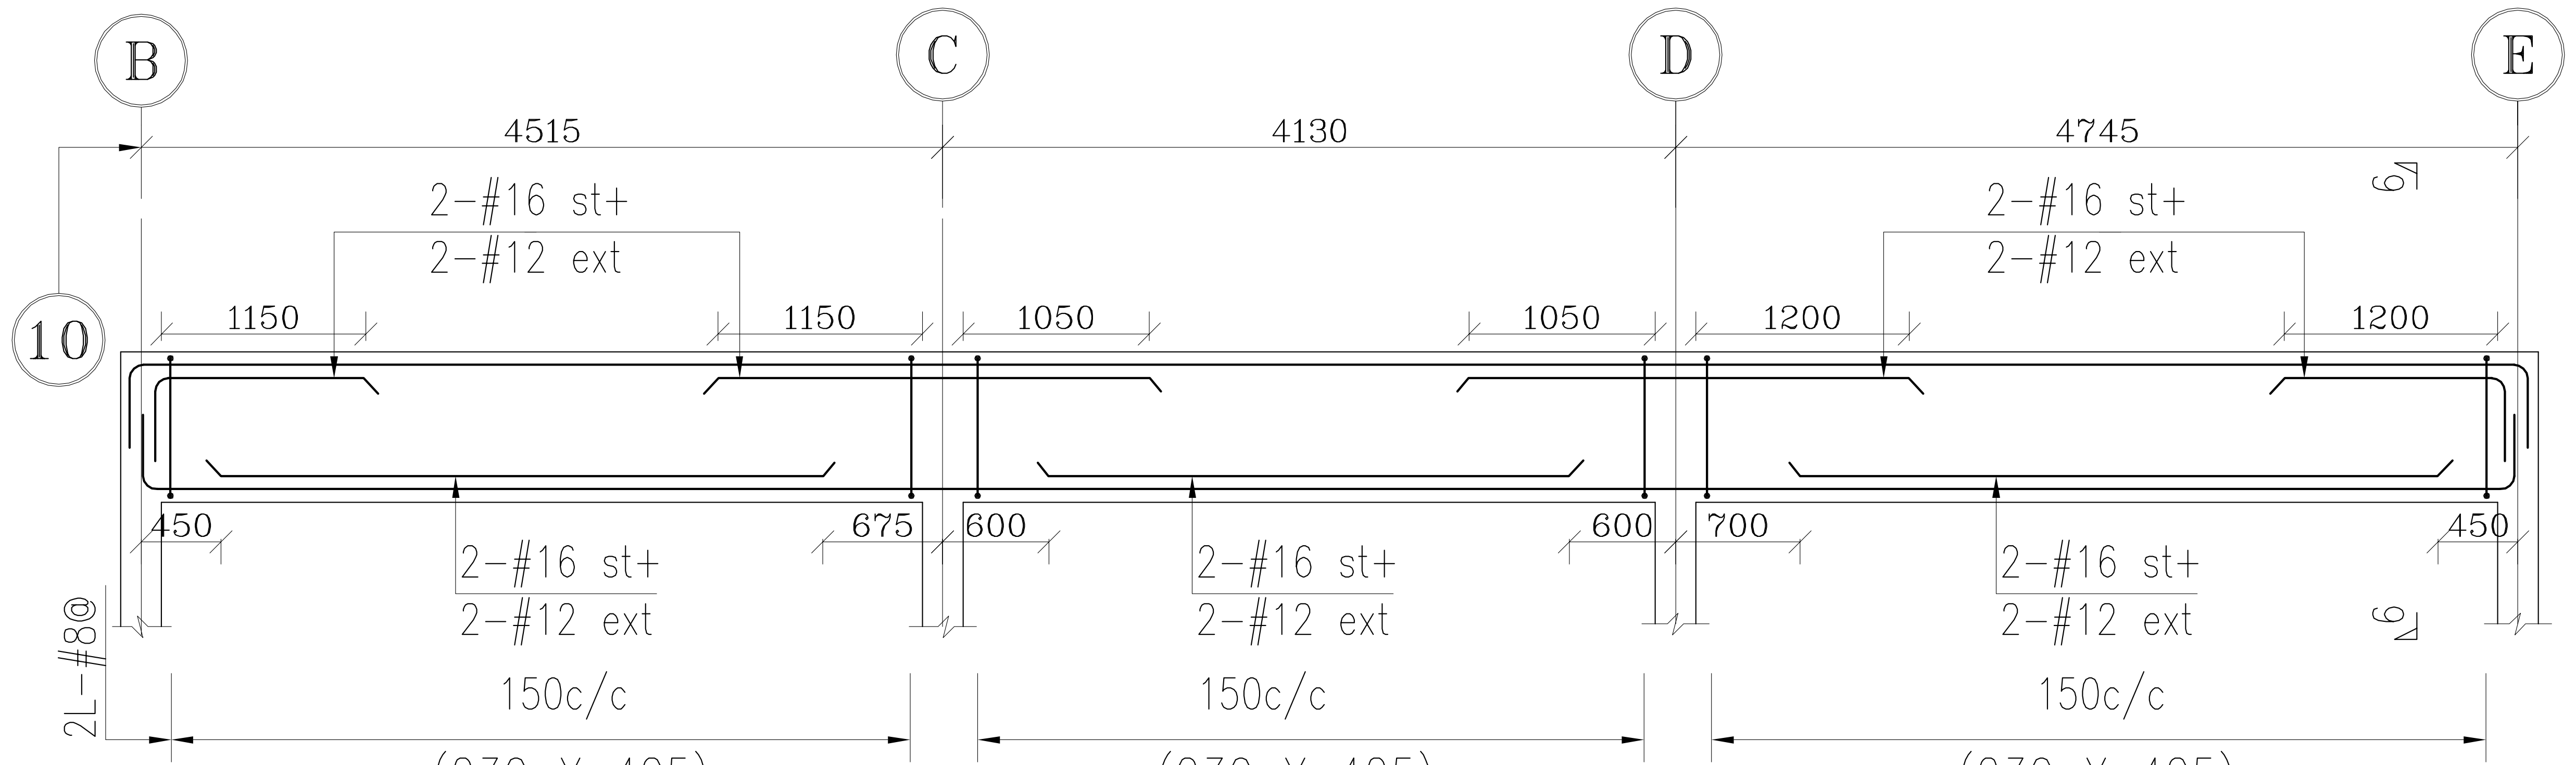
B
C
D
E
10
4515
4130
4745
2-#16 st+
2-#12 ext
1150
1150
1050
1050
1200
1200
450
675
600
600
700
450
2L-#8@
150c/c
(230 X 425)
6
6

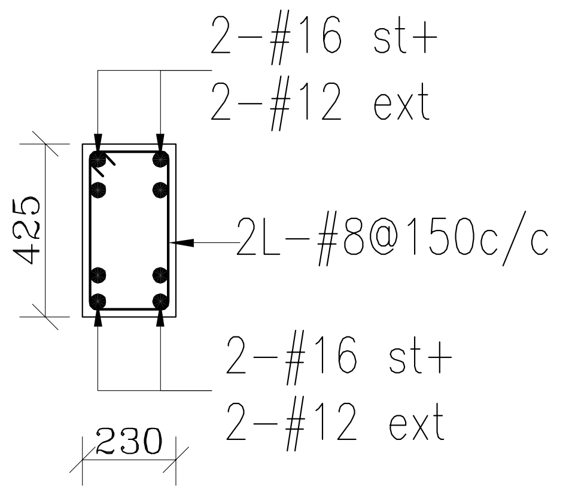
2-#16 st+
2-#12 ext
425
2L-#8@150c/c
2-#16 st+
2-#12 ext
230

SECTION 6-6

L/S OF BEAM B6(230X425)

- THIS DRAWING SHALL BE READ IN CONJUNCTION WITH ALL RELEVANT ARCHITECTURAL, STRUCTURAL AND SERVICES DRAWINGS. ANY DISCREPANCY NOTICED SHALL BE BROUGHT TO THE ATTENTION OF THE CONSULTANTS AND RESOLVED AS SOON AS POSSIBLE BUT ALWAYS PRIOR TO

DIRECTION:

ARCHITECTURAL CONSULTANT:

STRUCTURAL& MEP CONSULTANTS

JASHRITHA ASSOCIATES
AND MEP PLANNERS
4th FLOOR(4B), HIG 129, KPHB COLONY, KUKATPALLY,
(SUB BRANCH:PR NAGAR ERRAGADDA.)
HYDERABAD 500072, TELANGANA, INDIA
Phone : 9700441106.
E-mail : jashreyansh.consultatns@gmail.com
& jashritha.mep@gmail.com

PROJECT:

ANKURA HOMES_THE WOODS
AT KEESARAGUTTA

DRAWING TITLE:

1625_WEST VILLA
ROOF BEAM DETAILS

DESIGN ENGG : AJAY	APPROVED :
SCALE : NTS	DRAWN : PK
DATE : 25-09-2026	CHECKED : PRADEEP
DRAWING NO: SD-06	REV.NO: