
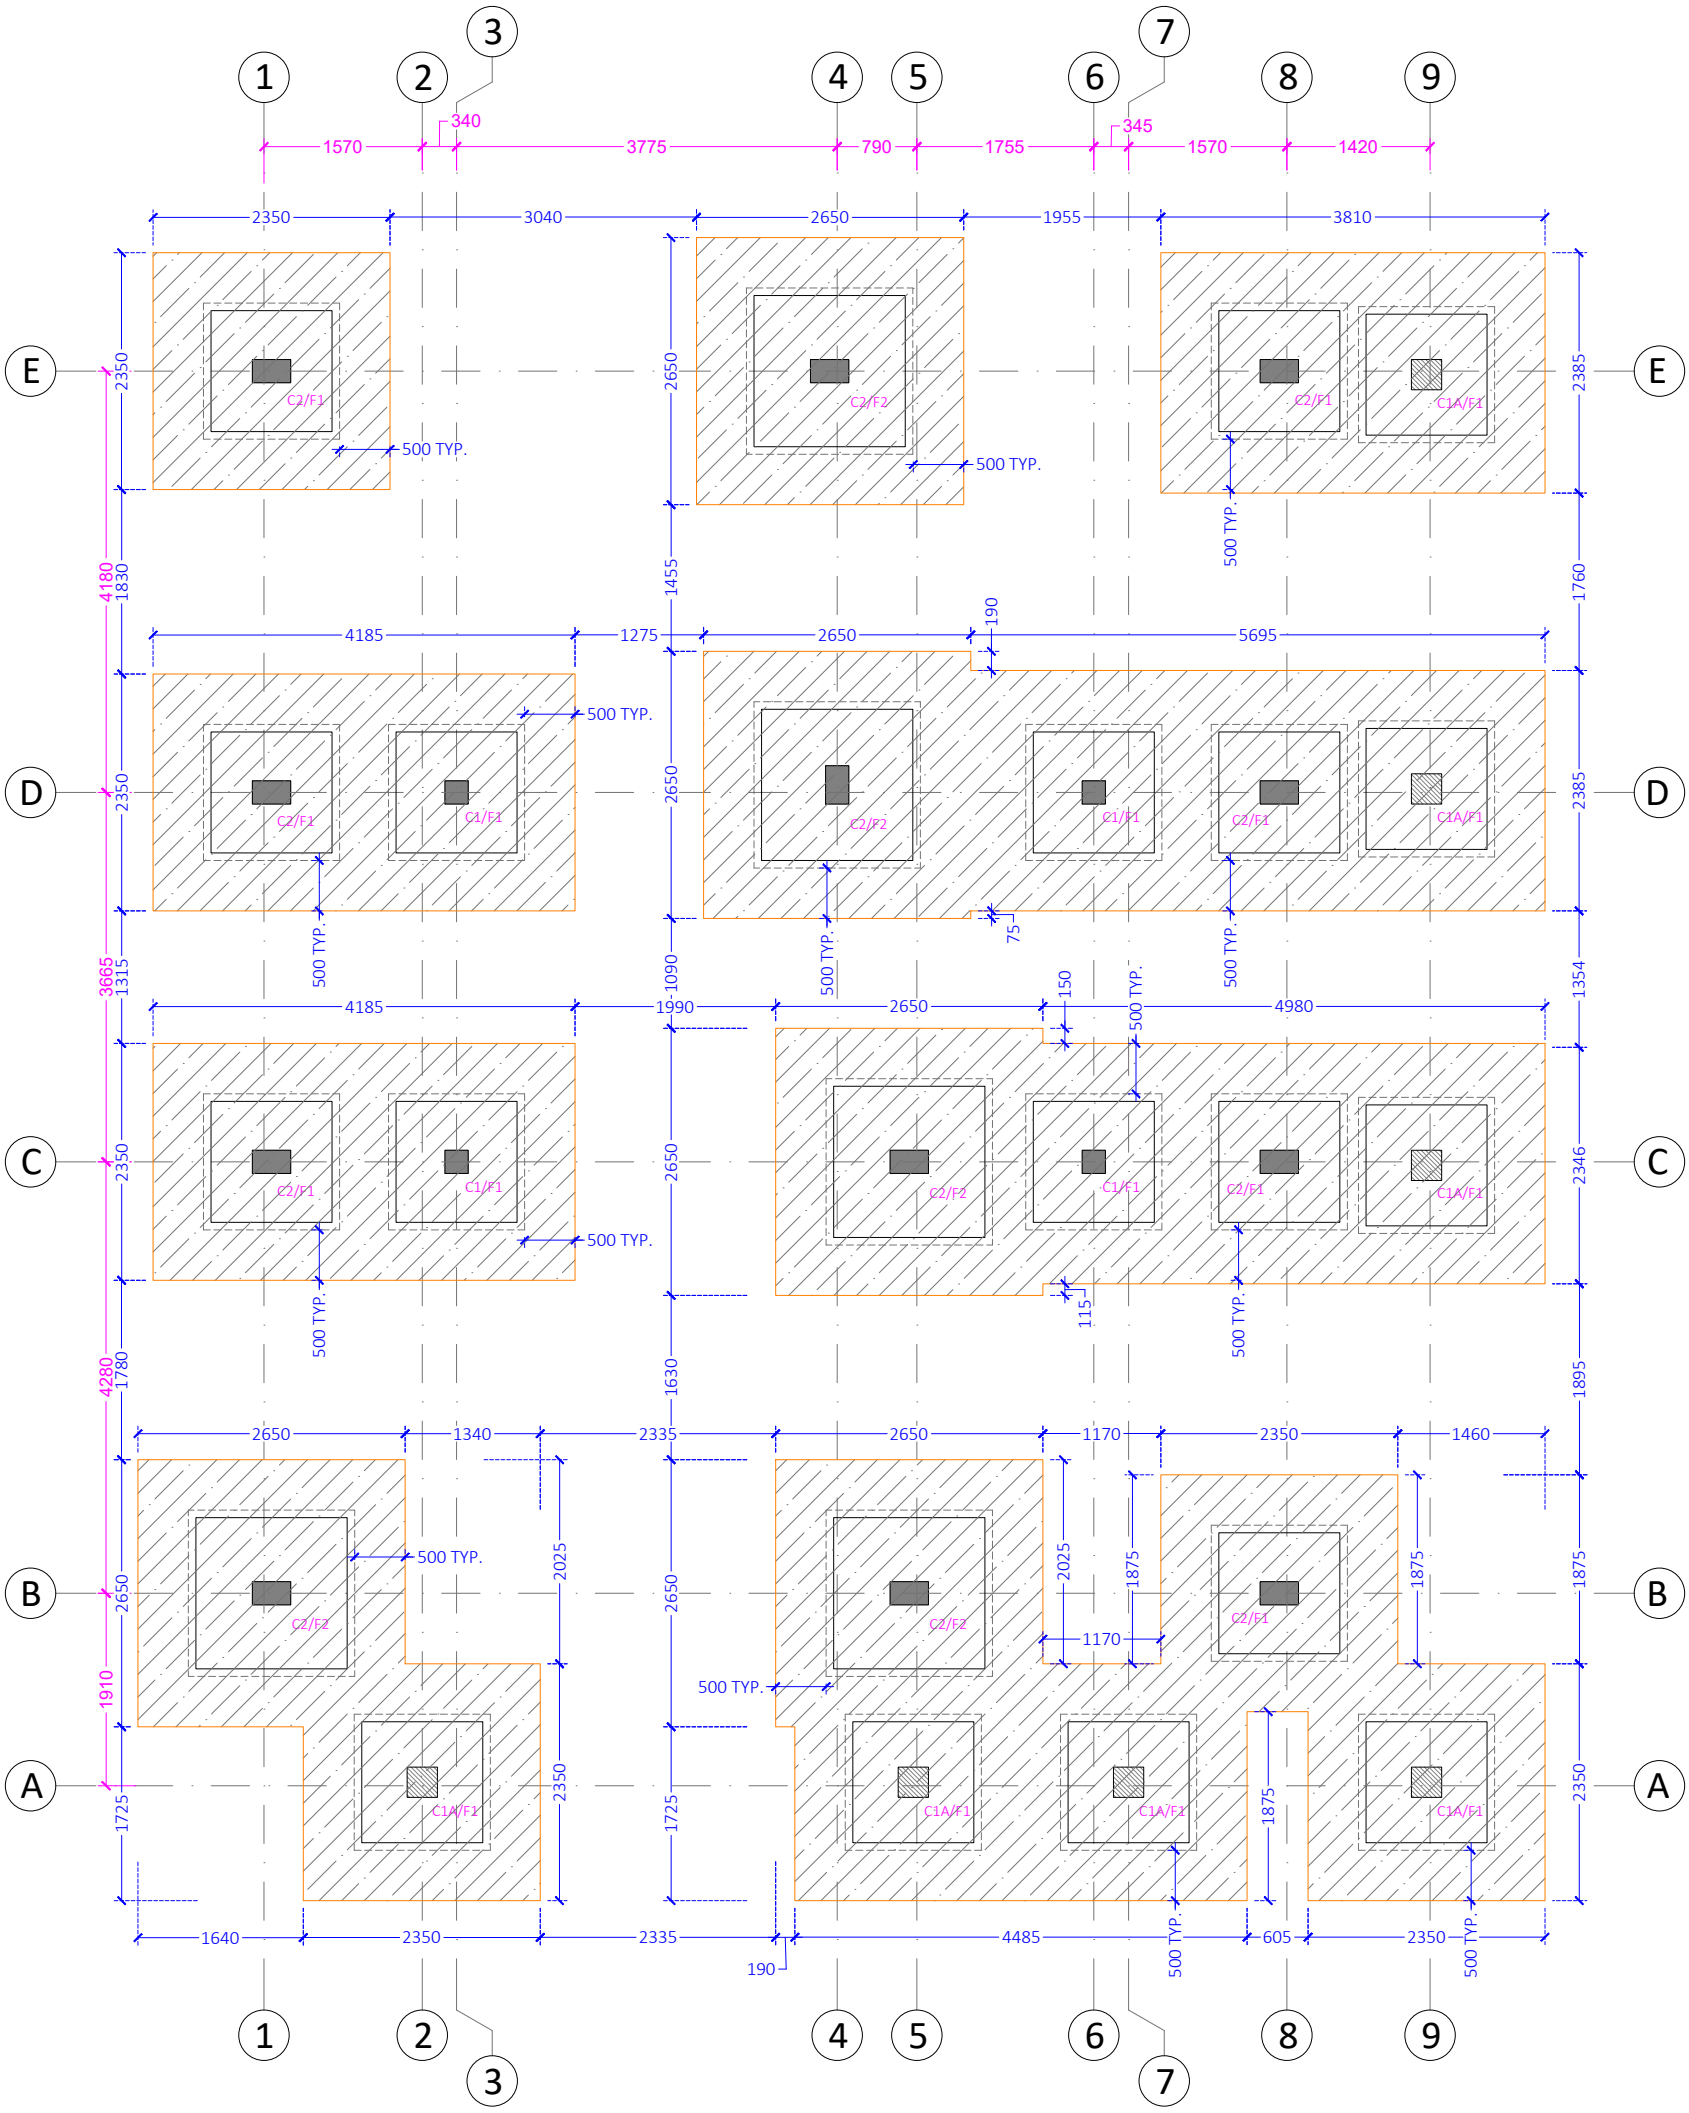


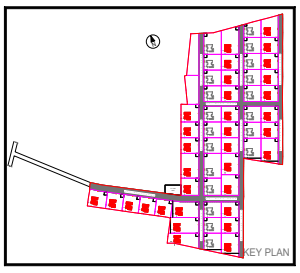

LEGEND:

- COLUMN TERMINATES AT ROOF LEVEL
- COLUMN TERMINATES AT PLINTH LEVEL
- EXCAVATION MARKING

NOTE: Excavation offset of 500mm is considered from PCC outer edge.

GENERAL NOTES:

- ALL DIMENSIONS ARE IN MILLIMETERS
- THIS DRAWING IS A COPYRIGHT AND PROPERTY OF THE ARCHITECT, IS NOT TO BE PRODUCED, COPIED, HANDED OVER TO THIRD PARTY OR USED FOR ANY OTHER PURPOSE OTHER THAN FOR WHICH IT IS INTENDED.
- ALL DIMENSIONS SHALL BE VERIFIED ON SITE PRIOR TO START OF WORK ANY DISCREPANCY SHALL BE BROUGHT TO THE NOTICE OF THE ARCHITECT.
- THE CONTRACTOR MUST CHECK ALL DIMENSIONS AND DETAILS AND BE RESPONSIBLE FOR THE SAME. ANY DISCREPANCY SHALL BE BROUGHT TO THE NOTICE OF THE ARCHITECT.
- THIS DRAWING IS TO BE READ AND NOT SCALED.
- THIS DRAWING SHALL BE READ IN CONJUNCTION WITH ALL RELEVANT ARCHITECTURAL, STRUCTURAL AND SERVICES DRAWINGS. ANY DISCREPANCY NOTICED SHALL BE BROUGHT TO THE ATTENTION OF THE CONSULTANTS AND RESOLVED AS SOON AS POSSIBLE BUT ALWAYS PRIOR TO PROCUREMENT / EXECUTION OF WORKS

NO	DESCRIPTION	DATE	SIGN.

REVISION

ARCHITECTURAL CONSULTANT: also.design

STRUCTURAL CONSULTANTS : JA

PROJECT :

ANKURA HOMES_THE WOODS
AT KEESARAGUTTA

MEP CONSULTANTS : JA


GOOD FOR CONSTRUCTION


DRAWING TITLE: (1/2)

1215_EAST VILLA
EXCAVATION LAYOUT

ARCHITECT :	HARISH	APPROVED :	HARISH
SCALE :	NTS	DRAWN :	DHARANI
DATE :	28-10-2026	CHECKED :	SHANMUKHI

DRAWING NO : REV.NO:

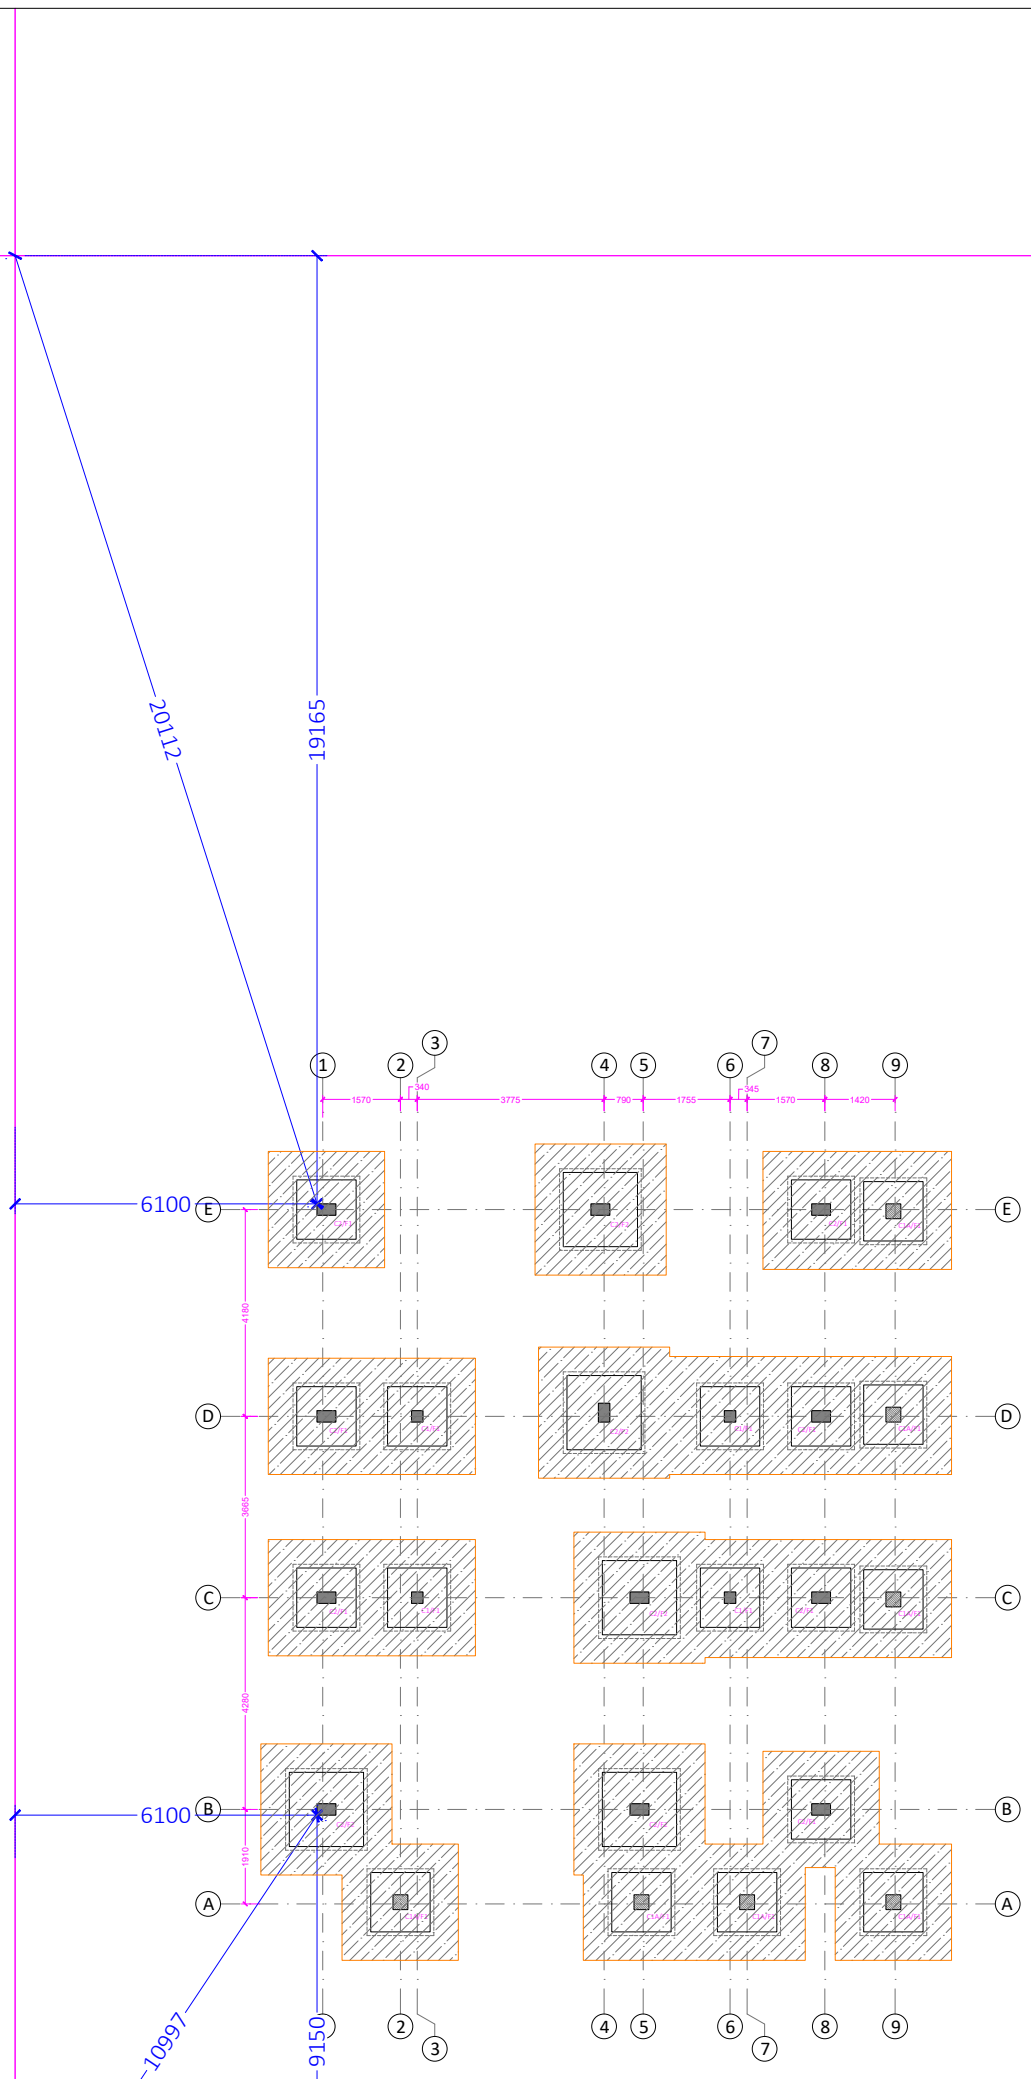

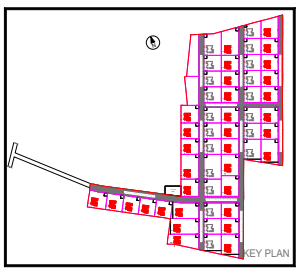

KEY PLAN

LEGEND:

- COLUMN TERMINATES AT ROOF LEVEL
- COLUMN TERMINATES AT PLINTH LEVEL
- EXCAVATION MARKING
- PLOT BOUNDARY

NOTE: Excavation offset of 500mm is considered from PCC outer edge.

GENERAL NOTES:

- ALL DIMENSIONS ARE IN MILLIMETERS
- THIS DRAWING IS A COPYRIGHT AND PROPERTY OF THE ARCHITECT, IS NOT TO BE PRODUCED, COPIED, HANDED OVER TO THIRD PARTY OR USED FOR ANY OTHER PURPOSE OTHER THAN FOR WHICH IT IS INTENDED.
- ALL DIMENSIONS SHALL BE VERIFIED ON SITE PRIOR TO START OF WORK ANY DISCREPANCY SHALL BE BROUGHT TO THE NOTICE OF THE ARCHITECT.
- THE CONTRACTOR MUST CHECK ALL DIMENSIONS AND DETAILS AND BE RESPONSIBLE FOR THE SAME. ANY DISCREPANCY SHALL BE BROUGHT TO THE NOTICE OF THE ARCHITECT.
- THIS DRAWING IS TO BE READ AND NOT SCALED.
- THIS DRAWING SHALL BE READ IN CONJUNCTION WITH ALL RELEVANT ARCHITECTURAL, STRUCTURAL AND SERVICES DRAWINGS. ANY DISCREPANCY NOTICED SHALL BE BROUGHT TO THE ATTENTION OF THE CONSULTANTS AND RESOLVED AS SOON AS POSSIBLE BUT ALWAYS PRIOR TO PROCUREMENT / EXECUTION OF WORKS

NO	DESCRIPTION	DATE	SIGN.

REVISION

ARCHITECTURAL CONSULTANT:

also. design

also design GFC HYDERABAD

STRUCTURAL CONSULTANTS :

JA

PROJECT :

ANKURA HOMES_THE WOODS
AT KEESARAGUTTA

MEP CONSULTANTS :

JA

GOOD FOR CONSTRUCTION

DRAWING TITLE: (2/2)

1215_EAST VILLA
EXCAVATION LAYOUT

ARCHITECT :	HARISH	APPROVED :	HARISH
SCALE :	NTS	DRAWN :	DHARANI
DATE :	28-10-2026	CHECKED :	SHANMUKHI

DRAWING NO :

REV.NO: