
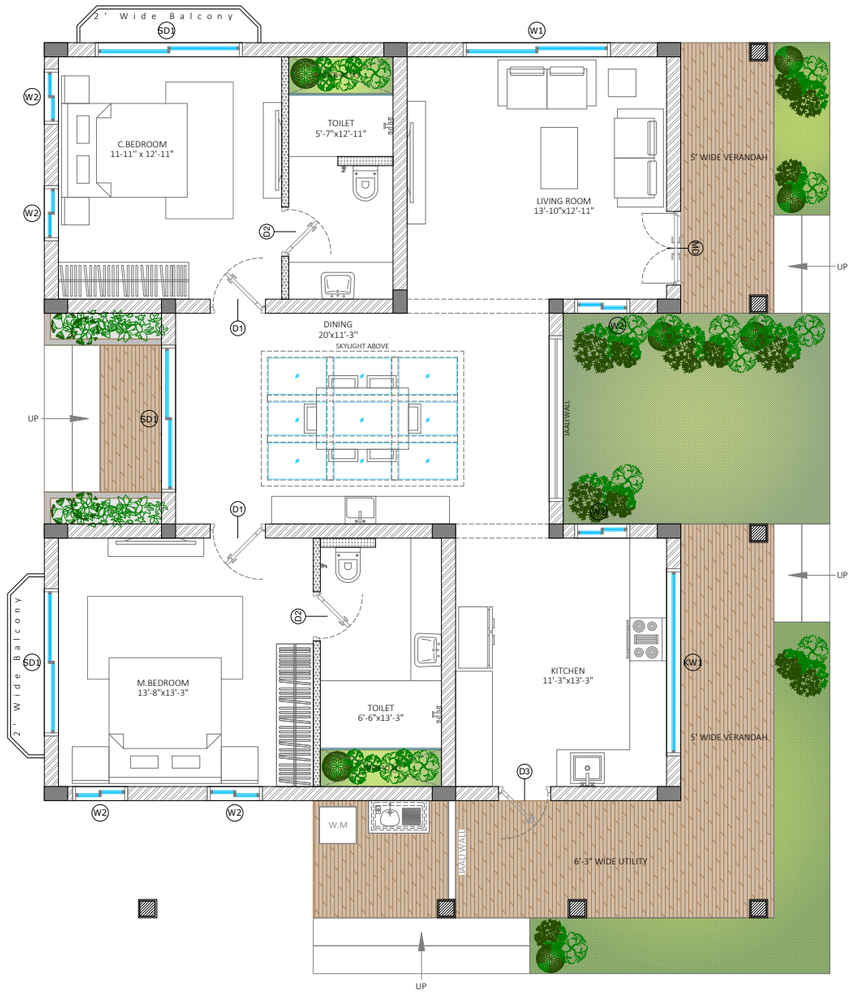



EAST VILLA FLOOR PLAN

BUILT-UP AREA : 1215 SQ.FT

VERANDAH AREA : 326 SQ.FT

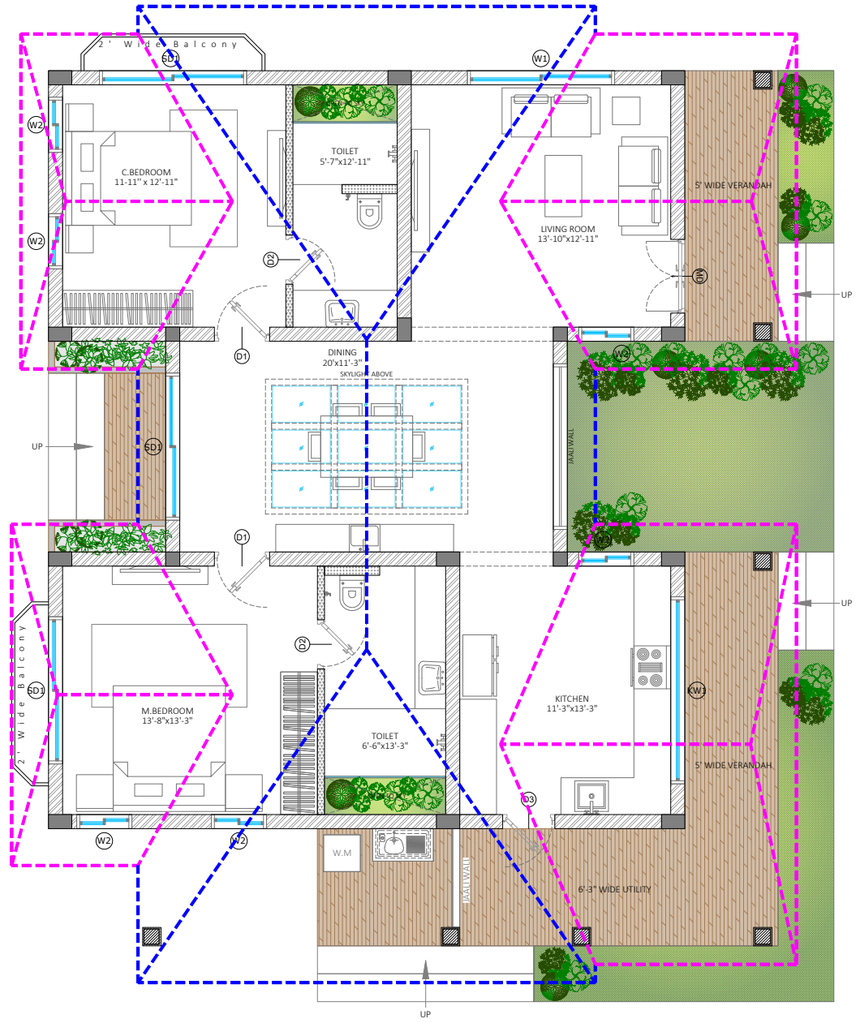

EAST VILLA FLOOR PLAN WITH ROOF ABOVE

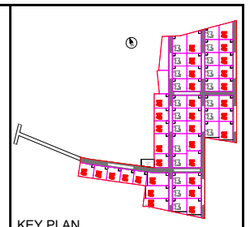

KEY PLAN

LEGEND:

- PRIMARY ROOF
- SECONDARY ROOF
- COLUMN TERMINATES AT ROOF LEVEL
- COLUMN TERMINATES AT PLINTH LEVEL
- MS COLUMN
- 230MM THICK WALL
- 115MM THICK WALL
- LEDGE WALL (150MM THICK WALL TERMINATING AT 1250MM FROM SFL)

GENERAL NOTES:

- ALL DIMENSIONS ARE IN MILLIMETERS
- THIS DRAWING IS A COPYRIGHT AND PROPERTY OF THE ARCHITECT, IS NOT TO BE PRODUCED, COPIED, HANDED OVER TO THIRD PARTY OR USED FOR ANY OTHER PURPOSE OTHER THAN FOR WHICH IT IS INTENDED.
- ALL DIMENSIONS SHALL BE VERIFIED ON SITE PRIOR TO START OF WORK. ANY DISCREPANCY SHALL BE BROUGHT TO THE NOTICE OF THE ARCHITECT.
- THE CONTRACTOR MUST CHECK ALL DIMENSIONS AND DETAILS AND BE RESPONSIBLE FOR THE SAME. ANY DISCREPANCY SHALL BE BROUGHT TO THE NOTICE OF THE ARCHITECT.
- THIS DRAWING IS TO BE READ AND NOT SCALED.
- THIS DRAWING SHALL BE READ IN CONJUNCTION WITH ALL RELEVANT ARCHITECTURAL, STRUCTURAL AND SERVICES DRAWINGS. ANY DISCREPANCY NOTICED SHALL BE BROUGHT TO THE ATTENTION OF THE CONSULTANTS AND RESOLVED AS SOON AS POSSIBLE BUT ALWAYS PRIOR TO

NO	DESCRIPTION	DATE	SIGN

ARCHITECTURAL CONSULTANT:

also. design

MEP CONSULTANT:

JA

STRUCTURAL CONSULTANT:

JA

PROJECT:

ANKURA HOMES_THE WOODS AT KEESARAGUTTA

GOOD FOR CONSTRUCTION

DRAWING TITLE:

1215_EAST VILLA FLOOR PLAN

ARCHITECT : HARISH		APPROVED : HARISH	
SCALE : NTS		DRAWN : DHARANI	
DATE : 28-10-2026		CHECKED : SHANMUKHI	
DRAWING NO.		REV.NO.	