
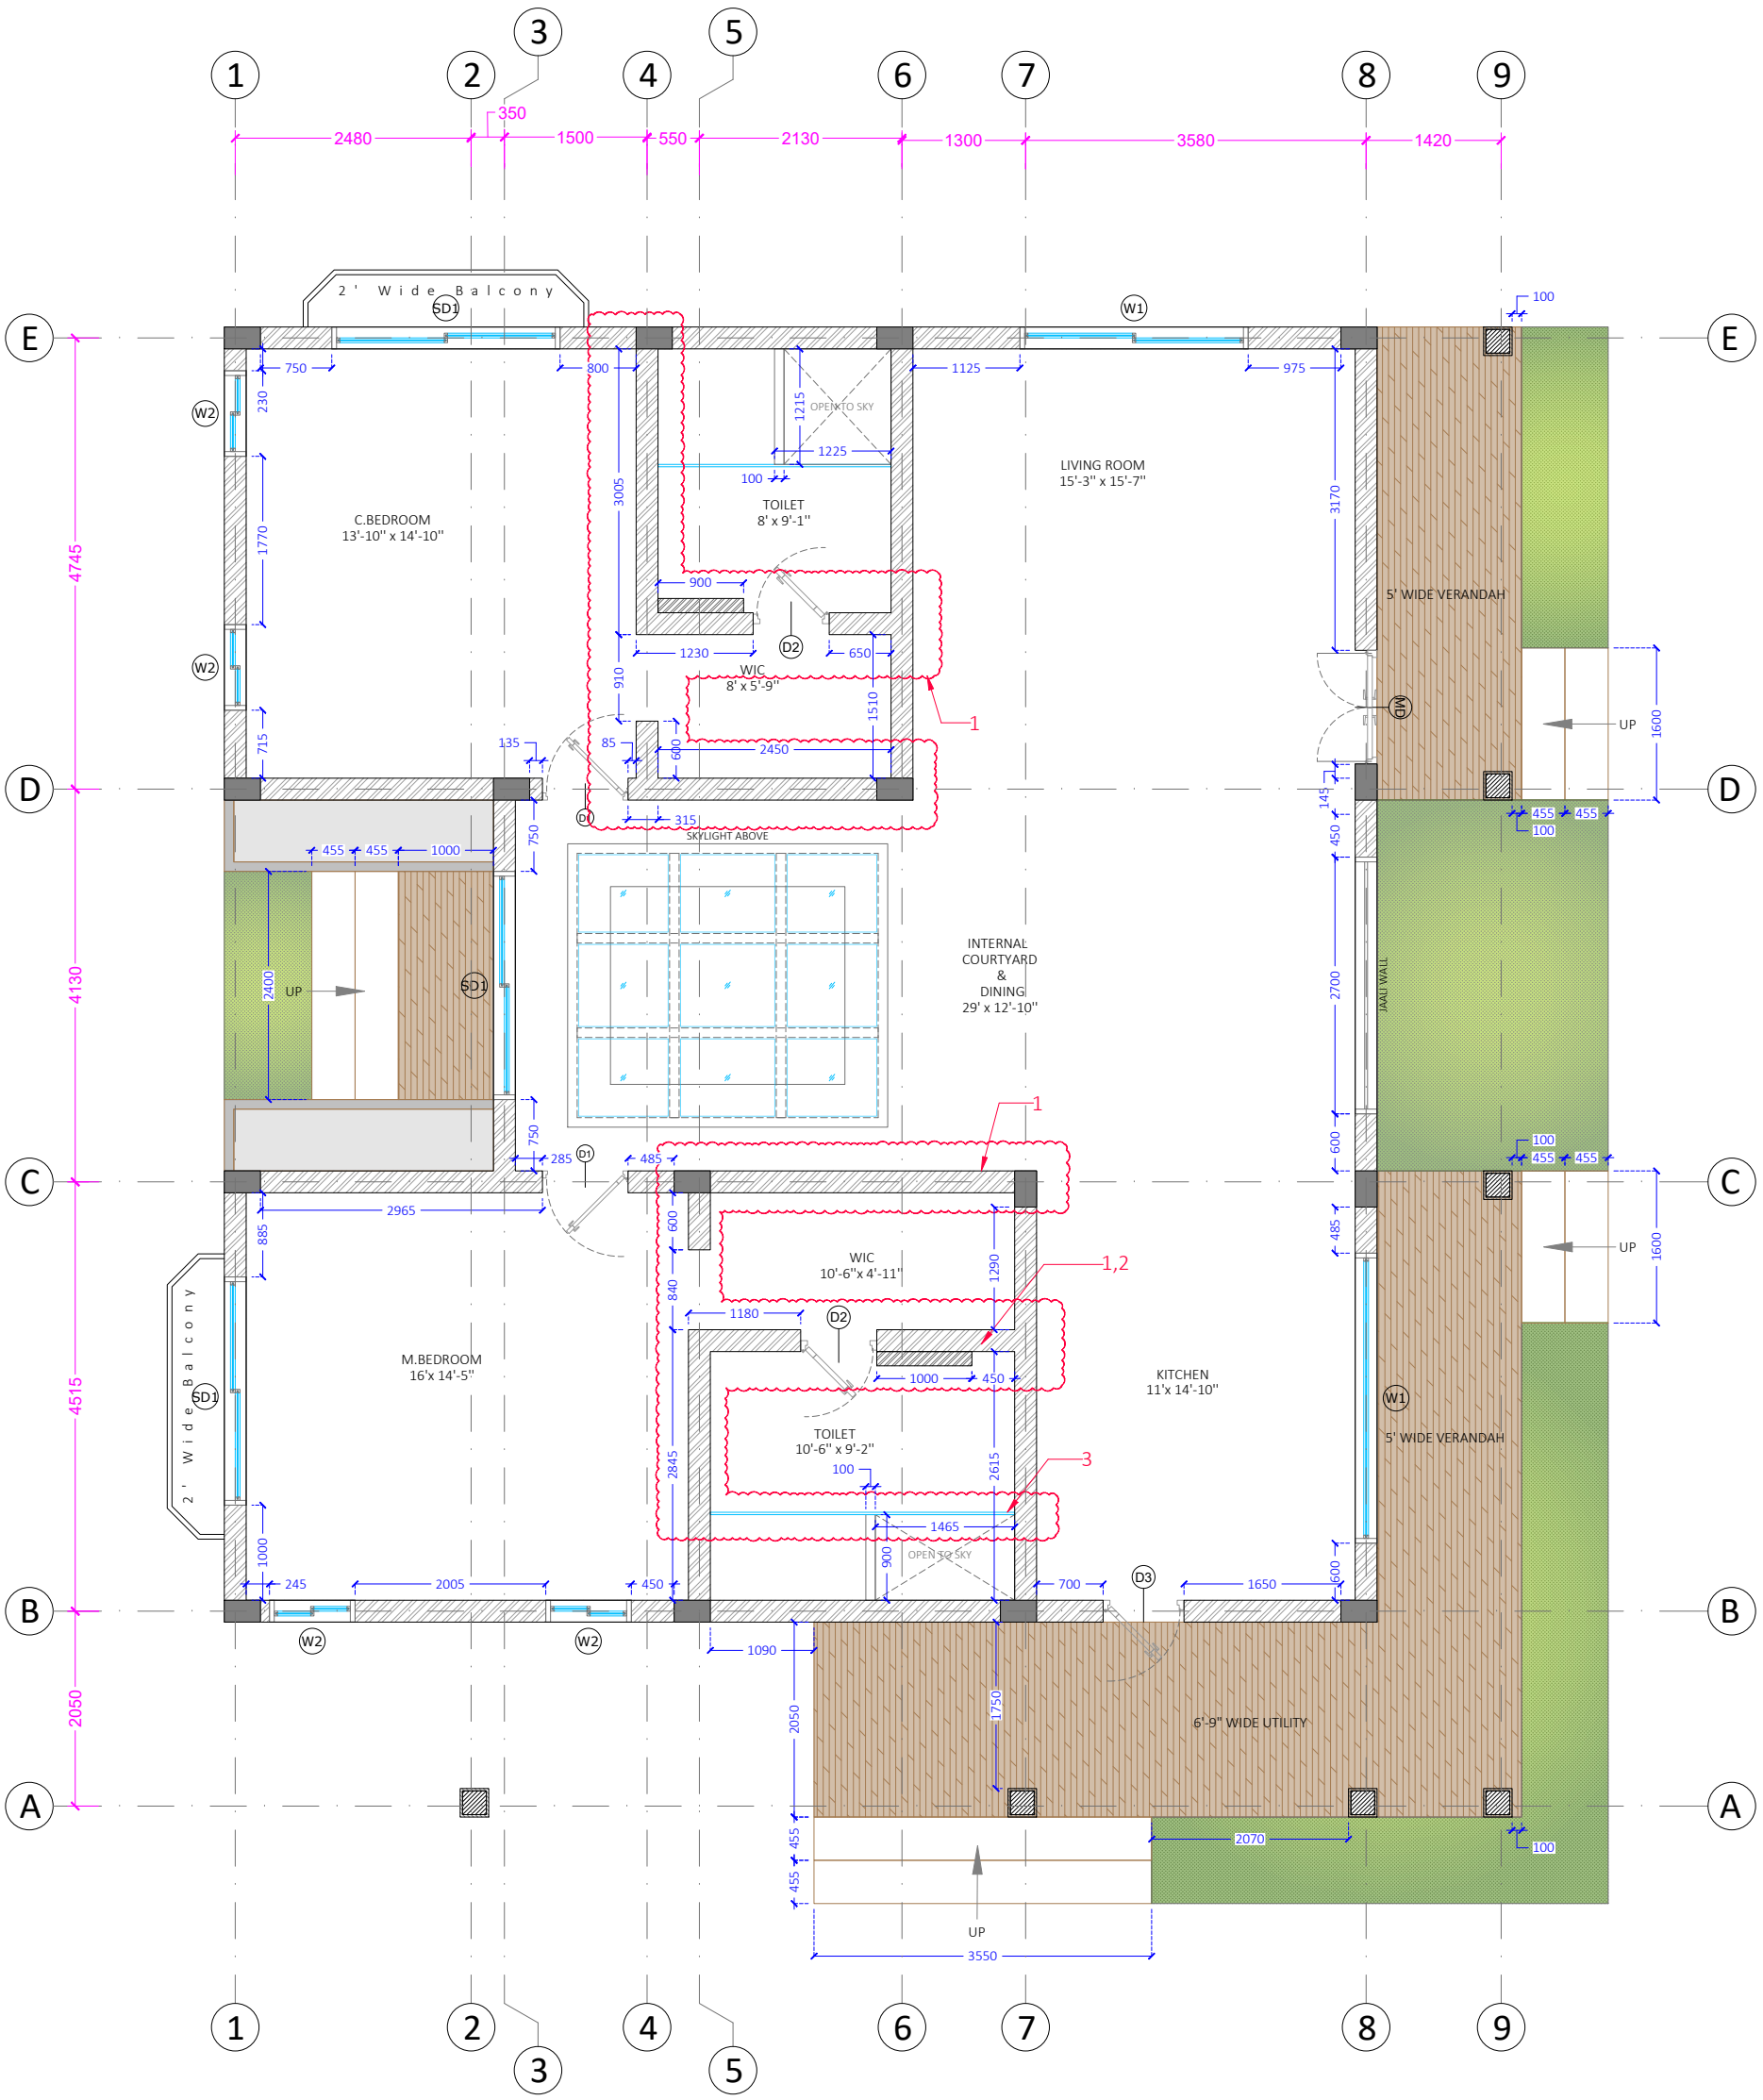



REVISION:

1. MARKED WALLS HAS BEEN REVISED TO 230MM WALLS
2. MARKED PORTION HAS BEEN MOVED 170MM TO THE SOUTH
3. MARKED PORTION HAS BEEN MOVED 60MM TO THE SOUTH

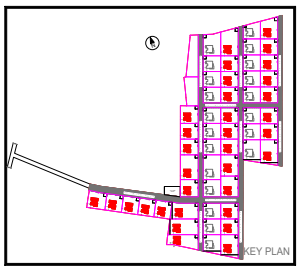


LEGEND:

- 230MM Thick Wall
- LEDGE WALL (150MM thick wall terminating at 1250mm from SFL)
- Column terminates at Roof Level
- Column terminates at Plinth Level
- MS Column

GENERAL NOTES:

- ALL DIMENSIONS ARE IN MILLIMETERS
- THIS DRAWING IS A COPYRIGHT AND PROPERTY OF THE ARCHITECT, IS NOT TO BE PRODUCED, COPIED, HANDED OVER TO THIRD PARTY OR USED FOR ANY OTHER PURPOSE OTHER THAN FOR WHICH IT IS INTENDED.
- ALL DIMENSIONS SHALL BE VERIFIED ON SITE PRIOR TO START OF WORK ANY DISCREPANCY SHALL BE BROUGHT TO THE NOTICE OF THE ARCHITECT.
- THE CONTRACTOR MUST CHECK ALL DIMENSIONS AND DETAILS AND BE RESPONSIBLE FOR THE SAME. ANY DISCREPANCY SHALL BE BROUGHT TO THE NOTICE OF THE ARCHITECT.
- THIS DRAWING IS TO BE READ AND NOT SCALED.
- THIS DRAWING SHALL BE READ IN CONJUNCTION WITH ALL RELEVANT ARCHITECTURAL, STRUCTURAL AND SERVICES DRAWINGS. ANY DISCREPANCY NOTICED SHALL BE BROUGHT TO THE ATTENTION OF THE CONSULTANTS AND RESOLVED AS SOON AS POSSIBLE BUT ALWAYS PRIOR TO PROCUREMENT / EXECUTION OF WORKS

| NO. | DESCRIPTION | DATE | SIGN. |
|---|---|---|---|
| R1 | 3. Marked portion moved 60mm to the south | 03-11-2026 | SR |
| R1 | 2. Marked portion moved 170mm to the south | 03-11-2026 | SR |
| R1 | 1. Marked walls has been revised to 230MM | 03-11-2026 | SR |

REVISION

ARCHITECTURAL CONSULTANT:

also. design

also design GFC HYDERABAD

STRUCTURAL CONSULTANTS :

JA

PROJECT :

ANKURA HOMES_THE WOODS
AT KEESARAGUTTA

MEP CONSULTANTS :

JA

GOOD FOR CONSTRUCTION

DRAWING TITLE:

1625_EAST VILLA-PLOT 30
BLOCK WORK DETAILS

| | | | |
|---|---|---|---|
| ARCHITECT : | HARISH | APPROVED : | HARISH |
| SCALE : | NTS | DRAWN : | DHARANI |
| DATE : | 03-11-2026 | CHECKED : | SHANMUKHI |

DRAWING NO : | REV.NO: R1