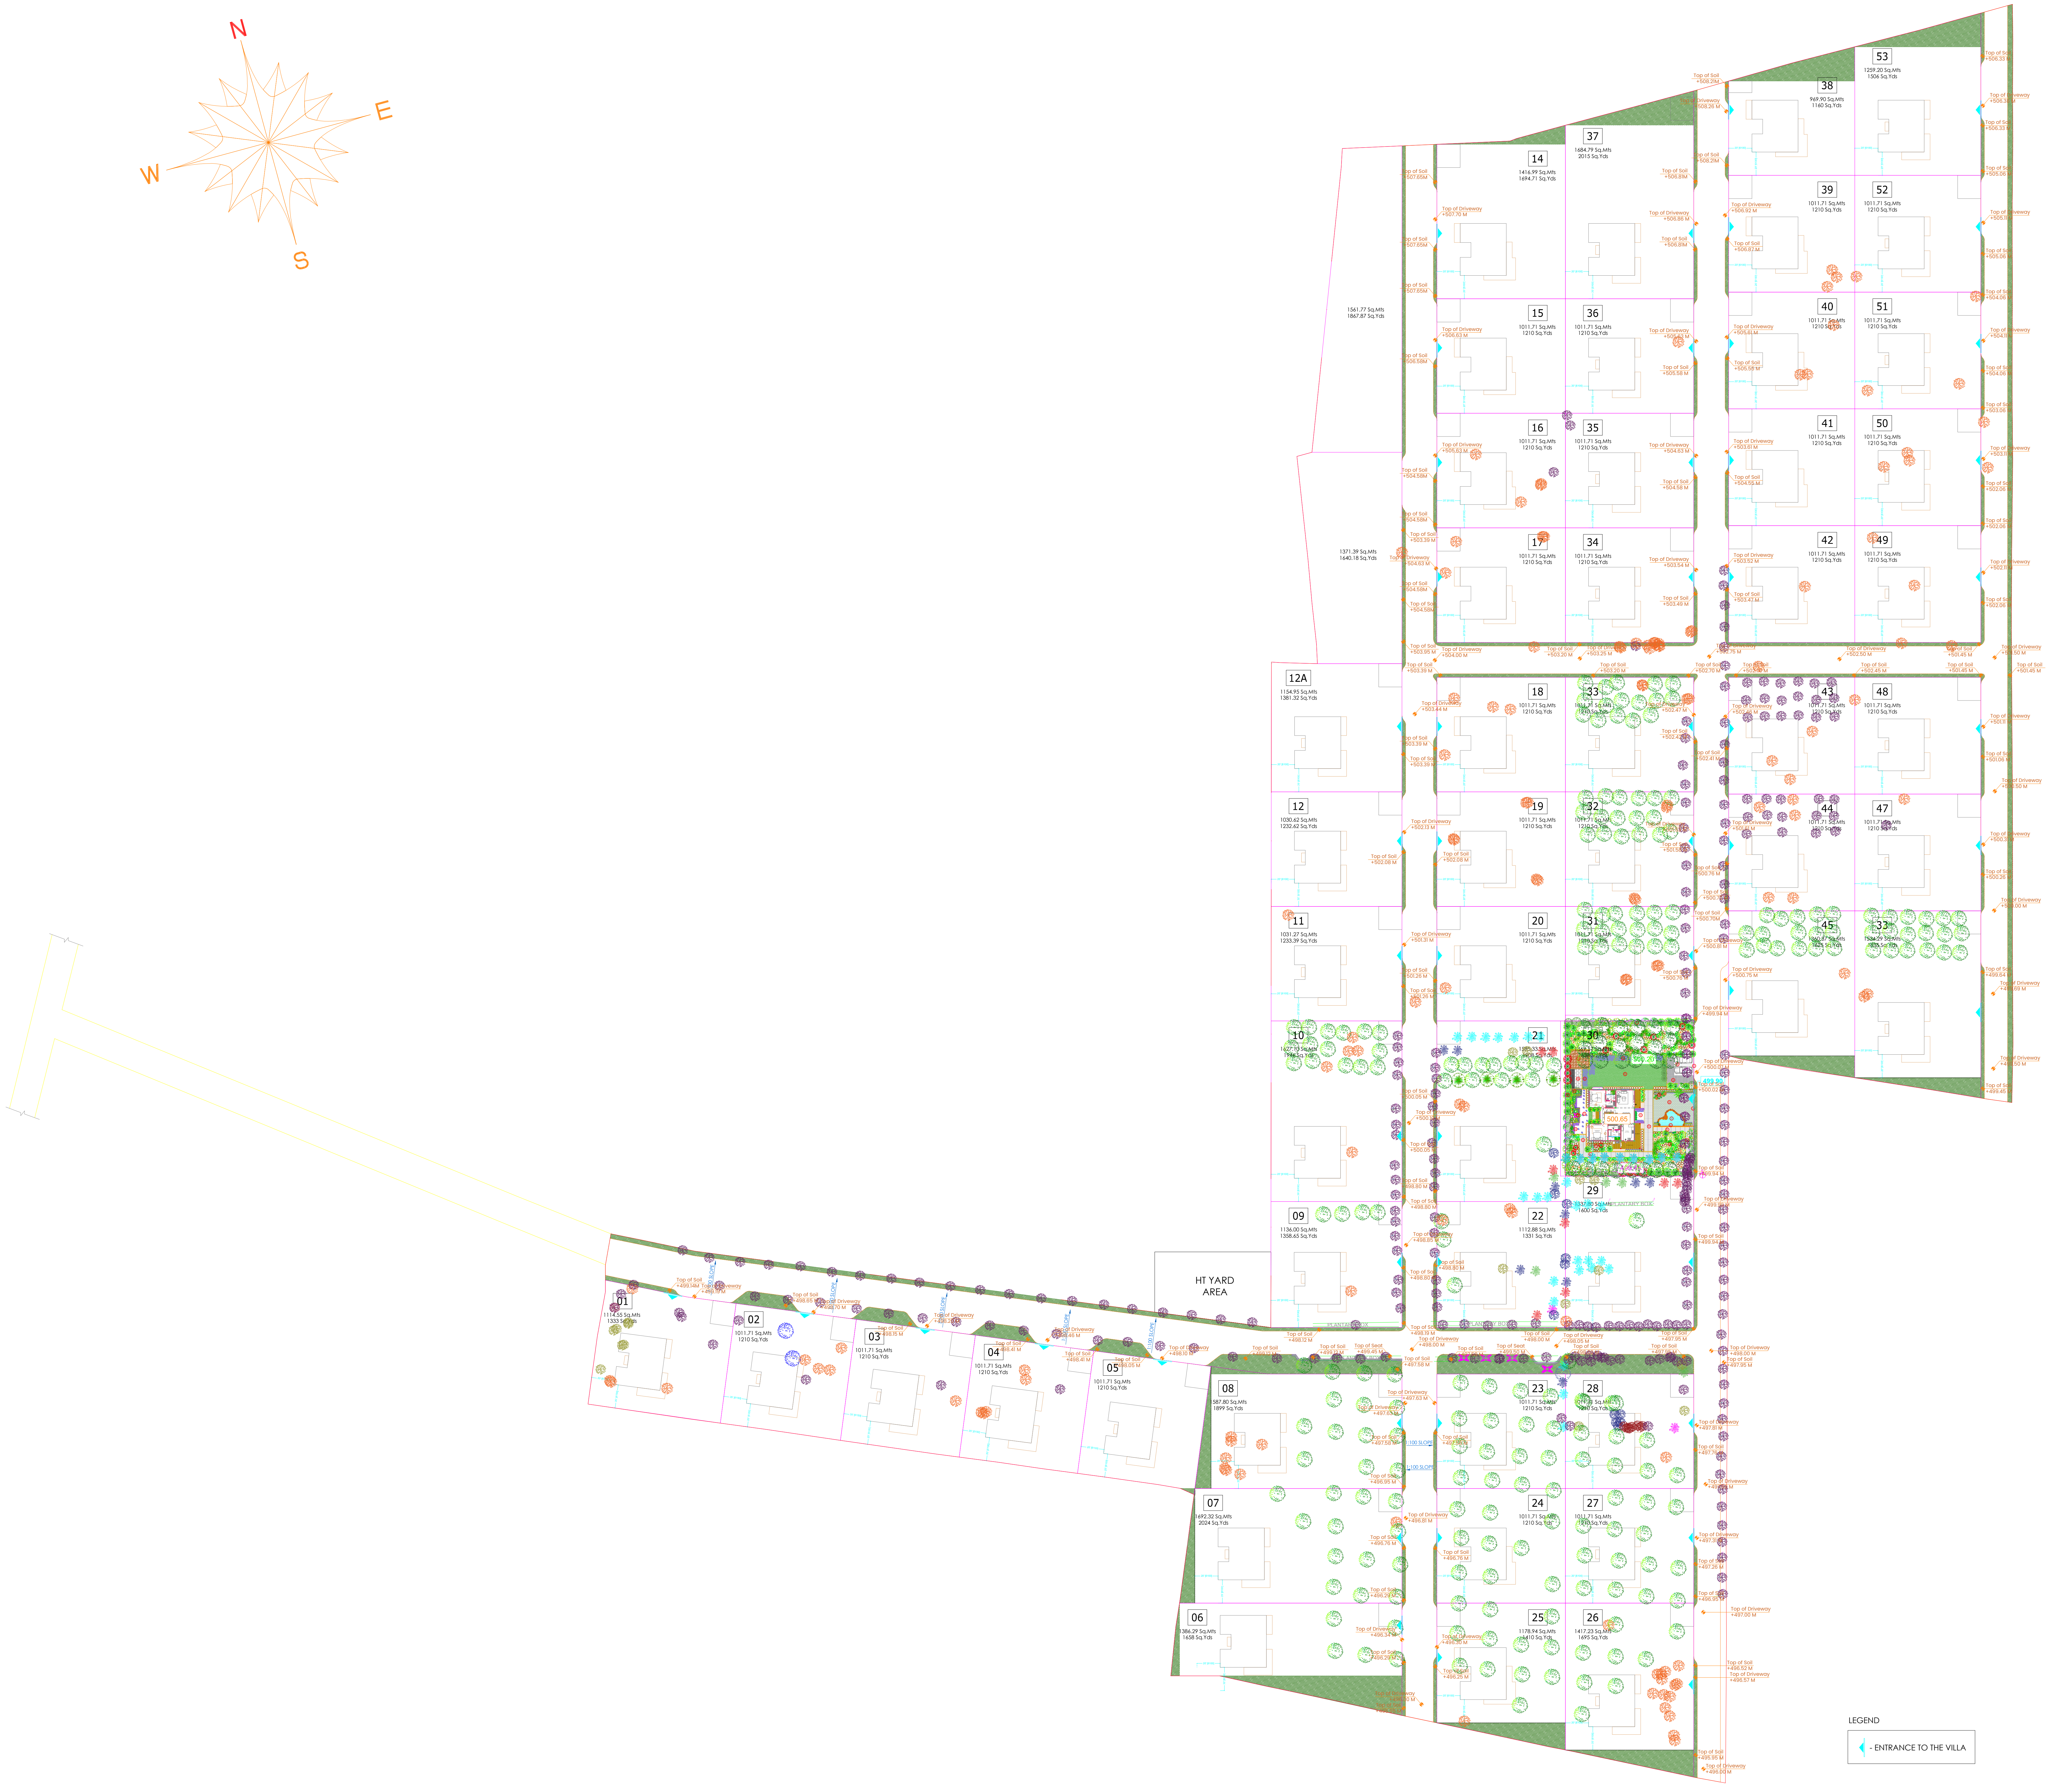
N
E
S
W
53
38
37
14
39
52
15
36
40
51
16
35
41
50
17
34
42
49
12A
18
33
43
48
12
19
32
44
47
11
20
31
45
46
10
21
30
29
09
22
HT YARD AREA
01
02
03
04
05
08
23
28
07
24
27
06
25
26

LEGEND

- ENTRANCE TO THE VILLA

Landscape Architects
Mob: +91 90309 62233 , +91 95151 03063
contact@lumiscapeslandscapes.in

NOTES

1. THIS DRAWING SHOULD BE READ AND NOT MEASURED.
2. ALL DIMENSIONS ARE IN MILLIMETERS AND LEVELS ARE IN METERS UNLESS STATED OTHERWISE.
3. ALL DRAWINGS MUST BE CROSS REFERENCE IN CASE OF ANY DOUBT / DISCREPANCY.
4. TOC REPRESENTS TOP OF CONCRETE & FFL REPRESENTS FINISHED FLOOR LEVELS. ALL DIMENSIONS SHOWN IN THE DRAWINGS ARE STRUCTURAL / MASONRY DIMENSIONS.
5. ALL ARCHITECTURAL DRAWINGS MUST BE REFERRED IN COORDINATION WITH STRUCTURAL DRAWINGS.
6. ALL SPECIALIST WORKS DETAILS AND ANY DEVIATIONS FROM THIS CONSTRUCTION DRAWINGS, THE CONTRACTOR / SUB-CONTRACTOR ARE TO PROVIDE SHOP DRAWINGS FOR ARCHITECT'S / ENGINEER'S APPROVAL PRIOR TO CONSTRUCTION.

KEY PLAN

DRAWING STAGE

FOR INFORMATION &APPROVAL

GFC STAMP

CLIENT

M/S. ANKURA HOMES

LEGEND

NOTE : ALL THE DIMENSIONS ARE IN FEET

ARCHITECTS

MEP CONSULTANTS

STRUCTURAL CONSULTANTS

PROJECT TITLE
"THE WOODS" BY ANKURA HOMES @BOMMALARAMARAM

DRAWING TITLE
LEVEL INDICATION PLAN

NORTH

N

LA ARCHITECT	YASASWINI & CHARITA	REV.	DATE
DWG NO :	LLA-TW-LC-01		
CHECKED BY :	CHARITA.M		
DRAWN BY :	P.VAMSI		
DATE :	22 -10 - 2026		
SCALE :	NTS	SHEET - A2	