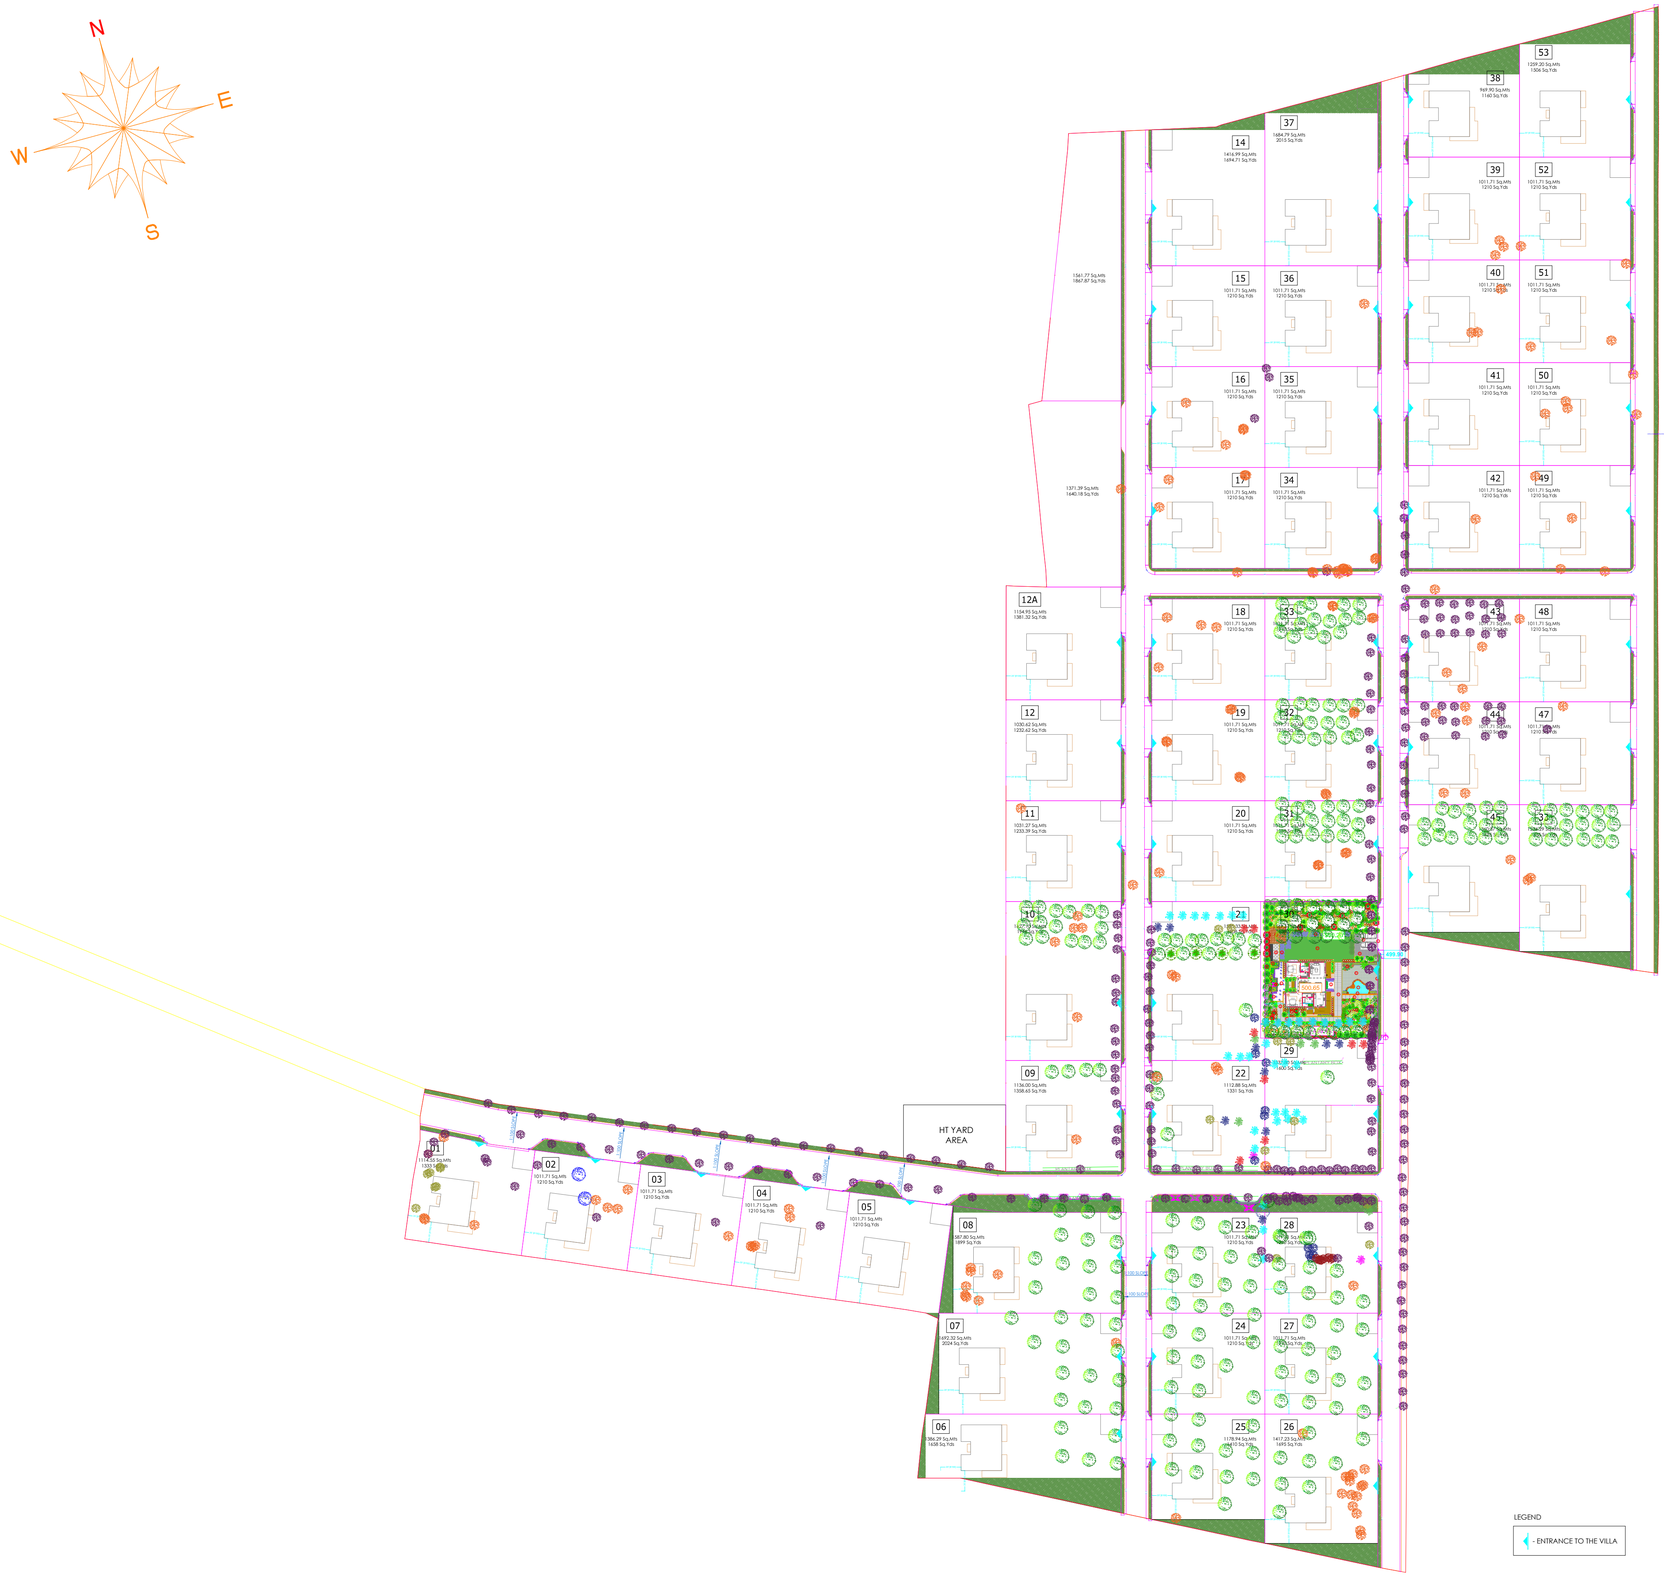


Landscape Architects Mob: +91 90309 62233 , +91 9515 03063 contact@ultrascapesandarchscapes.in	NOTES 1. THIS DRAWING SHOULD BE READ AND NOT MEASURED. 2. ALL DIMENSIONS ARE IN MILLIMETERS AND LEVELS ARE IN METERS UNLESS STATED OTHERWISE. 3. ALL DETAILS SHOWN ON ONE DRAWING OR CROSS REFERENCE IN CASE OF ANY DOUBT / DISCREPANCY. 4. TOC REPRESENTS TOP OF CONCRETE & FFL REPRESENTS FINISHED FLOOR LEVELS. ALL DIMENSIONS SHOWN IN THE DRAWINGS ARE STRUCTURAL / MASONRY DIMENSIONS. 5. ALL DRAWINGS SHALL BE CONSIDERED TO BE REFERRED IN COORDINATION WITH STRUCTURAL DRAWINGS. 6. ALL SPECIALIST WORKS DETAILS AND ANY DEVIATIONS FROM THIS CONSTRUCTION DRAWINGS, THE CONTRACTOR / SUB-CONTRACTOR SHALL OBTAIN THE APPROVAL FROM THE ARCHITECTS / ENGINEERS APPROVAL PRIOR TO CONSTRUCTION.	KEY PLAN	DRAWING STAGE **FOR INFORMATION &APPROVAL**	GFC STAMP	CLIENT **M/S. ANKURA HOMES**	LEGEND **NOTE : ALL THE DIMENSIONS ARE IN FEET**	ARCHITECTS also. design	MEP CONSULTANTS	STRUCTURAL CONSULTANTS	PROJECT TITLE "THE WOODS" BY ANKURA HOMES @BOMMALARAMARAM DRAWING TITLE LANDSCAPE MARKING PLAN	NORTH N	LA ARCHITECT : YASASWINI & CHARITA DWG NO : LLA-TW-LC-01 CHECKED BY : CHARITA.M DRAWN BY : P.VAMSI DATE : 22 -10 - 2026 SCALE : NTS	REV. / DATE SHEET – A2