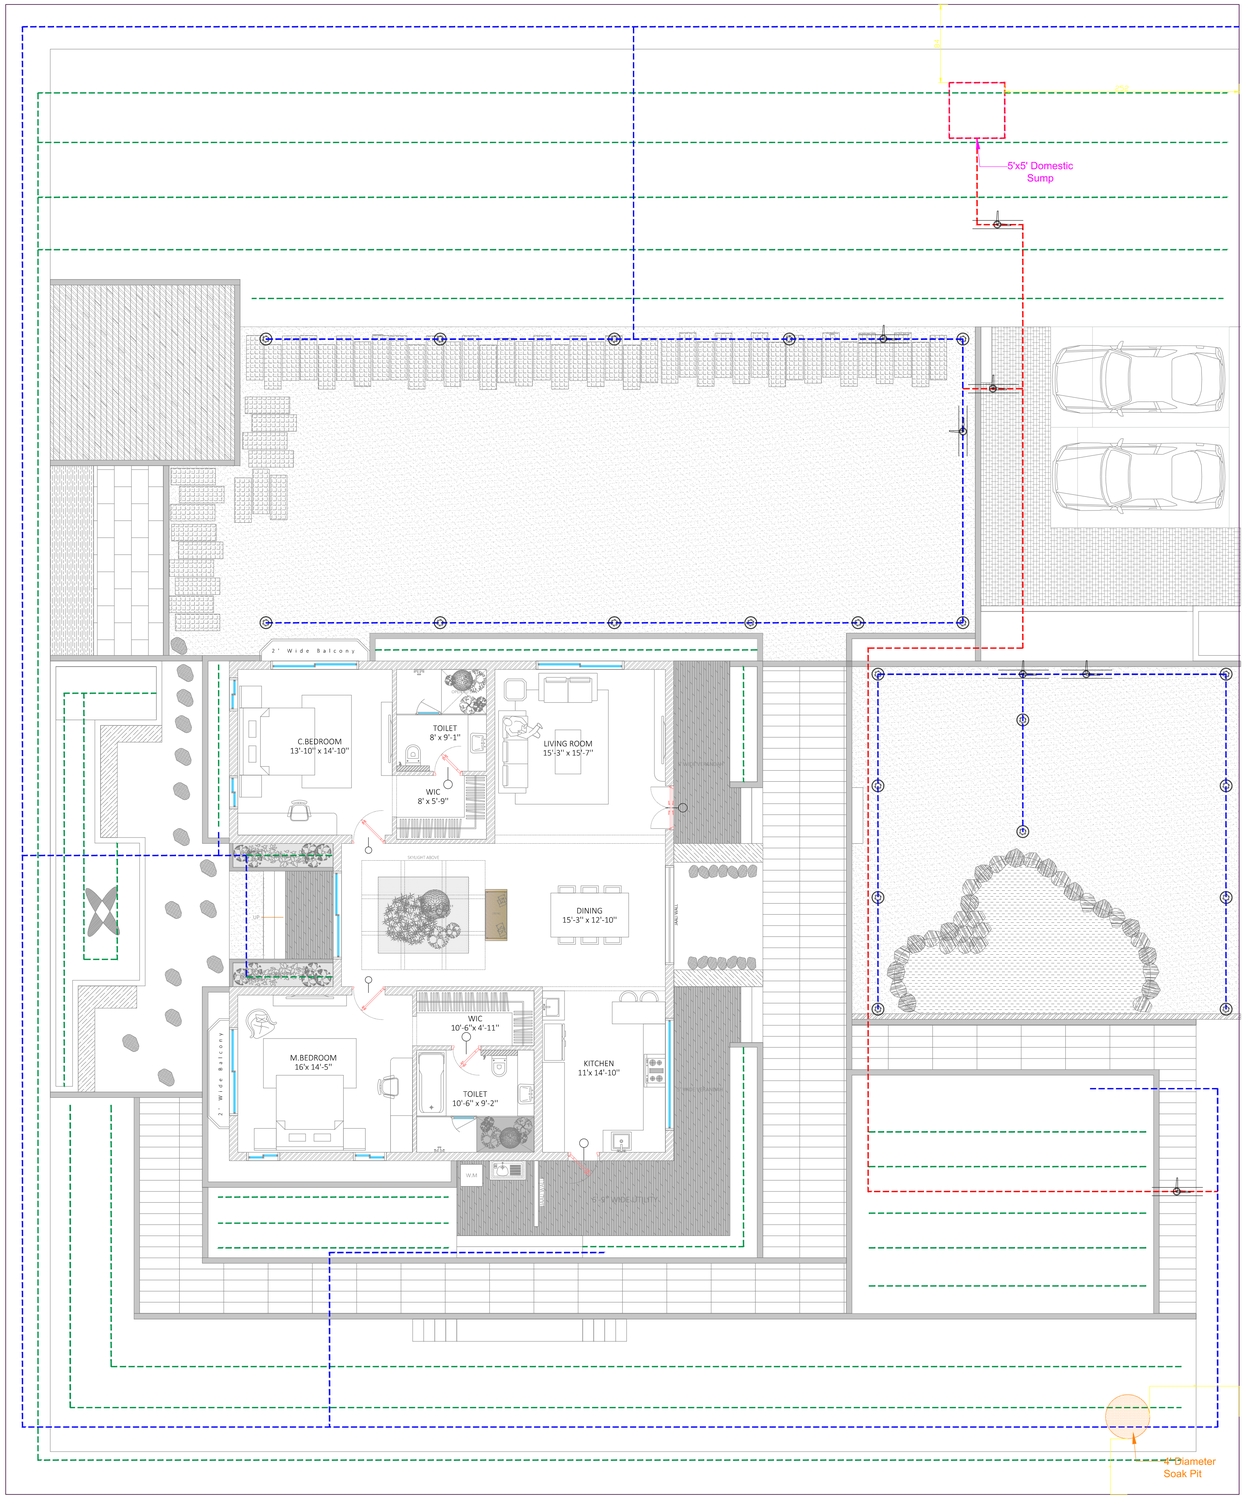


LEGEND:

S.NO	SYMBOL	SPECIFICATION
1.		VALVE'S
2.		50 MM PVC PIPE
3.		63 MM PVC PIPE(MAIN)
4.		SPINKLER'S
5.		DRIP PIPE

LUMINSCAPES
Landscape Associates
Mob: +91 90309 62233 , +91 95151 03063
contact@luminscapeslandscapes.in

NOTES
1. THIS DRAWING SHOULD BE READ AND NOT MEASURED.
2. ALL DIMENSIONS ARE IN MILLIMETERS AND LEVELS ARE IN METERS UNLESS STATED OTHERWISE.
3. ALL DRAWINGS MUST BE CROSS REFERENCE IN CASE OF ANY DOUBT / DISCREPANCY.
4. TOC REPRESENTS TOP OF CONCRETE & FFL REPRESENTS FINISHED FLOOR LEVELS. ALL DIMENSIONS SHOWN IN THE DRAWINGS ARE STRUCTURAL / MASONRY DIMENSIONS.
5. ALL ARCHITECTURAL DRAWINGS MUST BE REFERRED IN COORDINATION WITH STRUCTURAL DRAWINGS.
6. ALL SPECIALIST WORKS DETAILS AND ANY DEVIATIONS FROM THIS CONSTRUCTION DRAWINGS, THE CONTRACTOR / SUB-CONTRACTOR ARE TO PROVIDE SHOP DRAWINGS FOR ARCHITECTS / ENGINEER'S APPROVAL PRIOR TO CONSTRUCTION.

KEY PLAN

DRAWING STAGE: **FOR INFORMATION & APPROVAL**

GFC STAMP

CLIENT: **M/S. ANKURA HOMES**

LEGEND: **NOTE : ALL THE DIMENSIONS ARE IN FEET**

ARCHITECTS: also. design

MEP CONSULTANTS

STRUCTURAL CONSULTANTS

PROJECT TITLE: "THE WOODS" BY ANKURA HOMES @BOMMALARAMARAM

DRAWING TITLE: IRRIGATION

NORTH

LA ARCHITECT	YASASWINI & CHARITA	REV.	DATE
DWG NO :	LLA-TW-IR-01		
CHECKED BY :	CHARITA.M		
DRAWN BY :	VAMSI.P		
DATE :	13-10-2026		
SCALE :	NTS	SHEET – A1	