
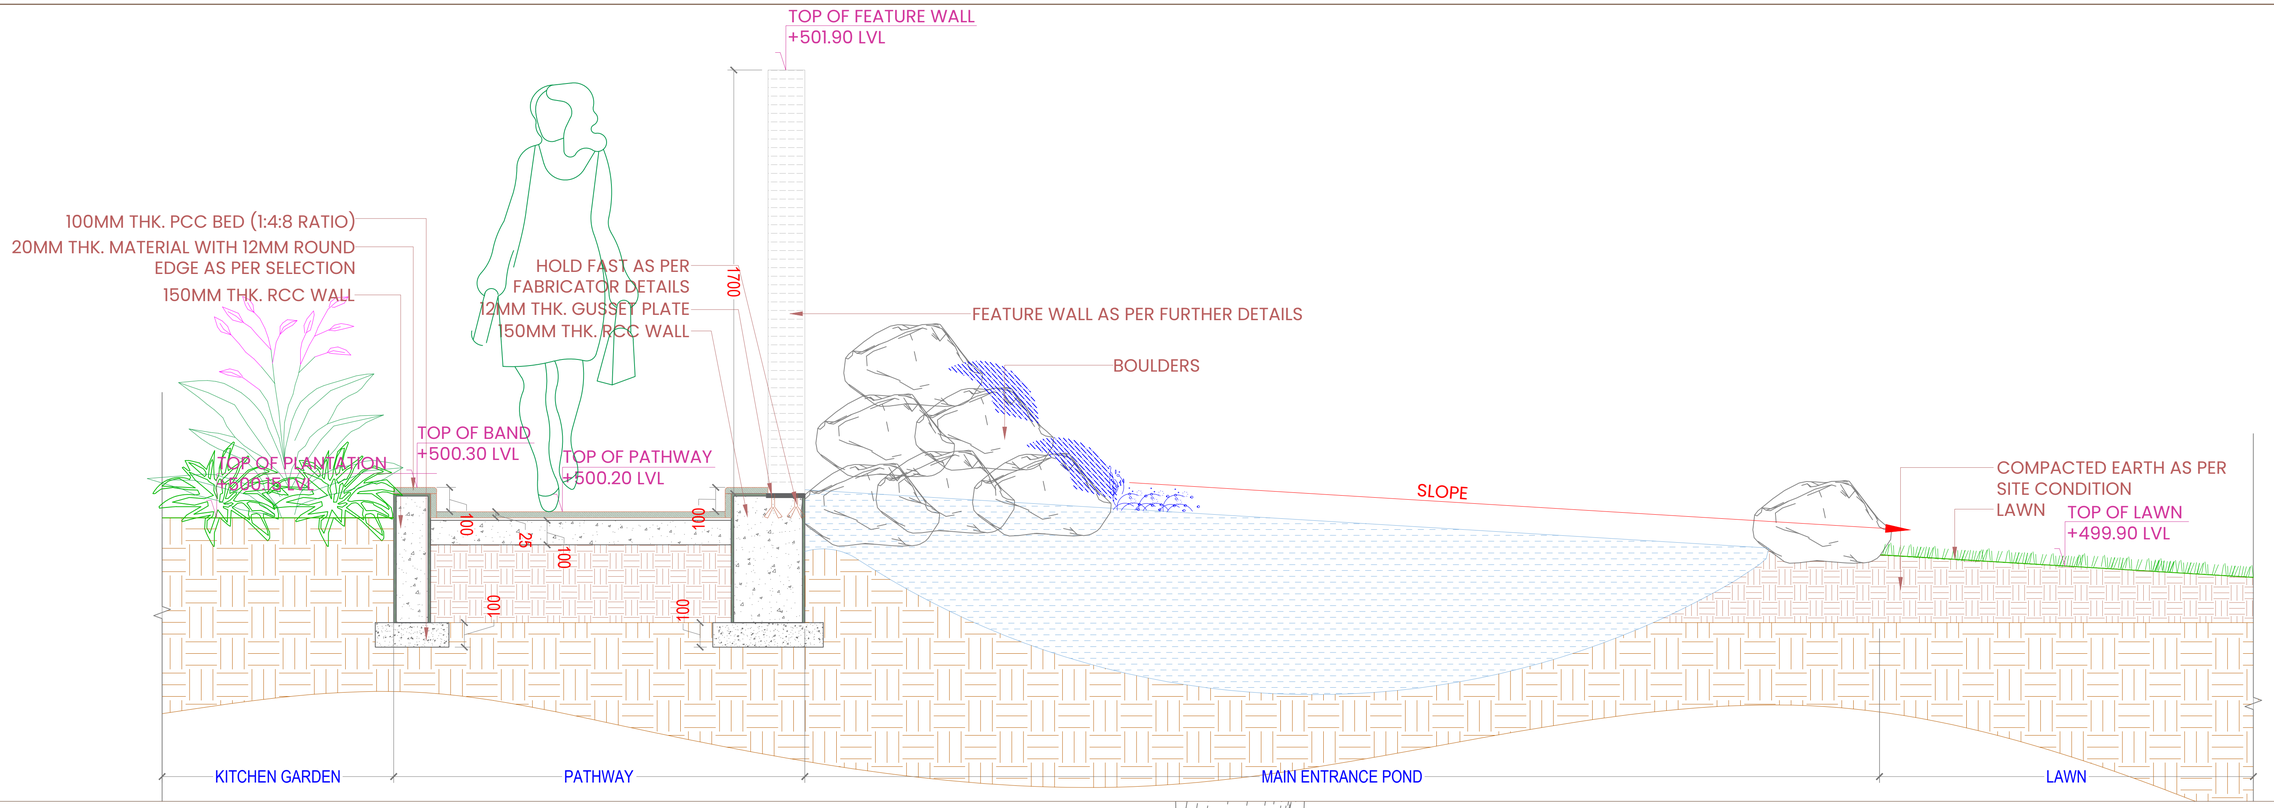


SECTION AA'

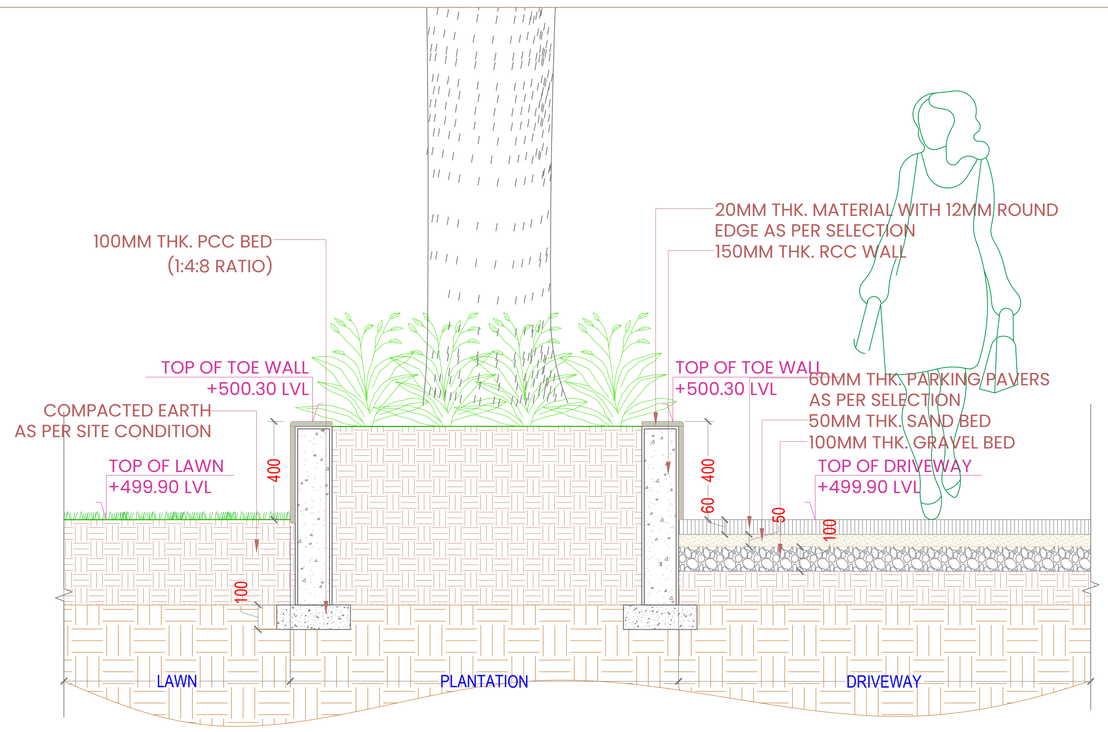

SECTION BB'

LUMSCAPES
Landscape Architects
Mob: +91 90309 62233 , +91 95151 03063
contact@lumiscapeslandscapes.in

NOTES
1. THIS DRAWING SHOULD BE READ AND NOT MEASURED.
2. ALL DIMENSIONS ARE IN MILLIMETERS AND LEVELS ARE IN METERS UNLESS STATED OTHERWISE.
3. ALL DRAWINGS MUST BE CROSS REFERENCE IN CASE OF ANY DOUBT / DISCREPANCY.
4. TOC REPRESENTS TOP OF CONCRETE & FFL REPRESENTS FINISHED FLOOR LEVELS. ALL DIMENSIONS SHOWN IN THE DRAWINGS ARE STRUCTURAL / MASONRY DIMENSIONS.
5. ALL ARCHITECTURAL DRAWINGS MUST BE REFERRED IN COORDINATION WITH STRUCTURAL DRAWINGS.
6. ALL SPECIALIST WORKS DETAILS AND ANY DEVIATIONS FROM THIS CONSTRUCTION DRAWINGS, THE CONTRACTOR / SUB-CONTRACTOR ARE TO PROVIDE SHOP DRAWINGS FOR ARCHITECTS / ENGINEER'S APPROVAL PRIOR TO CONSTRUCTION.

KEY PLAN

LEGEND
NOTE : ALL THE DIMENSIONS ARE IN MM

DRAWING STAGE
INFORMATION & APPROVAL

GFC STAMP

CLIENT
MR. ABHISHEK & ASHISH

ARCHITECTS
alia design

PROJECT TITLE
"THE WOODS" BY ANKURA HOMES @BOMMALARAMARAM

DRAWING TITLE
LANDSCAPE SECTIONAL DETAILS

NORTH
N

LUMSCAPES PROJECT REFERENCE NO :		REV.	DATE
DWG NO :	LLA-TW-LS-001.1		
CHECKED BY :	YASASWINI . K		
DRAWN BY :	VAMSI . P		
DATE :	13-10-2026		
SCALE :	NTS	SHEET - A1	