
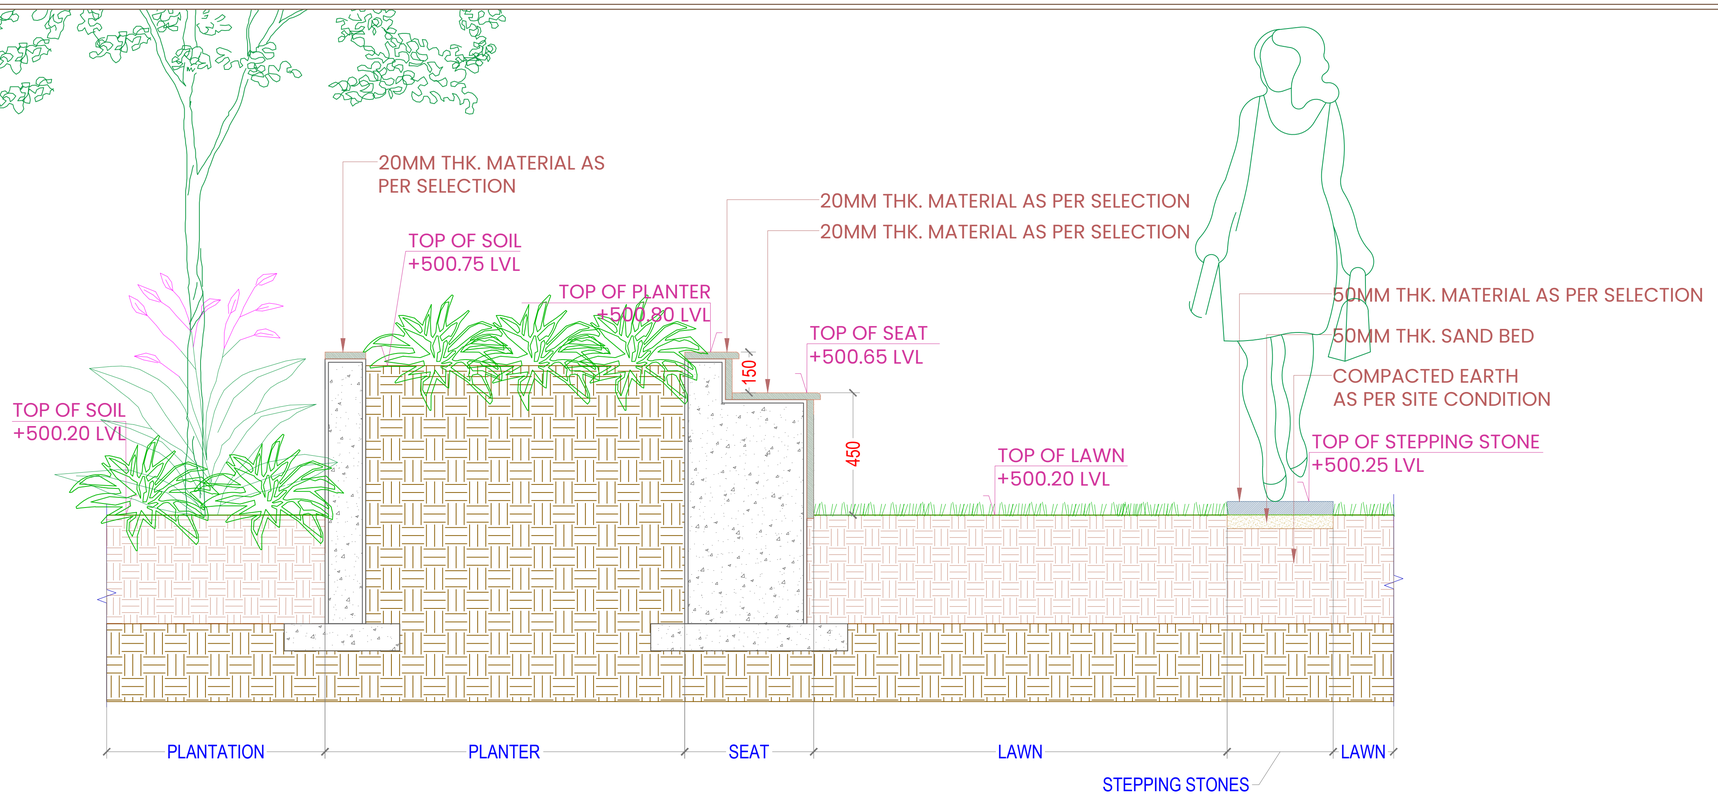


SECTION EE'

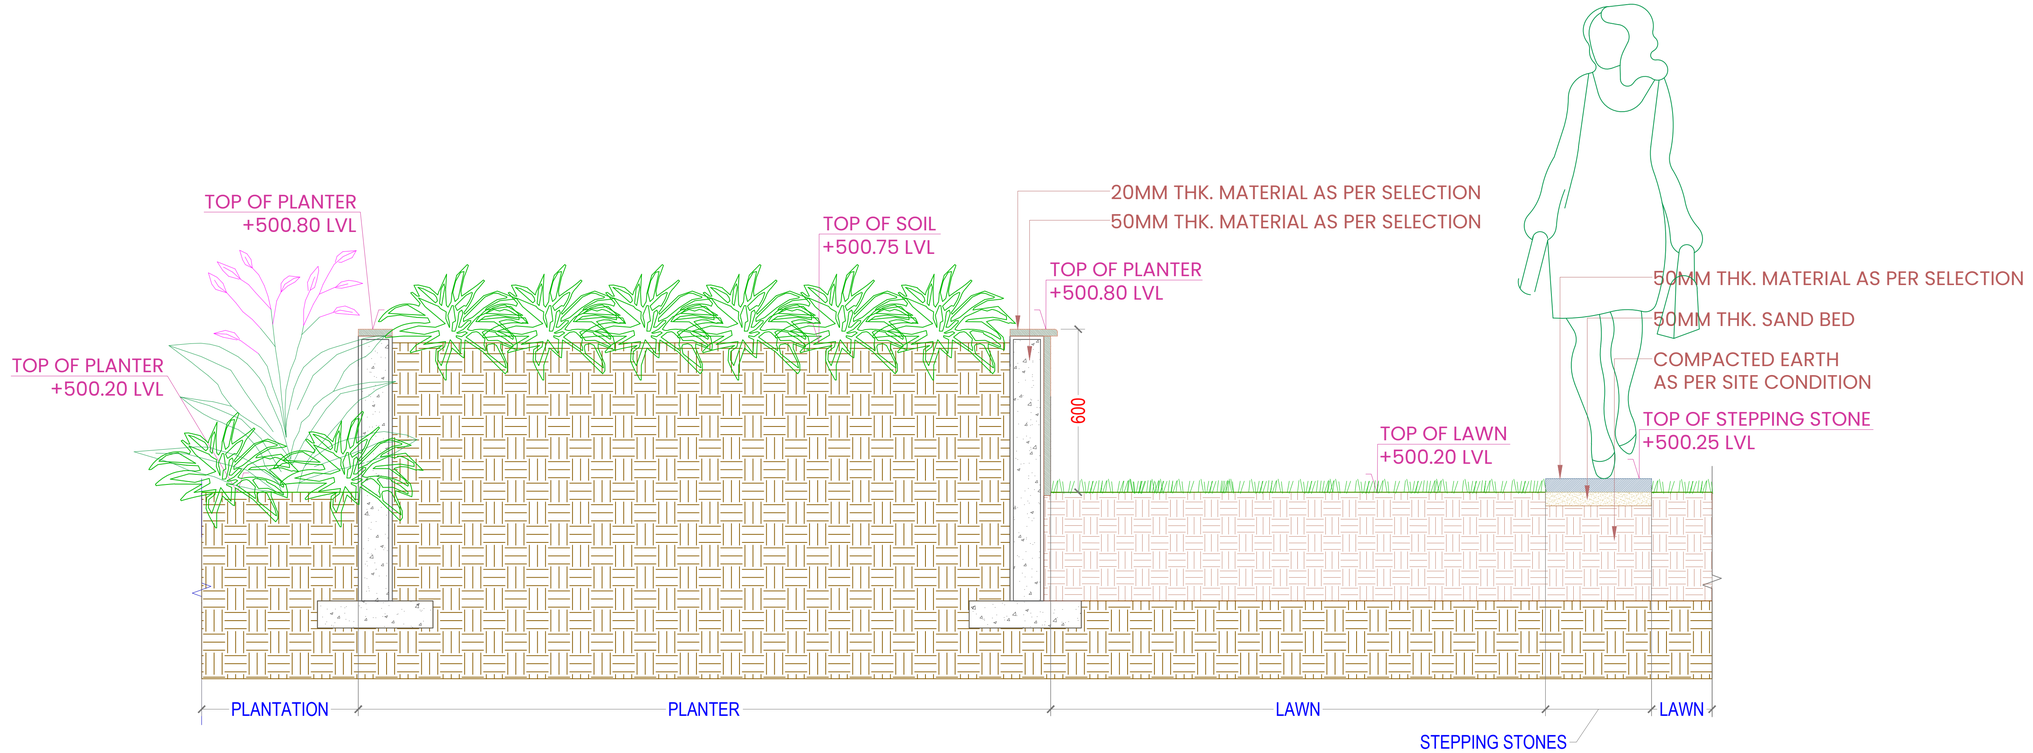

SECTION FF'

LUMISCAPES
Landscape Architects
Mob: +91 90309 62233 , +91 95151 03063
contact@lumiscapeslandscapes.in

NOTES

1. THIS DRAWING SHOULD BE READ AND NOT MEASURED.
2. ALL DIMENSIONS ARE IN MILLIMETERS AND LEVELS ARE IN METERS UNLESS STATED OTHERWISE.
3. ALL DRAWINGS MUST BE CROSS REFERENCE IN CASE OF ANY DOUBT / DISCREPANCY.
4. TOC REPRESENTS TOP OF CONCRETE & FFL REPRESENTS FINISHED FLOOR LEVEL). ALL DIMENSIONS SHOWN IN THE DRAWINGS ARE FINISHED DIMENSIONS UNLESS OTHERWISE.
5. ALL ARCHITECTURAL DRAWINGS MUST BE REFERRED IN COORDINATION WITH STRUCTURAL DRAWINGS.
6. ALL SPECIALIST WORKS DETAILS AND ANY DEVIATIONS FROM THIS CONSTRUCTION DRAWINGS, THE CONTRACTOR / SUB-CONTRACTOR ARE TO PROVIDE SHOP DRAWINGS FOR ARCHITECTS / ENGINEER'S APPROVAL PRIOR TO CONSTRUCTION.

KEY PLAN

LEGEND

NOTE : ALL THE DIMENSIONS ARE IN MM

DRAWING STAGE

INFORMATION & APPROVAL

GFC STAMP

CLIENT

MR. ABHISHEK & ASHISH

ARCHITECTS

PROJECT TITLE

"THE WOODS" BY ANKURA HOMES @BOMMALARAMARAM

DRAWING TITLE

LANDSCAPE SECTIONAL DETAILS

NORTH

N

LUMISCAPES PROJECT REFERENCE NO :		REV.	DATE
DWG NO :	LLA-TW-LS-001.3		
CHECKED BY :	YASASWINI . K		
DRAWN BY :	VAMSI . P		
DATE :	13-10-2026		
SCALE :	NTS	SHEET - A1	