

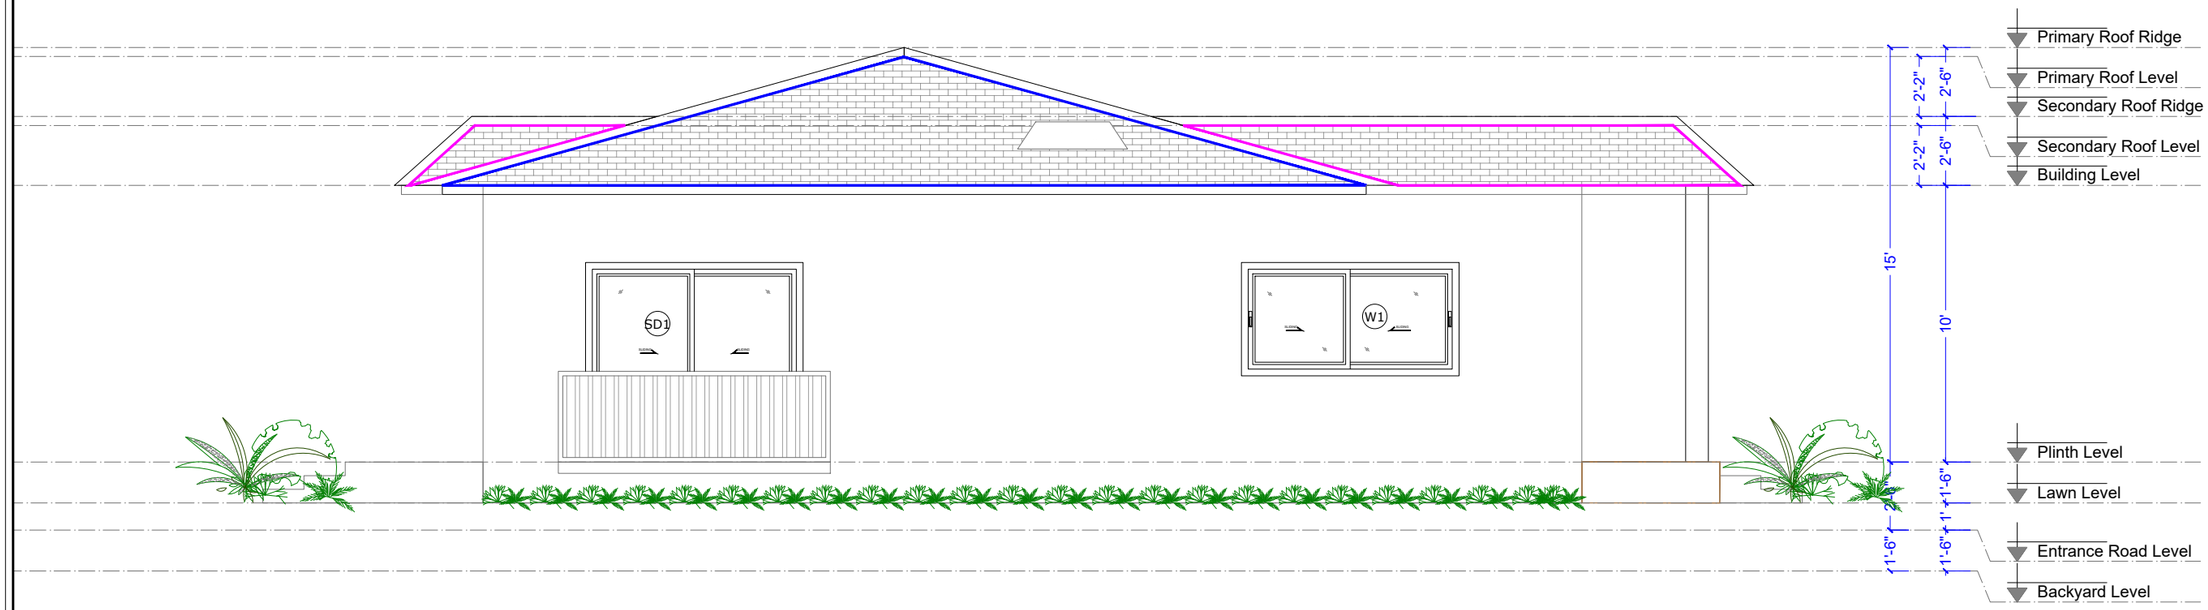


WEST VILLA NORTH ELEVATION

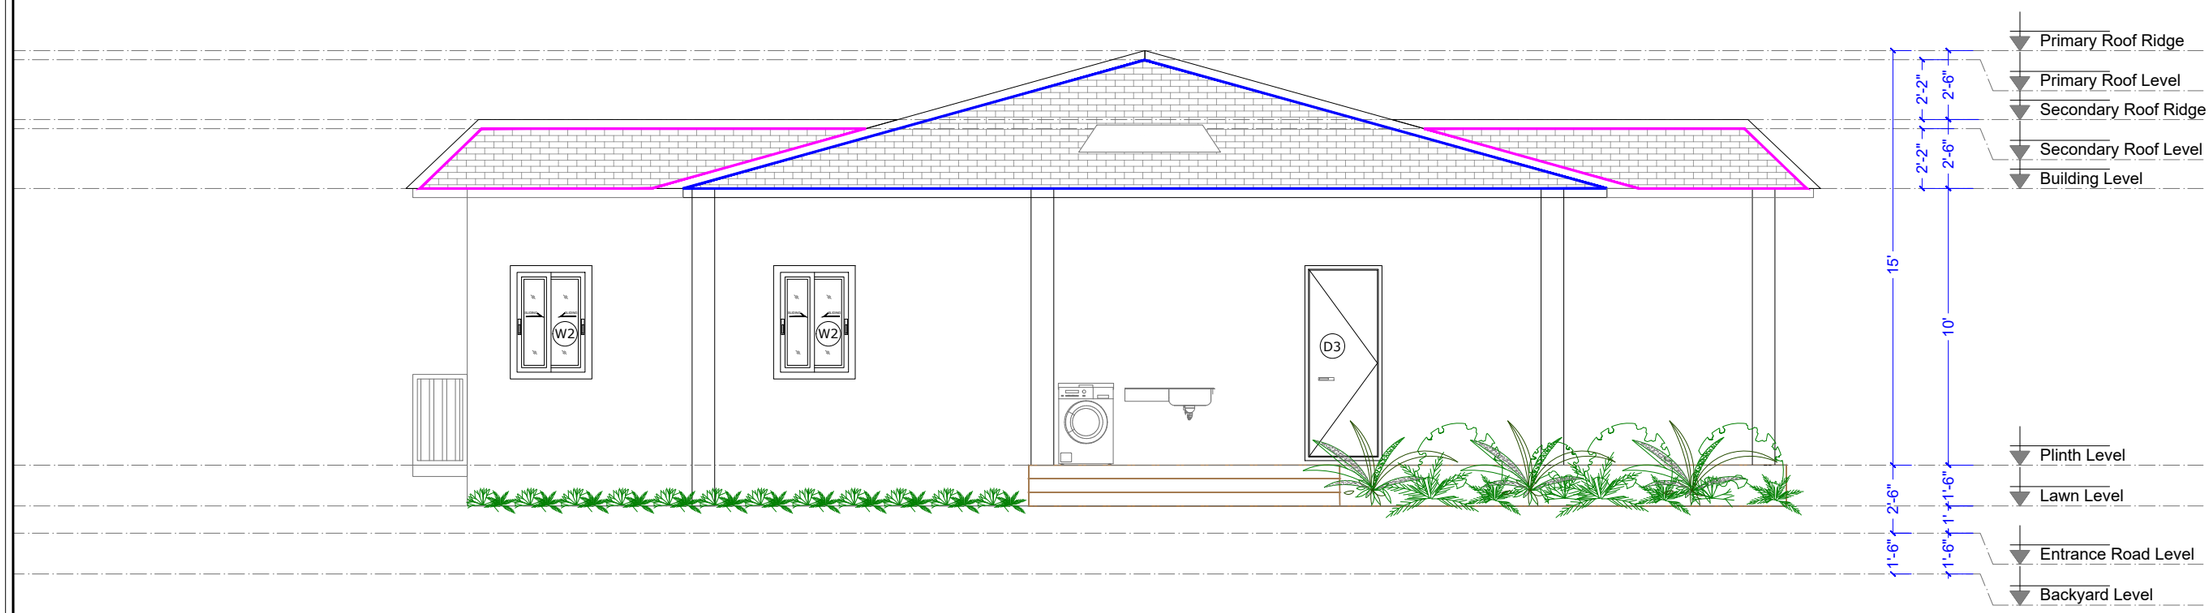

WEST VILLA SOUTH ELEVATION

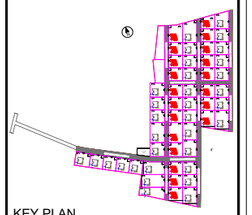


KEY PLAN

LEGEND:

- PRIMARY ROOF
- SECONDARY ROOF

NORTH ELEVATION

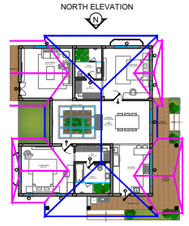

SOUTH ELEVATION

GENERAL NOTES:

- ALL DIMENSIONS ARE IN MILLIMETERS
- THIS DRAWING IS A COPYRIGHT AND PROPERTY OF THE ARCHITECT. IS NOT TO BE PRODUCED, COPIED, HANDED OVER TO THIRD PARTY OR USED FOR ANY OTHER PURPOSE OTHER THAN FOR WHICH IT IS INTENDED.
- ALL DIMENSIONS SHALL BE VERIFIED ON SITE PRIOR TO START OF WORK ANY DISCREPANCY SHALL BE BROUGHT TO THE NOTICE OF THE ARCHITECT.
- THE CONTRACTOR MUST CHECK ALL DIMENSIONS AND DETAILS AND BE RESPONSIBLE FOR THE SAME. ANY DISCREPANCY SHALL BE BROUGHT TO THE NOTICE OF THE ARCHITECT.
- THIS DRAWING IS TO BE READ AND NOT SCALED.
- THIS DRAWING SHALL BE READ IN CONJUNCTION WITH ALL RELEVANT ARCHITECTURAL, STRUCTURAL AND SERVICES DRAWINGS. ANY DISCREPANCY NOTICED SHALL BE BROUGHT TO THE ATTENTION OF THE CONSULTANTS AND RESOLVED AS SOON AS POSSIBLE BUT ALWAYS PRIOR TO

NO	DESCRIPTION	DATE	SIGN

ARCHITECTURAL CONSULTANT:

also. design

MEP CONSULTANT:

JA

STRUCTURAL CONSULTANT:

JA

PROJECT:

ANKURA HOMES_THE WOODS AT KEESARAGUTTA


GOOD FOR CONSTRUCTION

DRAWING TITLE: (1/2)


1625_WEST VILLA BUILDING ELEVATIONS

ARCHITECT : HARISH	APPROVED : HARISH
SCALE : NTS	DRAWN : DHARANI
DATE : 21-10-2026	CHECKED : SHANMUKHI


DRAWING NO: REV.NO:

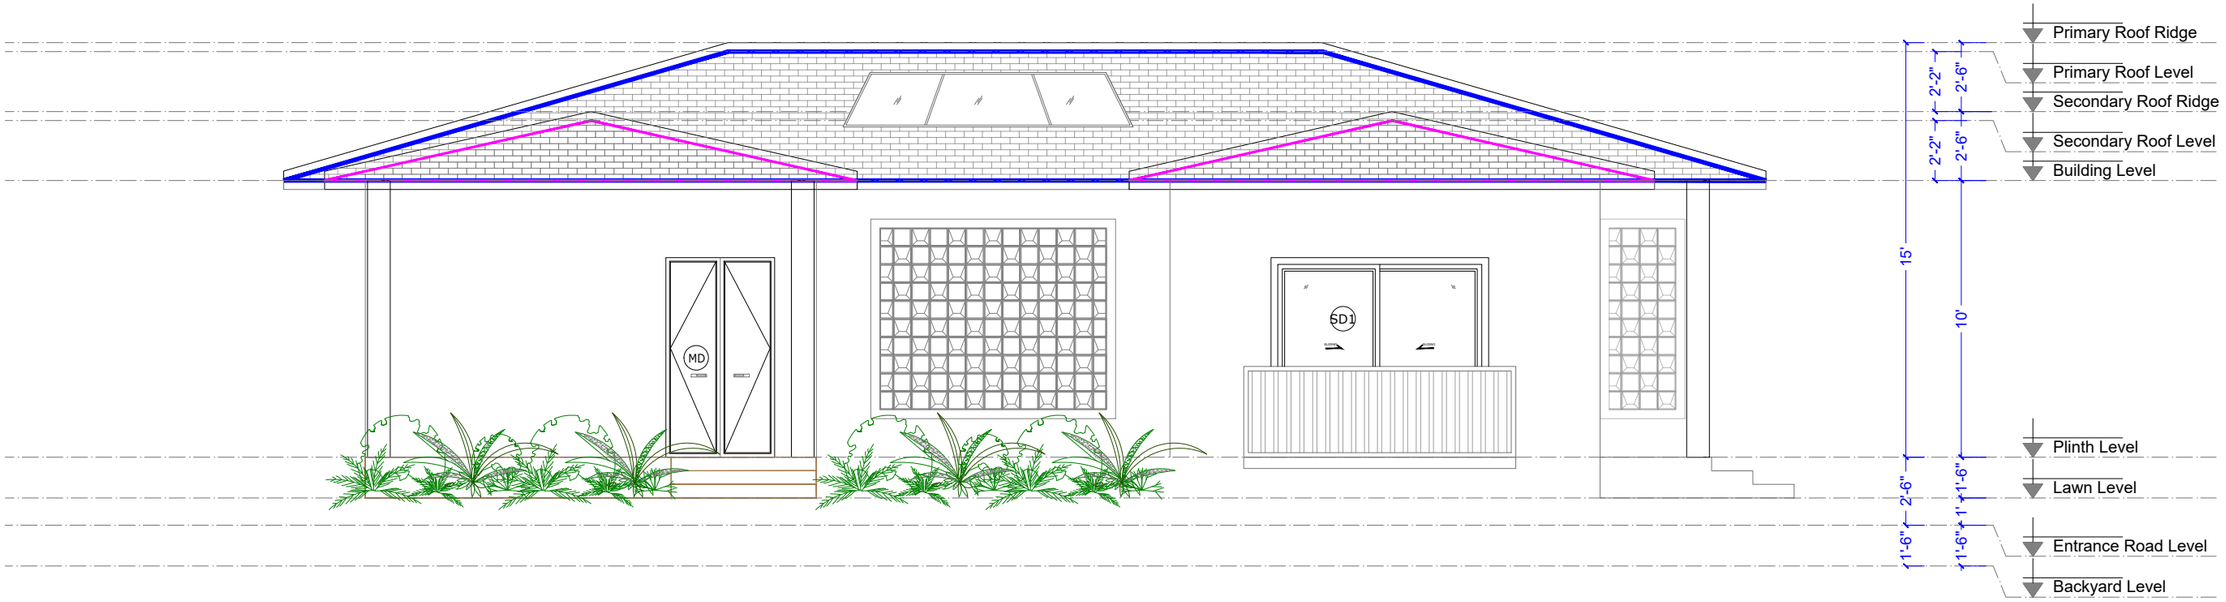

WEST VILLA WEST ELEVATION

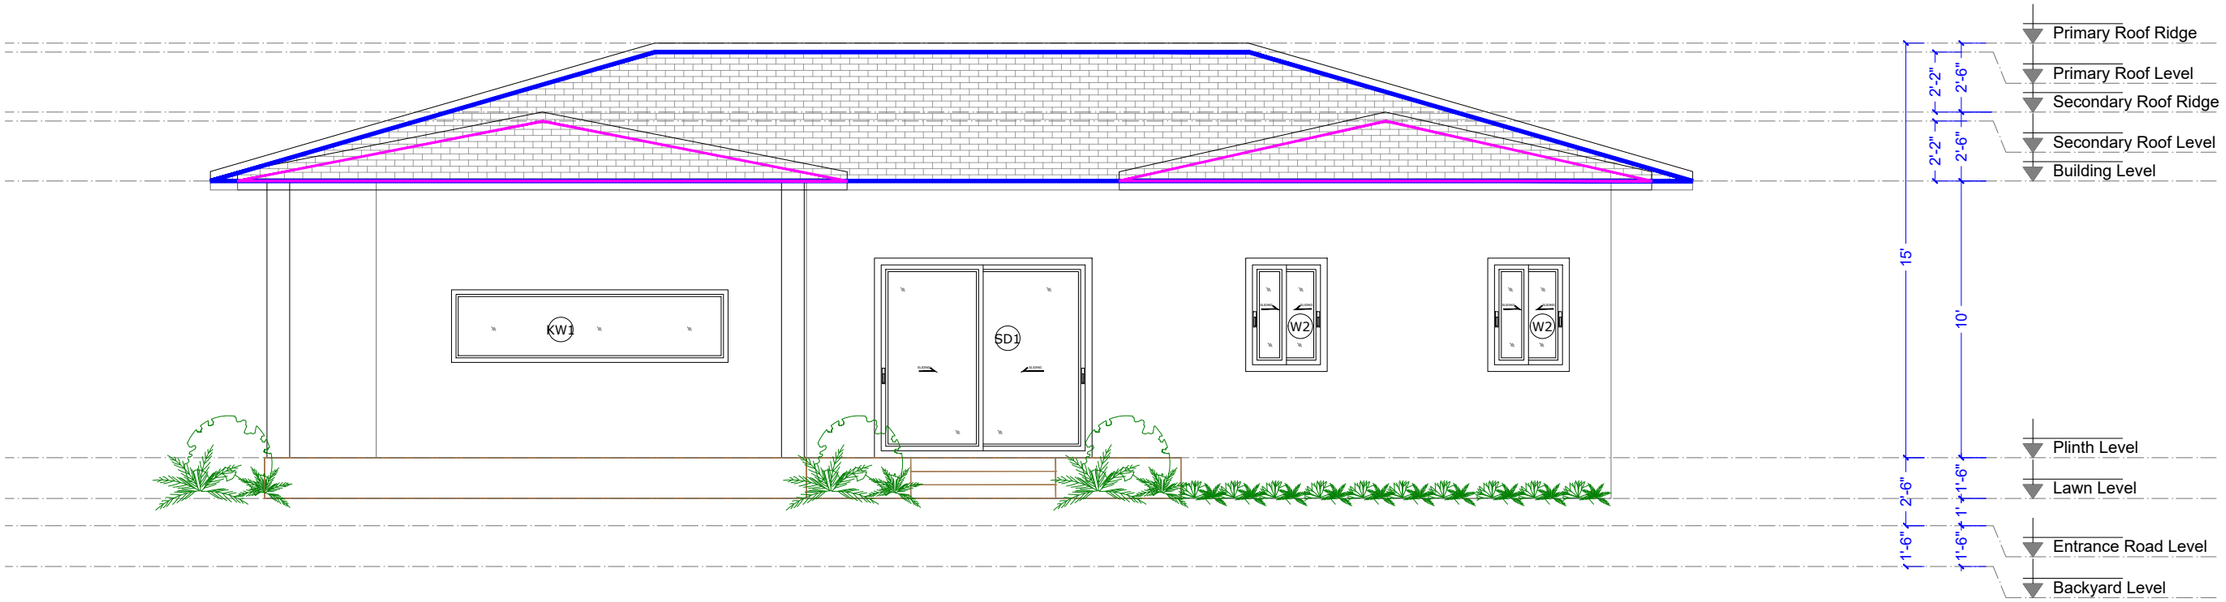


WEST VILLA EAST ELEVATION

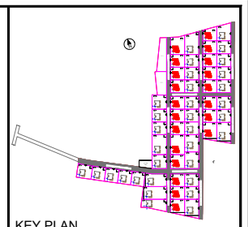

KEY PLAN

LEGEND:

- PRIMARY ROOF
- SECONDARY ROOF

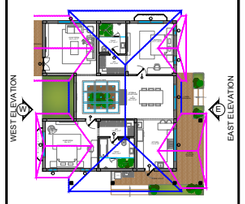

GENERAL NOTES:

- ALL DIMENSIONS ARE IN MILLIMETERS
- THIS DRAWING IS A COPYRIGHT AND PROPERTY OF THE ARCHITECT. IS NOT TO BE PRODUCED, COPIED, HANDED OVER TO THIRD PARTY OR USED FOR ANY OTHER PURPOSE OTHER THAN FOR WHICH IT IS INTENDED.
- ALL DIMENSIONS SHALL BE VERIFIED ON SITE PRIOR TO START OF WORK ANY DISCREPANCY SHALL BE BROUGHT TO THE NOTICE OF THE ARCHITECT.
- THE CONTRACTOR MUST CHECK ALL DIMENSIONS AND DETAILS AND BE RESPONSIBLE FOR THE SAME. ANY DISCREPANCY SHALL BE BROUGHT TO THE NOTICE OF THE ARCHITECT.
- THIS DRAWING IS TO BE READ AND NOT SCALED.
- THIS DRAWING SHALL BE READ IN CONJUNCTION WITH ALL RELEVANT ARCHITECTURAL, STRUCTURAL AND SERVICES DRAWINGS. ANY DISCREPANCY NOTICED SHALL BE BROUGHT TO THE ATTENTION OF THE CONSULTANTS AND RESOLVED AS SOON AS POSSIBLE BUT ALWAYS PRIOR TO

NO	DESCRIPTION	DATE	SIGN

ARCHITECTURAL CONSULTANT:

also. design

MEP CONSULTANT:

JA

STRUCTURAL CONSULTANT:

JA

PROJECT:

ANKURA HOMES_THE WOODS AT KEESARAGUTTA

GOOD FOR CONSTRUCTION

DRAWING TITLE: (2/2)

1625_WEST VILLA BUILDING ELEVATIONS

ARCHITECT : HARISH		APPROVED : HARISH	
SCALE : NTS		DRAWN : DHARANI	
DATE : 21-10-2026		CHECKED : SHANMUKHI	
DRAWING NO:		REV.NO:	