
- THIS DRAWING SHALL BE READ IN CONJUNCTION WITH ALL RELEVANT ARCHITECTURAL, STRUCTURAL AND SERVICES DRAWINGS. ANY DISCREPANCY NOTICED SHALL BE BROUGHT TO THE ATTENTION OF THE CONSULTANTS AND RESOLVED AS SOON AS POSSIBLE BUT ALWAYS PRIOR TO

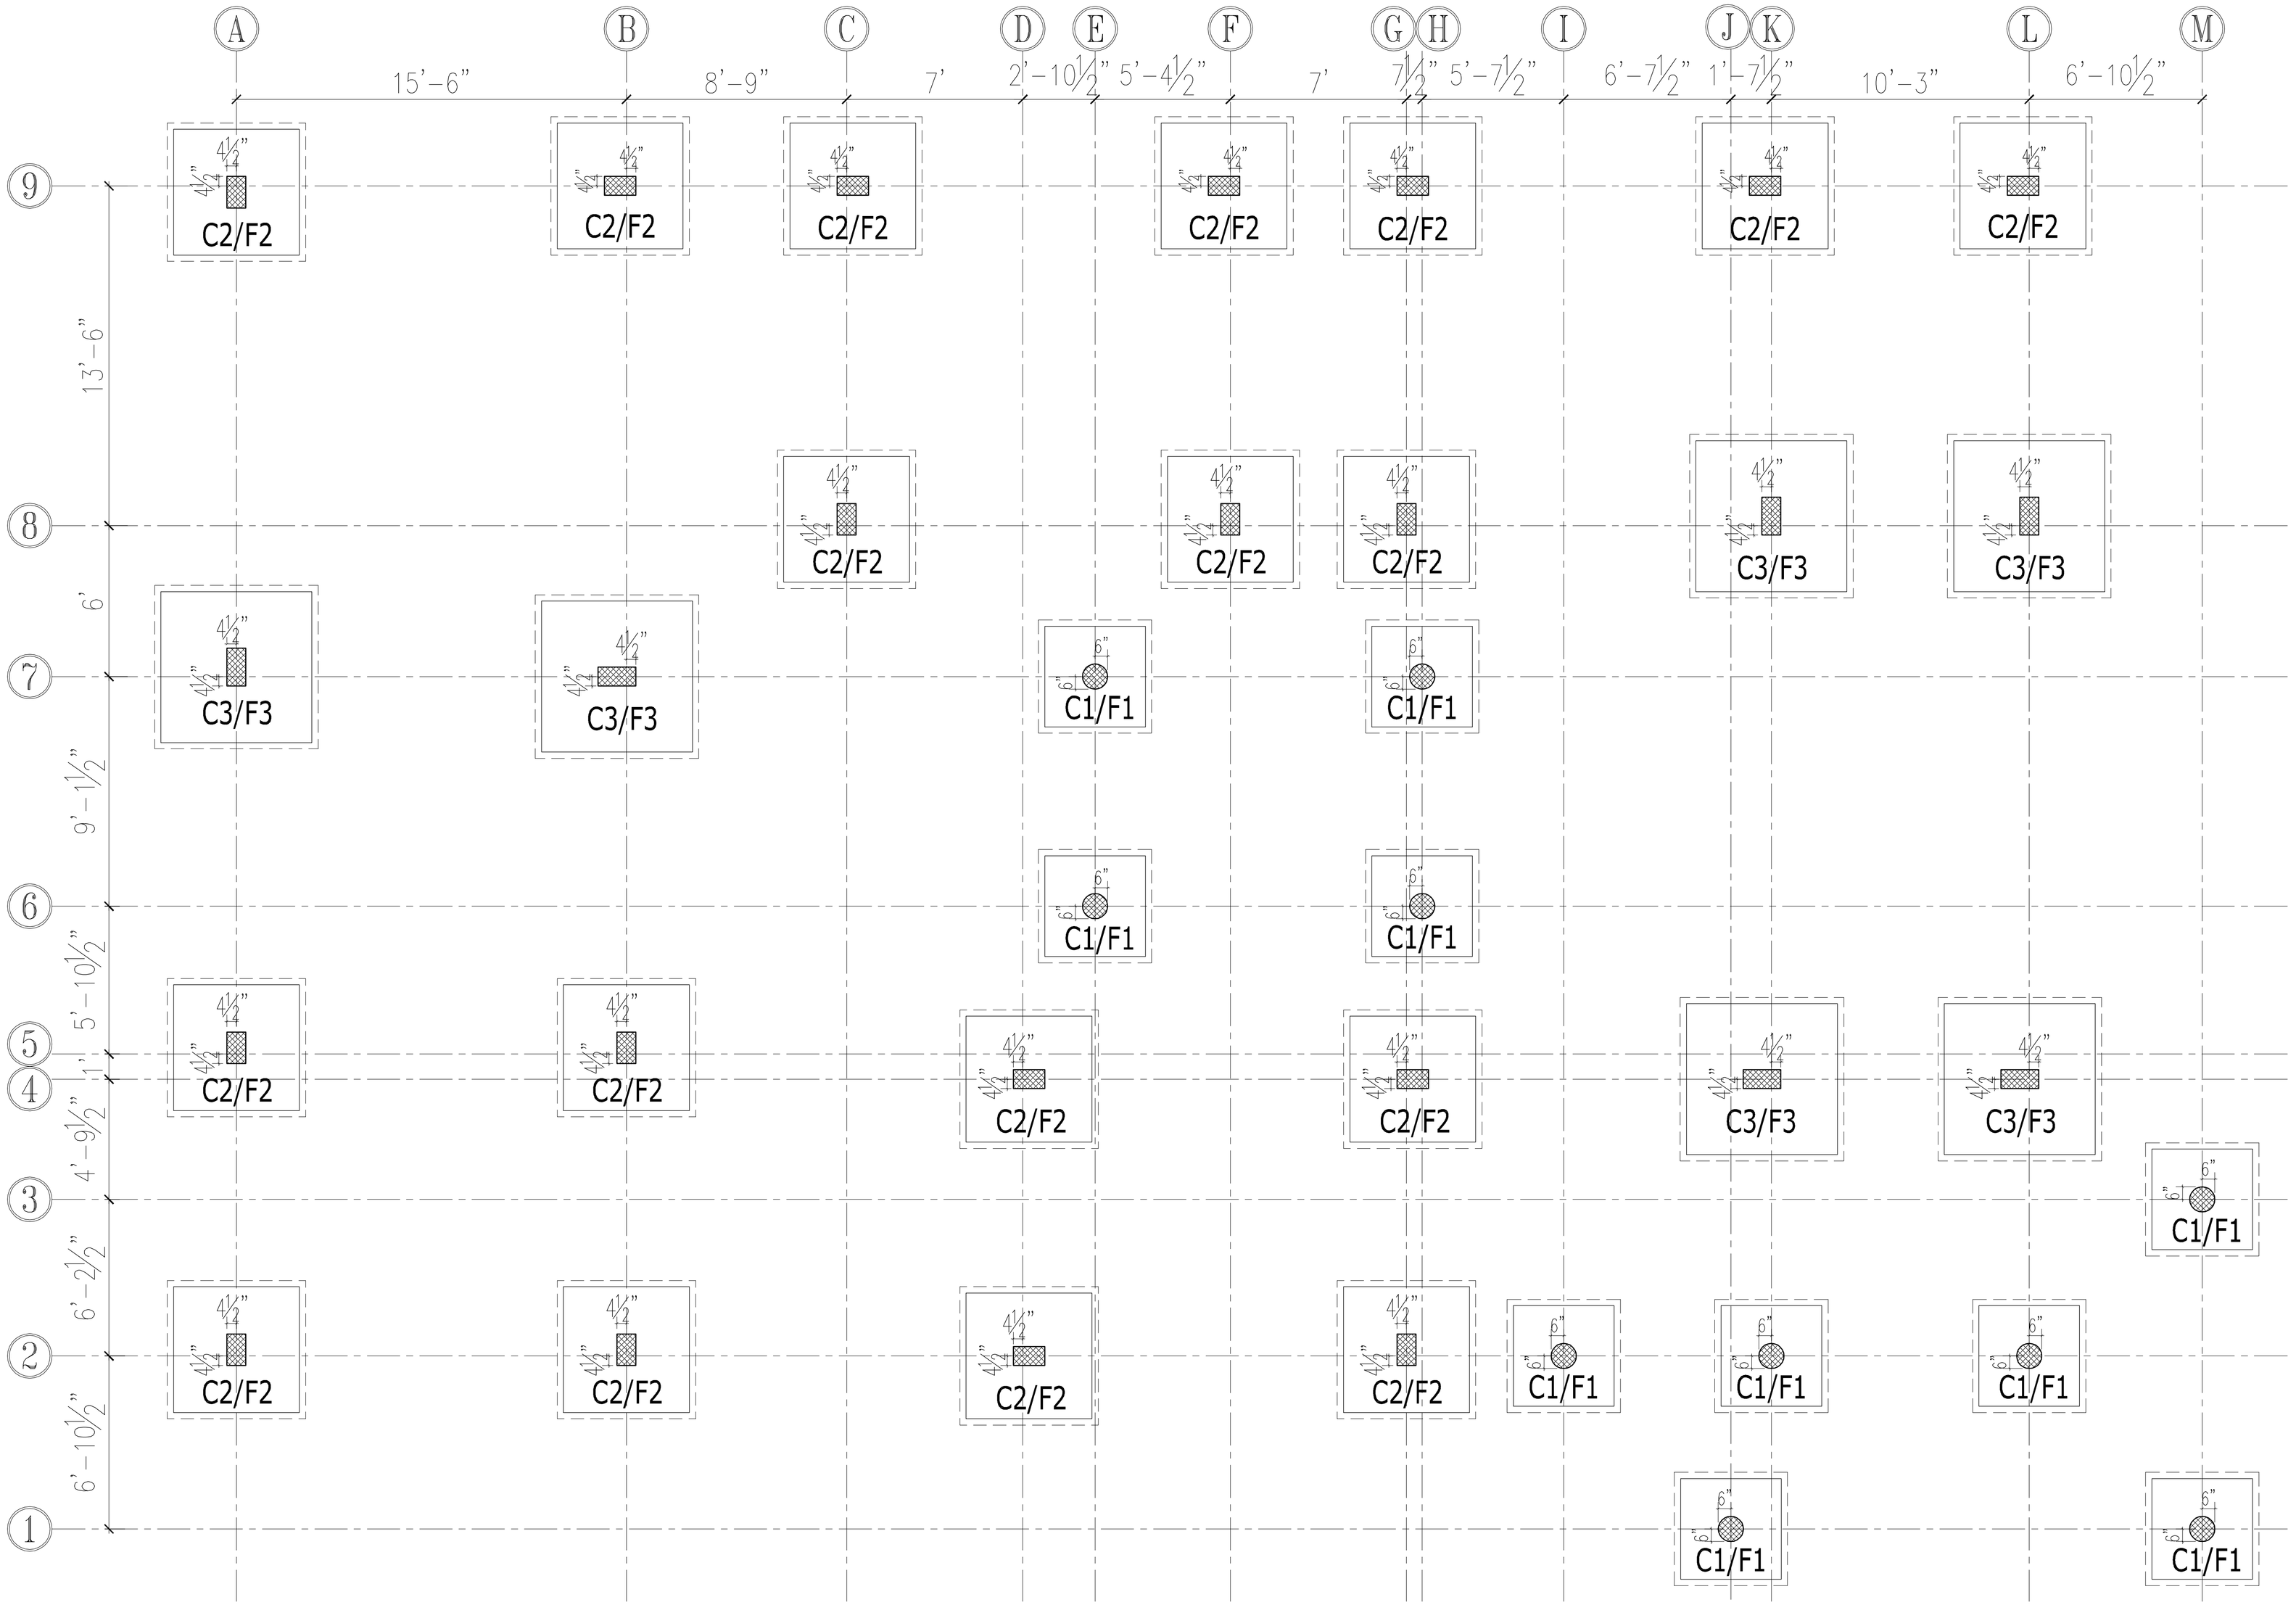

DIRECTION: N

ARCHITECTURAL CONSULTANT:

also. a design

STRUCTURAL& MEP CONSULTANTS

JASHRITHA ASSOCIATES AND MEP PLANNERS
4th FLOOR&BL HNO 12/5,KPHB COLONY, KUKATPALLY, (SUB BRANCH:PEN NAGAR,SRIKAKULAM) HYDERABAD-500072, TELANGANA, INDIA.
Phone : 9705441105,
E-mail@ jashreyansh.consultants@gmail.com
& Jashritha.mep@gmail.com

PROJECT:

ANKURA HOMES_THE WOODS AT KEESARAGUTTA

DRAWING TITLE:

FARM HOUSE BUILDING MARKING PLAN

DESIGN ENGG : AJAY	APPROVED :
SCALE : NTS	DRAWN : PK
DATE : 06-10-2026	CHECKED : PRADEEP
DRAWING NO: SD-01	REV.NO: