
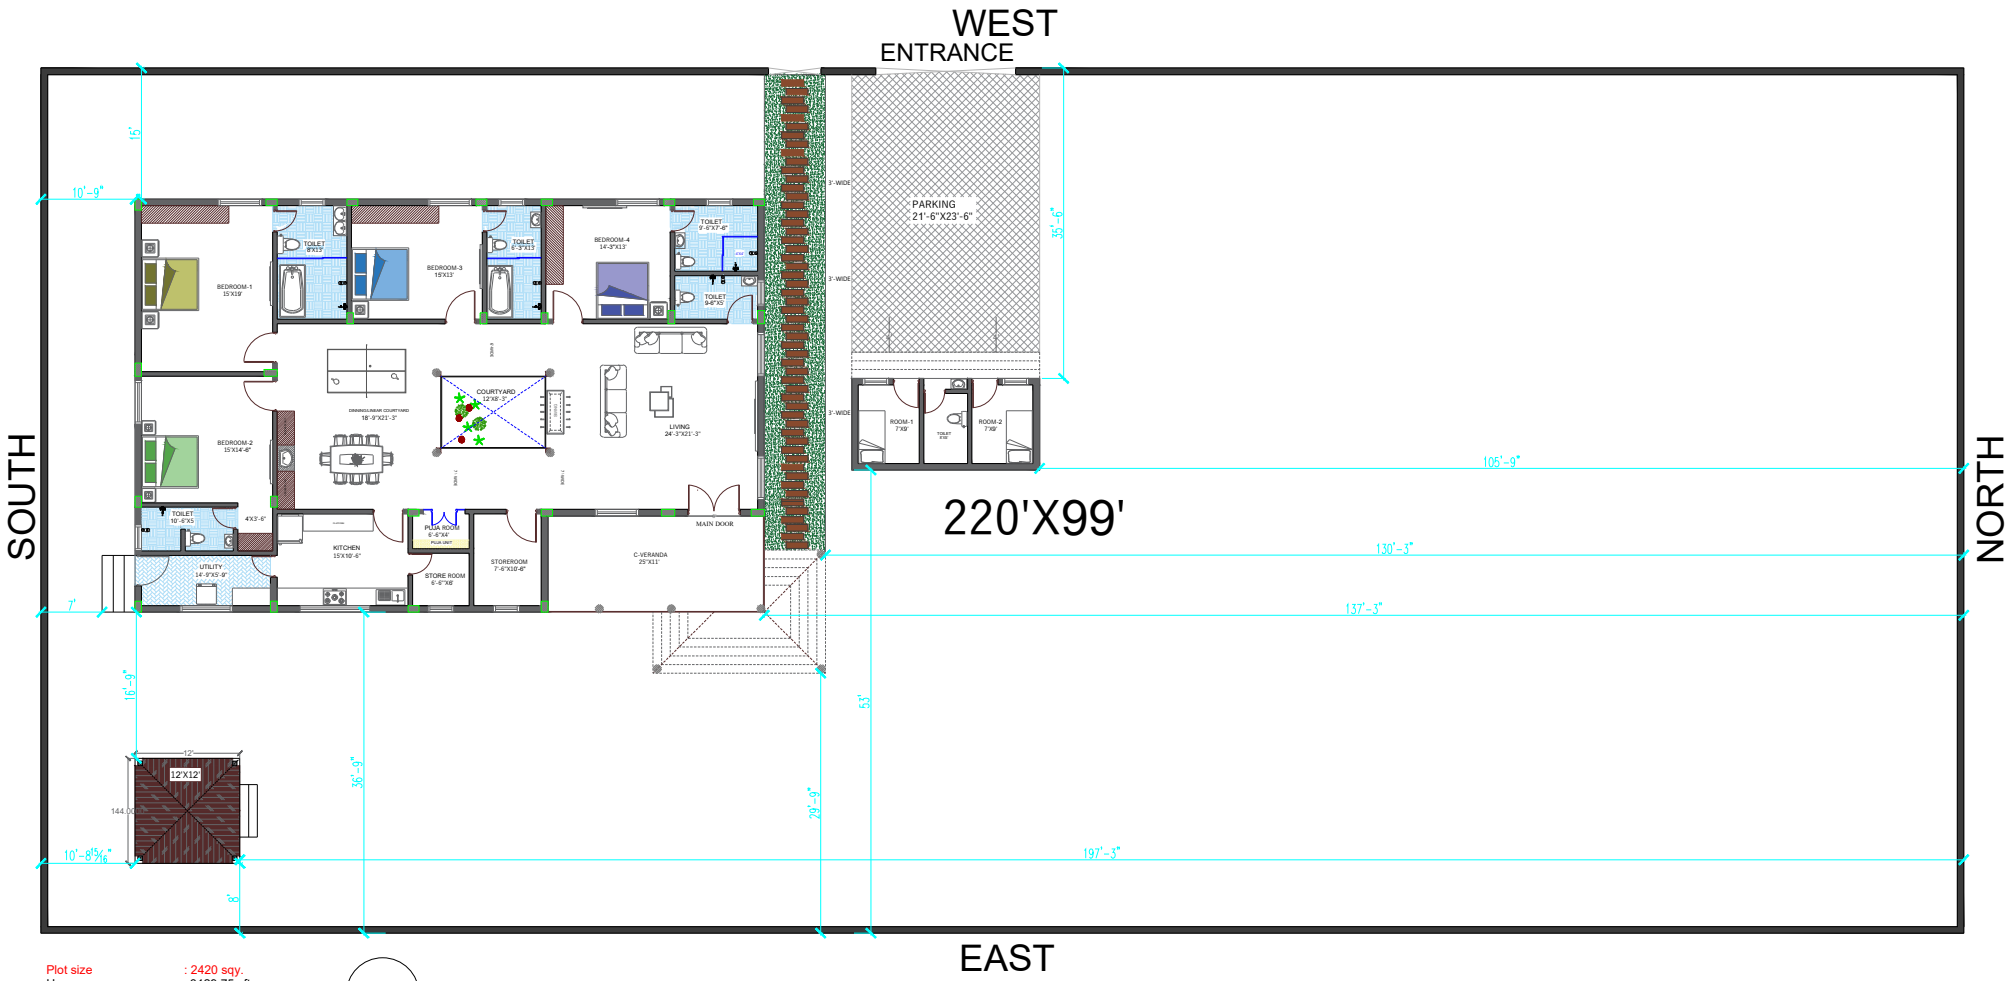


Plot size	: 2420 sqy.
House	: 3129.75 sft.
C-Veranda	: 272.25 sft.
Gazebo	: 144 sft.
Staircase	: 288.8 sft.
Servant Room	: 225.75 sft.
Total Basement Area	: 4096.92sft.
Car Parking	: 682.625 sft.

19&20

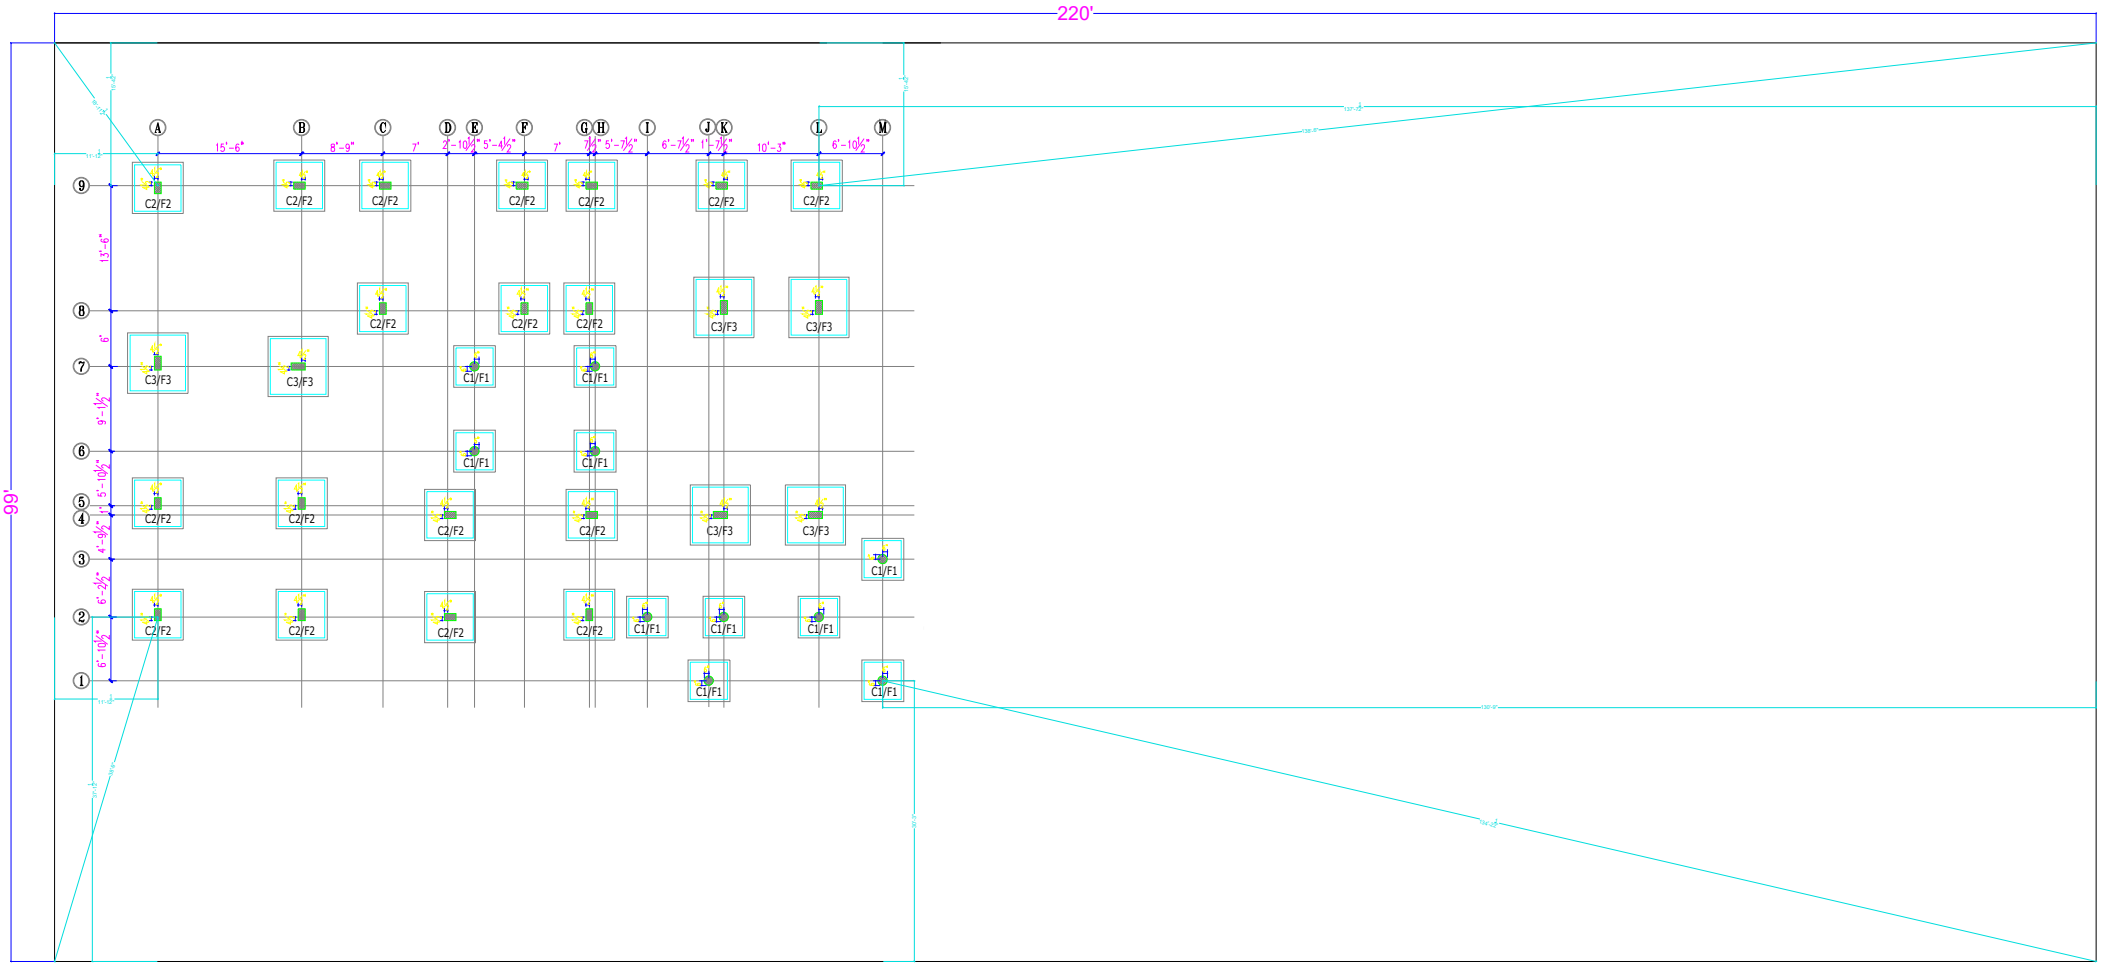


19&20

20261104_THE WOODS_Villa_19&20_Center Line Layout.

WEST

ENTRANCE

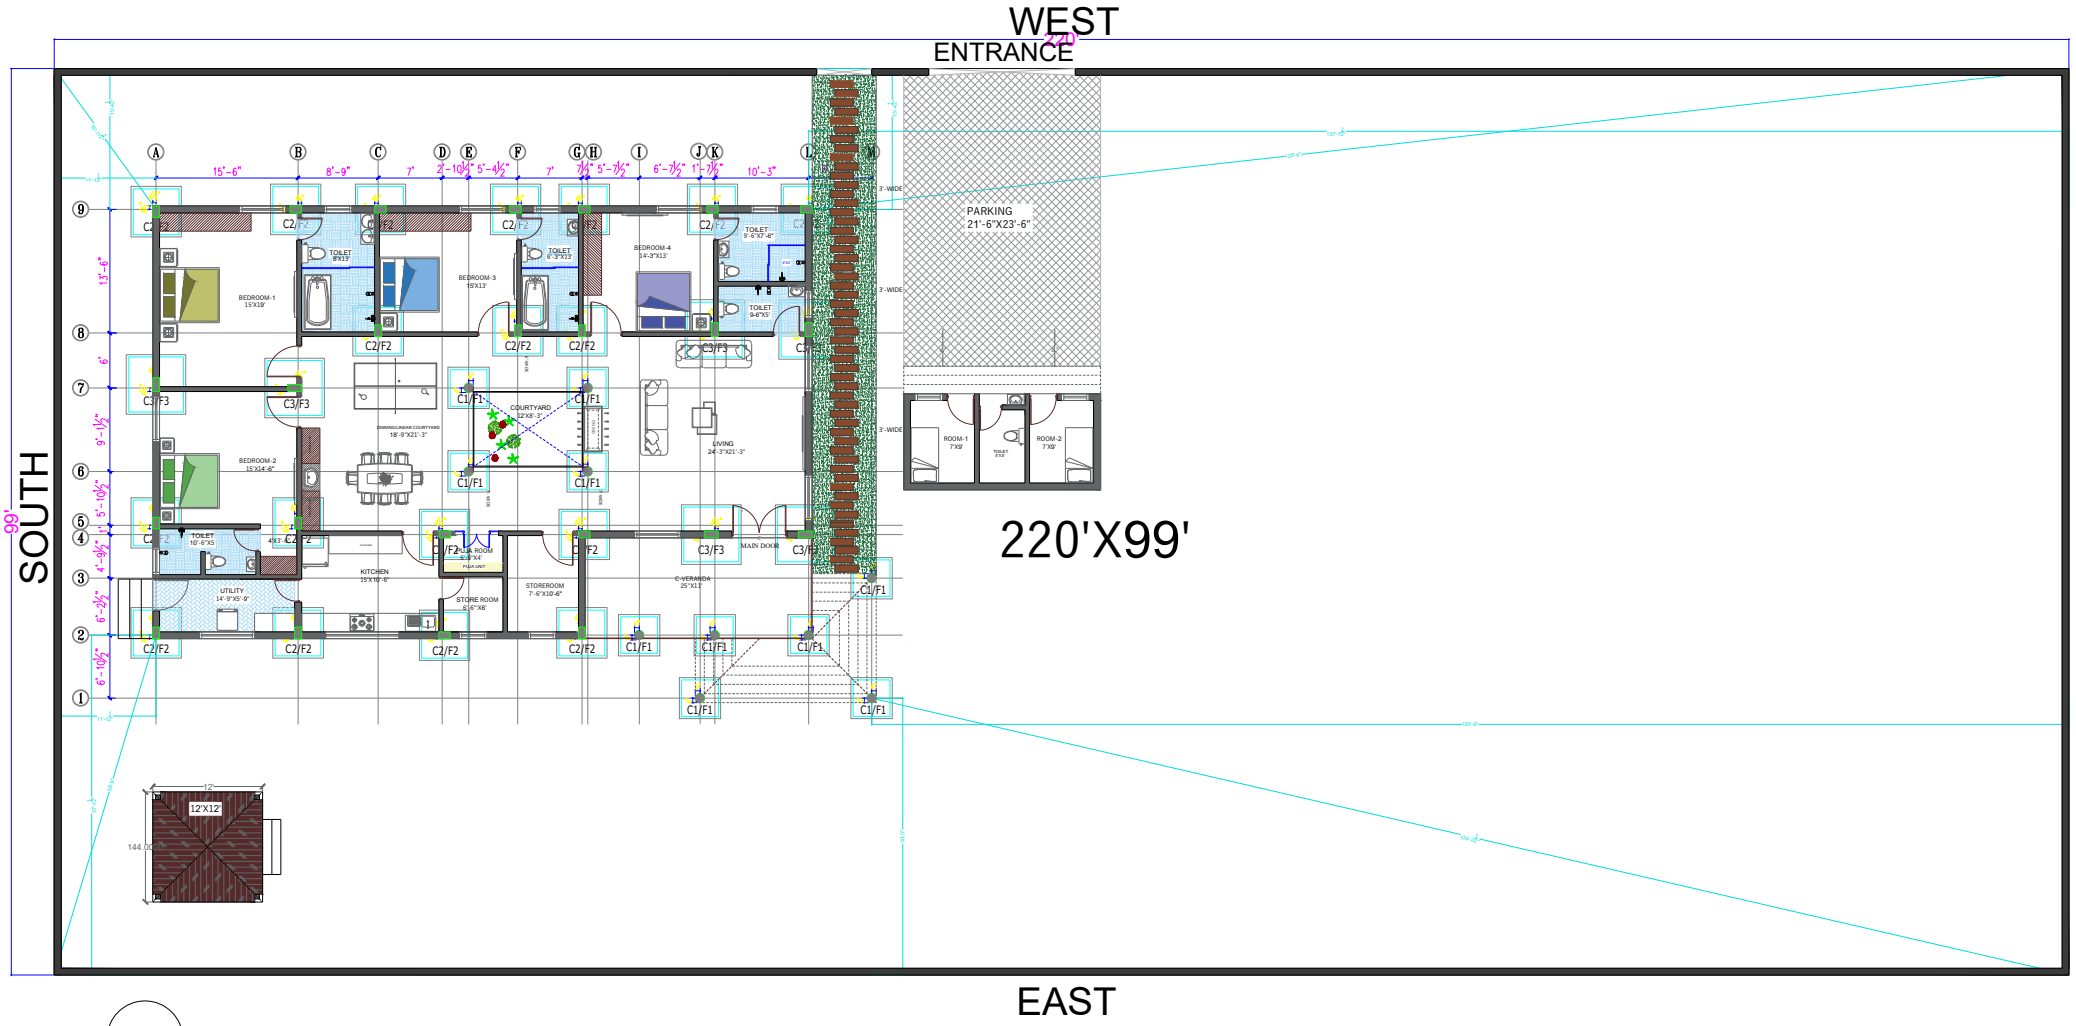

EAST

19&20

20261104_THE WOODS_Villa_19&20_Center Line With Floor Plan Layout.