

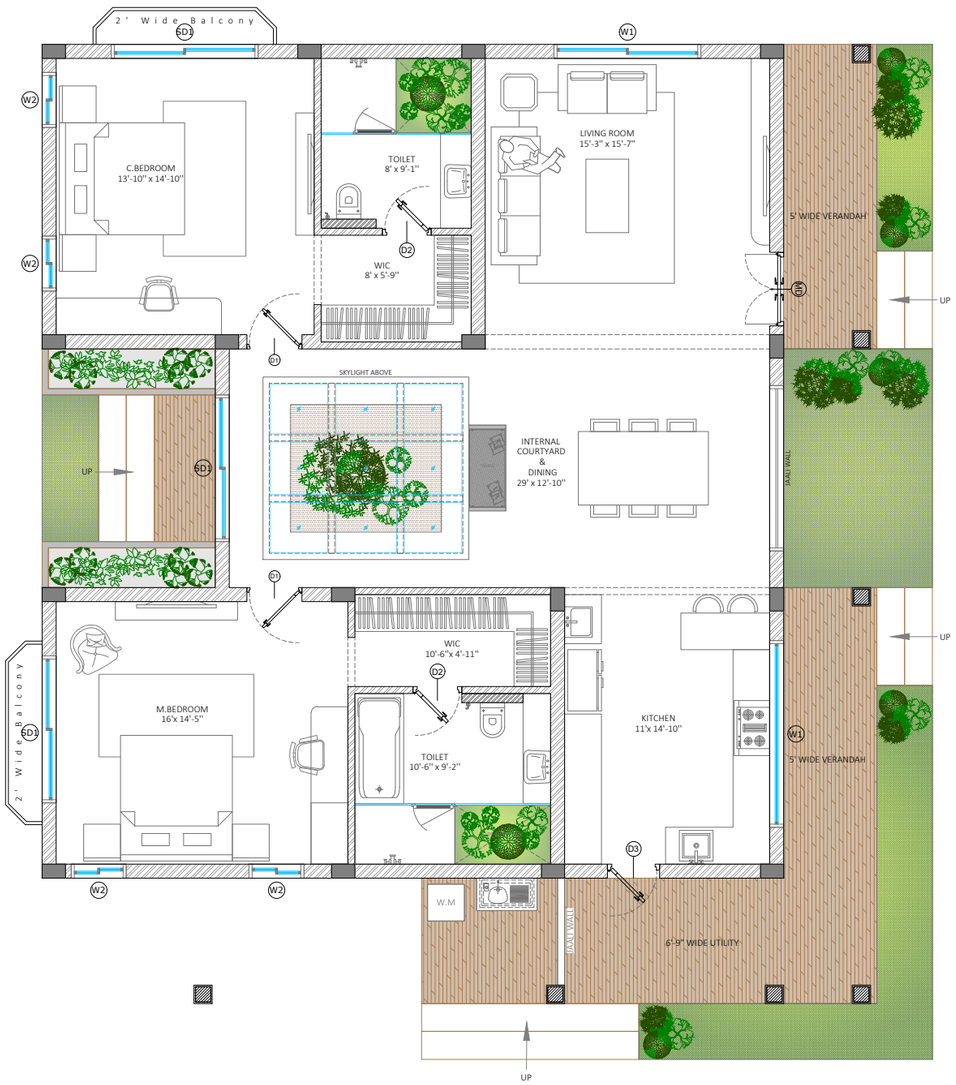



## EAST VILLA FLOOR PLAN

BUILT-UP AREA : 1625 SQ.FT
VERANDAH AREA : 350 SQ.FT

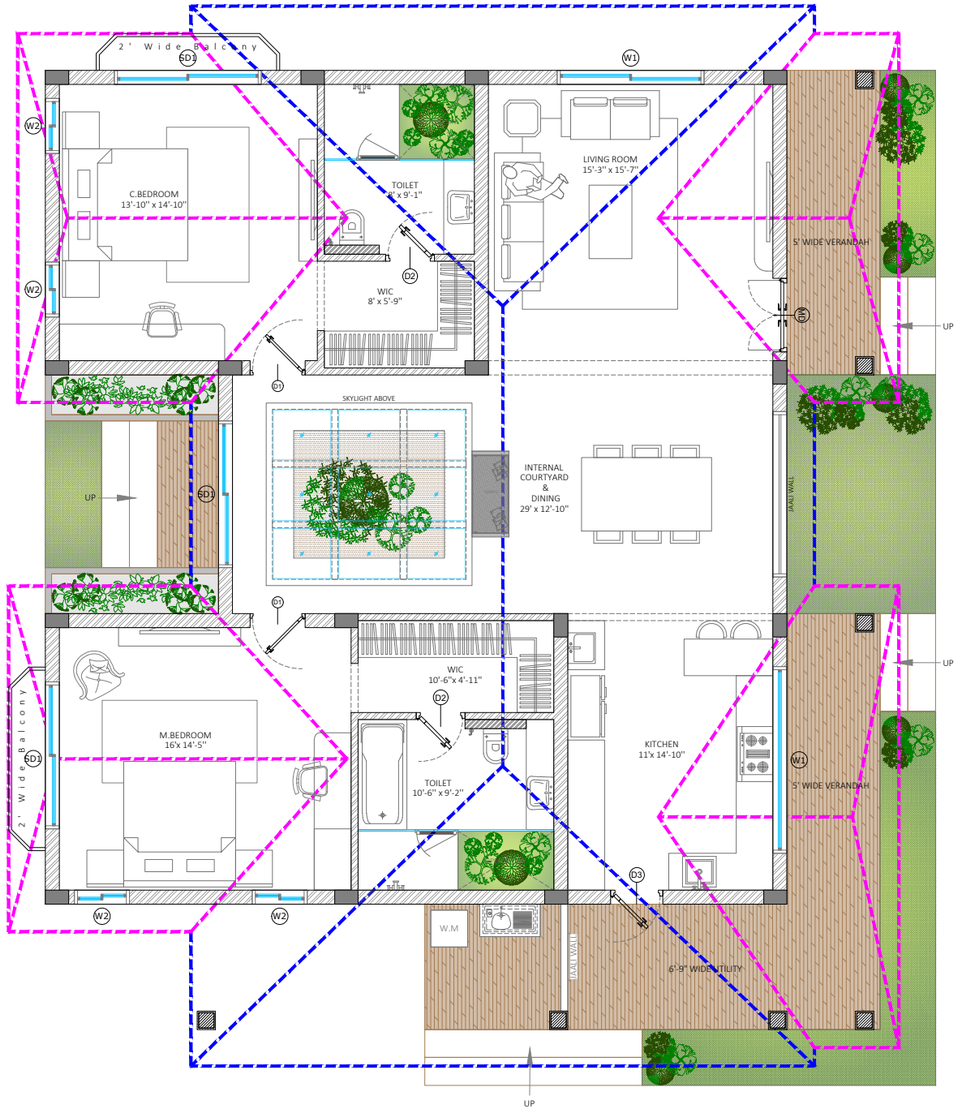


## EAST VILLA FLOOR PLAN WITH ROOF ABOVE

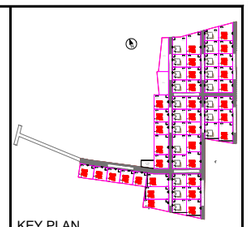

KEY PLAN

LEGEND:

- PRIMARY ROOF
- SECONDARY ROOF
- COLUMN TERMINATES AT ROOF LEVEL
- COLUMN TERMINATES AT PLINTH LEVEL
- MS COLUMN

GENERAL NOTES:

- ALL DIMENSIONS ARE IN MILLIMETERS
- THIS DRAWING IS A COPYRIGHT AND PROPERTY OF THE ARCHITECT, IS NOT TO BE PRODUCED, COPIED, HANDED OVER TO THIRD PARTY OR USED FOR ANY OTHER PURPOSE OTHER THAN FOR WHICH IT IS INTENDED.
- ALL DIMENSIONS SHALL BE VERIFIED ON SITE PRIOR TO START OF WORK ANY DISCREPANCY SHALL BE BROUGHT TO THE NOTICE OF THE ARCHITECT.
- THE CONTRACTOR MUST CHECK ALL DIMENSIONS AND DETAILS AND BE RESPONSIBLE FOR THE SAME. ANY DISCREPANCY SHALL BE BROUGHT TO THE NOTICE OF THE ARCHITECT.
- THIS DRAWING IS TO BE READ AND NOT SCALED.
- THIS DRAWING SHALL BE READ IN CONJUNCTION WITH ALL RELEVANT ARCHITECTURAL, STRUCTURAL AND SERVICES DRAWINGS. ANY DISCREPANCY NOTICED SHALL BE BROUGHT TO THE ATTENTION OF THE CONSULTANTS AND RESOLVED AS SOON AS POSSIBLE BUT ALWAYS PRIOR TO

| NO | DESCRIPTION | DATE | SIGN |
|---|---|---|---|

ARCHITECTURAL CONSULTANT:

also. design

MEP CONSULTANT:

JA

STRUCTURAL CONSULTANT:

JA

PROJECT:

ANKURA HOMES_THE WOODS
AT KEESARAGUTTA

GOOD FOR CONSTRUCTION

DRAWING TITLE:

1625_EAST VILLA
FLOOR PLAN

| | | | |
|---|---|---|---|
| ARCHITECT : HARISH | | APPROVED : HARISH | |
| SCALE : NTS | | DRAWN : DHARANI | |
| DATE : 08-10-2026 | | CHECKED : SHANMUKHI | |

DRAWING NO: REV.NO: