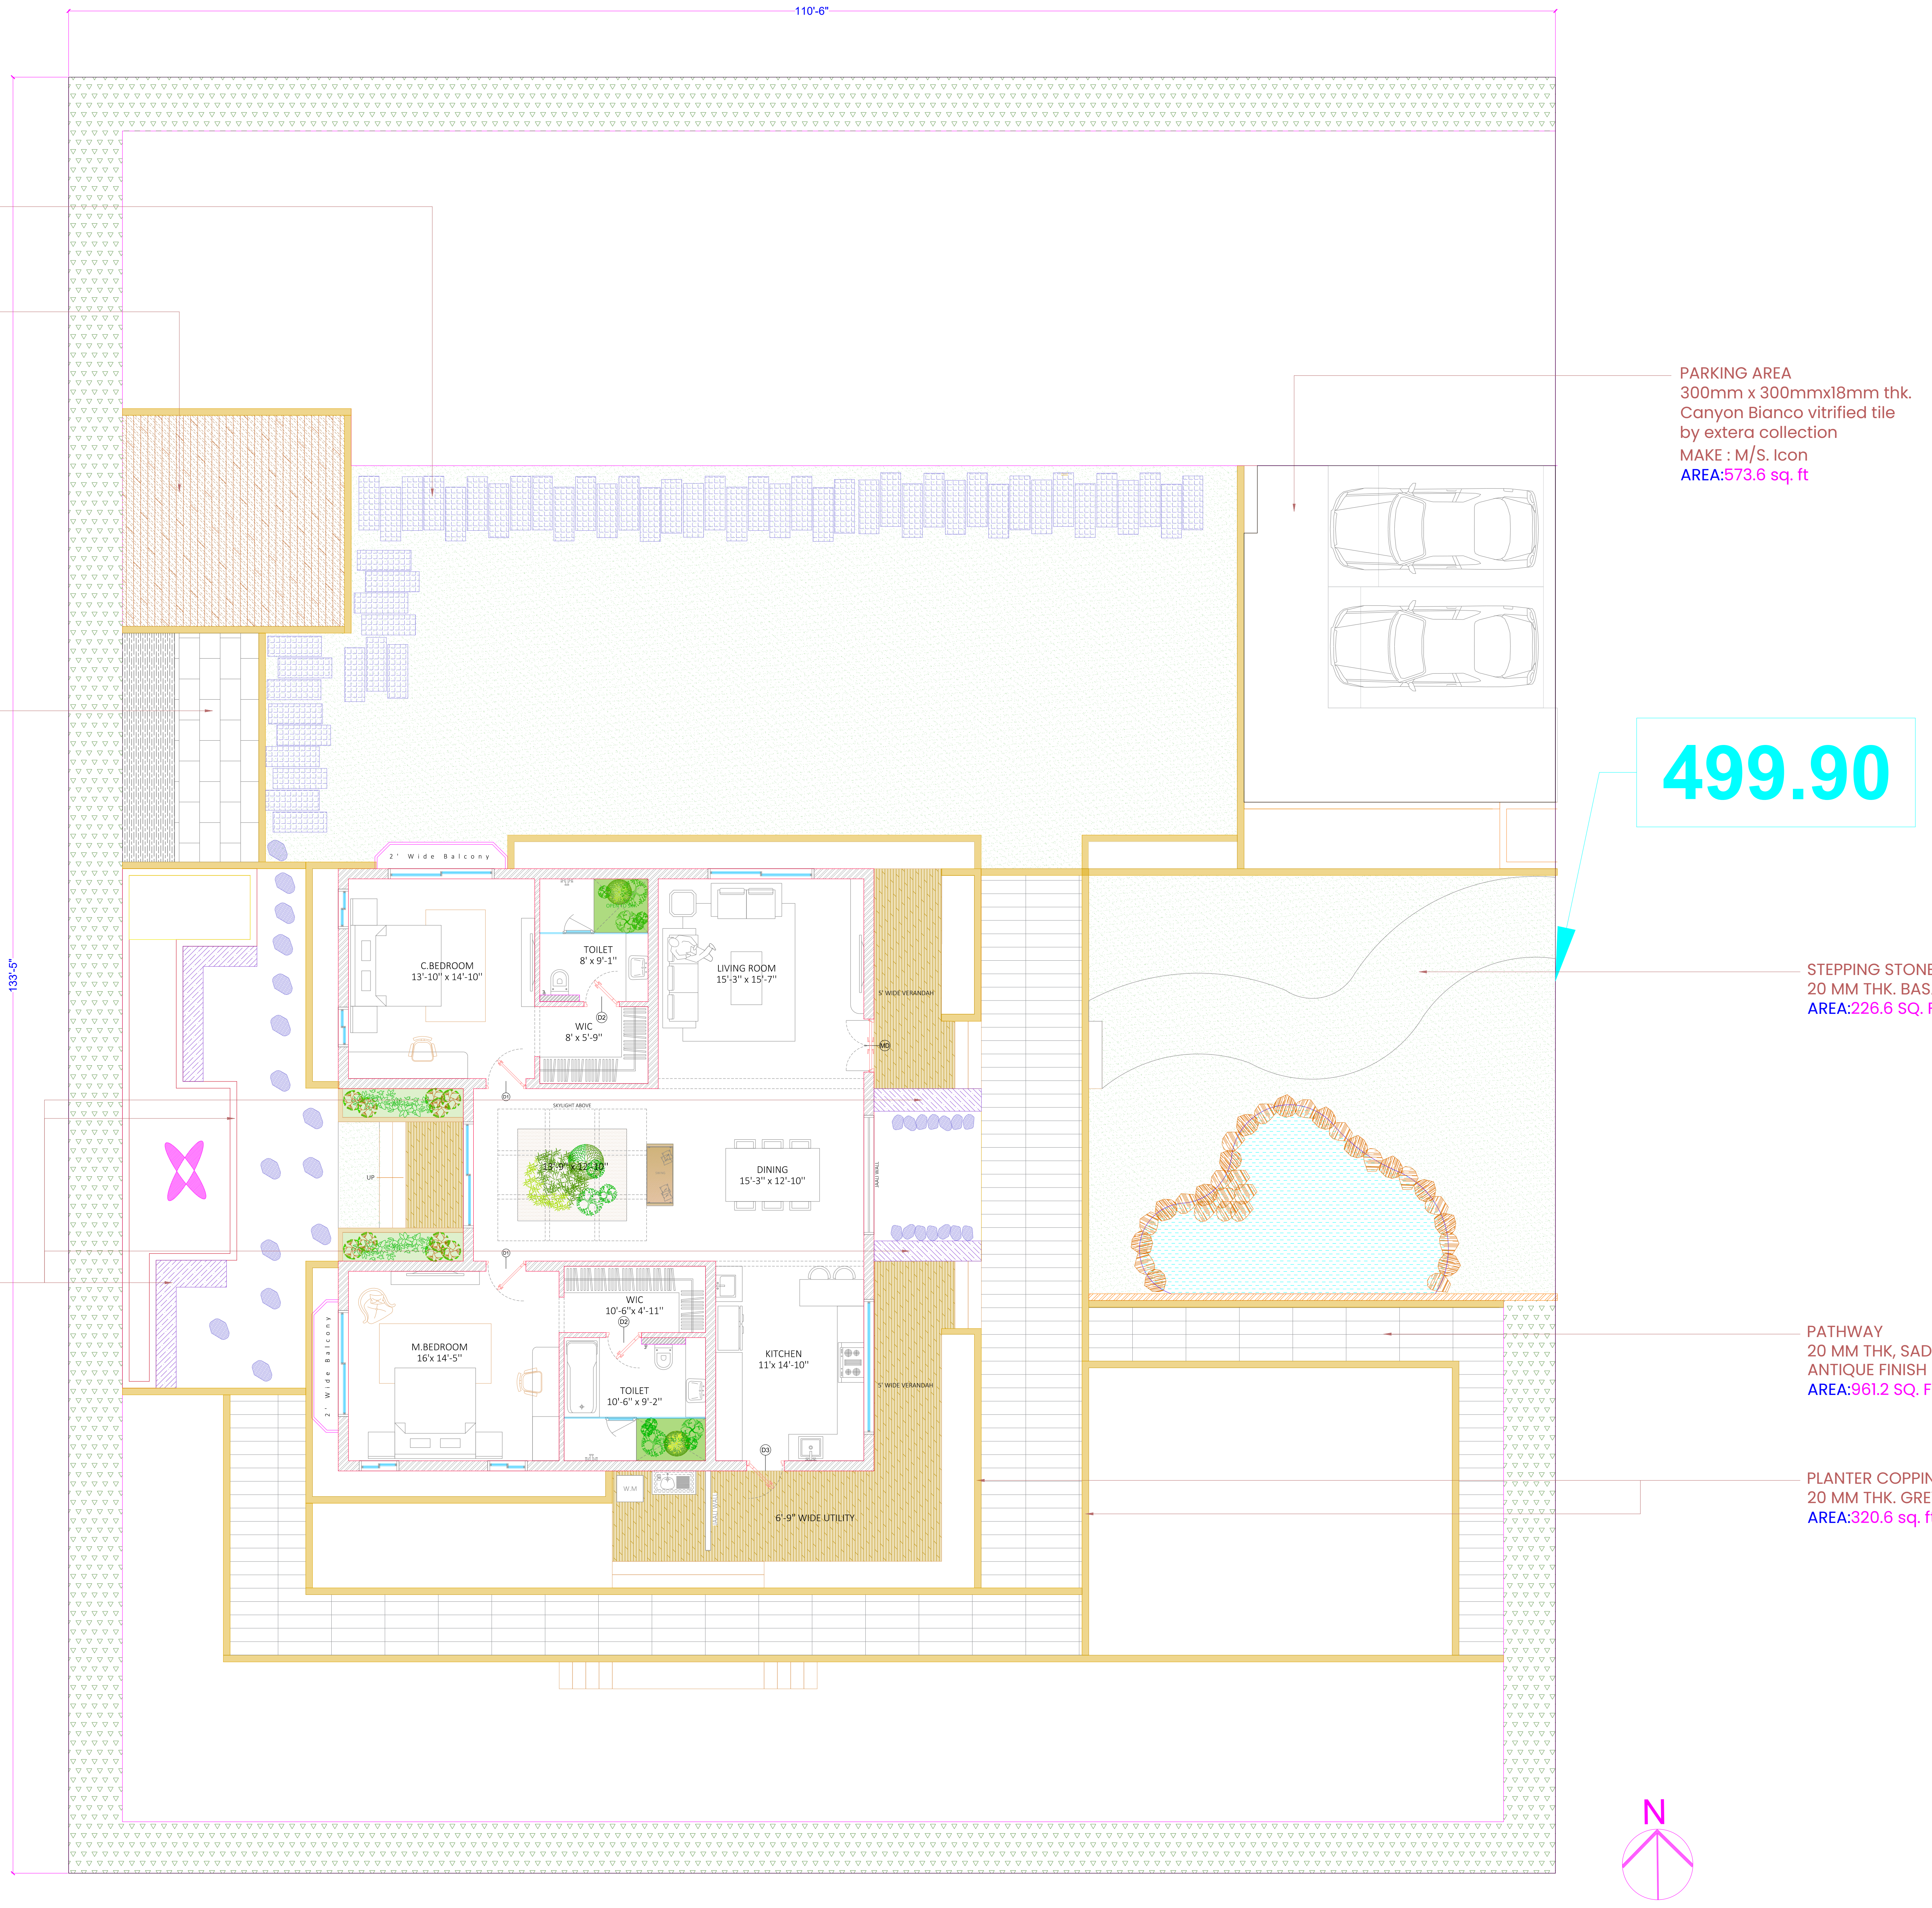

STEPPING STONES
20 MM THK. BASALT STONE ,RUSTIC FINISH
AREA:330 sq. ft.

DECK UNDER PERGOLA
20 MM KOTA YELLOW STONE
,LEATHER FINISH
AREA:258.7 sq. ft.

BARBEQUE COUNTER
20 MM THK.KOTA YELLOW
STONE ,LEATHER FINISH
AREA:172.3 SQ. FT.

SITTING & PLANTER,
20MM THK. SLIVER WAVES ,
HYDRO FINISH
AREA:68.1 sq. ft.(SEATING)
+51.6 sq. ft.(PLANTER)

PARKING AREA
300mm x 300mmx18mm thk.
Canyon Bianco vitrified tile
by extera collection
MAKE : M/S. Icon
AREA:573.6 sq. ft

STEPPING STONES
20 MM THK. BASALT STONE, RUSTIC FINISH
AREA:226.6 SQ. FT.

PATHWAY
20 MM THK, SADHARHALLI GREY GRANITE
ANTIQUE FINISH
AREA:961.2 SQ. FT.

PLANTER COPPING & BANDS
20 MM THK. GREY MAHOGANY ,LEATHER FINISH
AREA:320.6 sq. ft.

LUMISCAPES
Landscape Architects
Mob: +91 90309 62233 , +91 95151 03063
contact@lumiscapeslandscapes.in

NOTES
1. THIS DRAWING SHOULD BE READ AND NOT MEASURED.
2. ALL DIMENSIONS ARE IN MILLIMETERS AND LEVELS ARE IN METERS UNLESS STATED OTHERWISE.
3. ALL DRAWINGS MUST BE CROSS REFERENCE IN CASE OF ANY DOUBT / DISCREPANCY.
4. TOC REPRESENTS TOP OF CONCRETE & FFL REPRESENTS FINISHED FLOOR LEVELS. ALL DIMENSIONS SHOWN IN THE DRAWINGS ARE STRUCTURAL / MASONRY DIMENSIONS.
5. ALL ARCHITECTURAL DRAWINGS MUST BE REFERRED IN COORDINATION WITH STRUCTURAL DRAWINGS.
6. ALL SPECIALIST WORKS DETAILS AND ANY DEVIATIONS FROM THIS CONSTRUCTION DRAWINGS, THE CONTRACTOR / SUB-CONTRACTOR ARE TO PROVIDE SHOP DRAWINGS FOR ARCHITECT'S / ENGINEER'S APPROVAL PRIOR TO CONSTRUCTION.

KEY PLAN

DRAWING STAGE
FOR INFORMATION &APPROVAL

GFC STAMP

CLIENT
M/S. ANKURA HOMES

LEGEND
NOTE : ALL THE DIMENSIONS ARE IN FEET

ARCHITECTS
also. design

MEP CONSULTANTS

STRUCTURAL CONSULTANTS

PROJECT TITLE
"THE WOODS" BY ANKURA HOMES @BOMMALARAMARAM

DRAWING TITLE
LANDSCAPE MATERIAL PLAN OPTION -01

NORTH
N

LA ARCHITECT	YASASWINI & CHARITA	REV.	DATE
DWG NO :	LLA-TW-MP-01	08	25-08-26
CHECKED BY :	CHARITA.M	09	26-08-26
DRAWN BY :	P.VAMSI	10	20-09-26
DATE :	06-10-2026	11	25-09-26
SCALE :	NTS	SHEET - A2	