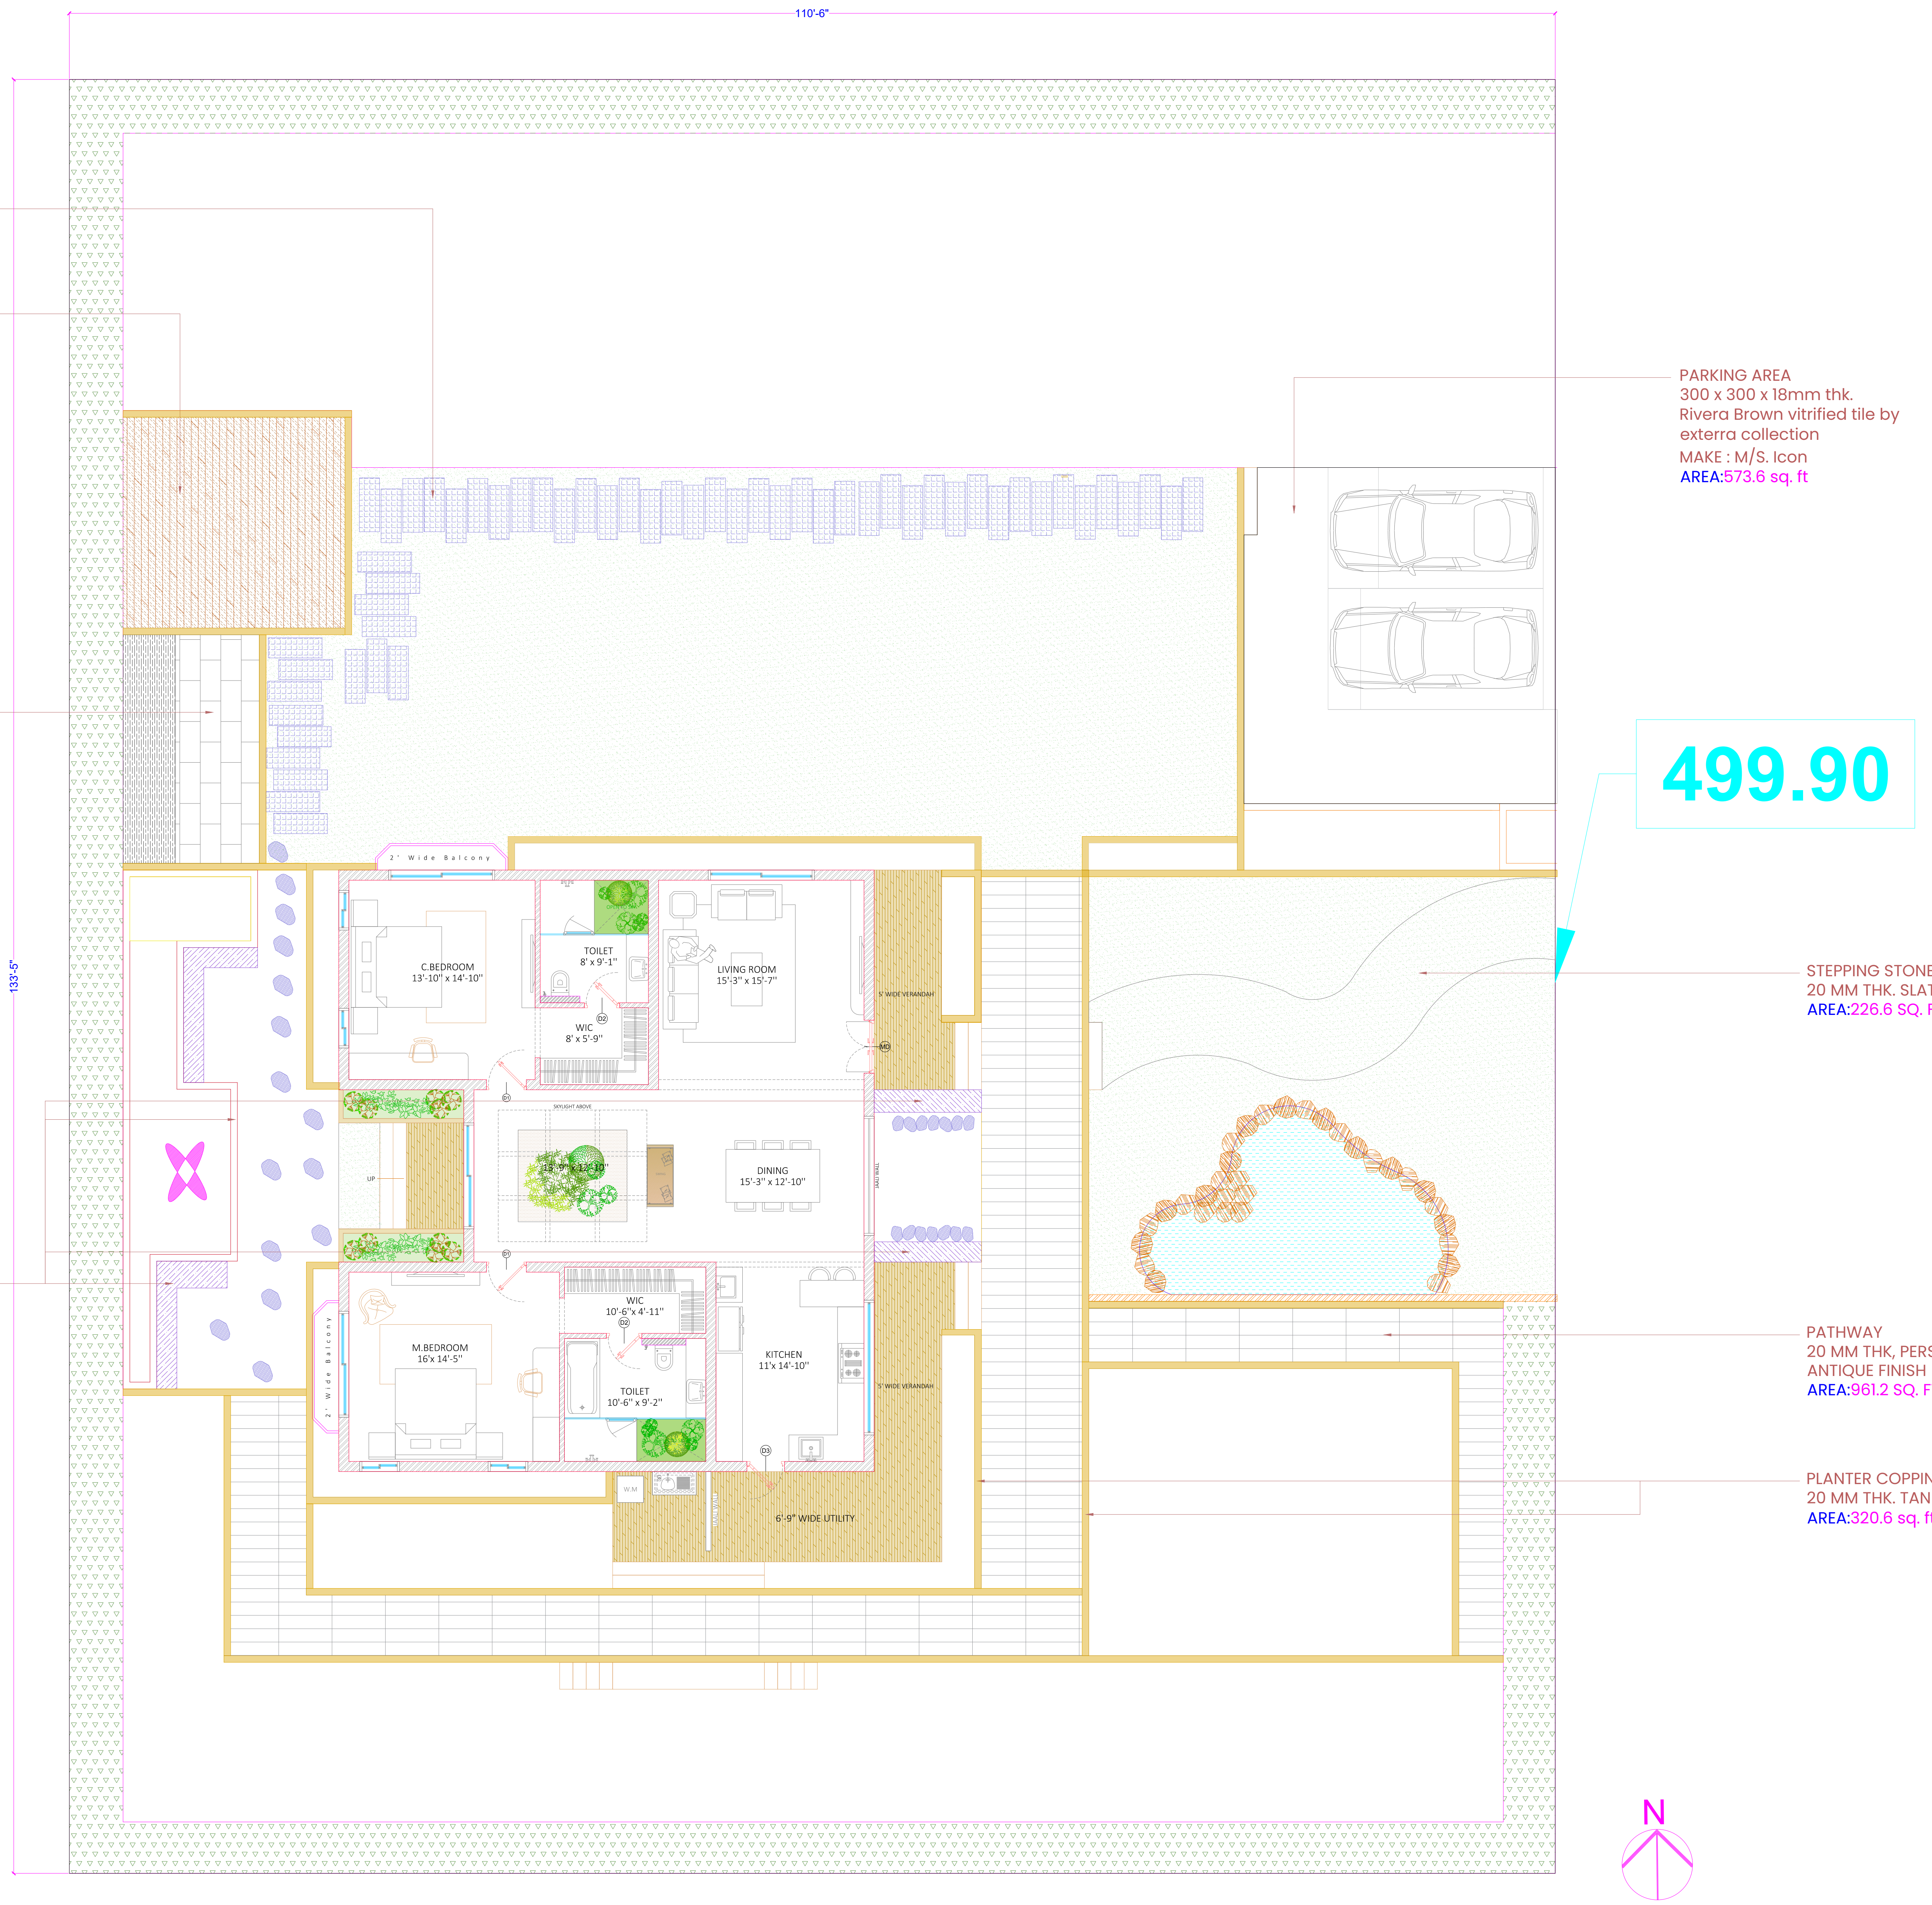
110'-6"
133'-5"
2' Wide Balcony
C.BEDROOM
13'-10" x 14'-10"
TOILET
8' x 9'-1"
OPEN TO SKY
WIC
8' x 5'-9"
D2
LIVING ROOM
15'-3" x 15'-7"
5' WIDE VERANDAH
MD
D1
SKYLIGHT ABOVE
UP
13'-9" x 12'-10"
SWING
DINING
15'-3" x 12'-10"
JAALI WALL
D1
WIC
10'-6"x 4'-11"
D2
M.BEDROOM
16'x 14'-5"
2' Wide Balcony
TOILET
10'-6" x 9'-2"
KITCHEN
11'x 14'-10"
D3
5' WIDE VERANDAH
W.M
JAALI WALL
6'-9" WIDE UTILITY
499.90
N

STEPPING STONES
20 MM THK. SLATE STONE NATURAL FINISH
AREA:330 sq. ft.

DECK UNDER PERGOLA
20 MM KOTA YELLOW STONE ,LEATHER FINISH
AREA:258.7 sq. ft.

BARBEQUE COUNTER
20 MM KOTA YELLOW STONE ,LEATHER FINISH
AREA:172.3 sq. ft.

SITTING & PLANTER,
20MM THK. GOLDEN DREAM, HYDRO FINISH
AREA:68.1 sq. ft.(SEATING)
+51.6 sq. ft.(PLANTER)

PARKING AREA
300 x 300 x 18mm thk.
Rivera Brown vitrified tile by
exterra collection
MAKE : M/S. Icon
AREA:573.6 sq. ft

STEPPING STONES
20 MM THK. SLATE STONE ,NATURAL FINISH
AREA:226.6 SQ. FT.

PATHWAY
20 MM THK, PERSIAN BROWN GRANITE ANTIQUE FINISH
AREA:961.2 SQ. FT.

PLANTER COPPING & BANDS
20 MM THK. TAN BROWN ,LEATHER FINISH
AREA:320.6 sq. ft.

LUMISCAPES
Landscape Architects
Mob: +91 90309 62233 , +91 95151 03063
contact@lumiscapeslandscapes.in

NOTES
1. THIS DRAWING SHOULD BE READ AND NOT MEASURED.
2. ALL DIMENSIONS ARE IN MILLIMETERS AND LEVELS ARE IN METERS UNLESS STATED OTHERWISE.
3. ALL DRAWINGS MUST BE CROSS REFERENCE IN CASE OF ANY DOUBT / DISCREPANCY.
4. TOC REPRESENTS TOP OF CONCRETE & FFL REPRESENTS FINISHED FLOOR LEVELS. ALL DIMENSIONS SHOWN IN THE DRAWINGS ARE STRUCTURAL / MASONRY DIMENSIONS.
5. ALL ARCHITECTURAL DRAWINGS MUST BE REFERRED IN COORDINATION WITH STRUCTURAL DRAWINGS.
6. ALL SPECIALIST WORKS DETAILS AND ANY DEVIATIONS FROM THIS CONSTRUCTION DRAWINGS, THE CONTRACTOR / SUB-CONTRACTOR ARE TO PROVIDE SHOP DRAWINGS FOR ARCHITECT'S / ENGINEER'S APPROVAL PRIOR TO CONSTRUCTION.

KEY PLAN

DRAWING STAGE
FOR INFORMATION &APPROVAL

GFC STAMP

CLIENT
M/S. ANKURA HOMES

LEGEND
NOTE : ALL THE DIMENSIONS ARE IN FEET

ARCHITECTS
also. design
a little story of design

MEP CONSULTANTS

STRUCTURAL CONSULTANTS

PROJECT TITLE
"THE WOODS" BY ANKURA HOMES @BOMMALARAMARAM

DRAWING TITLE
LANDSCAPE MATERIAL PLAN OPTION -02

NORTH
N

		REV.	DATE
LA ARCHITECT	YASASWINI & CHARITA		
DWG NO :	LLA-TW-MP-02	08	25-08-26
CHECKED BY :	CHARITA.M	09	26-08-26
DRAWN BY :	P.VAMSI	10	20-09-26
DATE :	06-10-2026	11	25-09-26
SCALE :	NTS	SHEET - A2	