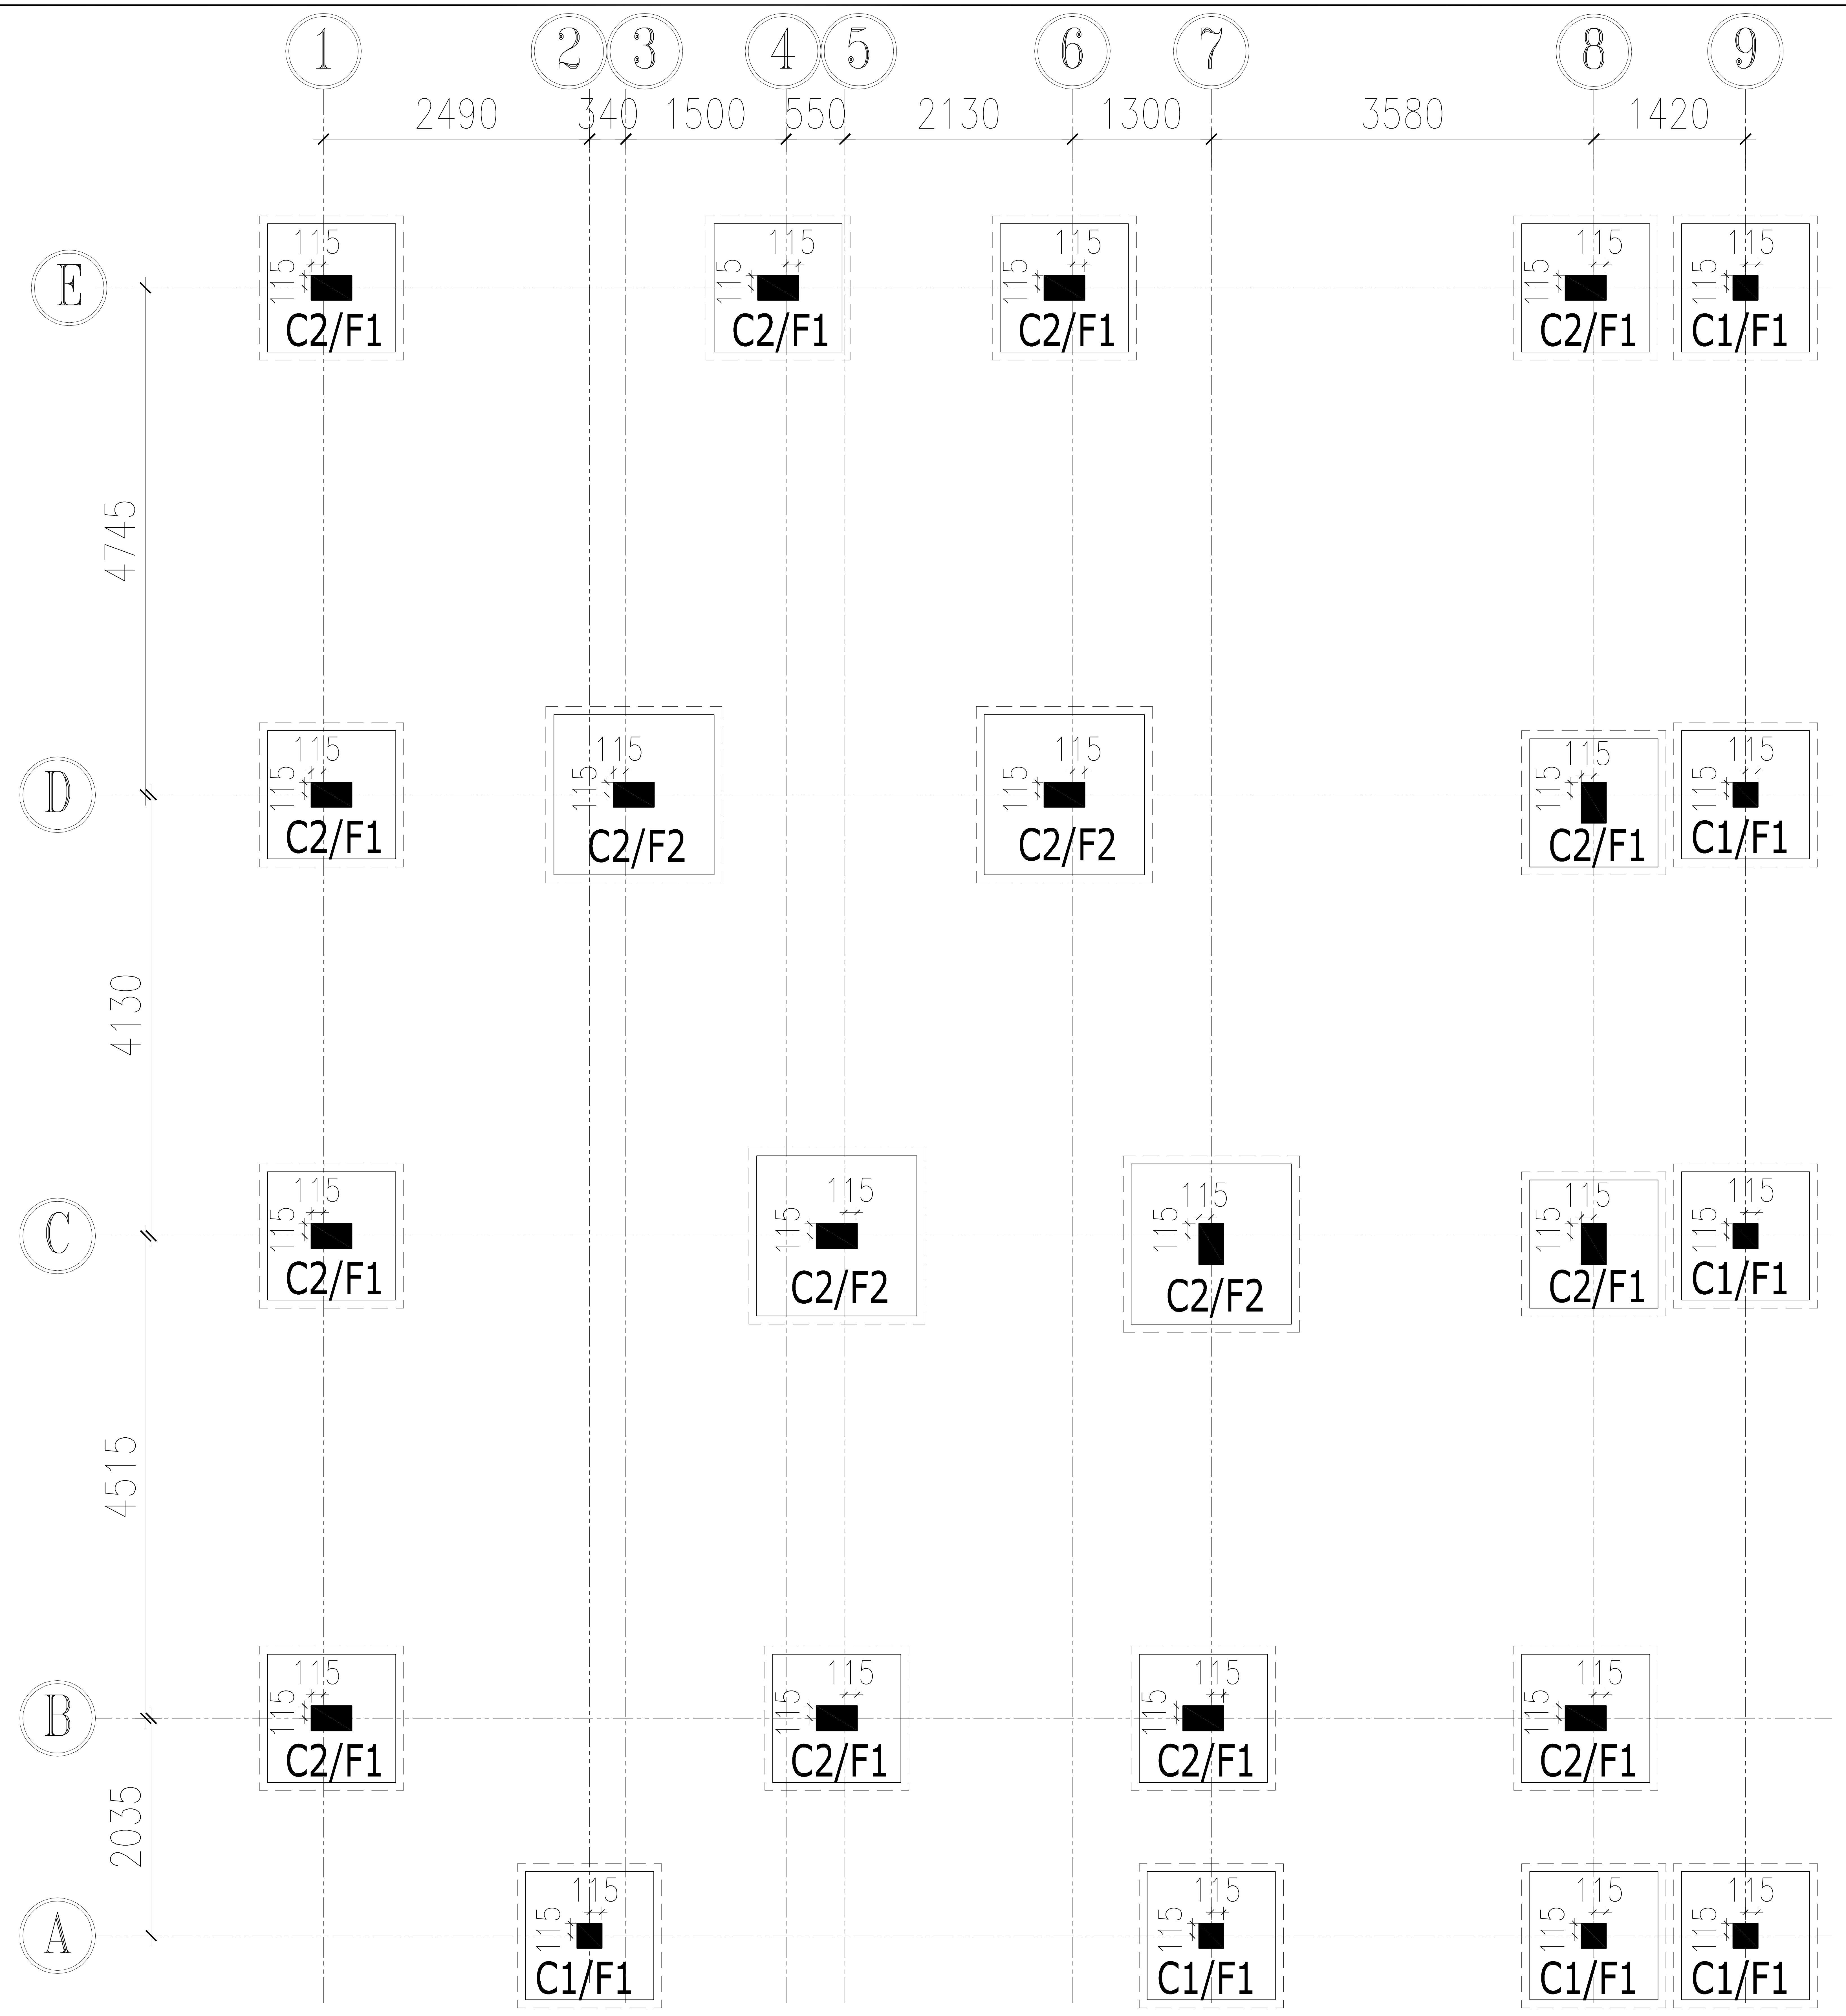

- THIS DRAWING SHALL BE READ IN CONJUNCTION WITH ALL RELEVANT ARCHITECTURAL, STRUCTURAL AND SERVICES DRAWINGS. ANY DISCREPANCY NOTICED SHALL BE BROUGHT TO THE ATTENTION OF THE CONSULTANTS AND RESOLVED AS SOON AS POSSIBLE BUT ALWAYS PRIOR TO

DIRECTION:

N

ARCHITECTURAL CONSULTANT:

also. design
a little story of design

STRUCTURAL& MEP CONSULTANTS

JASHRITHA ASSOCIATES
AND MEP PLANNERS
4th FLOOR(4B), HIG 129, KPHB COLONY, KUKATPALLY,
(SUB BRANCH:PR NAGAR ERRAGADDA.)
HYDERABAD 500072, TELANGANA, INDIA
Phone : 9700441106.
E-mail : jashreyansh.consultatns@gmail.com
& jashritha.mep@gmail.com

PROJECT:

ANKURA HOMES_THE WOODS
AT KEESARAGUTTA

DRAWING TITLE:

1625_EAST VILLA
MARKING PLAN

| | |
|---|---|
| DESIGN ENGG : AJAY | APPROVED : |
| SCALE : NTS | DRAWN : PK |
| DATE : 23-09-2026 | CHECKED : PRADEEP |
| DRAWING NO: SD-01 | REV.NO: 01 |

## COLUMN SCHEDULE

| COLUMN ID | GRADE OF CONCRETE | COLUMN SIZE UPTO GROUND FLOOR ROOF | REFERENCE SECTION |
|---|---|---|---|
| C1 | M - 25 | 230 x 230<br>#12 -4Nos | A1 |
| C2 | M - 25 | 230 x 380<br>#16 -4Nos + #12 -4Nos | A2 |

## ARRANGEMENT OF TIES, LINKS & MAIN BARS IN COLUMN

| | | | | |
|---|---|---|---|---|
| 4 BARS ARRANGEMENT | 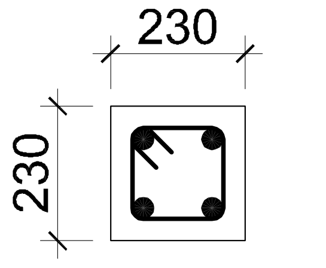 4 EQUAL DIA (A1) | 8 BARS ARRANGEMENT | 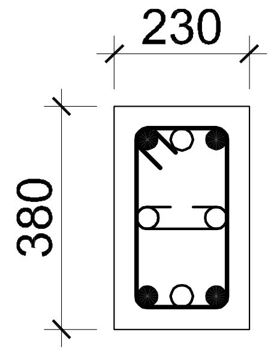 • 4 LARGER DIA<br>○ 4 LARGER DIA<br>(A2) | 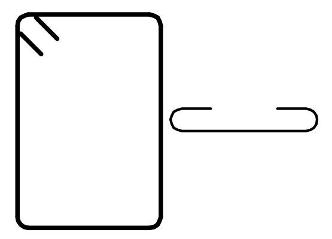 1 Tie +<br>1 Link<br>#8 @150c/c |

## FLAT FOOTING SCHEDULE:

| GROUP | MIX | SIZE | DEPTH | BOTTOM REINFORCEMENT PARALLEL TO | |
|---|---|---|---|---|---|
| | | | | SHORTER DIRECTION | LONGER DIRECTION |
| F1 | M - 25 | 1200 x 1200 | 375 | #10 -10 NOS | #10 -10 NOS |
| F2 | M - 25 | 1500 x 1500 | 400 | #10 -15 NOS | #10 -15 NOS |

### GENERAL NOTES:

1. DO NOT SCALE THIS DRAWING. FOLLOW FIGURED DIMENSIONS ONLY.
2. ALL DIMENSIONS ARE IN MM ONLY AND LEVELS ARE IN METERS UNLESS SPECIFIED.
3. S.B.C OF SOIL IS CONSIDERED AS 270 KN/M$^2$ @ 2.0M DEPTH
4. USE VIBRATED REINFORCED CONCRETE CONFORMING TO IS:456-2000. THE GRADES FOR DIFFERENT COMPONENTS ARE AS FOLLOWS

| COMPONENT | FOOTING | COLUMNS | BEAMS | SLABS | WATER TANK SIDE WALLS |
|---|---|---|---|---|---|
| MIX | M25 | M25 | M25 | M25 | M25 |

5. GRADE OF STEEL SHALL BE Fe 500 CONFORMING TO IS:1786-85 & AMENDMENTS.
6. LAPS SHALL BE STAGGERED AND LAP LENGTHS ARE AS FOLLOWS.

| MIX | M25 |
|---|---|
| Ld | 48 Dia |

7. NOT MORE THAN 50% OF COLUMN REINFORCEMENT SHALL BE LAPPED AT A PARTICULAR LOCATION.
8. CLEAR COVERS ARE AS FOLLOWS

| FOOTING TO MAIN BAR | COLUMN TO MAIN BAR | BEAMS TO STIRRUPS | SLABS TO MAIN BAR |
|---|---|---|---|
| 50mm | 40mm | 20mm | 20mm |

9. CURING SHOULD BE DONE ATLEAST FOR 21 DAYS.
10. THIS DRAWING SHOULD BE READ IN CONJUNCTION WITH RELEVANT ARCHITECTURAL DRAWINGS.
11. STRIPPING TIME OF FORMWORK SHALL CONFORM TO CLAUSE 11.3 OF IS:456-2000.
12. FOR TIES,LINKS IN COLUMNS Y8-150mm c/c REFER COLUMN SCHEDULE DWG.
13. FOR EXACT LOCATION OF WALLS REFER RELEVANT ARCHITECTURAL DRAWINGS FOR NECESSARY DETAILS.
14. ANY DISCREPANCY FROM THE DRAWING SHALL BE BROUGHT TO THE NOTICE OF CONSULTANTS.
15. THE STRUCTURE IS DESIGNED FOR GROUND FLOOR ONLY

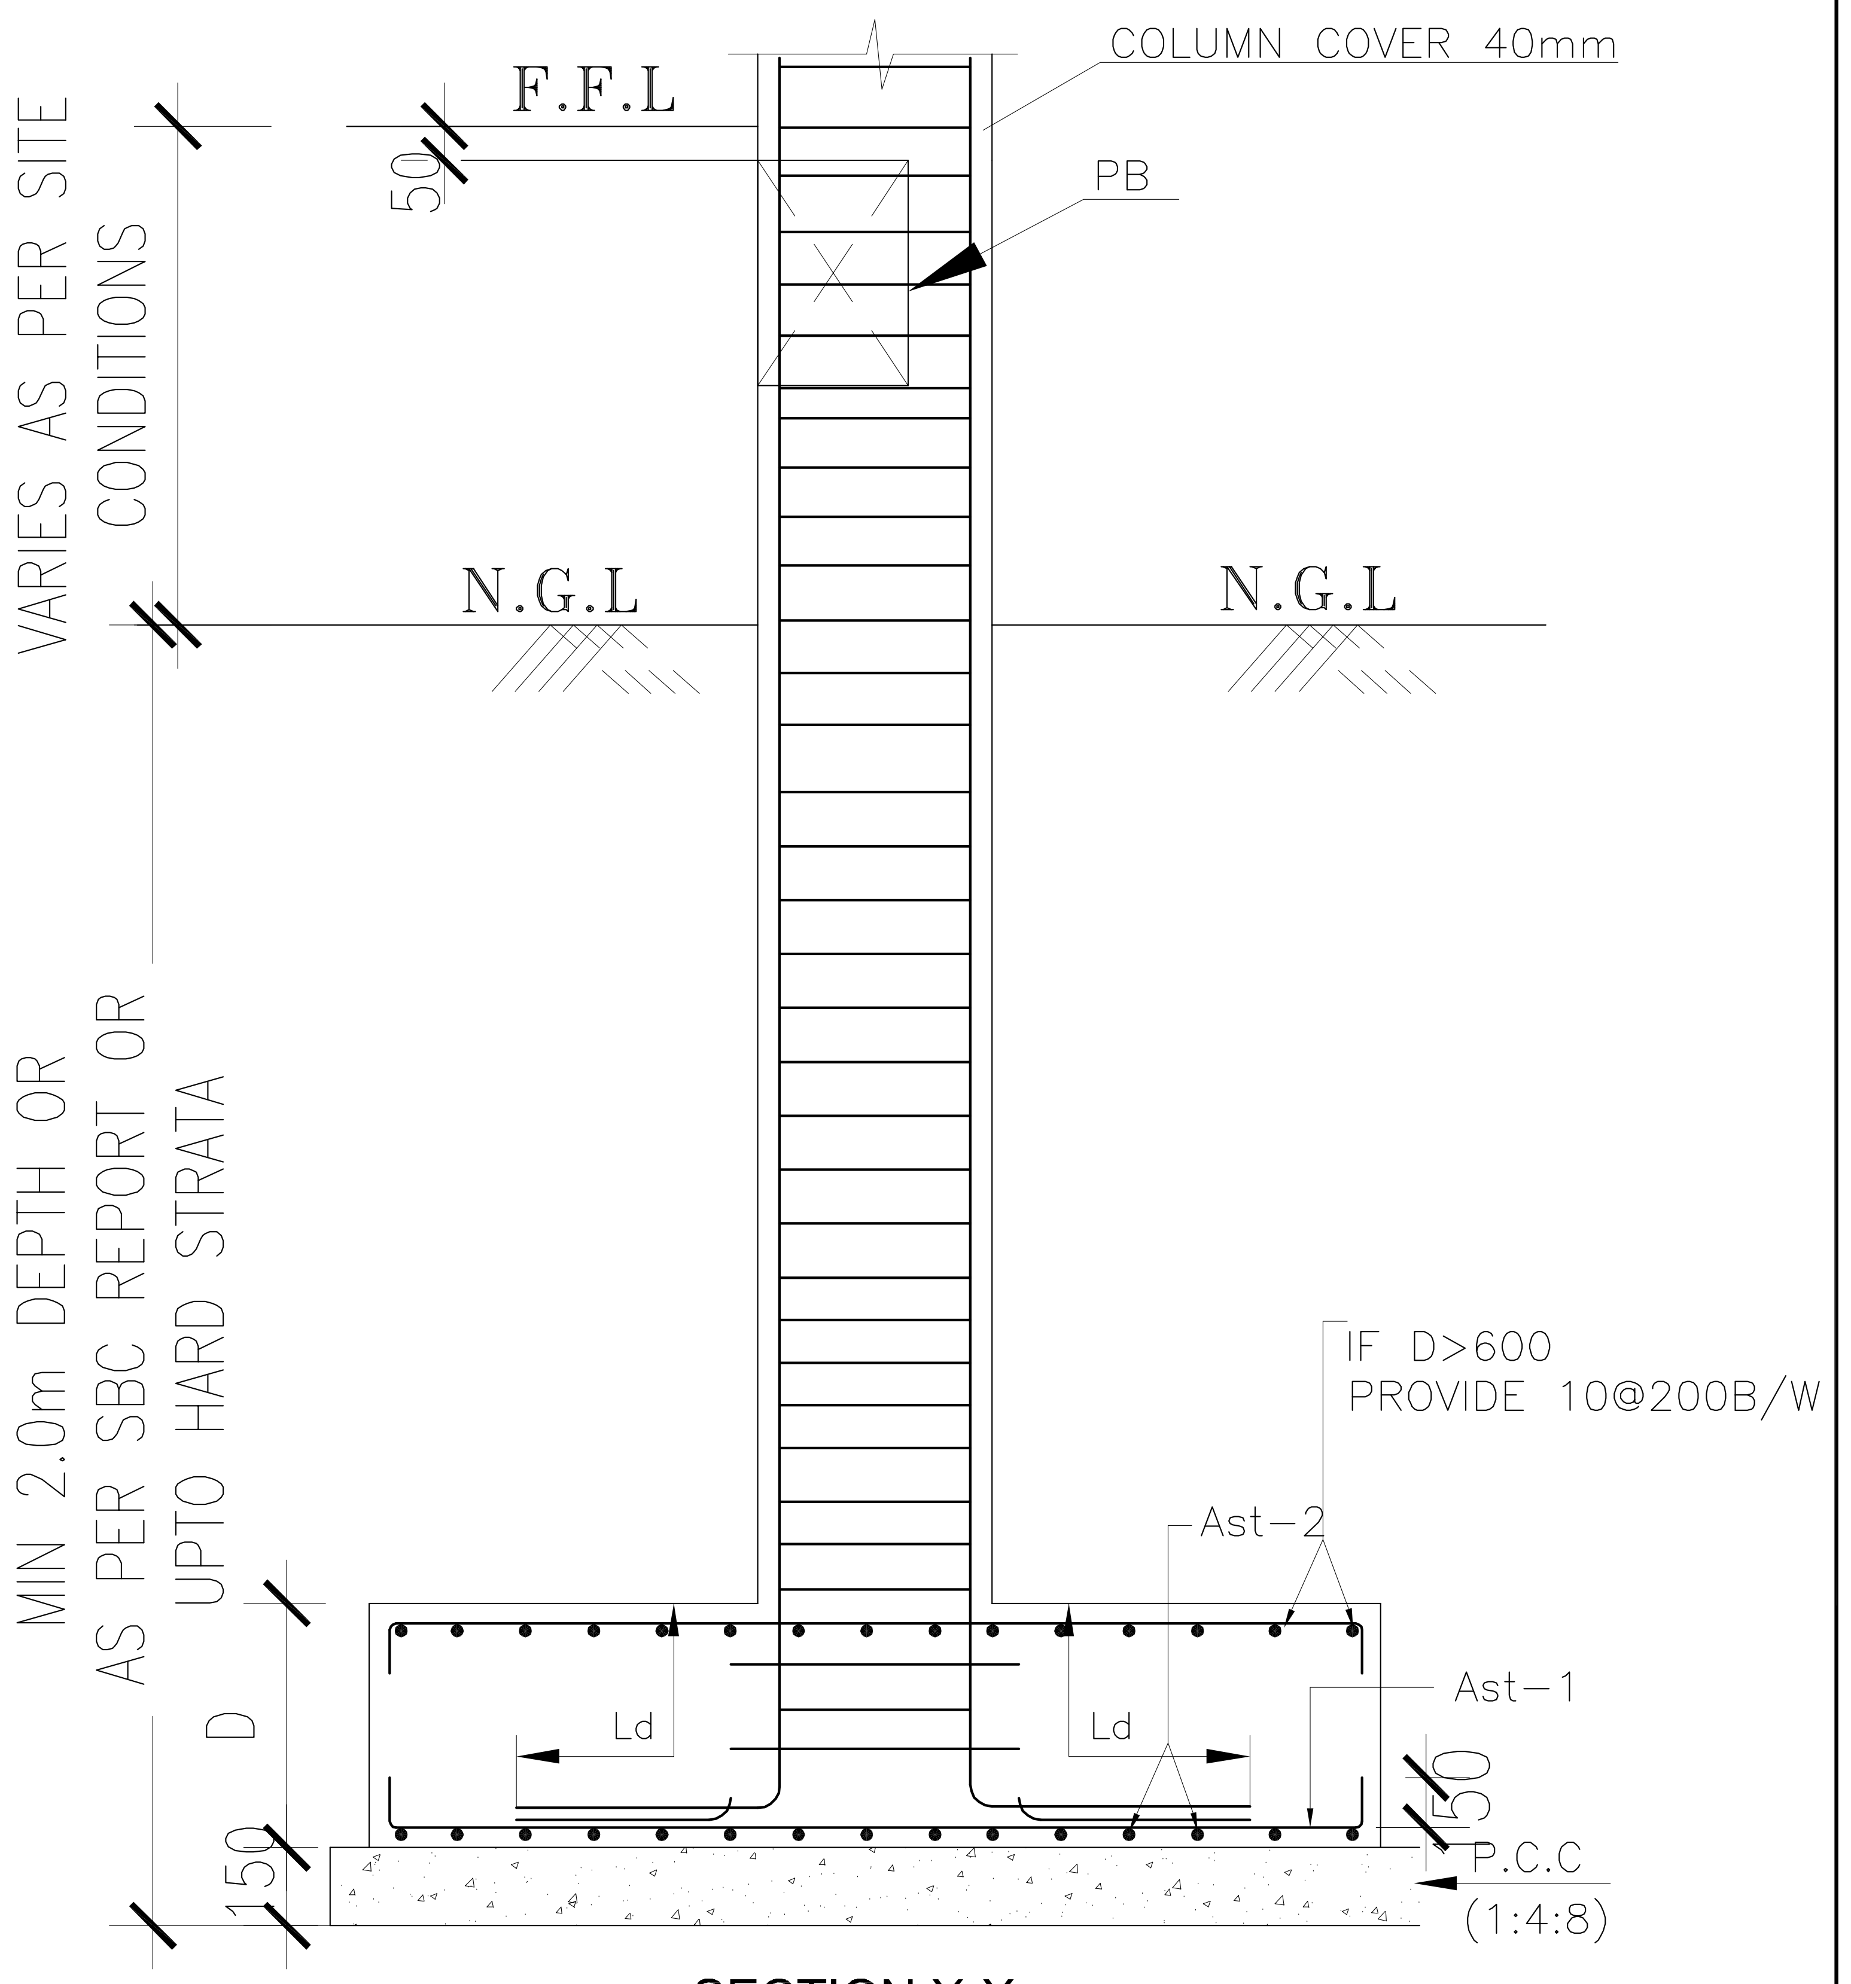
VARIES AS PER SITE CONDITIONS
MIN 2.0m DEPTH OR AS PER SBC REPORT OR UPTO HARD STRATA
F.F.L
50
COLUMN COVER 40mm
PB
N.G.L
N.G.L
IF D>600 PROVIDE 10@200B/W
Ast-2
Ast-1
Ld
Ld
D
150
50
P.C.C (1:4:8)

SECTION X-X

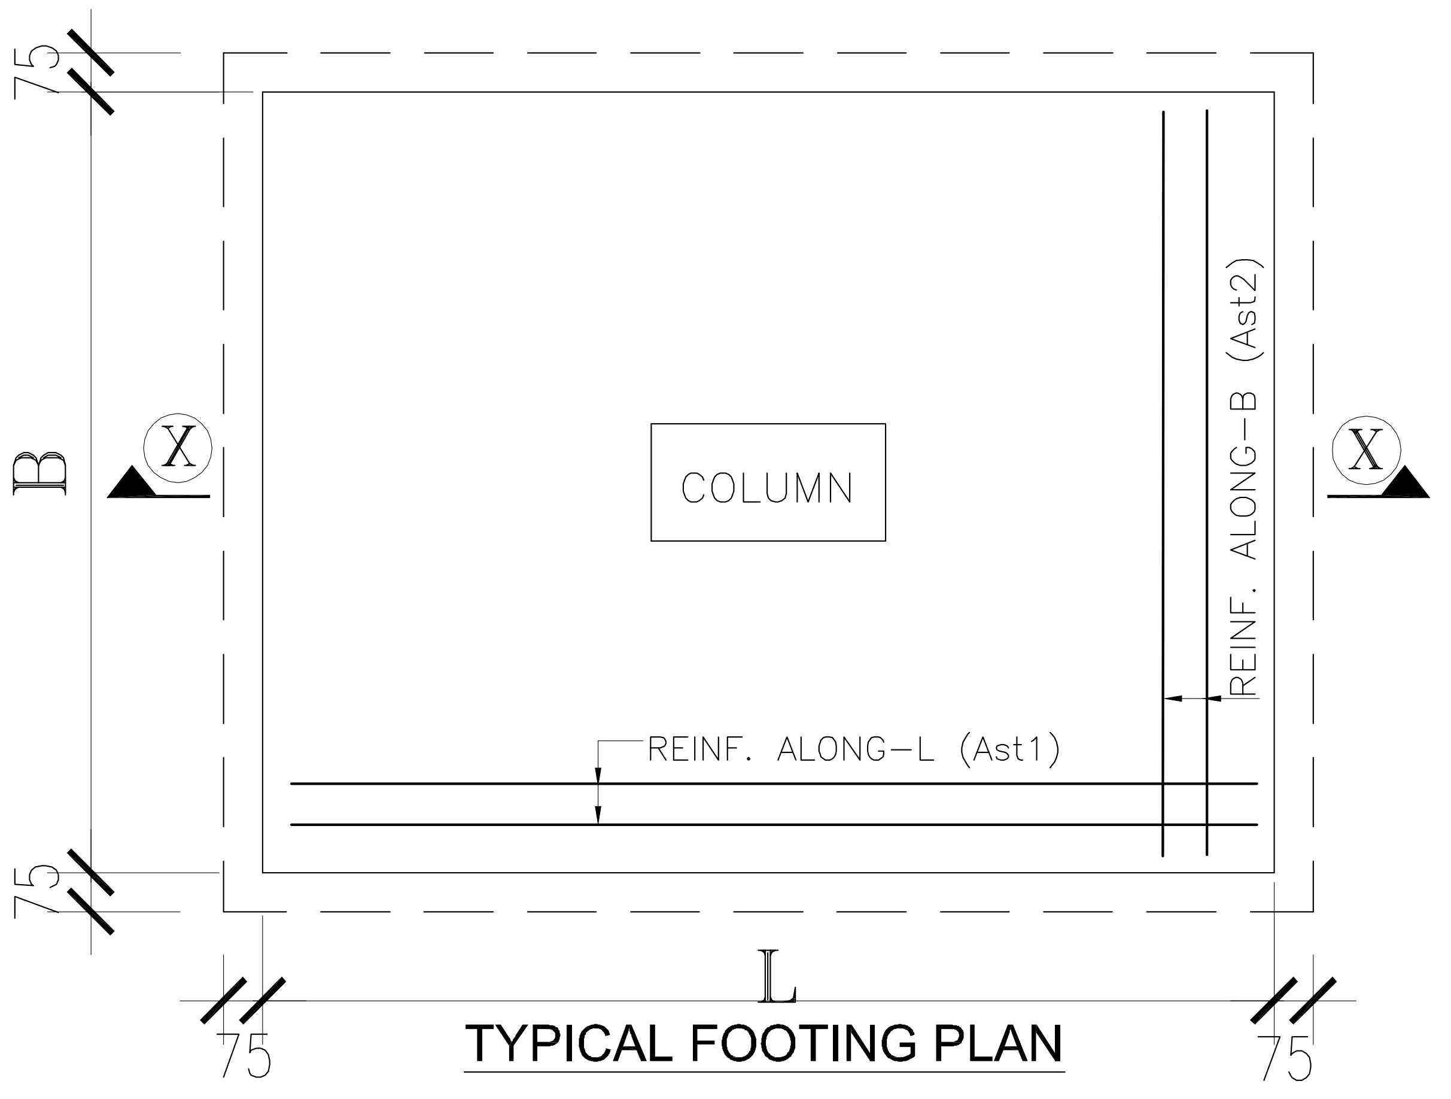

TYPICAL FOOTING PLAN

- THIS DRAWING SHALL BE READ IN CONJUNCTION WITH ALL RELEVANT ARCHITECTURAL, STRUCTURAL AND SERVICES DRAWINGS. ANY DISCREPANCY NOTICED SHALL BE BROUGHT TO THE ATTENTION OF THE CONSULTANTS AND RESOLVED AS SOON AS POSSIBLE BUT ALWAYS PRIOR TO

ARCHITECTURAL CONSULTANT:

also. design
a little story of design

STRUCTURAL& MEP CONSULTANTS

JASHRITHA ASSOCIATES
AND MEP PLANNERS
4th FLOOR(4B), HIG 129, KPHB COLONY, KUKATPALLY,
(SUB BRANCH:PR NAGAR ERRAGADDA.)
HYDERABAD 500072, TELANGANA, INDIA
Phone : 9700441106.
E-mail : jashreyansh.consultatns@gmail.com
& jashritha.mep@gmail.com

PROJECT:

ANKURA HOMES_THE WOODS
AT KEESARAGUTTA

DRAWING TITLE:

1625_EAST VILLA
COLUMN & FOOTING
SCHEDULE

| | |
|---|---|
| DESIGN ENGG : AJAY | APPROVED : |
| SCALE : NTS | DRAWN : PK |
| DATE : 19-09-2026 | CHECKED : PRADEEP |
| DRAWING NO: SD-02 | REV.NO: |

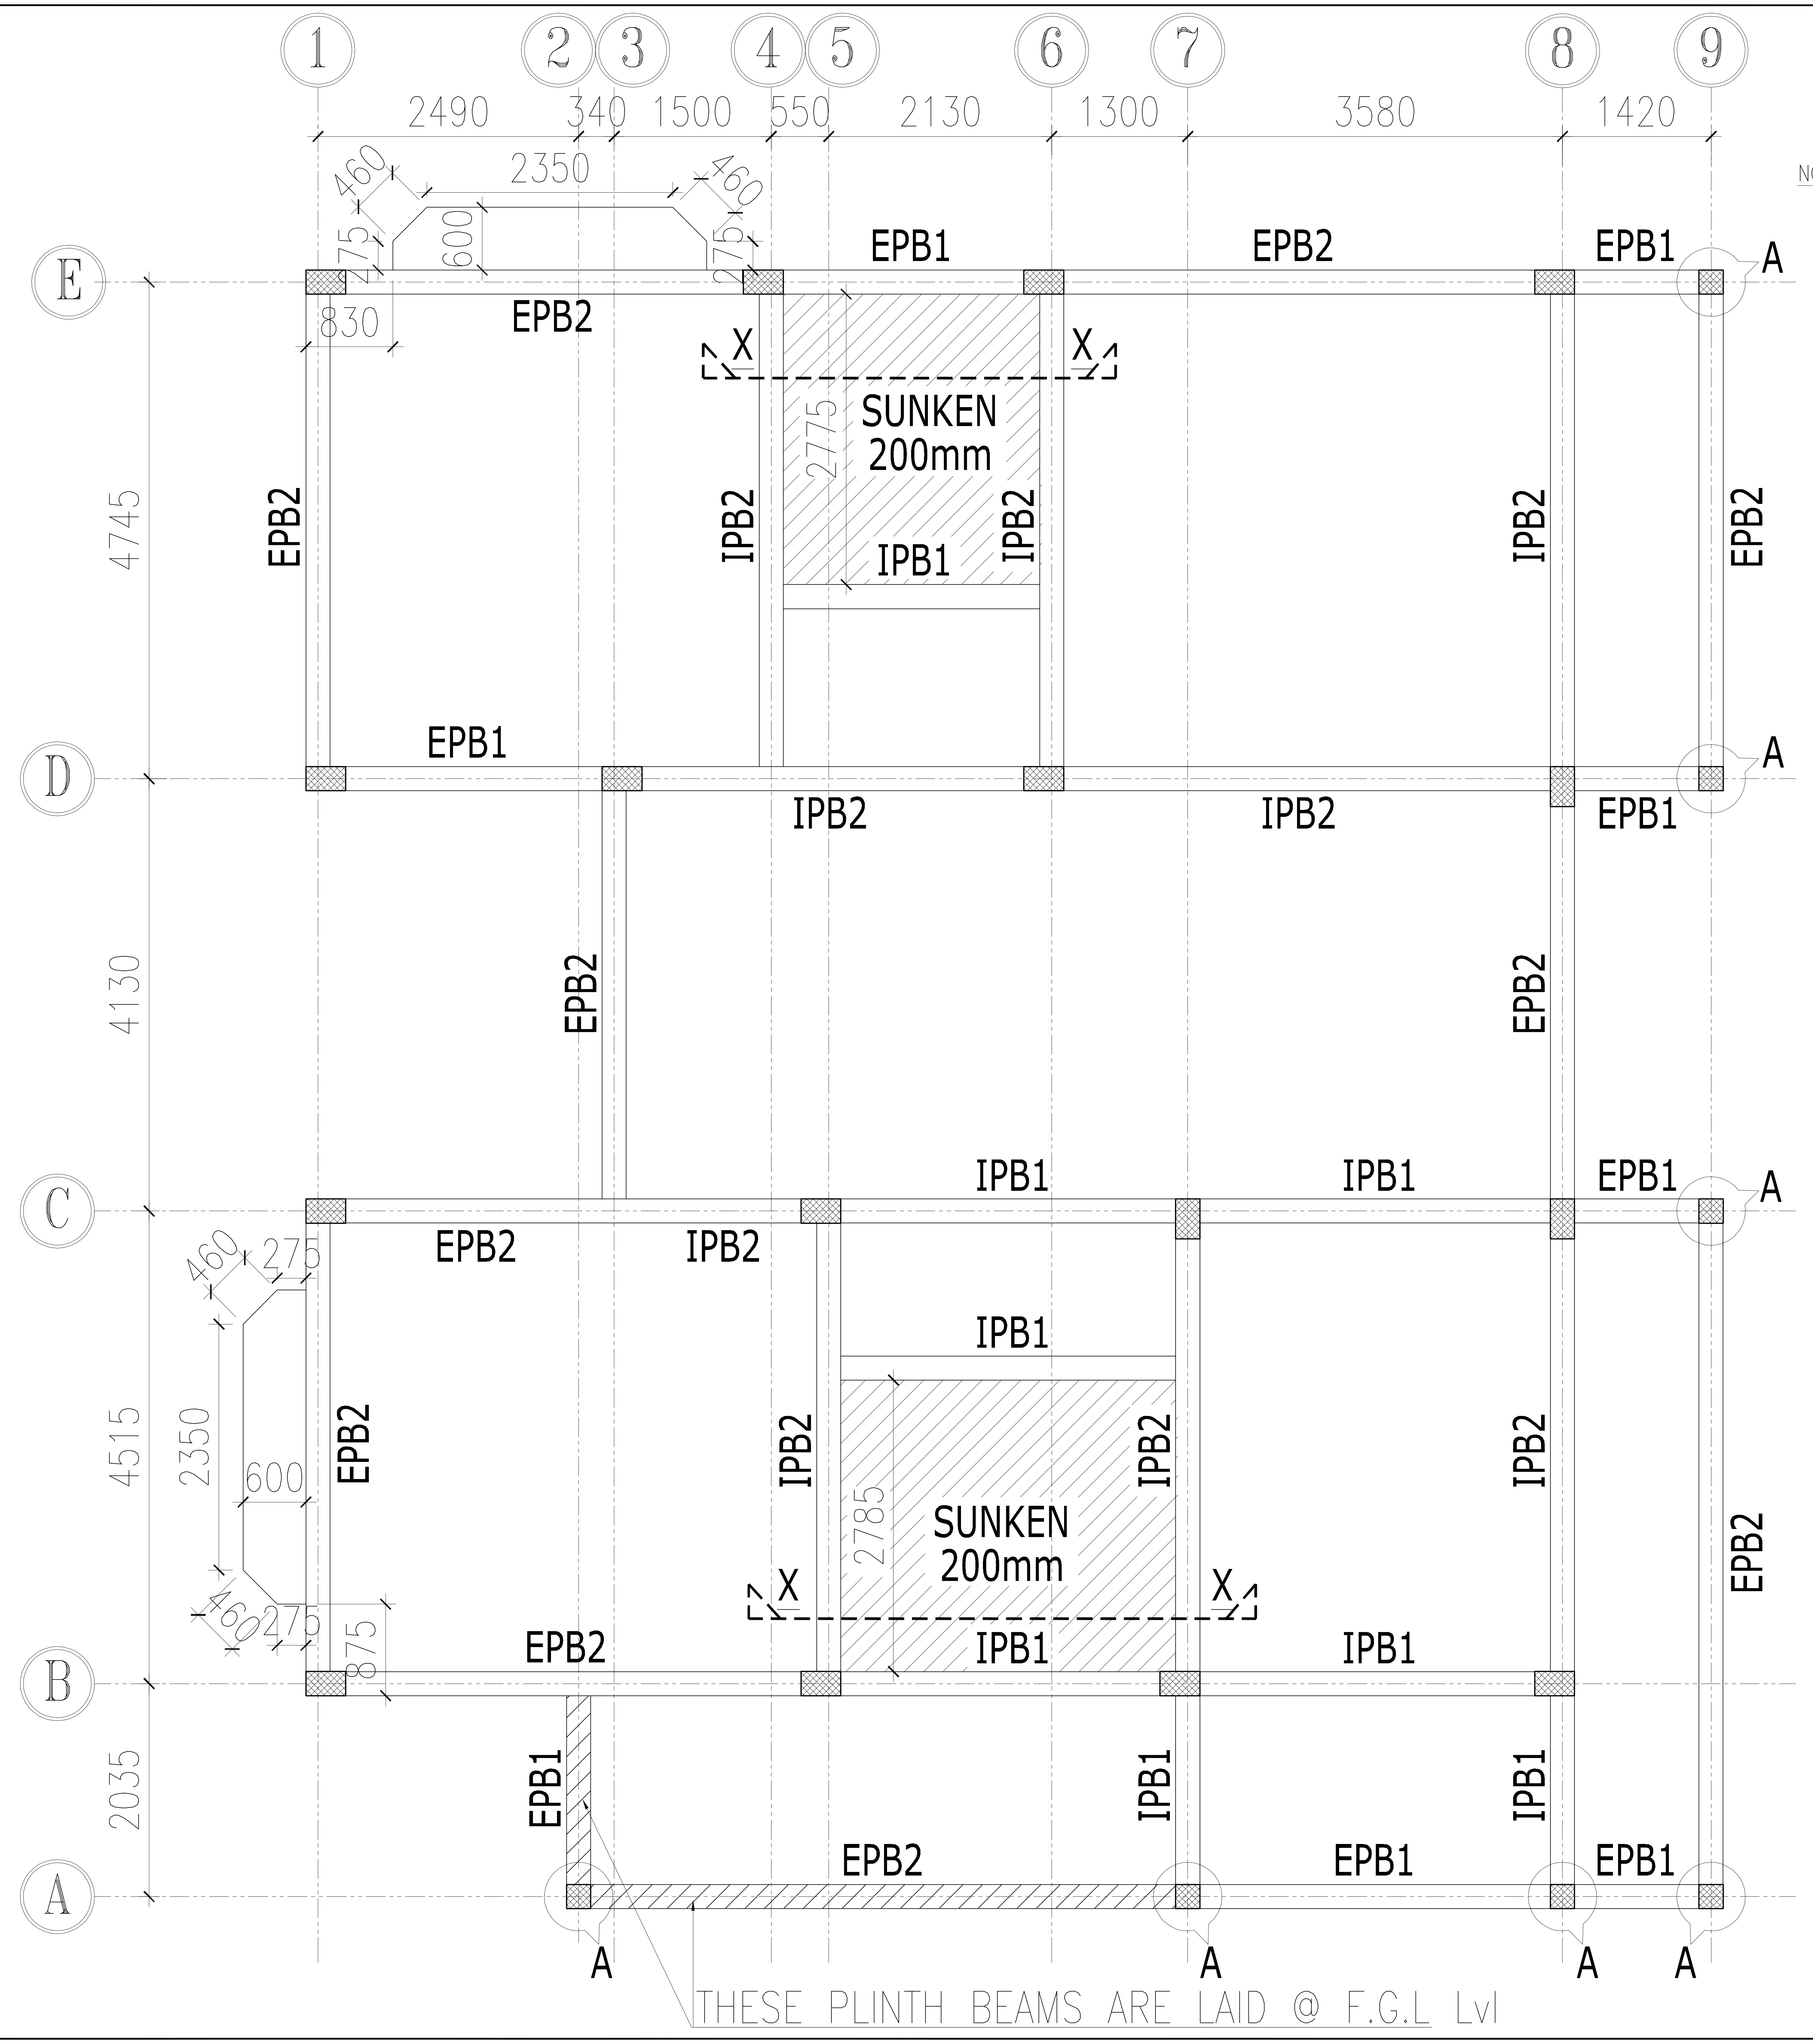

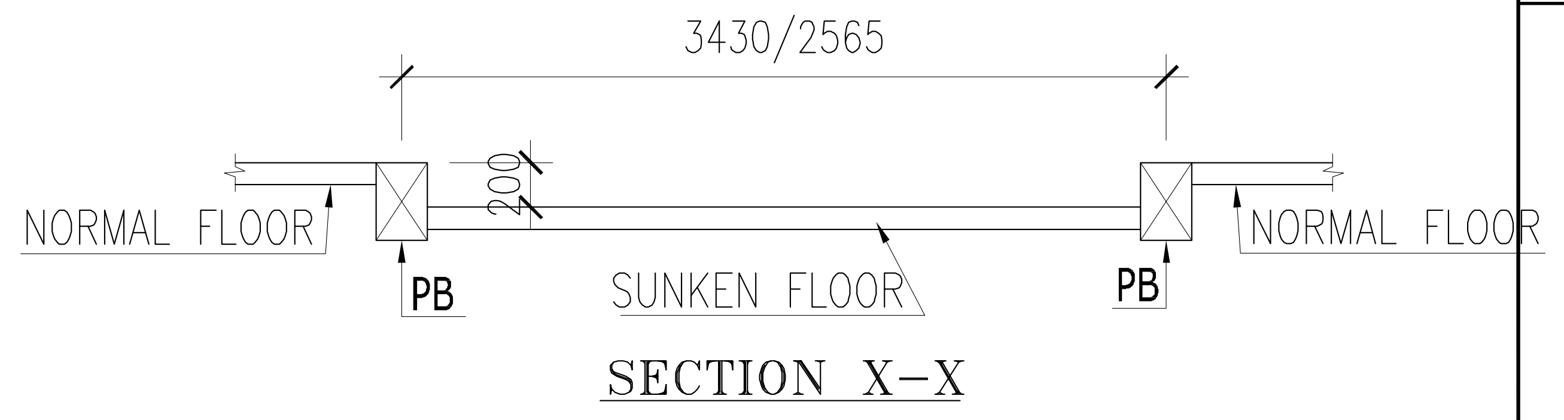

SECTION X-X

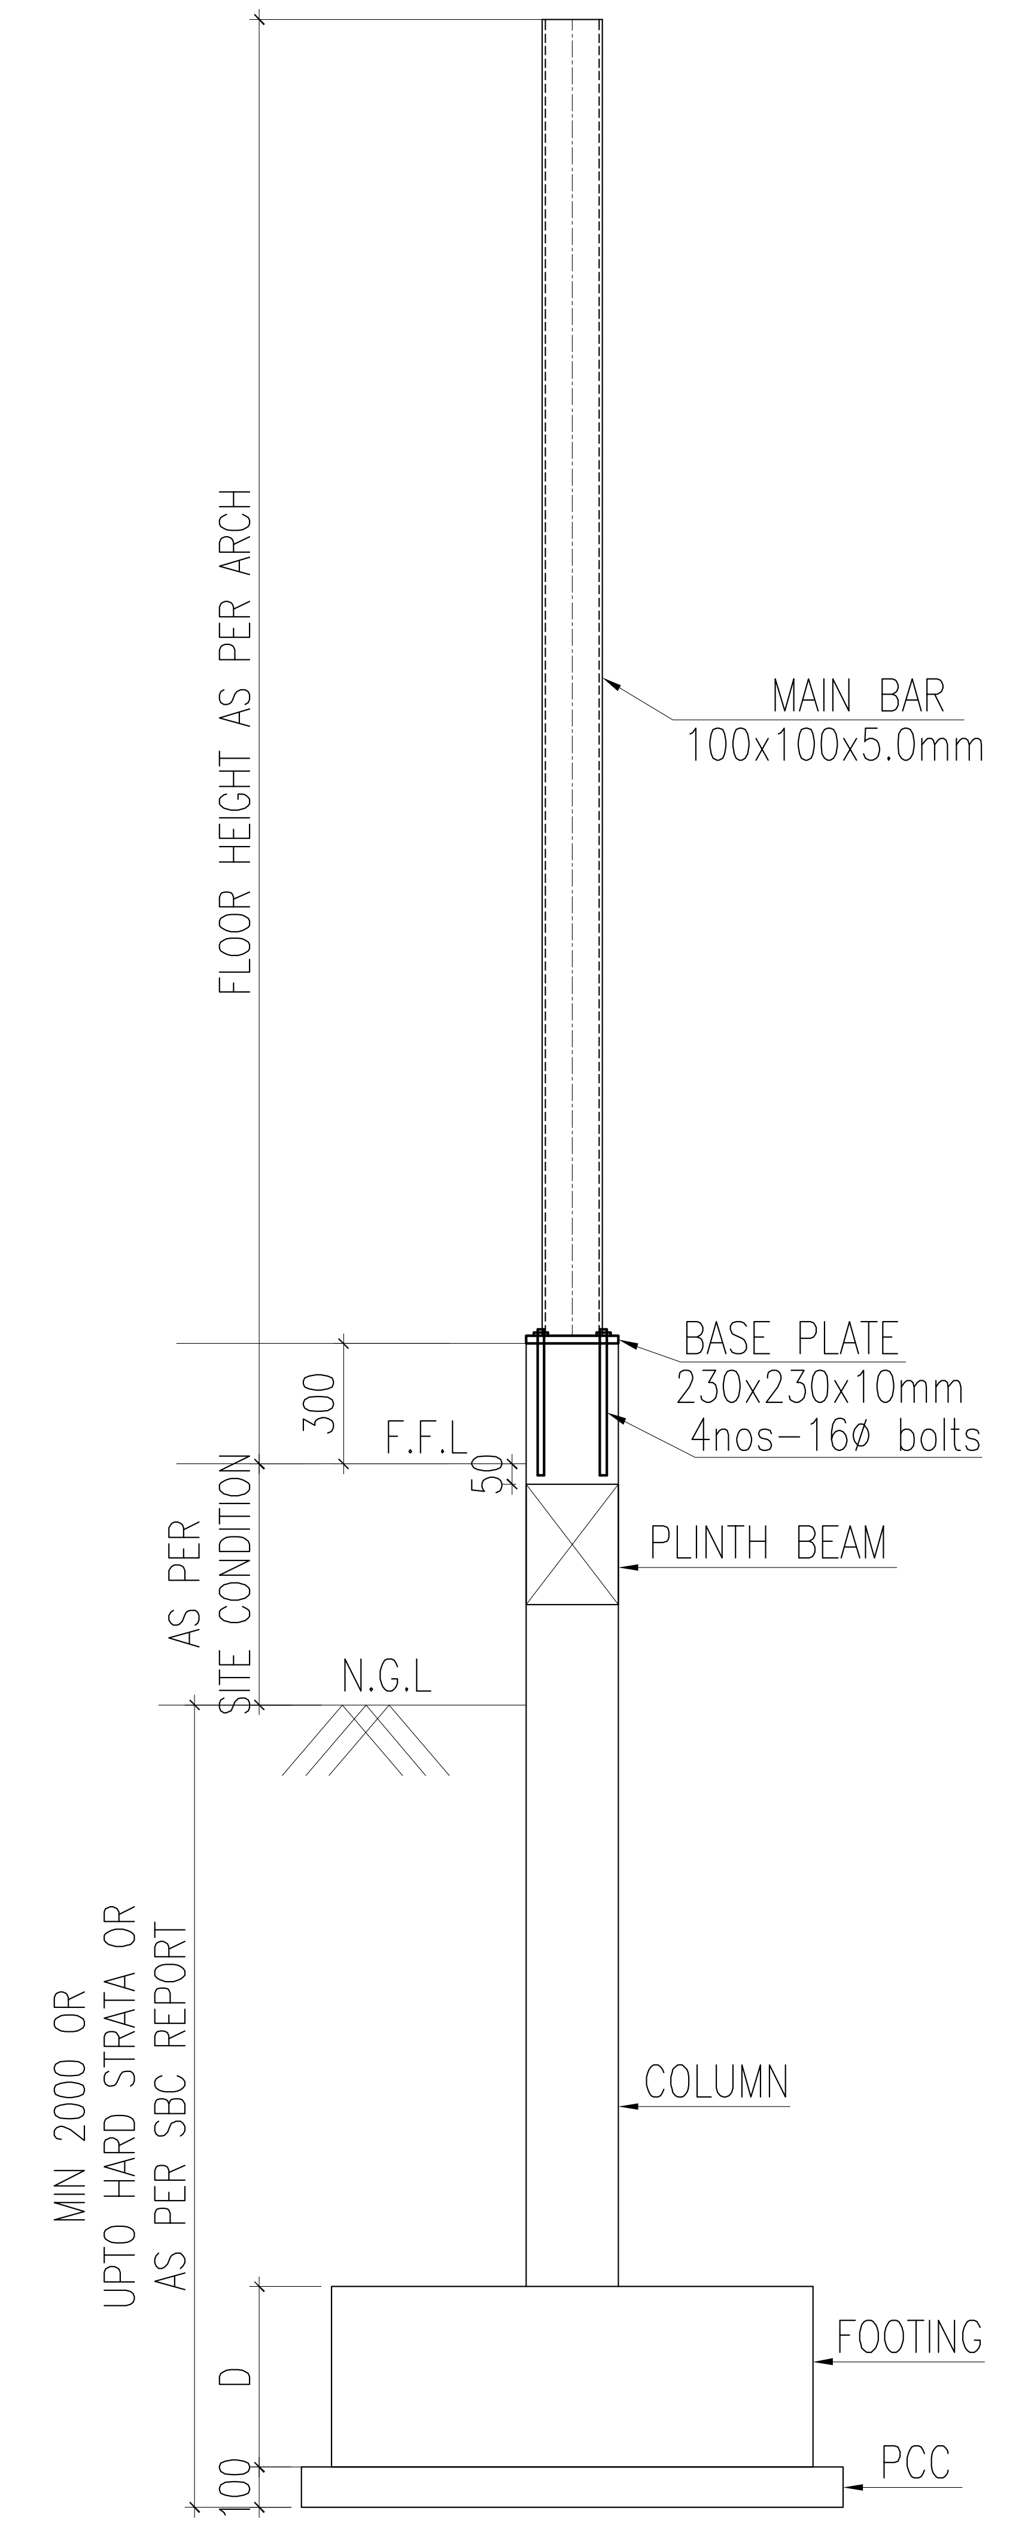

DETAIL-A

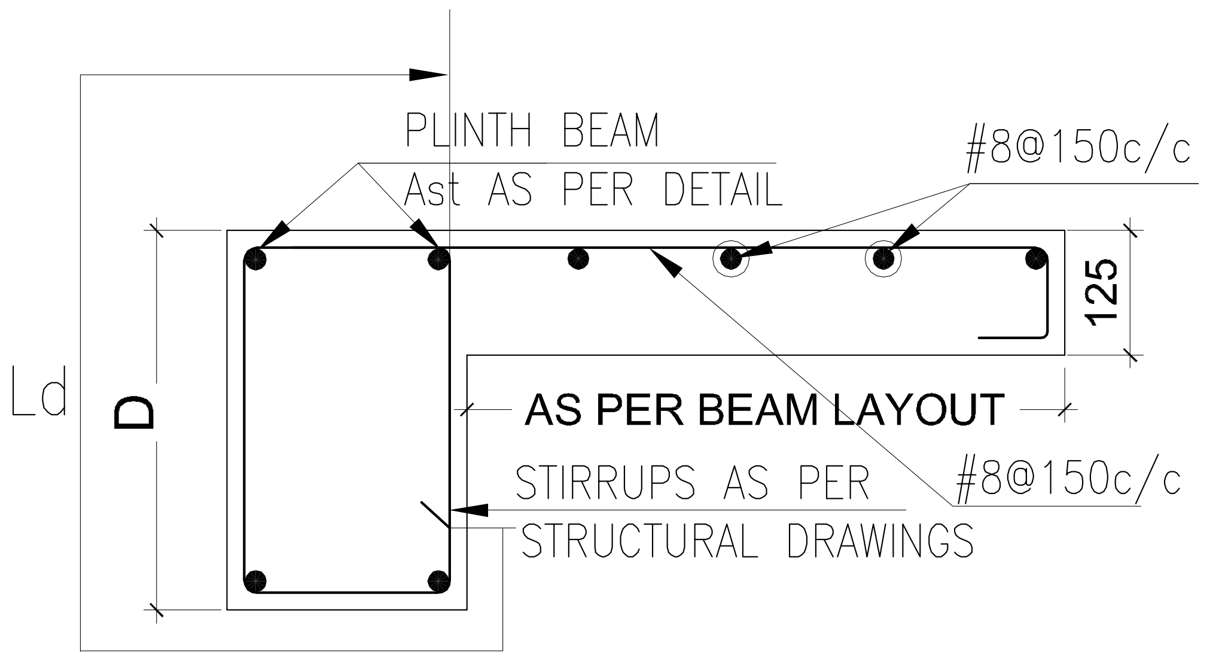

TYPICAL
SLAB PROJECTION DETAILS

- THIS DRAWING SHALL BE READ IN CONJUNCTION WITH ALL RELEVANT ARCHITECTURAL, STRUCTURAL AND SERVICES DRAWINGS. ANY DISCREPANCY NOTICED SHALL BE BROUGHT TO THE ATTENTION OF THE CONSULTANTS AND RESOLVED AS SOON AS POSSIBLE BUT ALWAYS PRIOR TO

DIRECTION:

N

ARCHITECTURAL CONSULTANT:

also. design
a little story of design

STRUCTURAL& MEP CONSULTANTS

JASHRITHA ASSOCIATES
AND MEP PLANNERS
4th FLOOR(4B), HIG 129, KPHB COLONY, KUKATPALLY,
(SUB BRANCH:PR NAGAR ERRAGADDA.)
HYDERABAD 500072, TELANGANA, INDIA
Phone : 9700441106.
E-mail : jashreyansh.consultatns@gmail.com
& jashritha.mep@gmail.com

PROJECT:

ANKURA HOMES_THE WOODS
AT KEESARAGUTTA

DRAWING TITLE:

1625_EAST VILLA
PLINTH BEAM LAYOUT

| | |
|---|---|
| DESIGN ENGG : AJAY | APPROVED : |
| SCALE : NTS | DRAWN : PK |
| DATE : 23-09-2026 | CHECKED : PRADEEP |
| DRAWING NO: SD-03 | REV.NO: 01 |

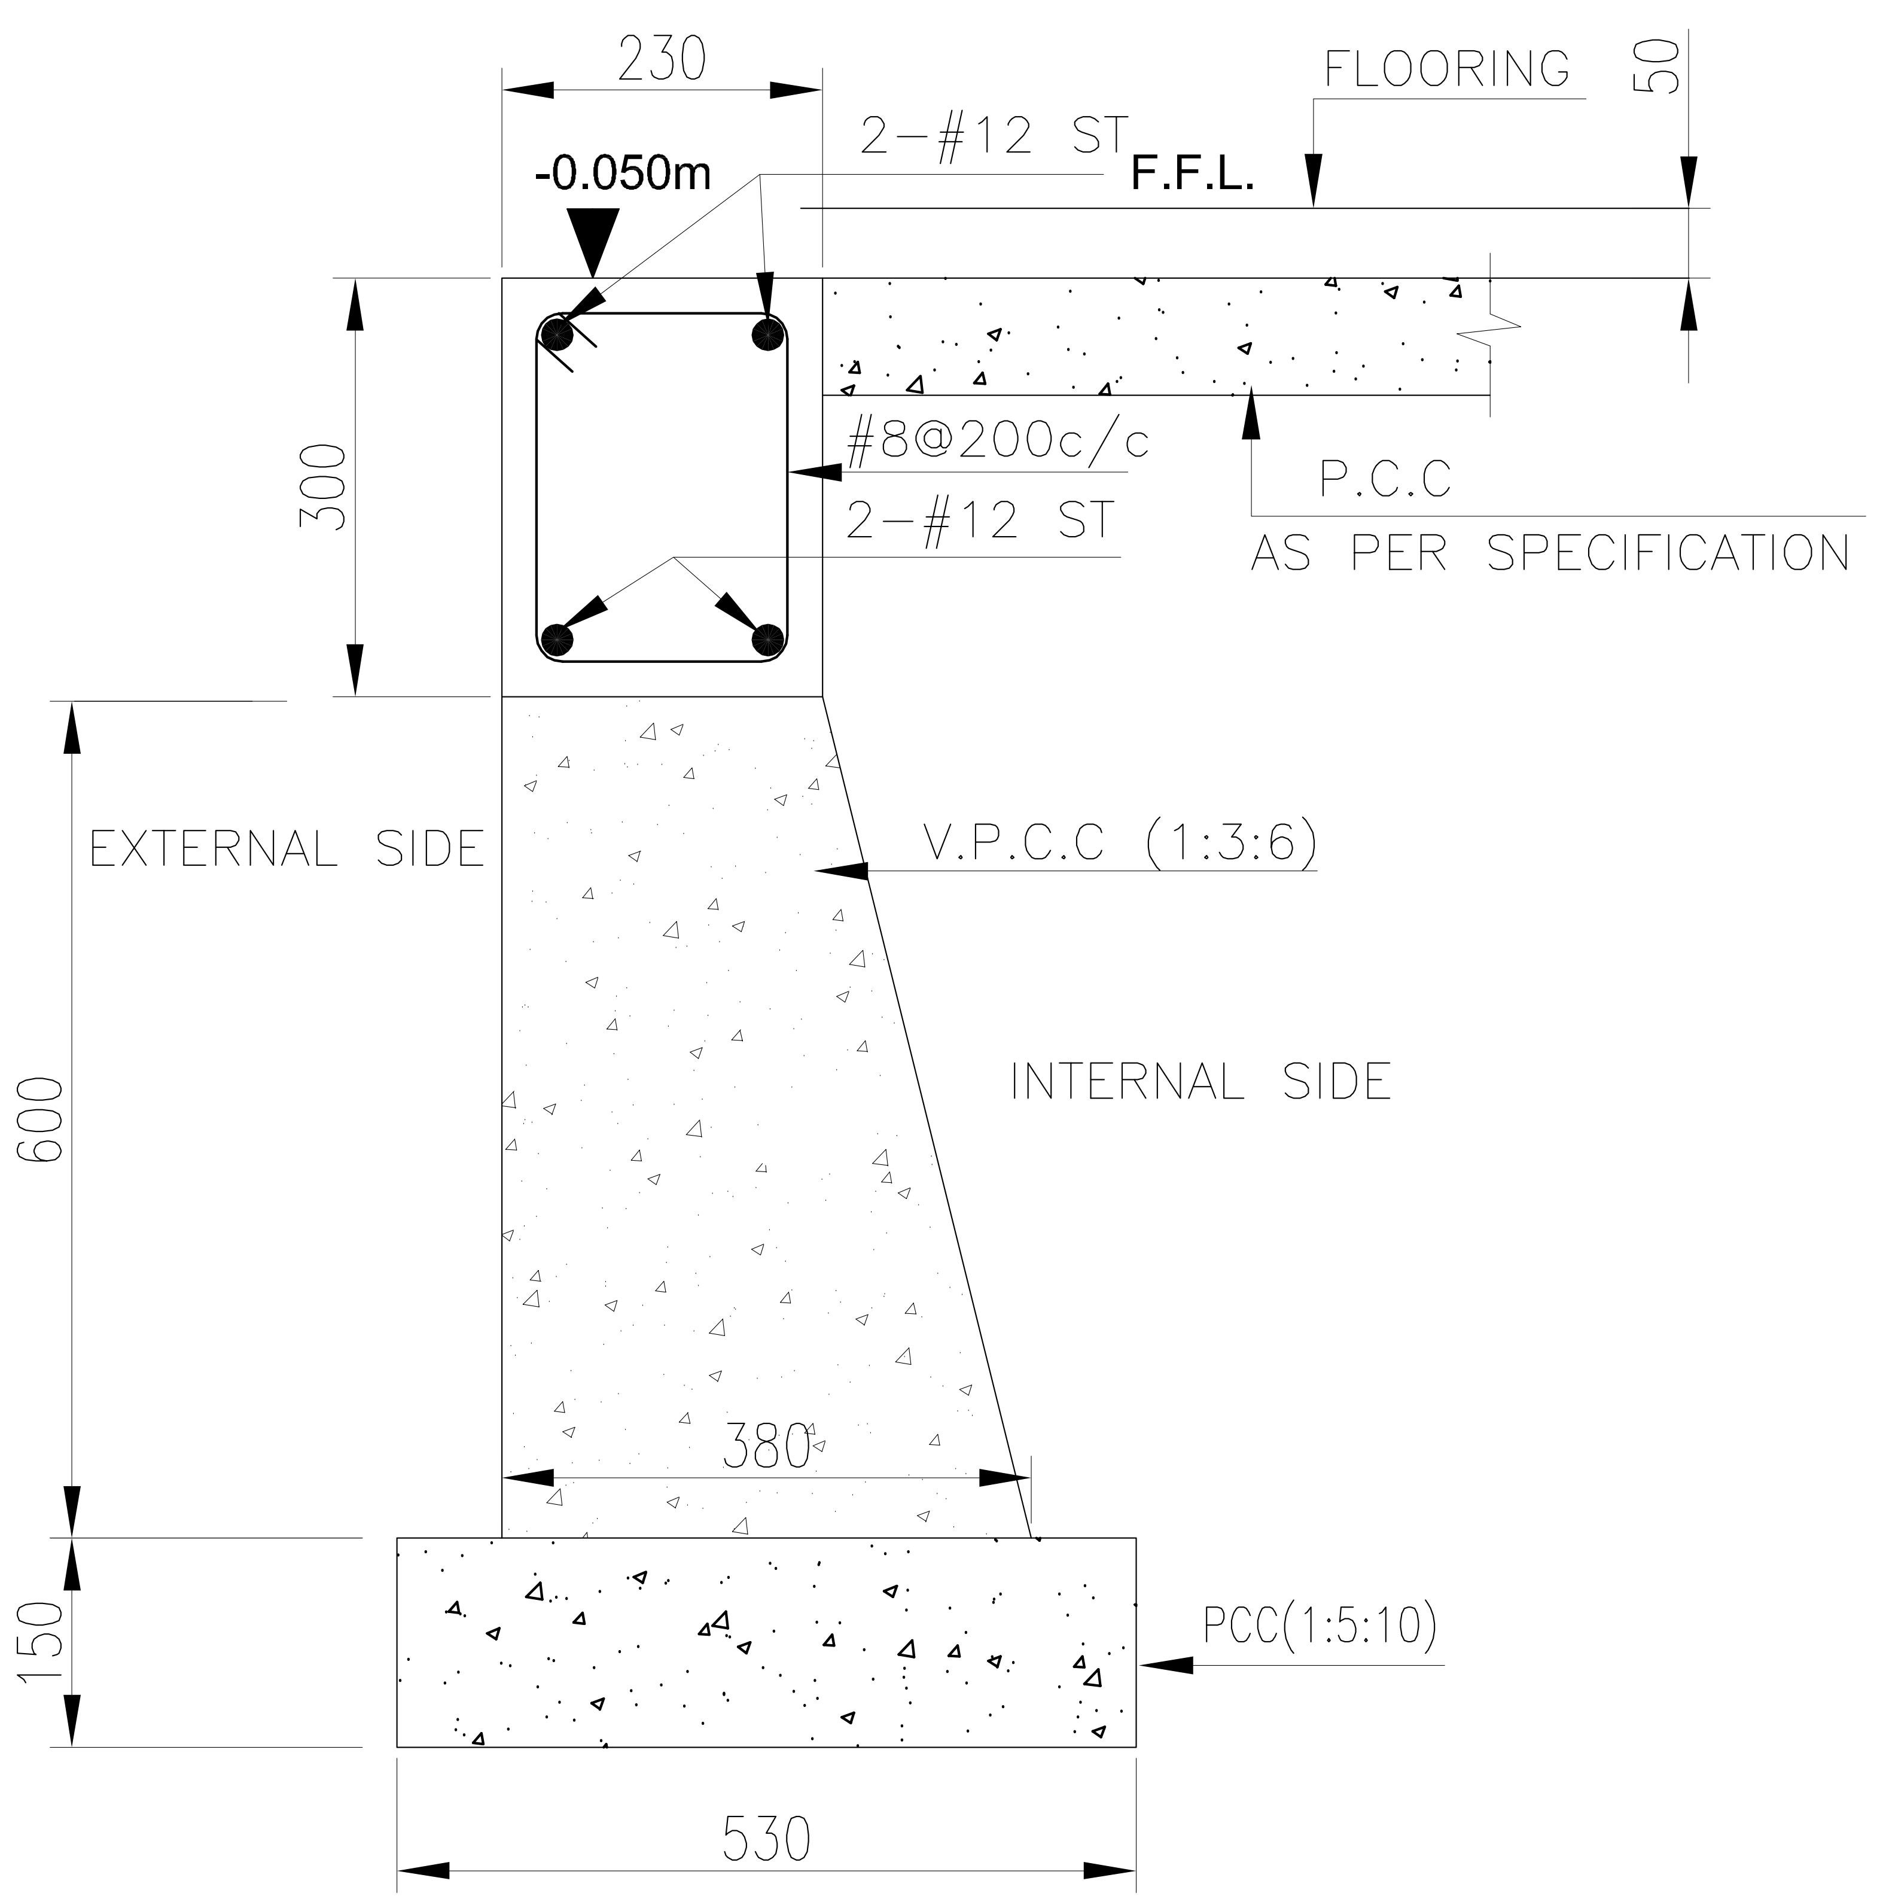

EPB1

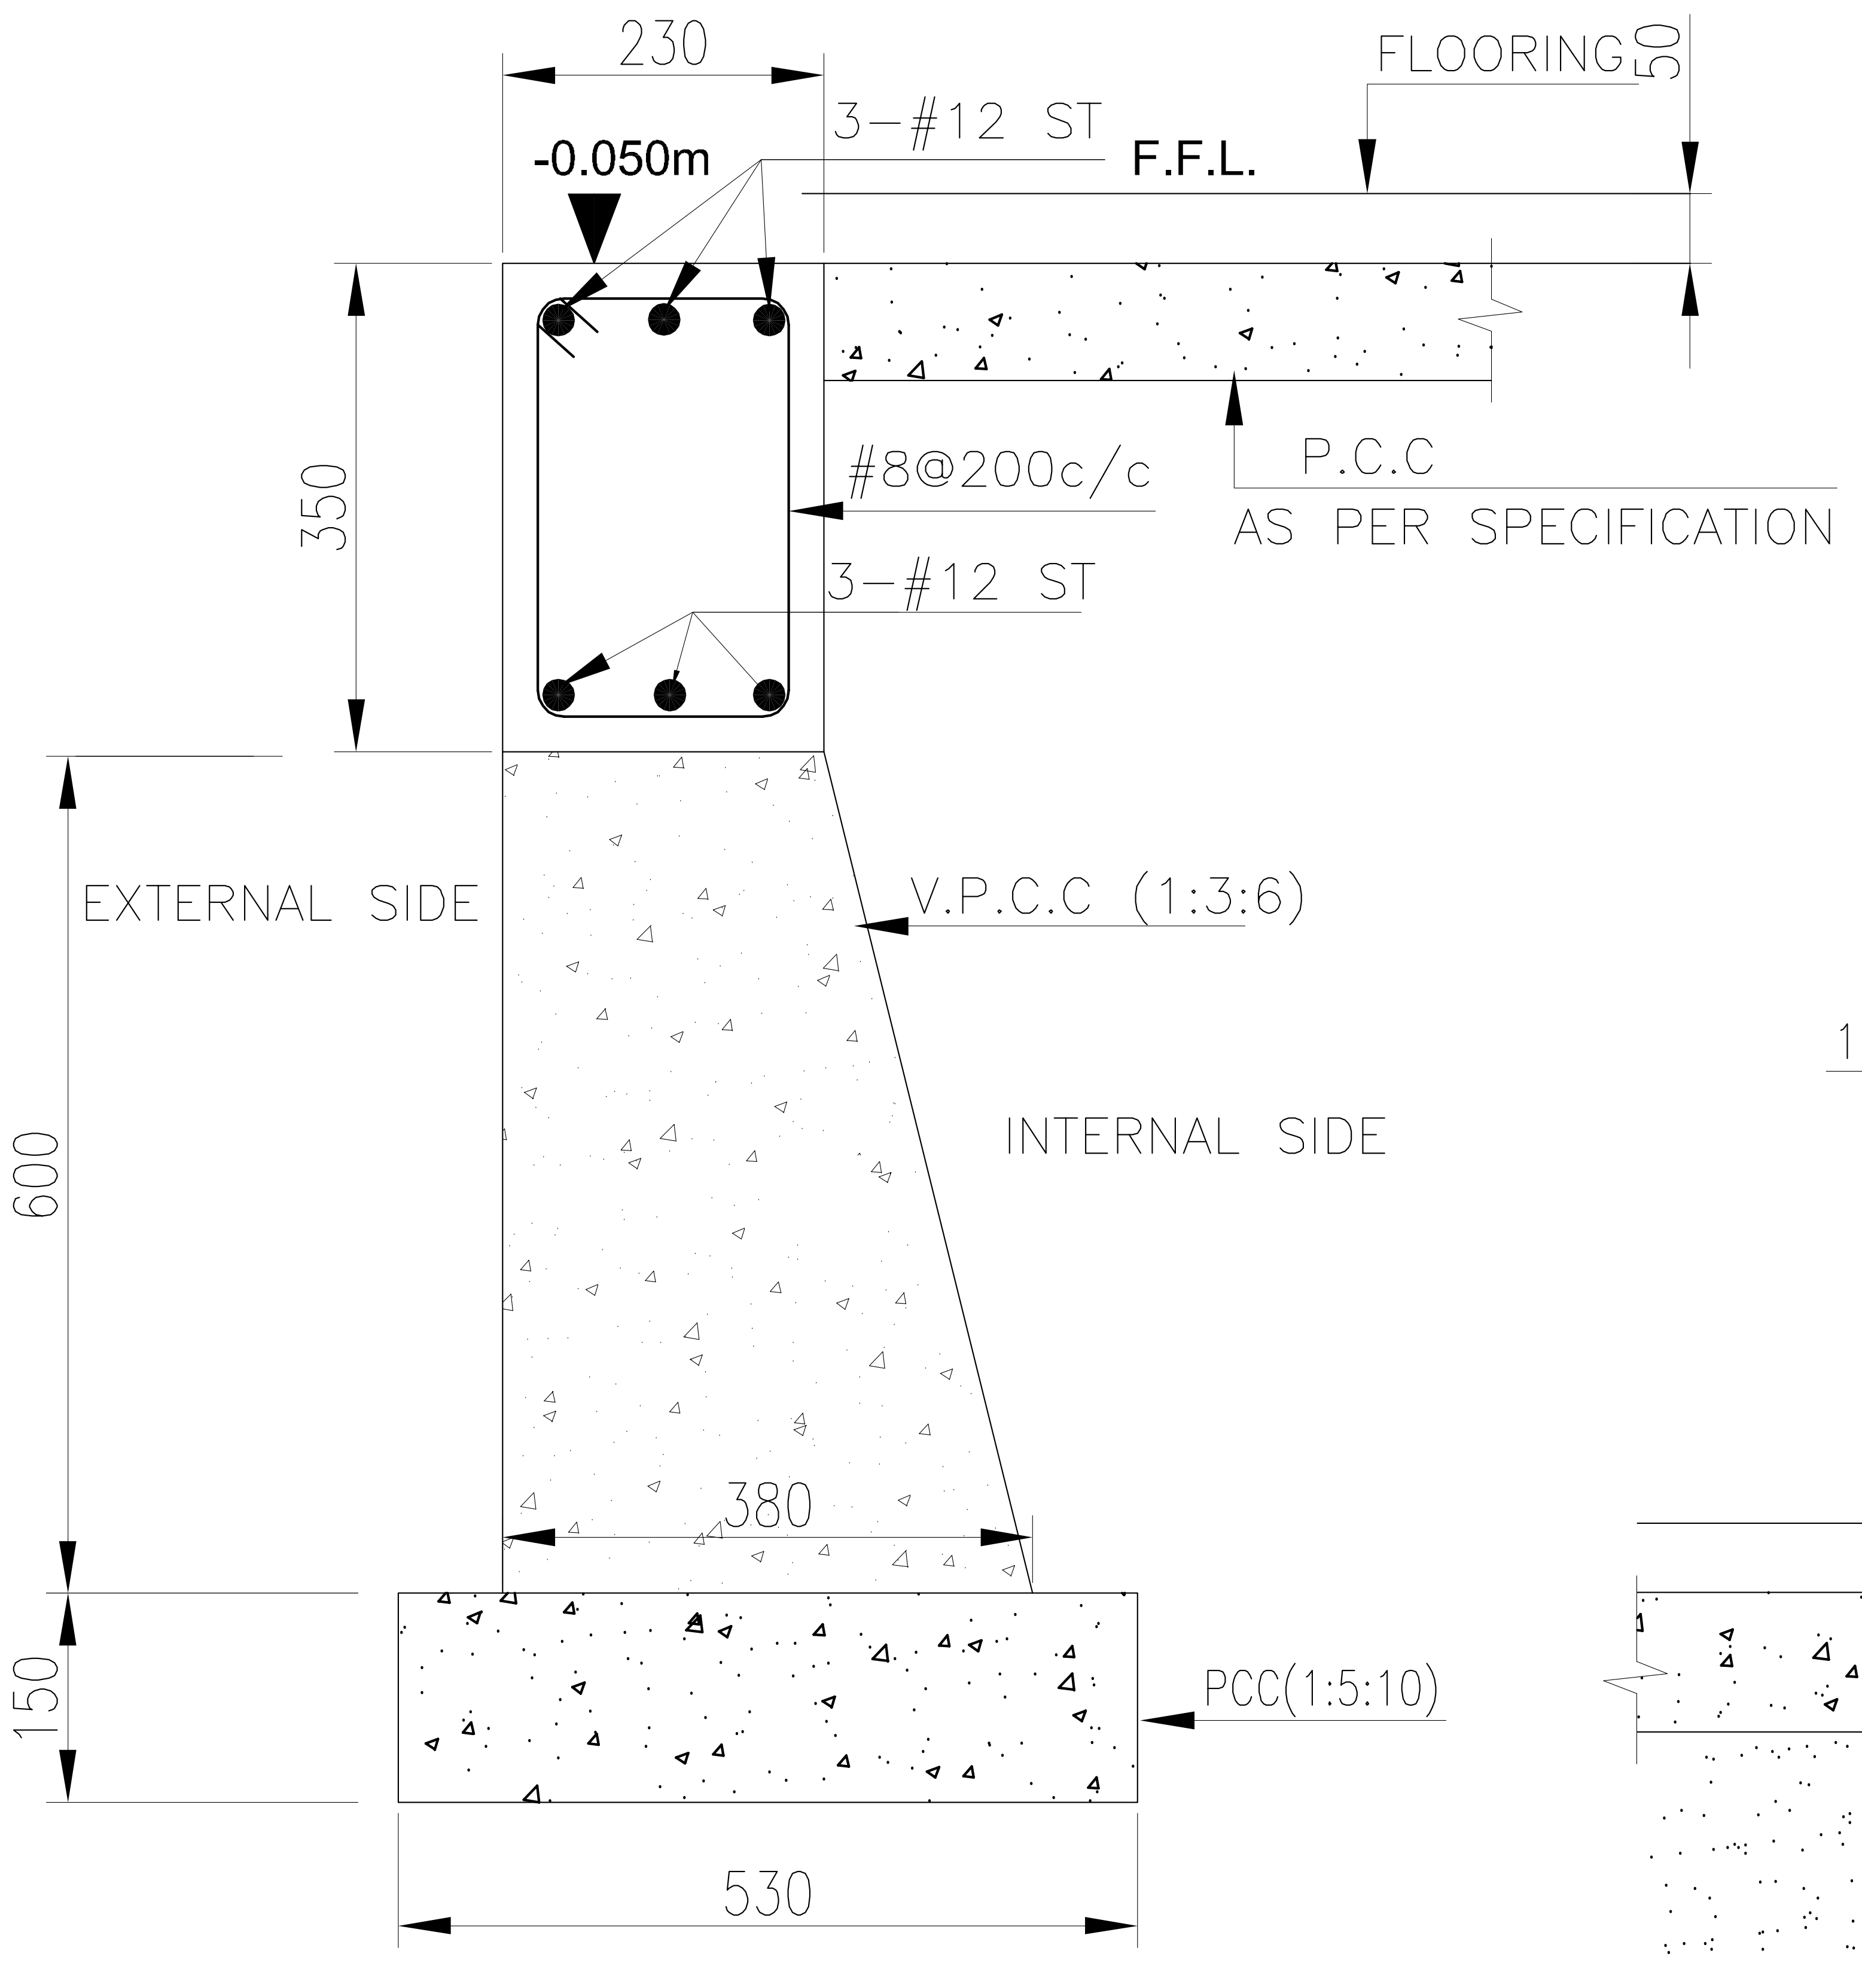

EPB2

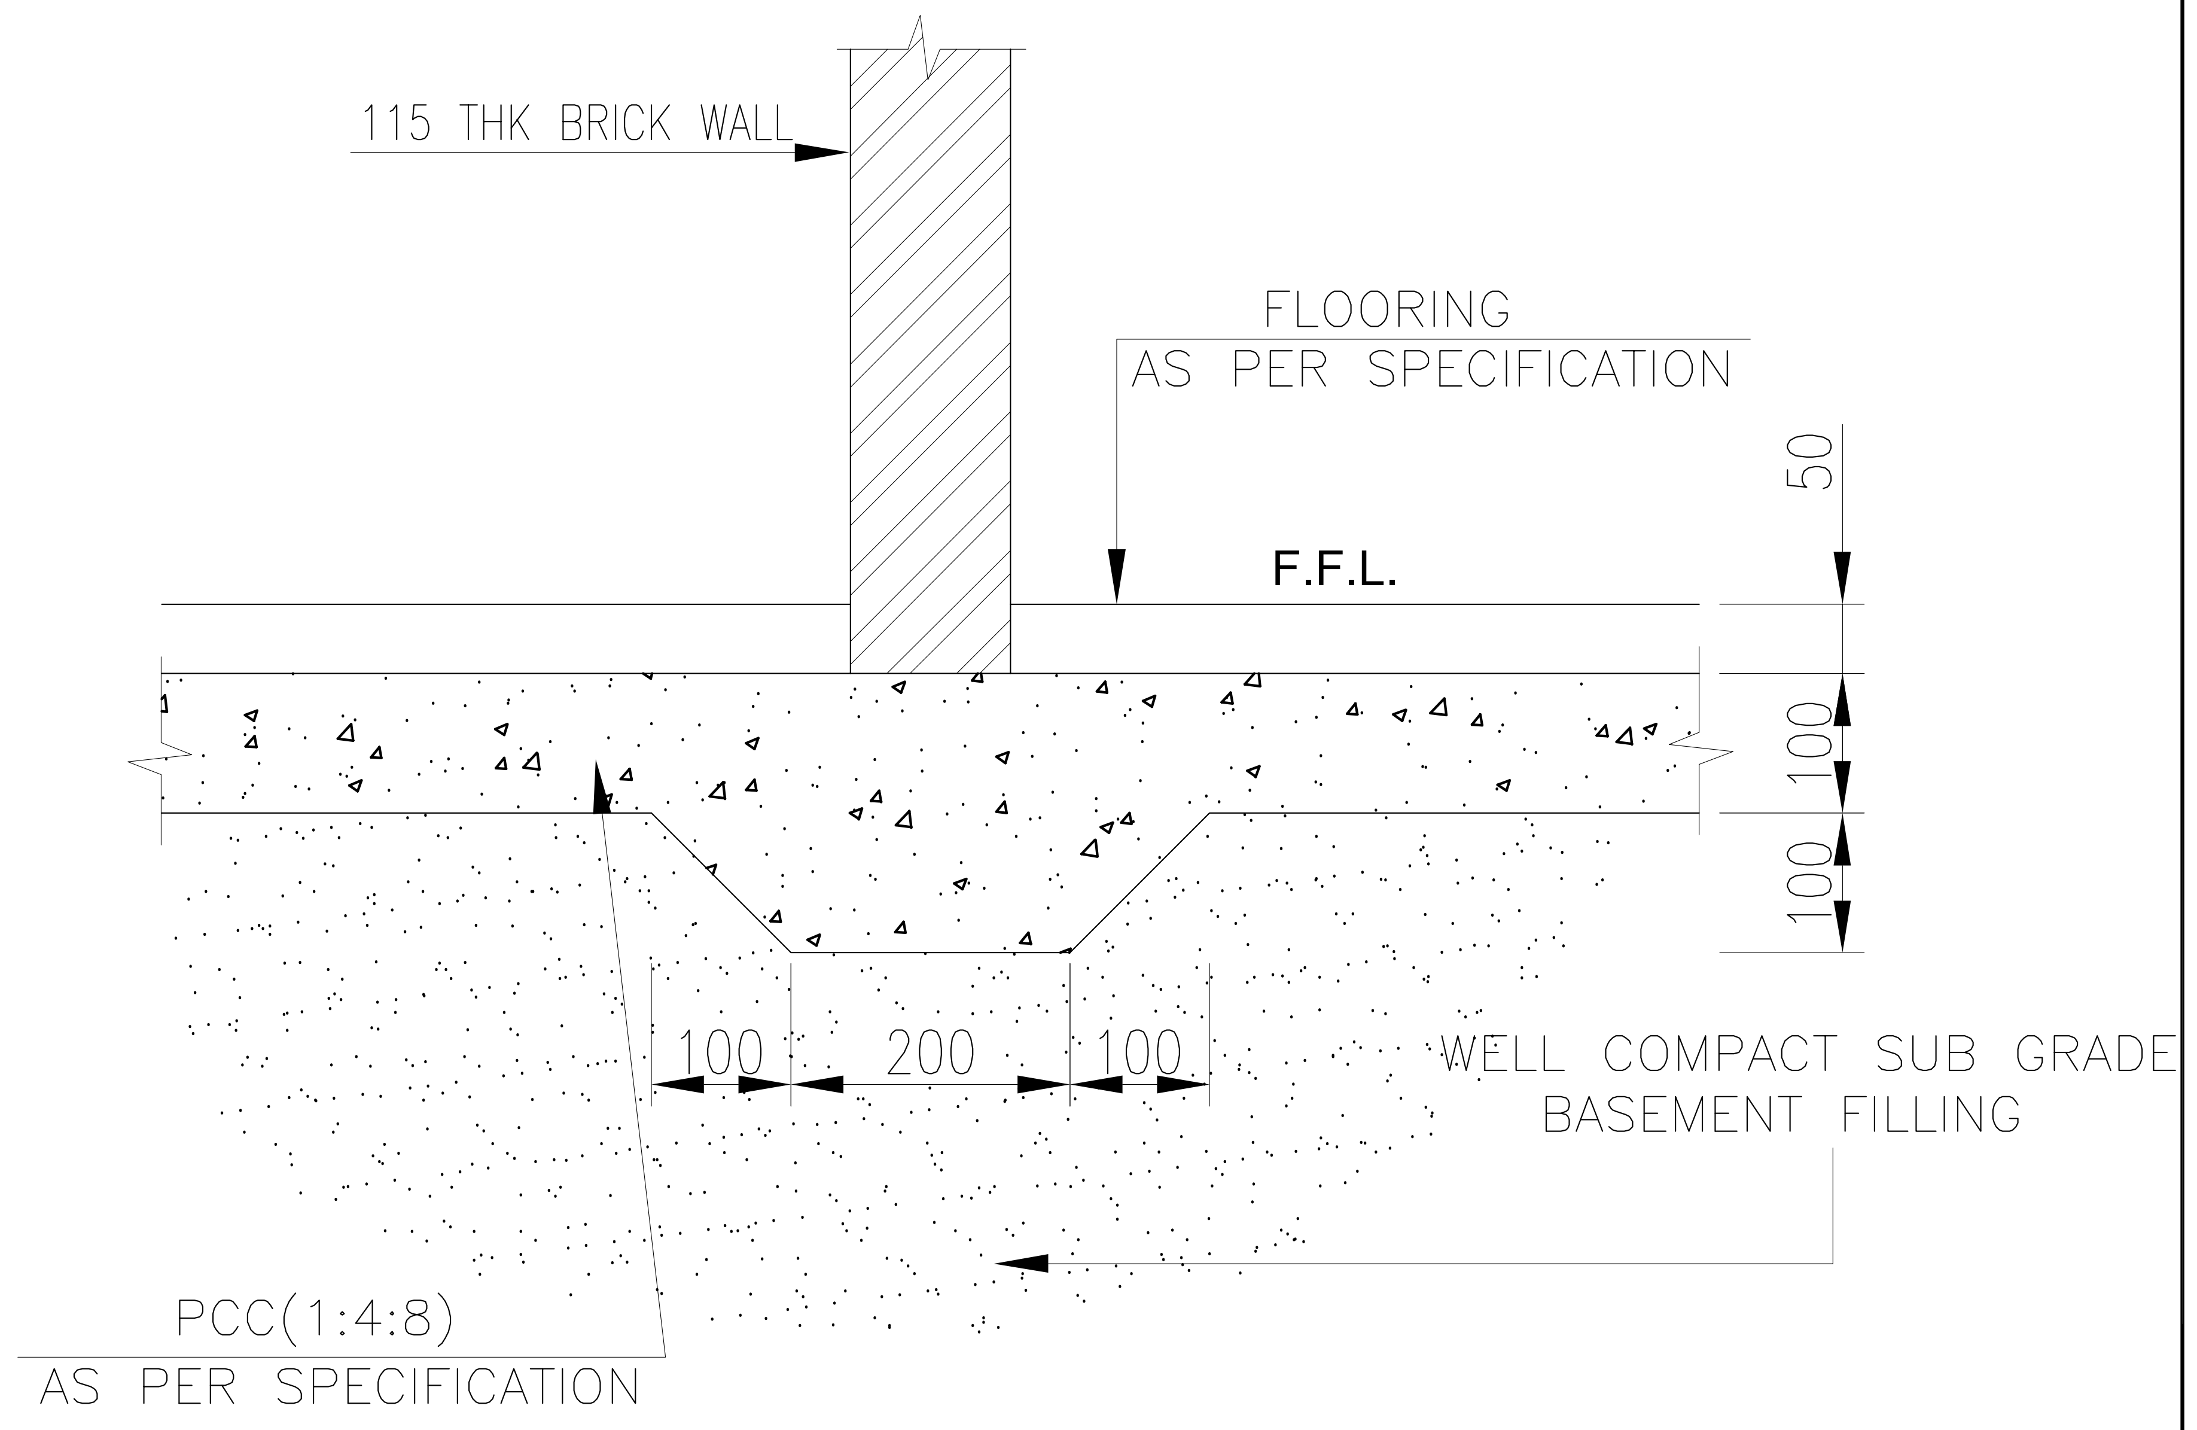

## FOUNDATION DETAIL UNDER 115mm THICK BRICK WALL

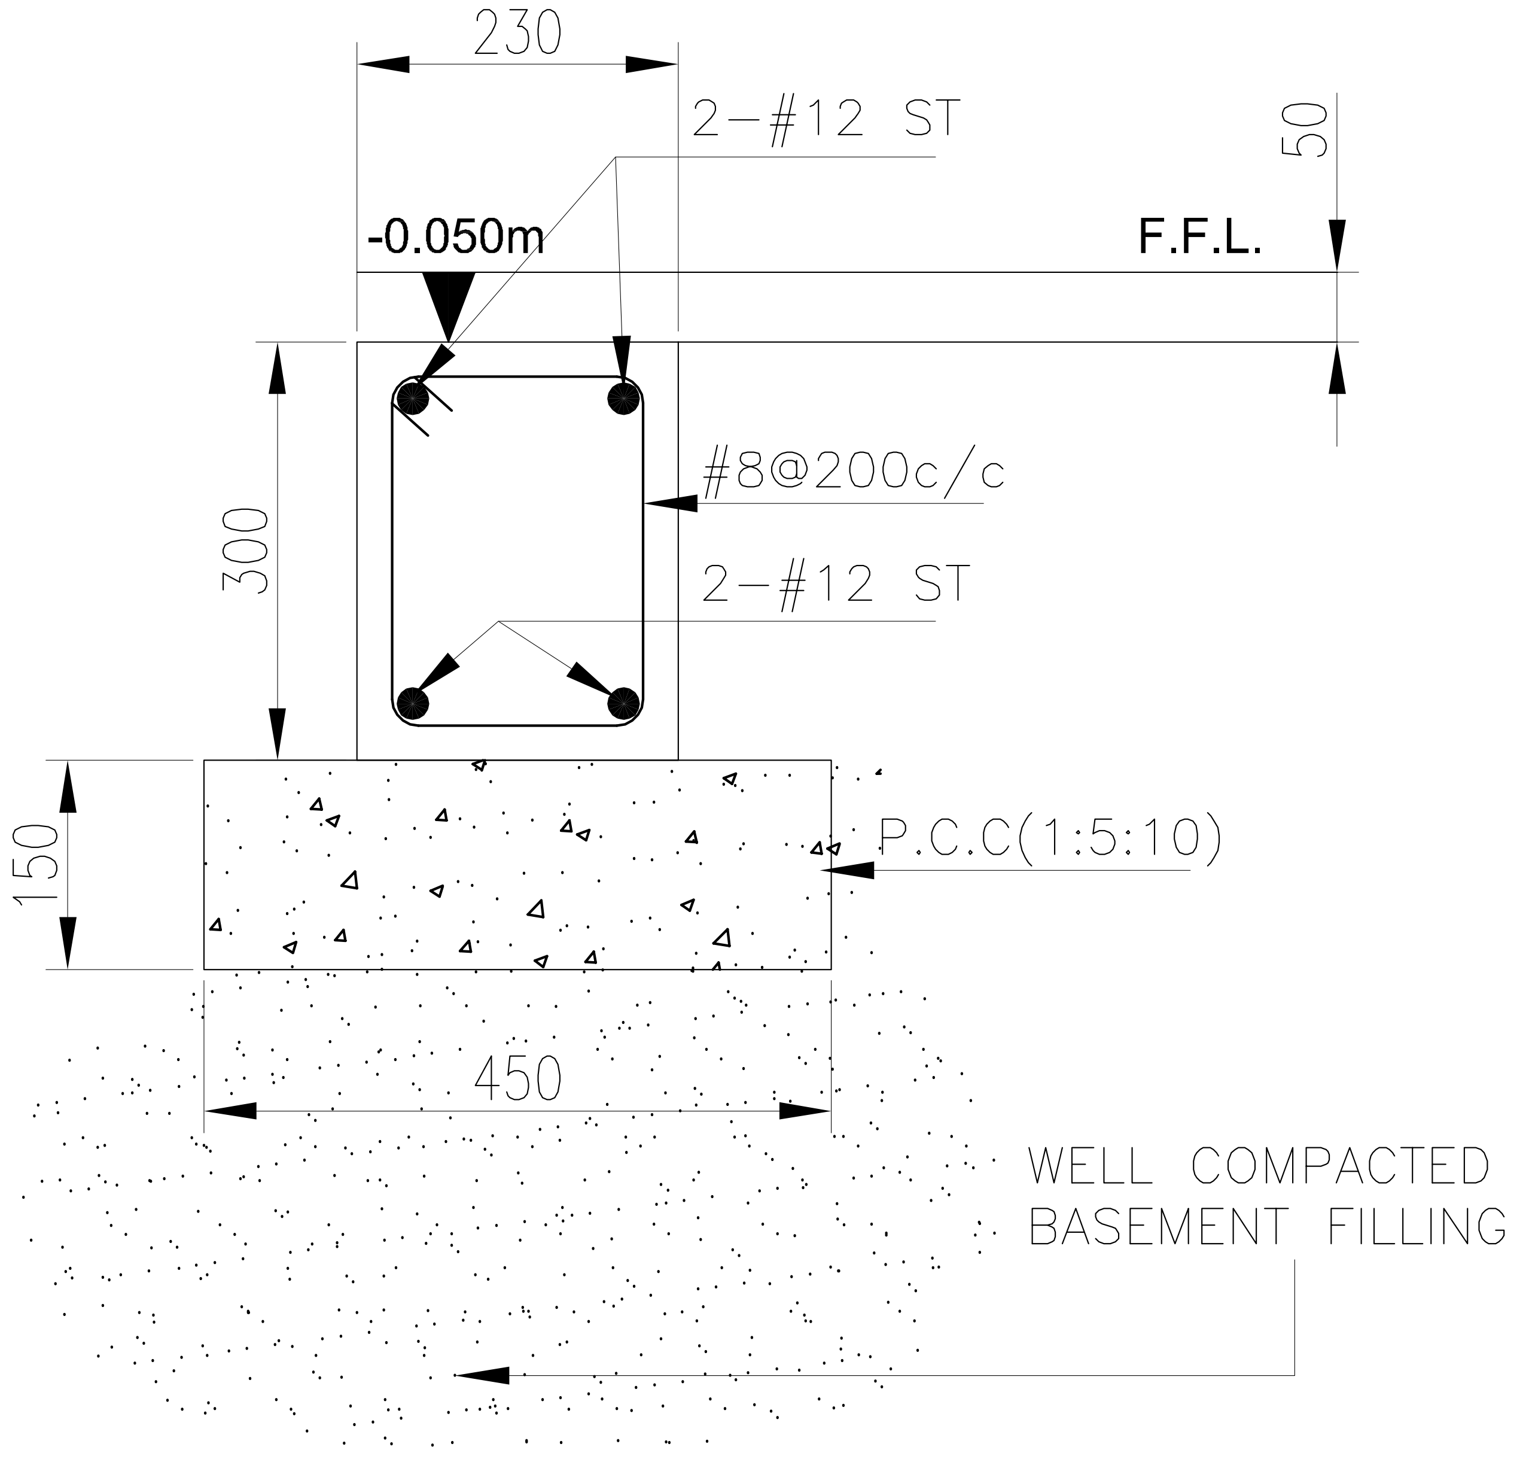

IPB1

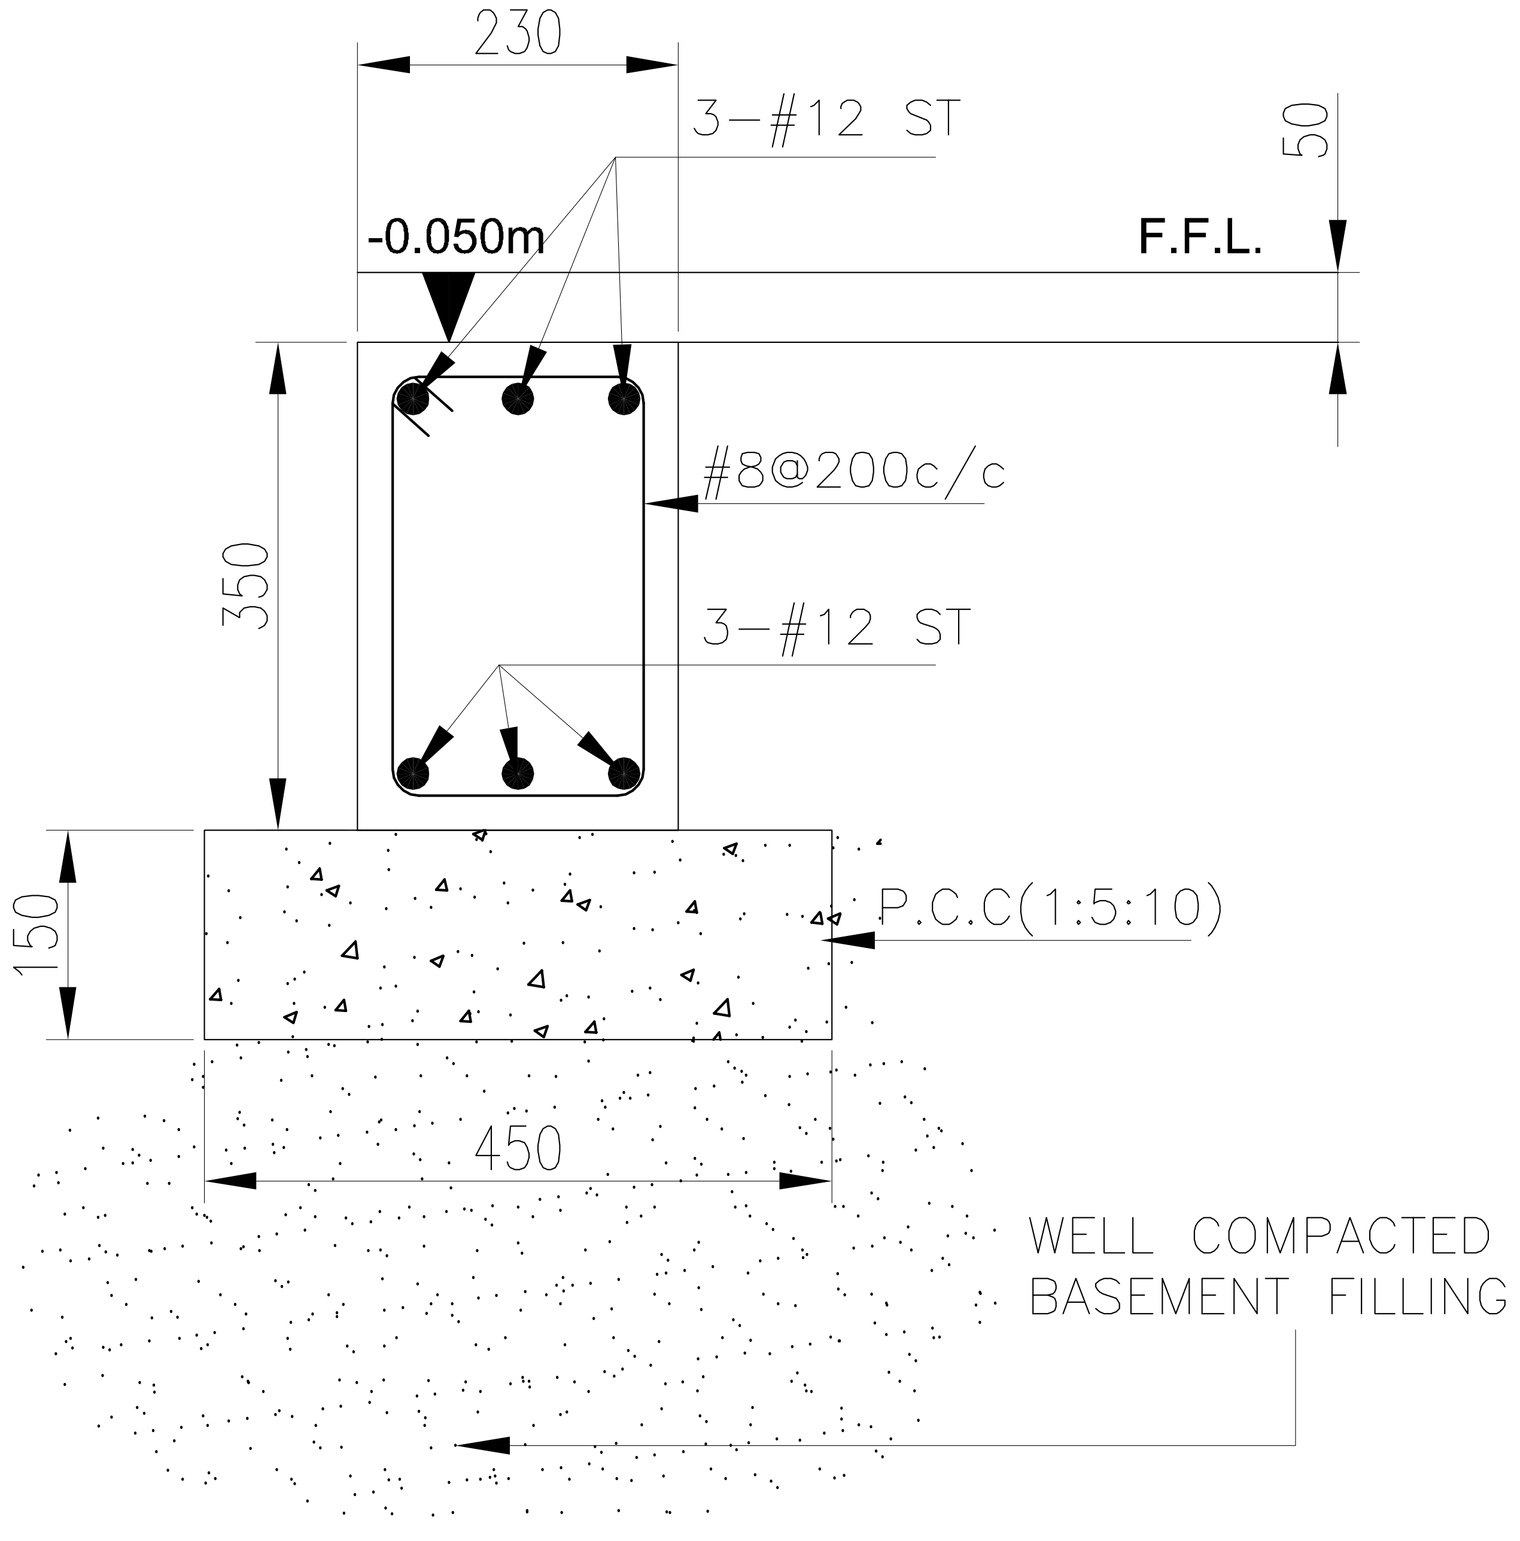

IPB2

- THIS DRAWING SHALL BE READ IN CONJUNCTION WITH ALL RELEVANT ARCHITECTURAL, STRUCTURAL AND SERVICES DRAWINGS. ANY DISCREPANCY NOTICED SHALL BE BROUGHT TO THE ATTENTION OF THE CONSULTANTS AND RESOLVED AS SOON AS POSSIBLE BUT ALWAYS PRIOR TO

ARCHITECTURAL CONSULTANT:

also. design
a little story of design

STRUCTURAL& MEP CONSULTANTS

JASHRITHA ASSOCIATES
AND MEP PLANNERS
4th FLOOR(4B), HIG 129, KPHB COLONY, KUKATPALLY,
(SUB BRANCH:PR NAGAR ERRAGADDA.)
HYDERABAD 500072, TELANGANA, INDIA
Phone : 9700441106.
E-mail : jashreyansh.consultatns@gmail.com
& jashritha.mep@gmail.com

PROJECT:

ANKURA HOMES_THE WOODS
AT KEESARAGUTTA

DRAWING TITLE:

1625_EAST VILLA
PLINTH BEAM DETAILS

| | |
|---|---|
| DESIGN ENGG : AJAY | APPROVED : |
| SCALE : NTS | DRAWN : PK |
| DATE : 19-09-2026 | CHECKED : PRADEEP |

| | | | |
|---|---|---|---|
| DRAWING NO: | SD-04 | REV.NO: | |

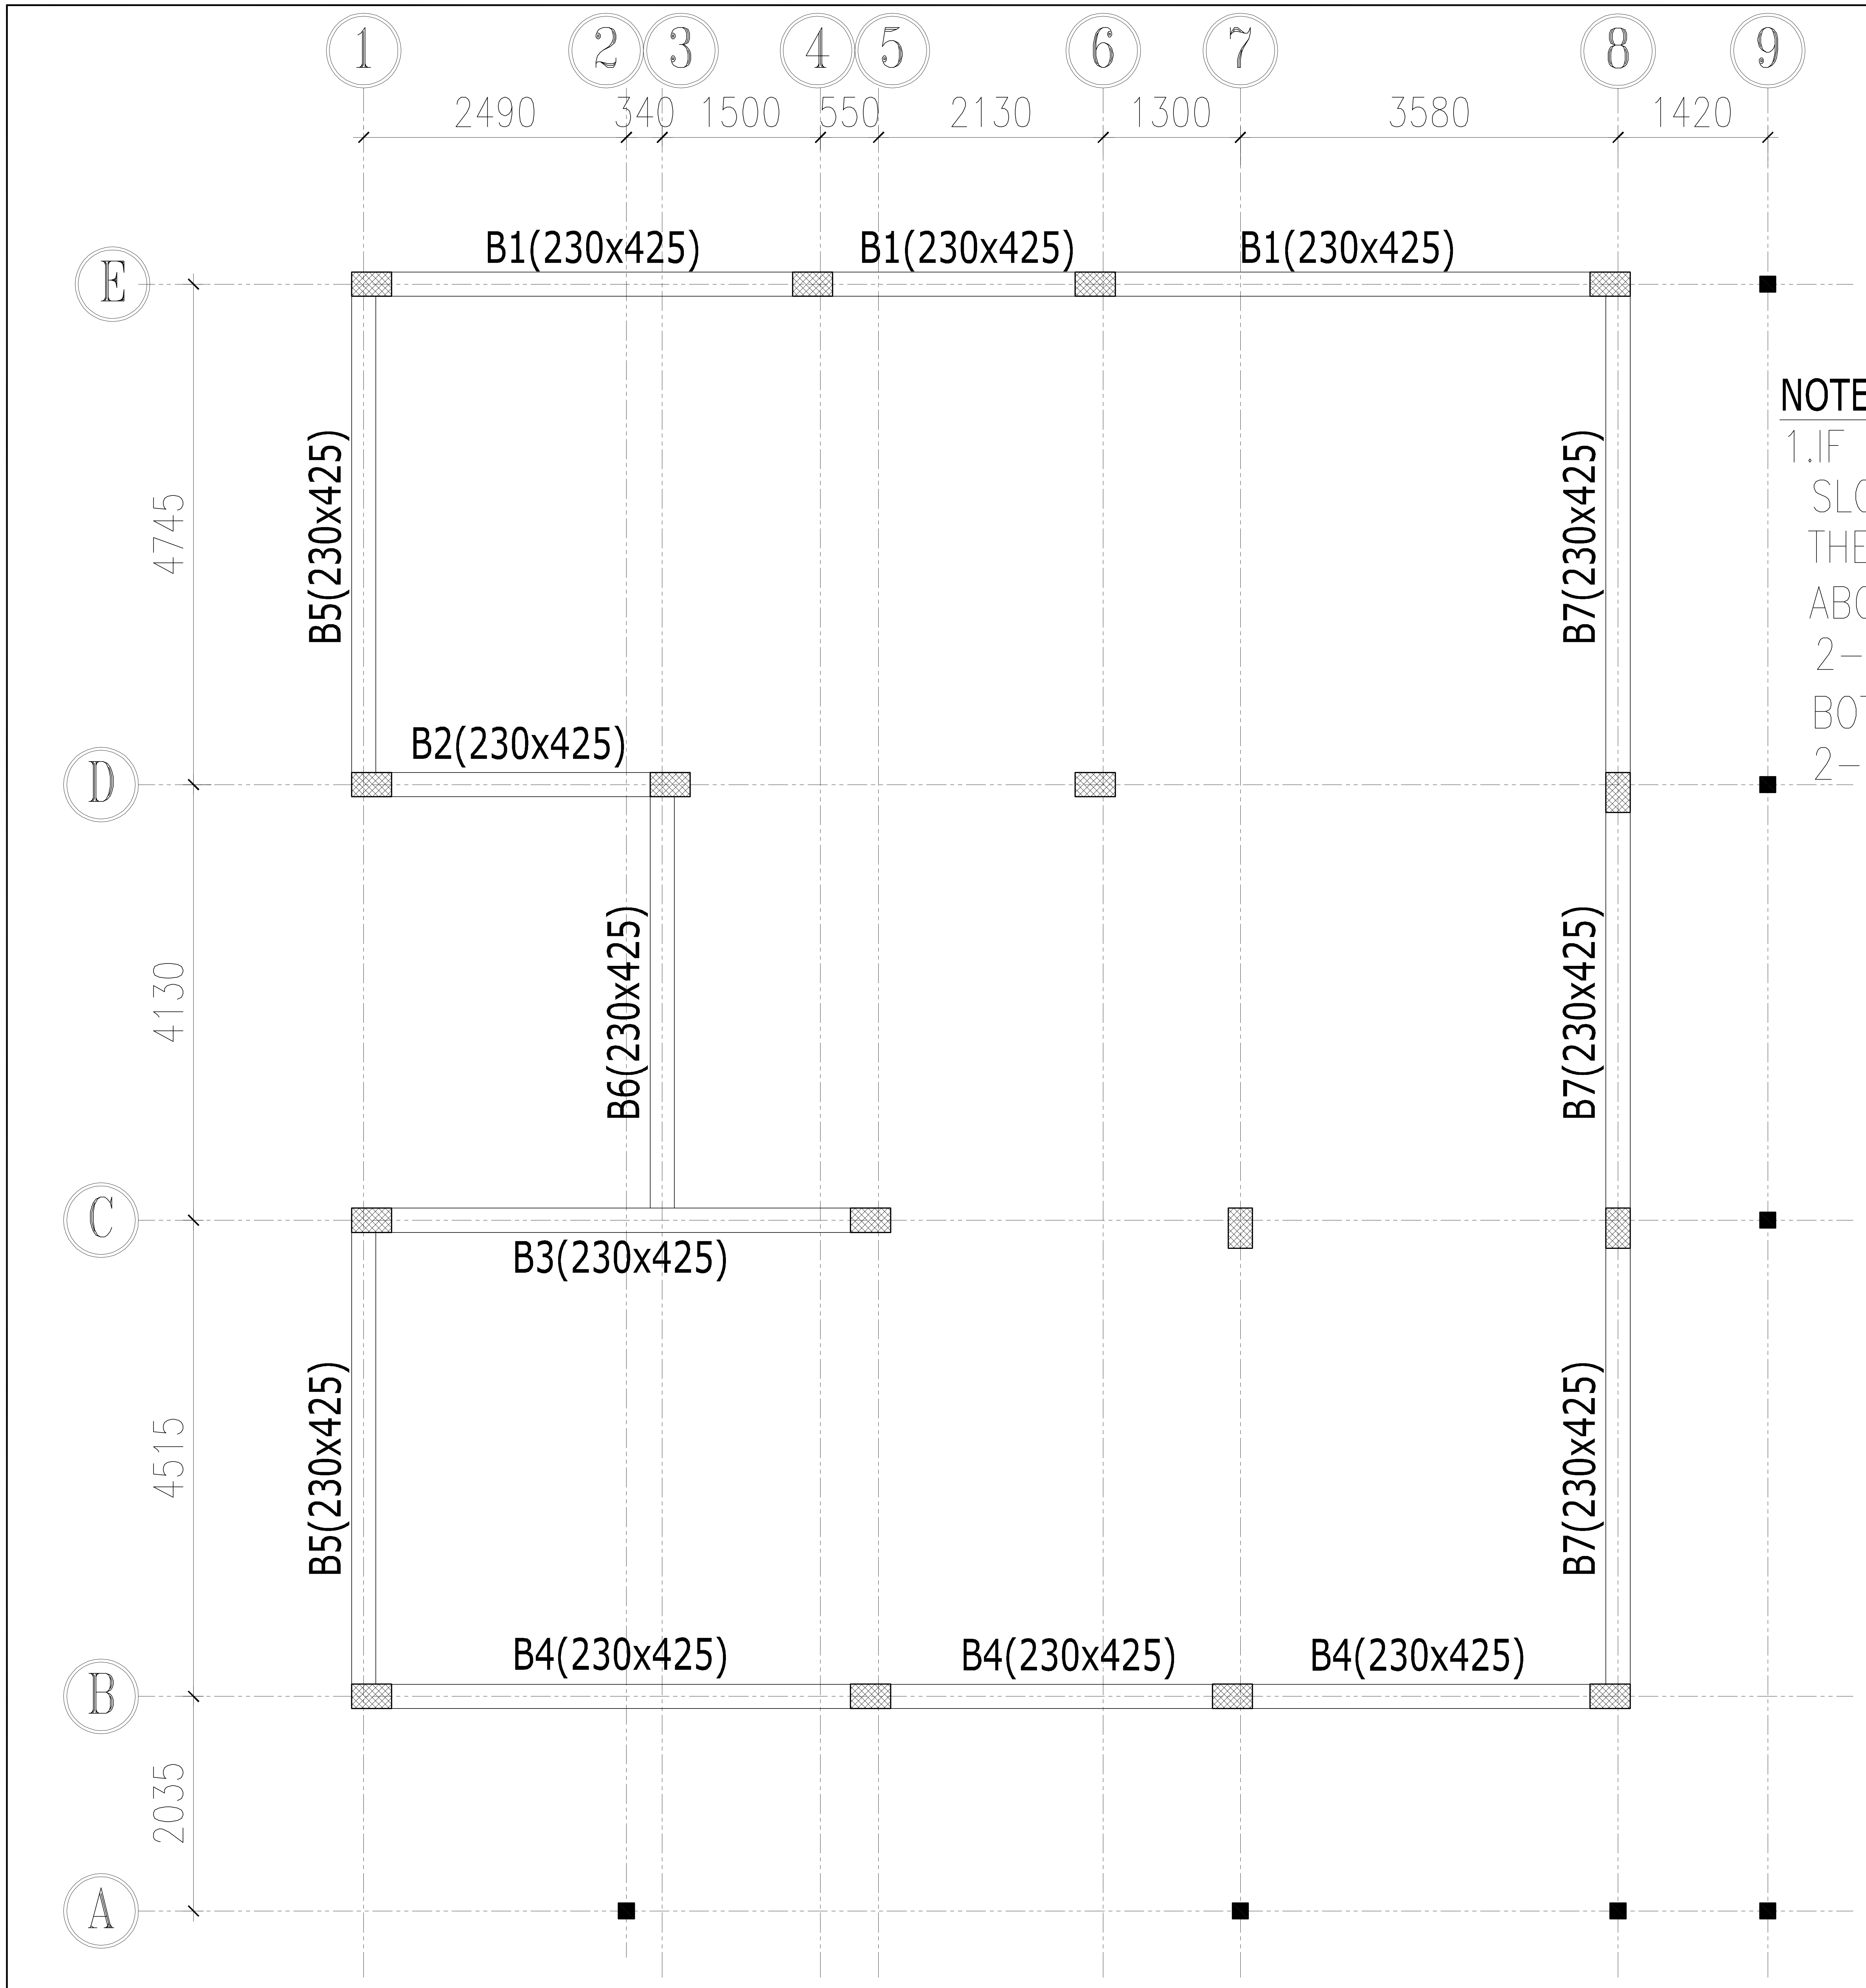

**NOTE:**

1.IF YOU WANT ANY INTERNAL BEAMS FOR SLOPED ROOF STRUCTURE PLEASE MAINTAIN THE STEEL 2-#16(Top&Bottom) UPTO 3.5M ABOVE 3.5M SPAN MAINTAIN TOP STEEL
2-#16 ST+ 2-#12 EXT @ SUPPORTS
BOTTOM STEEL
2-#16 ST+ 2-#12 EXT @ MID SPAN

- THIS DRAWING SHALL BE READ IN CONJUNCTION WITH ALL RELEVANT ARCHITECTURAL, STRUCTURAL AND SERVICES DRAWINGS. ANY DISCREPANCY NOTICED SHALL BE BROUGHT TO THE ATTENTION OF THE CONSULTANTS AND RESOLVED AS SOON AS POSSIBLE BUT ALWAYS PRIOR TO

DIRECTION:

N

ARCHITECTURAL CONSULTANT:

also. design
a little story of design

STRUCTURAL& MEP CONSULTANTS

JASHRITHA ASSOCIATES
AND MEP PLANNERS
4th FLOOR(4B), HIG 129, KPHB COLONY, KUKATPALLY,
(SUB BRANCH:PR NAGAR ERRAGADDA.)
HYDERABAD 500072, TELANGANA, INDIA
Phone : 9700441106.
E-mail : jashreyansh.consultatns@gmail.com
& jashritha.mep@gmail.com

PROJECT:

ANKURA HOMES_THE WOODS
AT KEESARAGUTTA

DRAWING TITLE:

1625_EAST VILLA
ROOF BEAM LAYOUT

| | |
|---|---|
| DESIGN ENGG : AJAY | APPROVED : |
| SCALE : NTS | DRAWN : PK |
| DATE : 23-09-2026 | CHECKED : PRADEEP |
| DRAWING NO: SD-05 | REV.NO: 01 |

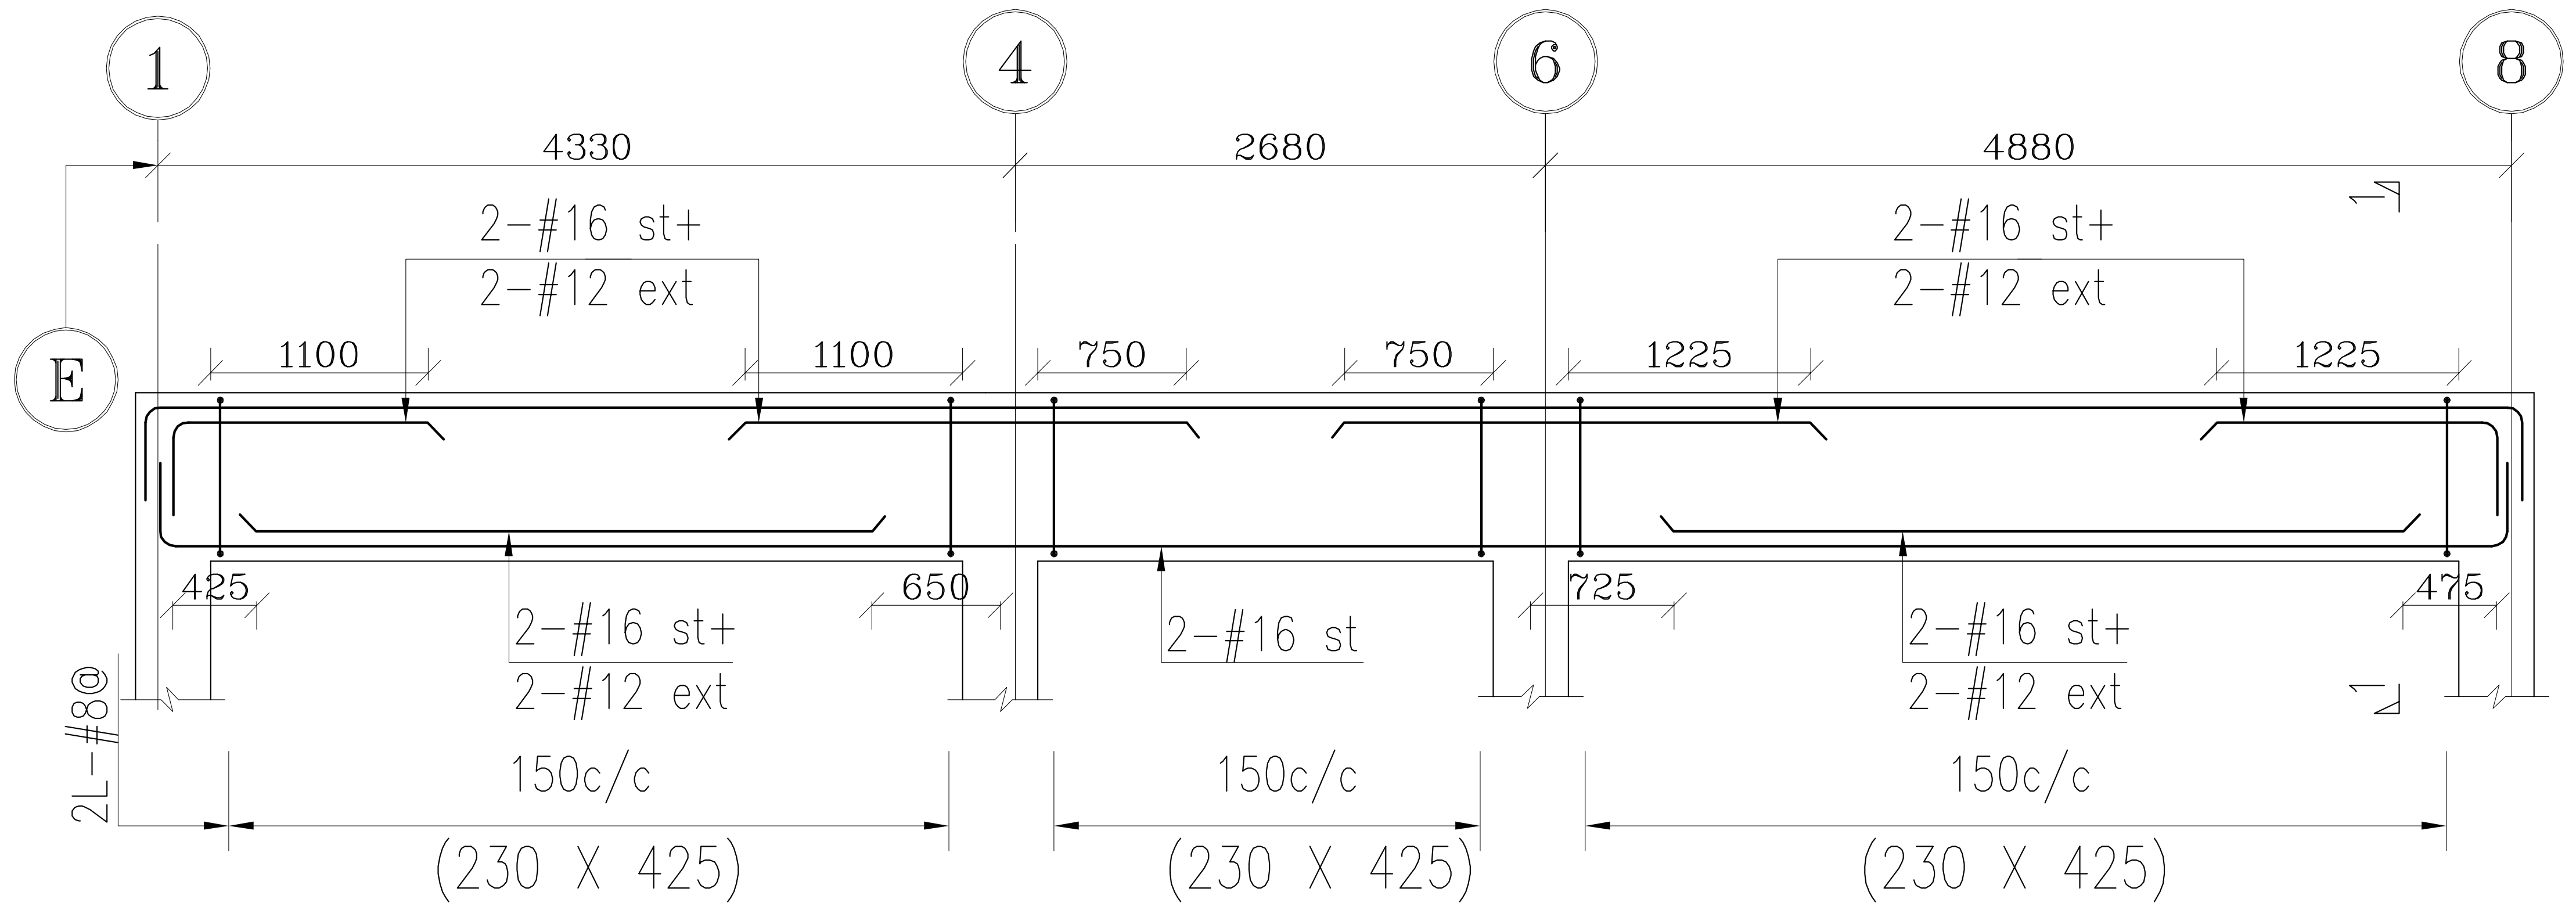

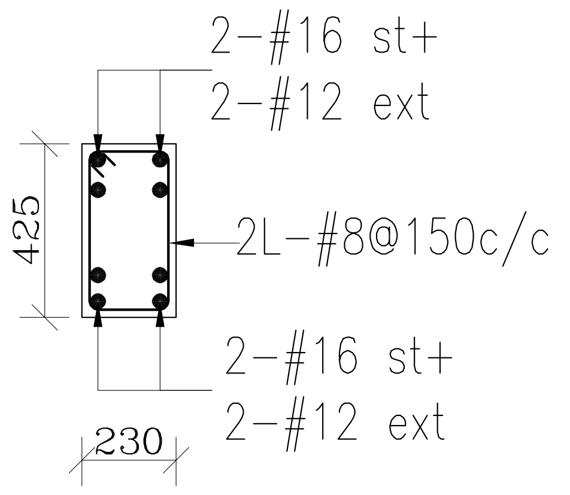

SECTION 1-1

L/S OF BEAM B1(230X425)

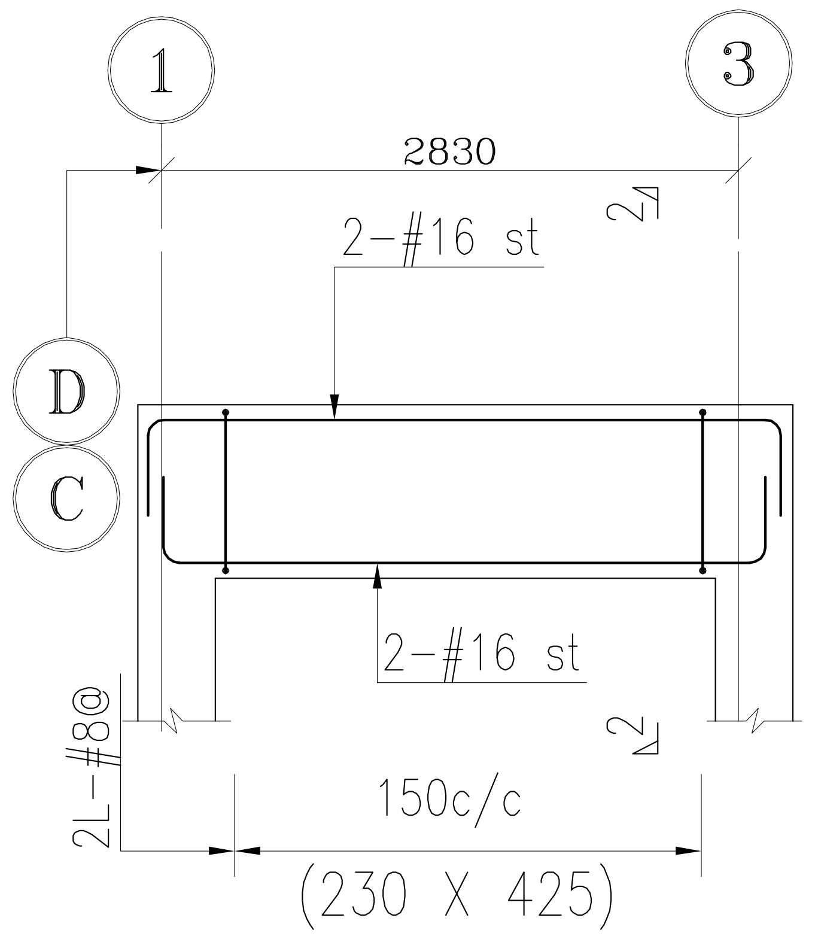

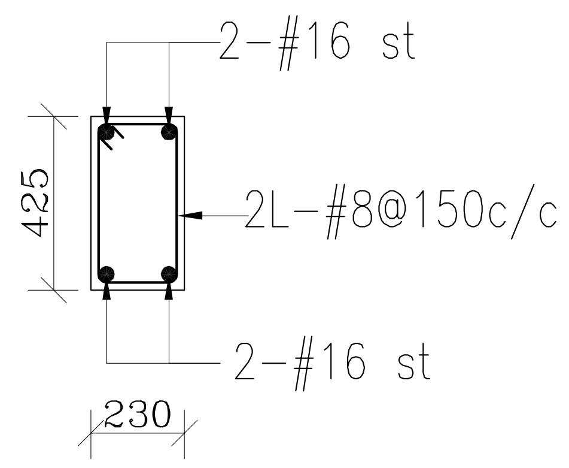

SECTION 2-2

L/S OF BEAM B2(230X425)

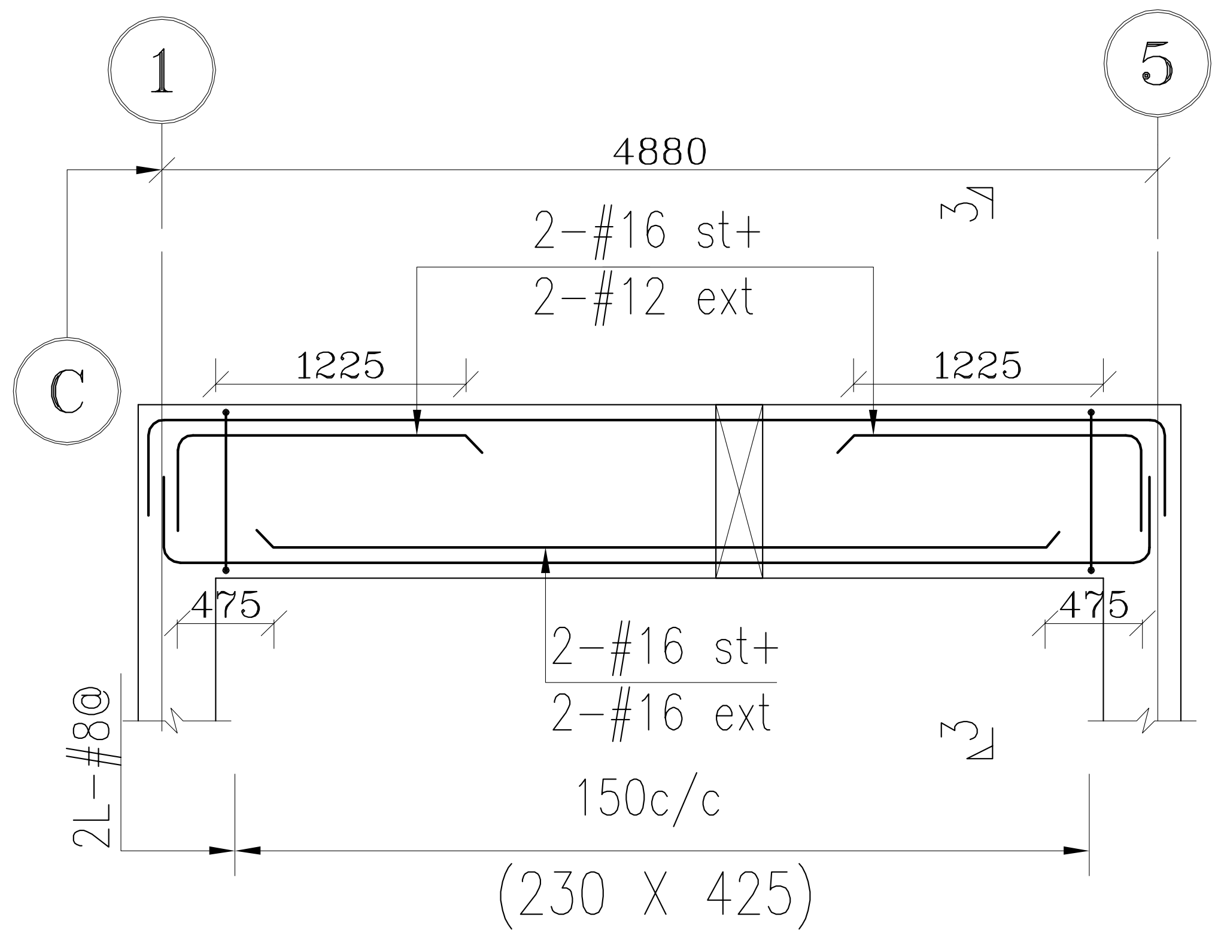

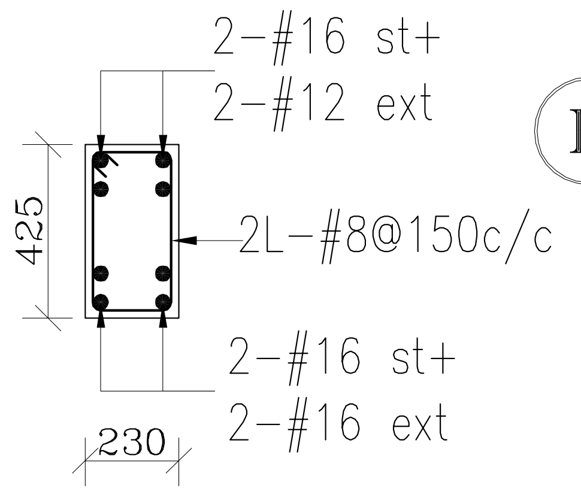

SECTION 3-3

L/S OF BEAM B3(230X425)

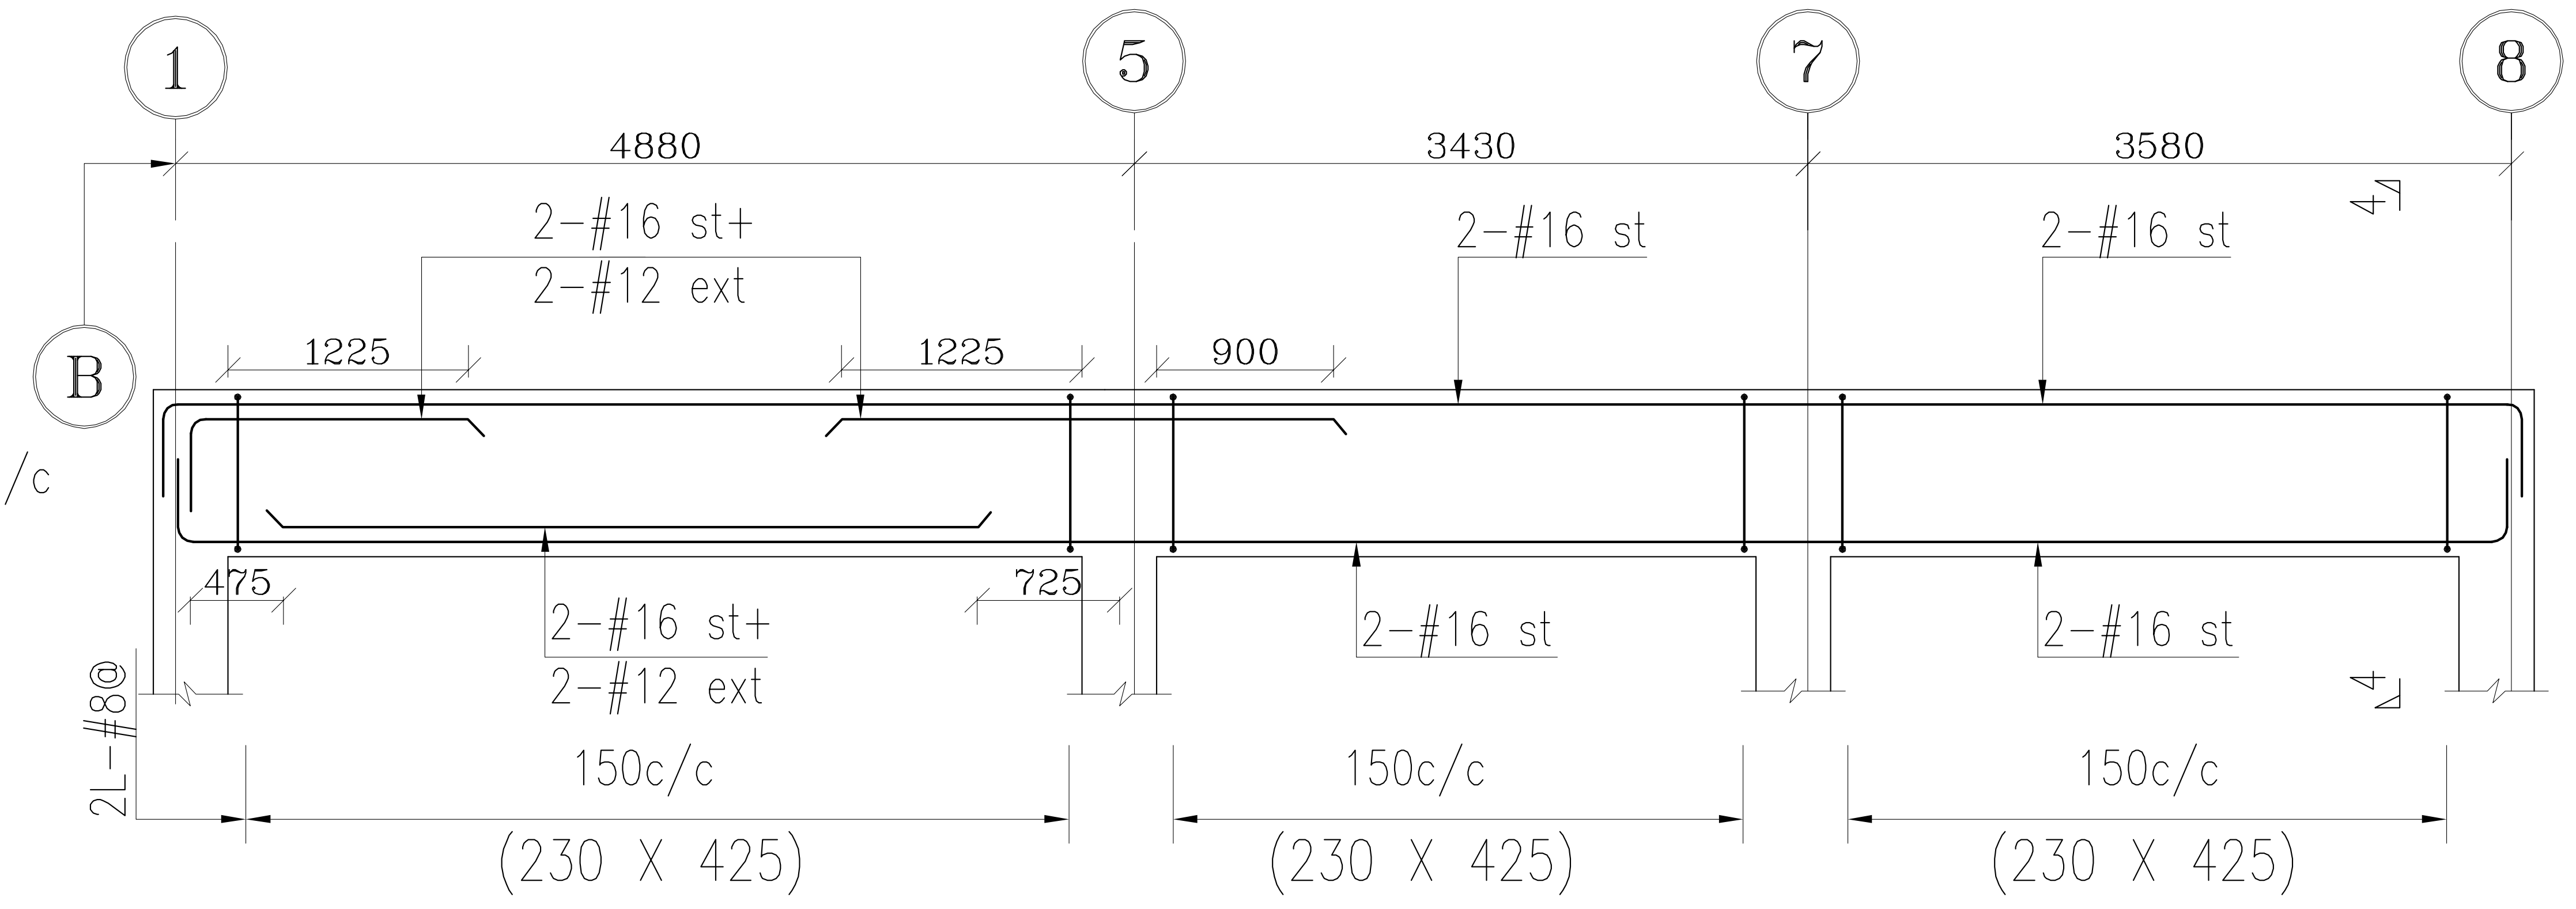

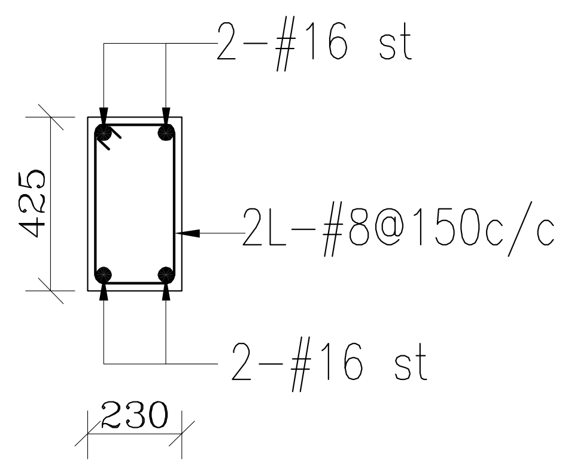

SECTION 4-4

L/S OF BEAM B4(230X425)

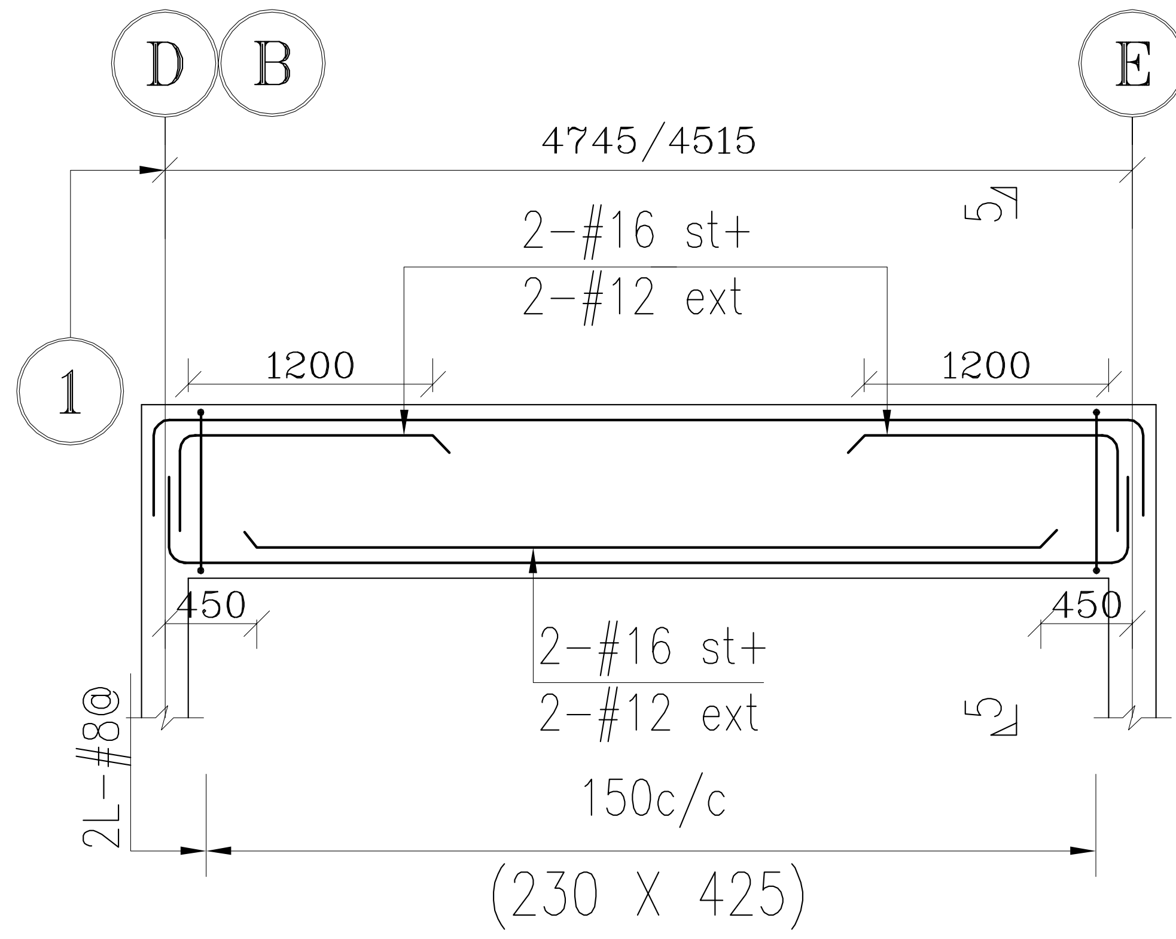

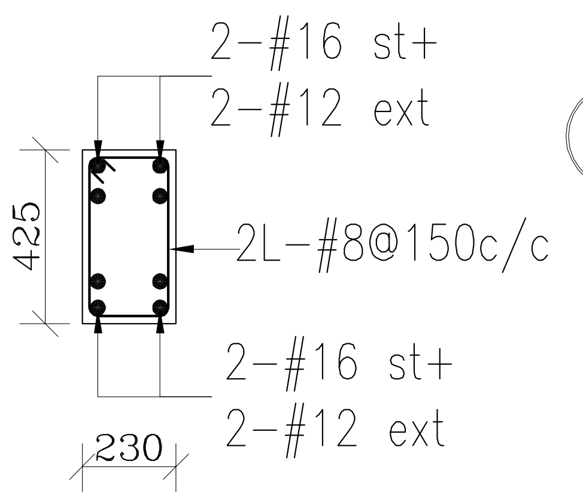

SECTION 5-5

L/S OF BEAM B5(230X425)

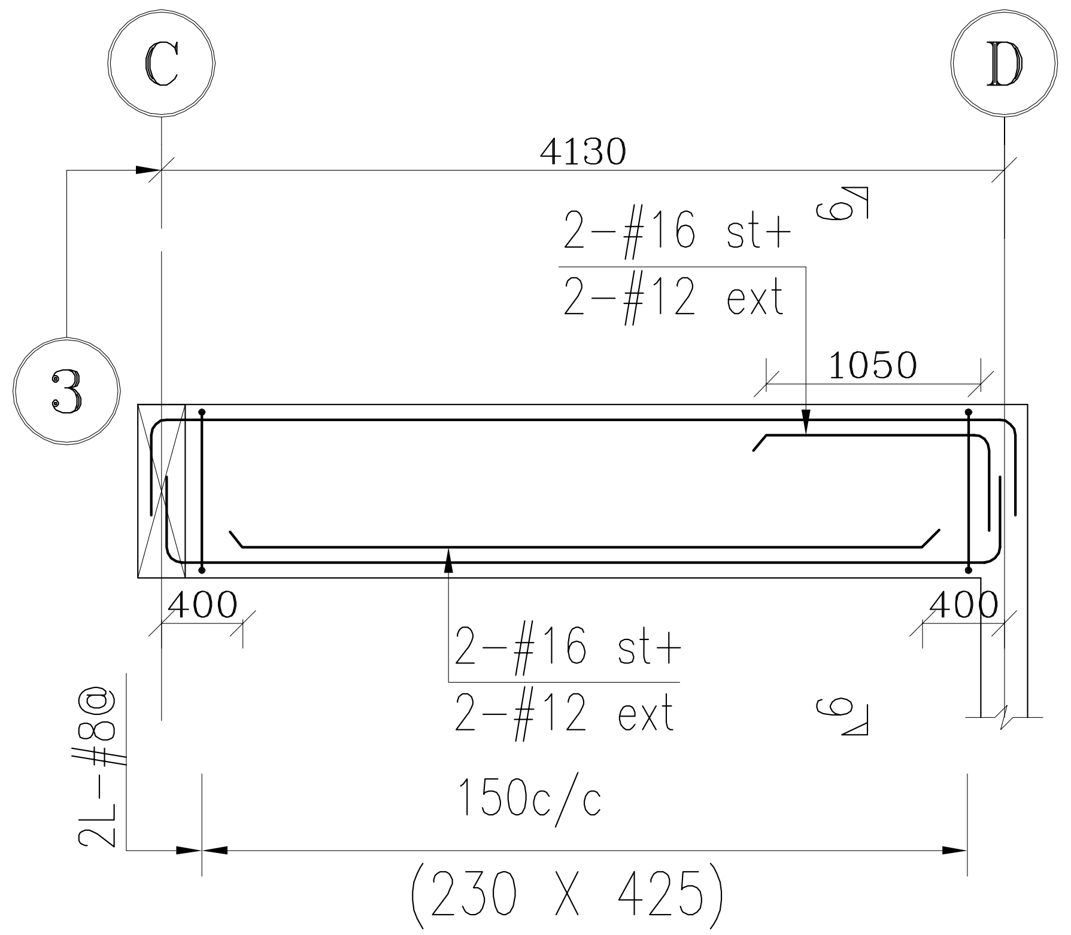

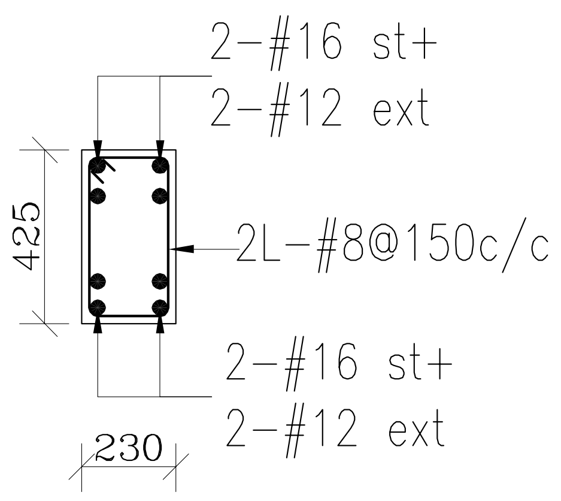

SECTION 6-6

L/S OF BEAM B6(230X425)

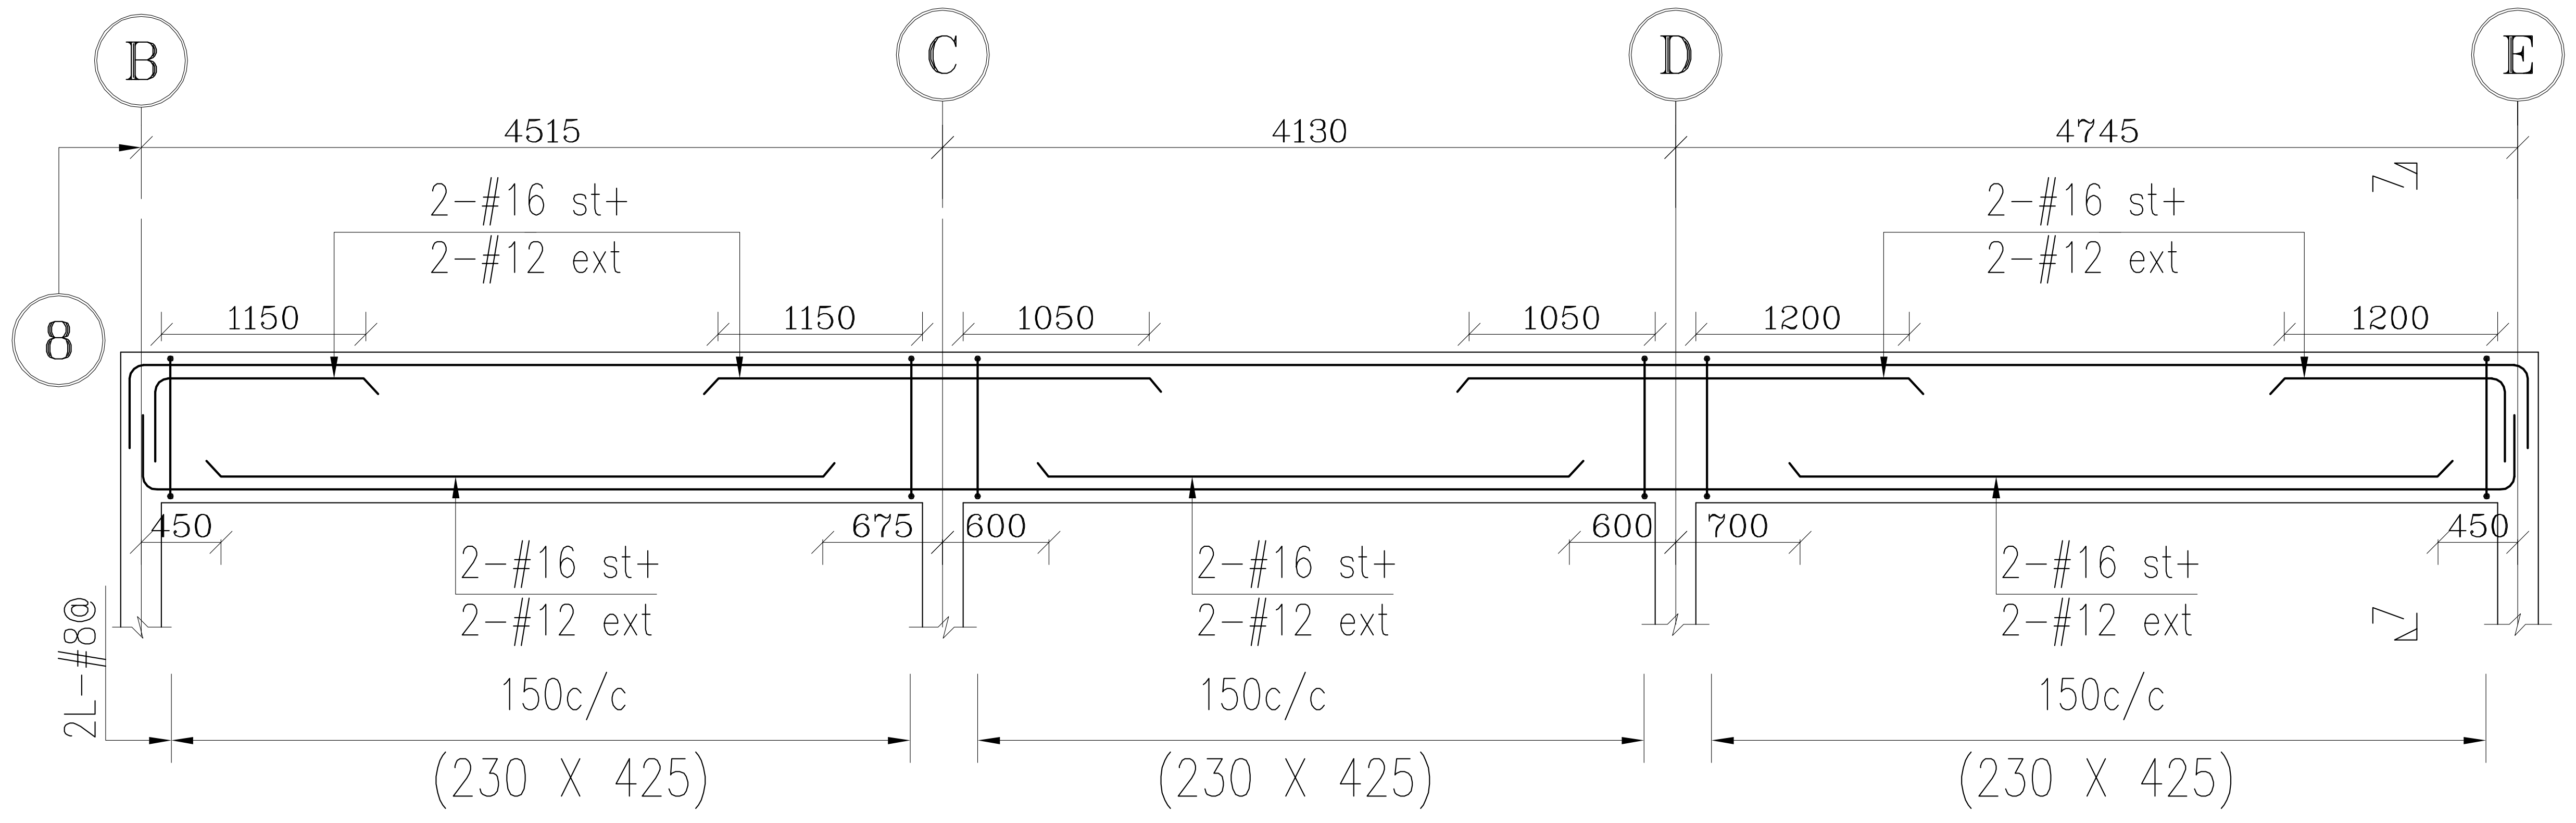

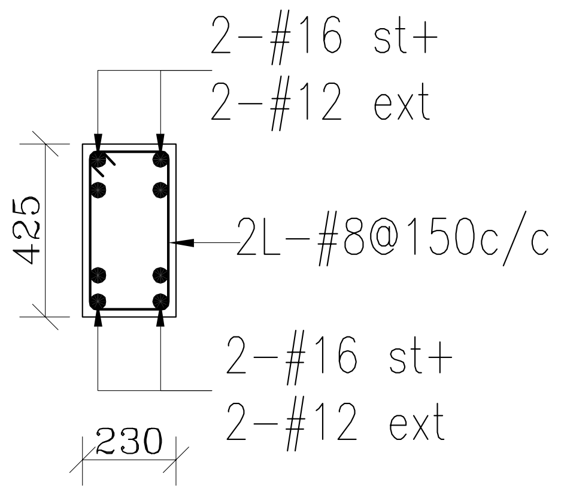

SECTION 7-7

L/S OF BEAM B7(230X425)

- THIS DRAWING SHALL BE READ IN CONJUNCTION WITH ALL RELEVANT ARCHITECTURAL, STRUCTURAL AND SERVICES DRAWINGS. ANY DISCREPANCY NOTICED SHALL BE BROUGHT TO THE ATTENTION OF THE CONSULTANTS AND RESOLVED AS SOON AS POSSIBLE BUT ALWAYS PRIOR TO

DIRECTION:

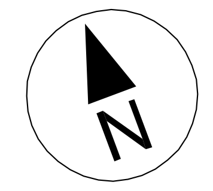

ARCHITECTURAL CONSULTANT:

also.
design
a little story of design

STRUCTURAL& MEP CONSULTANTS

JASHRITHA ASSOCIATES
AND MEP PLANNERS
4th FLOOR(4B), HIG 129, KPHB COLONY, KUKATPALLY,
(SUB BRANCH:PR NAGAR ERRAGADDA.)
HYDERABAD 500072, TELANGANA, INDIA
Phone : 9700441106.
E-mail : jashreyansh.consultatns@gmail.com
& jashritha.mep@gmail.com

PROJECT:

ANKURA HOMES_THE WOODS
AT KEESARAGUTTA

DRAWING TITLE:

1625_EAST VILLA
ROOF BEAM DETAILS

| | |
|---|---|
| DESIGN ENGG : AJAY | APPROVED : |
| SCALE : NTS | DRAWN : PK |
| DATE : 23-09-2026 | CHECKED : PRADEEP |
| DRAWING NO: SD-06 | REV.NO: 01 |