
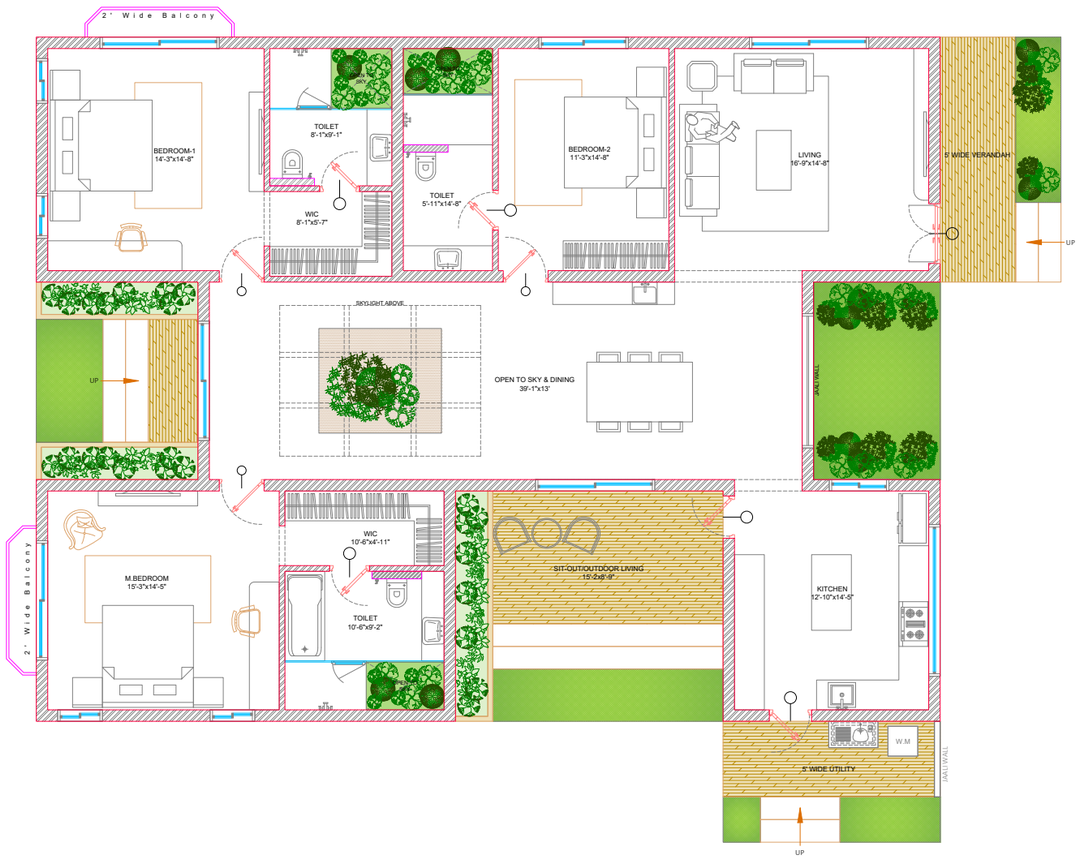


EAST VILLA FLOOR PLAN
2175 SQ.FT

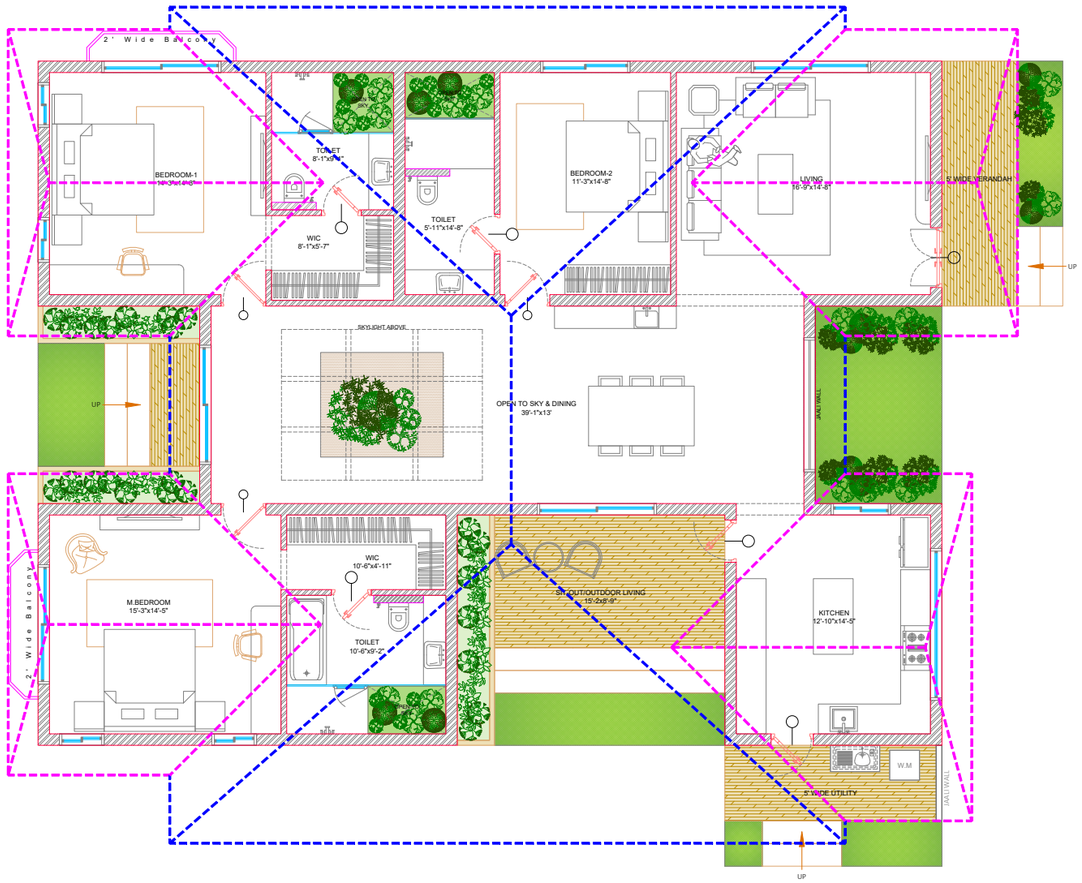

EAST VILLA FLOOR PLAN WITH ROOF ABOVE
2175 SQ.FT

KEY PLAN

LEGEND:

- PRIMARY ROOF
- SECONDARY ROOF

GENERAL NOTES:

- ALL DIMENSIONS ARE IN MILLIMETERS
- THIS DRAWING IS A COPYRIGHT AND PROPERTY OF THE ARCHITECT. IS NOT TO BE PRODUCED, COPIED, HANDED OVER TO THIRD PARTY OR USED FOR ANY OTHER PURPOSE OTHER THAN FOR WHICH IT IS INTENDED.
- ALL DIMENSIONS SHALL BE VERIFIED ON SITE PRIOR TO START OF WORK. ANY DISCREPANCY SHALL BE BROUGHT TO THE NOTICE OF THE ARCHITECT.
- THE CONTRACTOR MUST CHECK ALL DIMENSIONS AND DETAILS AND BE RESPONSIBLE FOR THE SAME. ANY DISCREPANCY SHALL BE BROUGHT TO THE NOTICE OF THE ARCHITECT.
- THIS DRAWING IS TO BE READ AND NOT SCALED.
- THIS DRAWING SHALL BE READ IN CONJUNCTION WITH ALL RELEVANT ARCHITECTURAL, STRUCTURAL AND SERVICES DRAWINGS. ANY DISCREPANCY NOTICED SHALL BE BROUGHT TO THE ATTENTION OF THE CONSULTANTS AND RESOLVED AS SOON AS POSSIBLE BUT ALWAYS PRIOR TO

NO	DESCRIPTION	DATE	SIGN

DIRECTION:

ARCHITECTURAL CONSULTANT:

also. design

PROJECT:

ANKURA HOMES_THE WOODS
AT KEESARAGUTTA

INFORMATION COPY

DRAWING TITLE:


2175_EAST VILLA
FLOOR PLAN

ARCHITECT : HARISH	APPROVED : HARISH
SCALE : NTS	DRAWN : DHARANI
DATE : 13-10-2026	CHECKED : SHANMUKHI

DRAWING NO: REV.NO:



WEST VILLA FLOOR PLAN
2175 SQ.FT

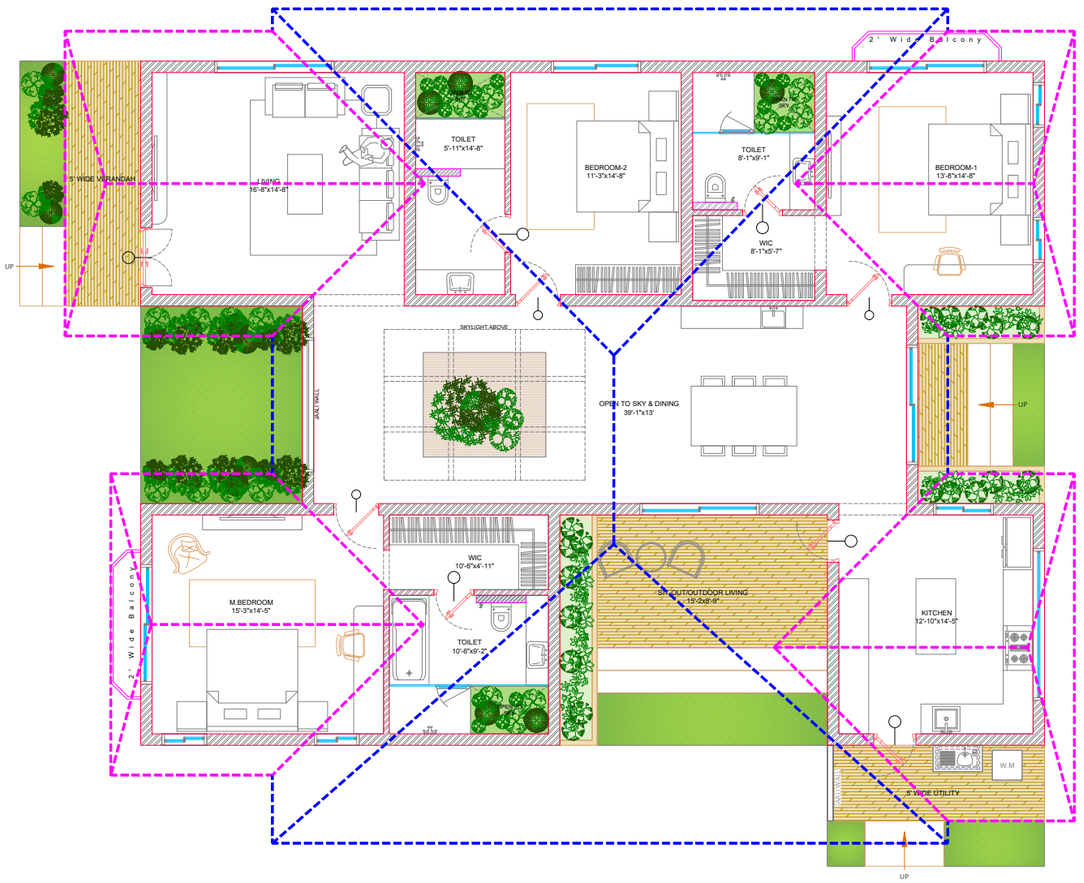

WEST VILLA FLOOR PLAN WITH ROOF ABOVE
2175 SQ.FT

KEY PLAN

LEGEND:

- PRIMARY ROOF
- SECONDARY ROOF

GENERAL NOTES:

- ALL DIMENSIONS ARE IN MILLIMETERS
- THIS DRAWING IS A COPYRIGHT AND PROPERTY OF THE ARCHITECT. IS NOT TO BE PRODUCED, COPIED, HANDED OVER TO THIRD PARTY OR USED FOR ANY OTHER PURPOSE OTHER THAN FOR WHICH IT IS INTENDED.
- ALL DIMENSIONS SHALL BE VERIFIED ON SITE PRIOR TO START OF WORK. ANY DISCREPANCY SHALL BE BROUGHT TO THE NOTICE OF THE ARCHITECT.
- THE CONTRACTOR MUST CHECK ALL DIMENSIONS AND DETAILS AND BE RESPONSIBLE FOR THE SAME. ANY DISCREPANCY SHALL BE BROUGHT TO THE NOTICE OF THE ARCHITECT.
- THIS DRAWING IS TO BE READ AND NOT SCALED.
- THIS DRAWING SHALL BE READ IN CONJUNCTION WITH ALL RELEVANT ARCHITECTURAL, STRUCTURAL AND SERVICES DRAWINGS. ANY DISCREPANCY NOTICED SHALL BE BROUGHT TO THE ATTENTION OF THE CONSULTANTS AND RESOLVED AS SOON AS POSSIBLE BUT ALWAYS PRIOR TO

NO	DESCRIPTION	DATE	SIGN

DIRECTION:

ARCHITECTURAL CONSULTANT:

also. design

PROJECT:

ANKURA HOMES_THE WOODS
AT KEESARAGUTTA

INFORMATION COPY

DRAWING TITLE:

2175_WEST VILLA
FLOOR PLAN

ARCHITECT : HARISH	APPROVED : HARISH
SCALE : NTS	DRAWN : DHARANI
DATE : 13-10-2026	CHECKED : SHANMUKHI

DRAWING NO: | REV.NO: