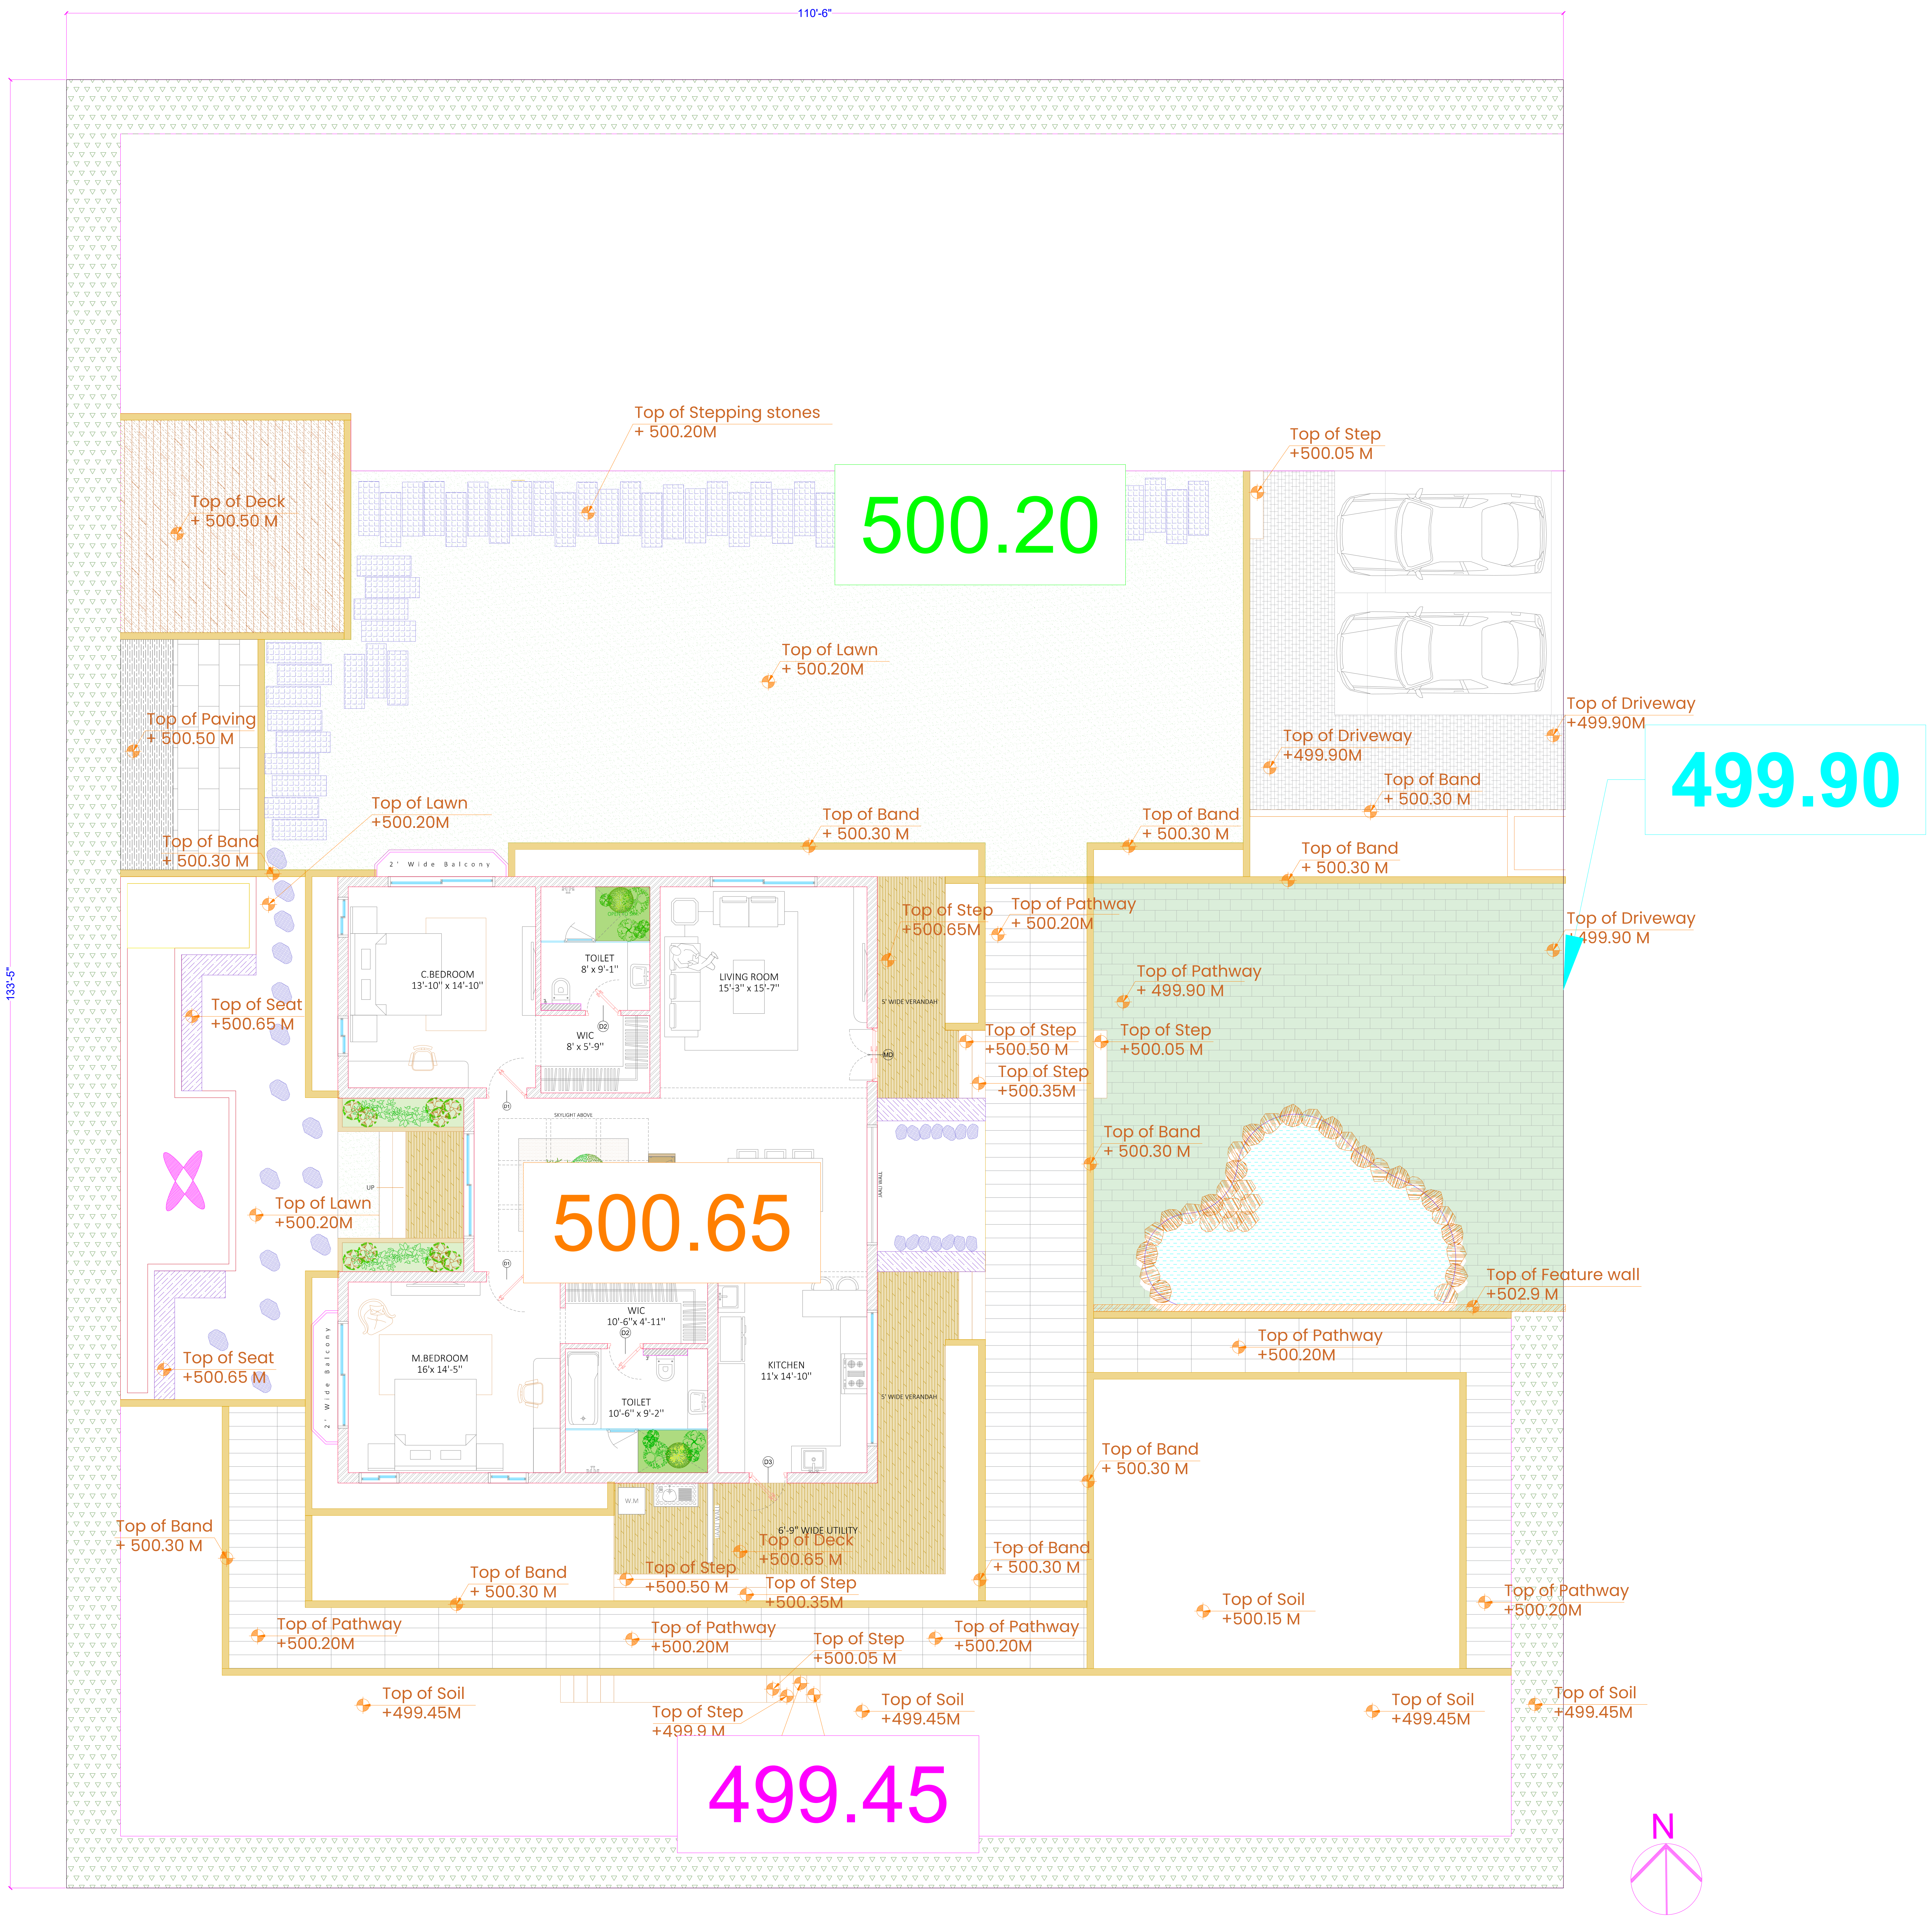

LUMISCAPES
Landscape Architects
Mob: +91 90309 62233 , +91 95151 03063
contact@lumiscapeslandscapes.in

NOTES
1. THIS DRAWING SHOULD BE READ AND NOT MEASURED.
2. ALL DIMENSIONS ARE IN MILLIMETERS AND LEVELS ARE IN METERS UNLESS STATED OTHERWISE.
3. ALL DRAWINGS MUST BE CROSS REFERENCE IN CASE OF ANY DOUBT / DISCREPANCY.
4. TOC REPRESENTS TOP OF CONCRETE & FFL REPRESENTS FINISHED FLOOR LEVELS. ALL DIMENSIONS SHOWN IN THE DRAWINGS ARE STRUCTURAL / MASONRY DIMENSIONS.
5. ALL ARCHITECTURAL DRAWINGS MUST BE REFERRED IN COORDINATION WITH STRUCTURAL DRAWINGS.
6. ALL SPECIALIST WORKS DETAILS AND ANY DEVIATIONS FROM THIS CONSTRUCTION DRAWINGS, THE CONTRACTOR / SUB-CONTRACTOR ARE TO PROVIDE SHOP DRAWINGS FOR ARCHITECT'S / ENGINEER'S APPROVAL PRIOR TO CONSTRUCTION.

KEY PLAN

DRAWING STAGE

FOR INFORMATION &APPROVAL

GFC STAMP

CLIENT

M/S. ANKURA HOMES

LEGEND

NOTE : ALL THE DIMENSIONS ARE IN FEET

ARCHITECTS

MEP CONSULTANTS

STRUCTURAL CONSULTANTS

PROJECT TITLE

"THE WOODS" BY ANKURA HOMES @BOMMALARAMARAM

DRAWING TITLE

LEVEL INDICATION PLAN

NORTH

N

		REV.	DATE
LA ARCHITECT	YASASWINI & CHARITA		
DWG NO :	LLA-TW-MP-01	08	25-08-26
CHECKED BY :	CHARITA.M	09	26-08-26
DRAWN BY :	P.VAMSI	10	20-09-26
DATE :	05-10-2026	11	25-09-26
SCALE :	NTS	SHEET - A2	