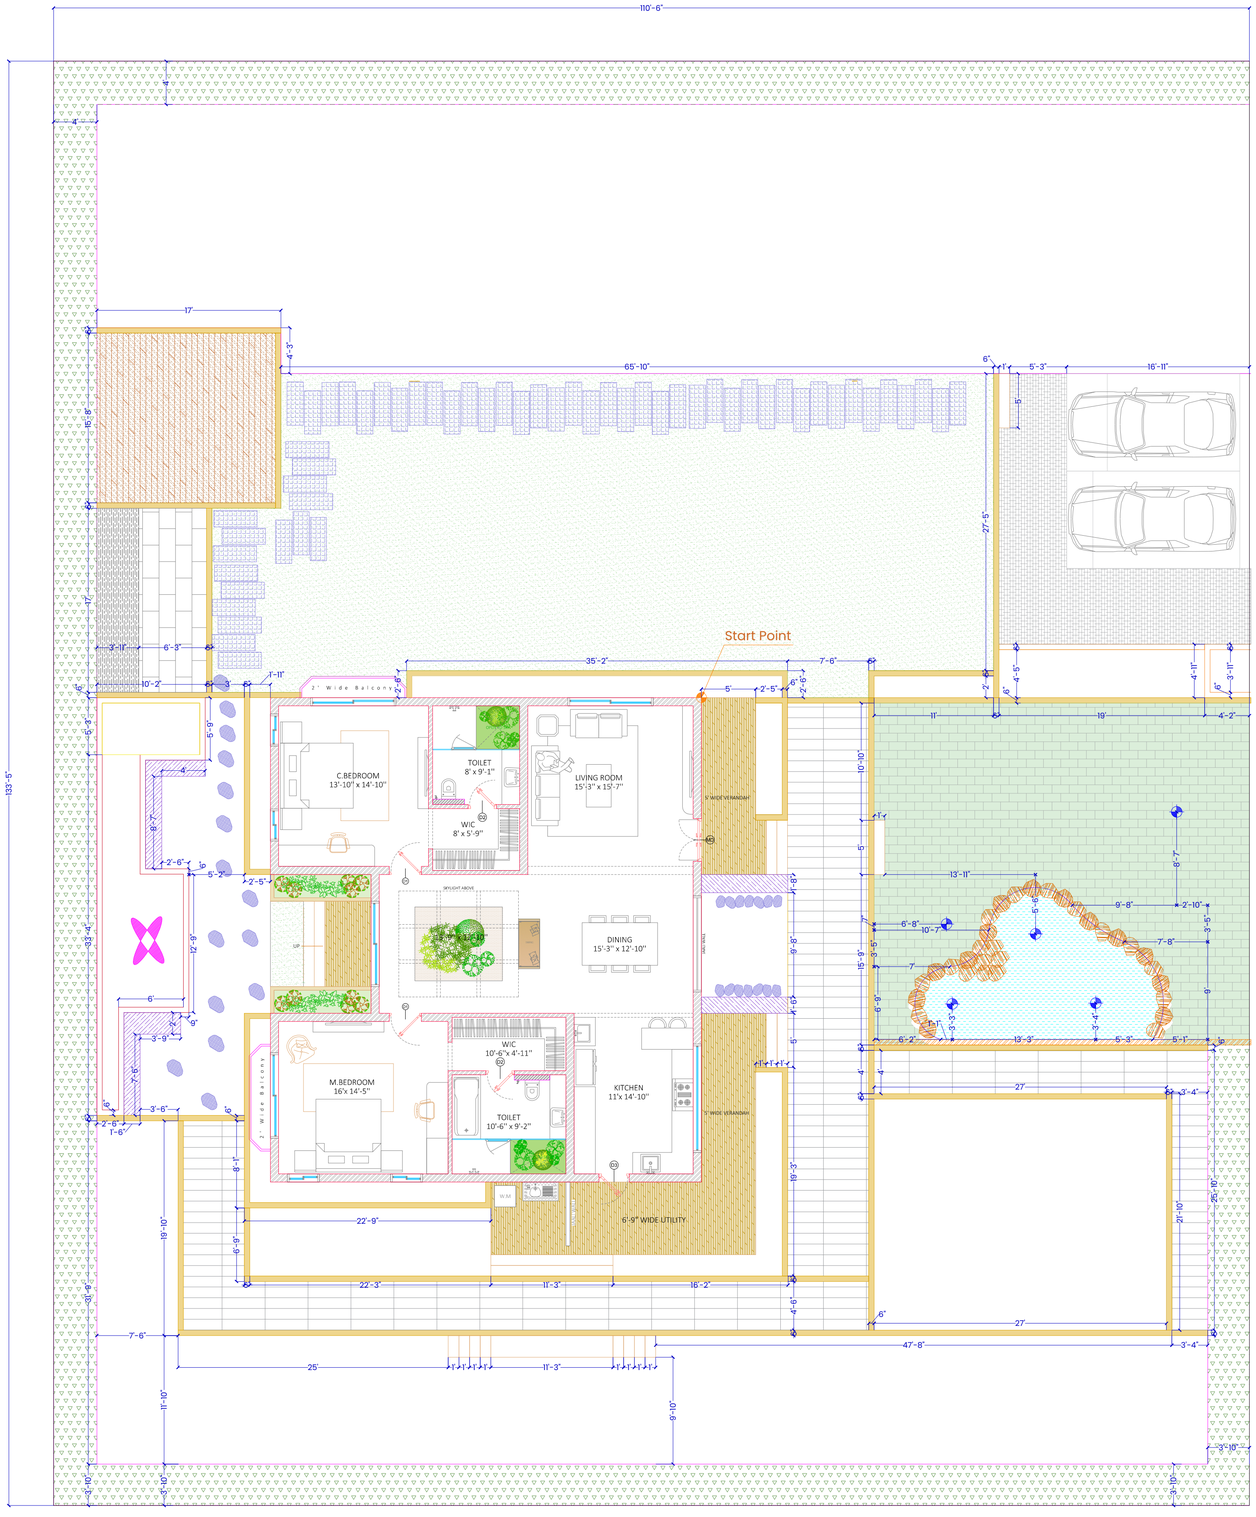


Landscape Architects

Mob: +91 90359 62233, +91 9515 03063

contact@lumiscapesandscapes.in

NOTES

1. THIS DRAWING SHOULD BE READ AND NOT MEASURED.
2. ALL DIMENSIONS ARE IN METERS AND LEVELS ARE IN METERS UNLESS STATED OTHERWISE.
3. ALL DRAWINGS MUST BE CROSS REFERENCE IN CASE OF ANY DISCREPANCY OCCURS.
4. TOC REPRESENTS TOP OF CONCRETE & FFL REPRESENTS FINISHED FLOOR LEVELS. ALL DIMENSIONS SHOWN IN THE DRAWINGS ARE TO FINISHED FACE OF WALLS UNLESS NOTED.
5. ALL ARCHITECTURAL DRAWINGS MUST BE REFERRED IN COORDINATION WITH STRUCTURAL DRAWINGS.
6. ALL SPECIALIST WORKS DETAILS AND ANY DEVIATIONS FROM THIS DRAWING TO BE CONFIRMED BY THE CONTRACTOR / SUB-CONTRACTOR ARE TO PROVIDE SHOP DRAWINGS FOR ARCHITECTS / ENGINEER'S APPROVAL PRIOR TO CONSTRUCTION.

KEY PLAN

DRAWING STAGE

FOR INFORMATION &APPROVAL

GFC STAMP

CLIENT

M/S. ANKURA HOMES

LEGEND

NOTE : ALL THE DIMENSIONS ARE IN FEET

ARCHITECTS

MEP CONSULTANTS

STRUCTURAL CONSULTANTS

PROJECT TITLE

"THE WOODS" BY ANKURA HOMES @BOMMALARAMARAM

DRAWING TITLE

MARKING PLAN

NORTH

LA ARCHITECT	YASASWINI & CHARITA	REV.	DATE
DWG NO :	LLA-TW-LIP-11	08	25-08-26
CHECKED BY :	CHARITA.M	09	26-08-26
DRAWN BY :	P.VAMSI	10	20-09-26
DATE :	05-10-2026	11	25-09-26
SCALE :	NTS	SHEET - A2	