
















OPENING TYPE		MD	D1	D2	D3	SD1
						
						
DIMENSIONS		1200x2150	900x2150	800x2150	850x2150	2400x2150
TYPE		SWING	SWING	SWING	SWING	SLIDING
LOCATION		LIVING AREA	LIVING AREA	LIVING AREA	LIVING AREA	BEDROOMS, DINING AREA
MAKE	FRAME	ENGINEERING WOOD	ENGINEERING WOOD	ENGINEERING WOOD	ENGINEERING WOOD	UPVC
	SHUTTER	ENGINEERING WOOD	ENGINEERING WOOD	ENGINEERING WOOD	ENGINEERING WOOD	UPVC + GLASS

OPENING TYPE	W1	W2	KW1
			
			
DIMENSIONS	2400x1250	900x1250	3050x800
TYPE	SLIDING	SLIDING	SLIDING
LOCATION	LIVING AREA, BEDROOMS	LIVING AREA, BEDROOMS	LIVING AREA, BEDROOMS
MAKE	UPVC + GLASS	UPVC + GLASS	UPVC + GLASS

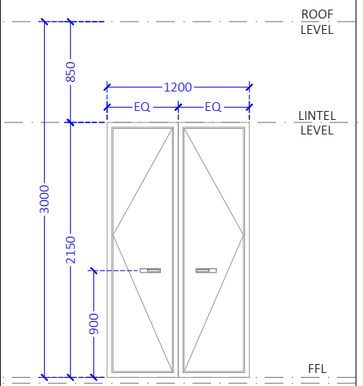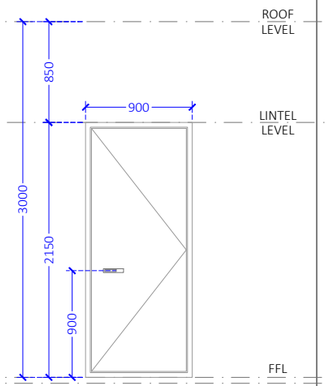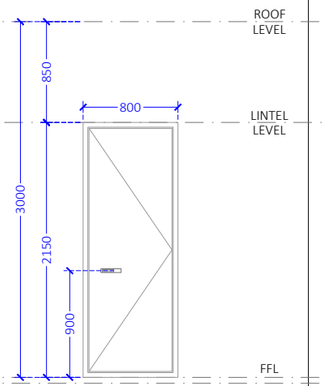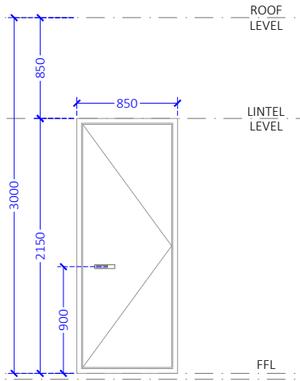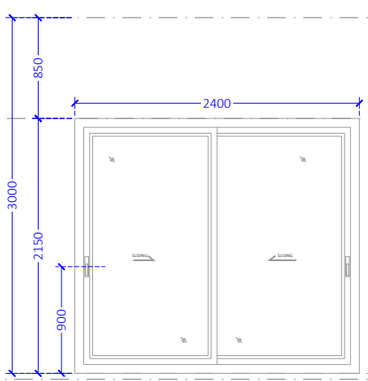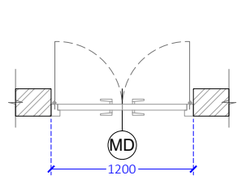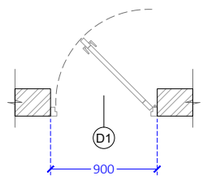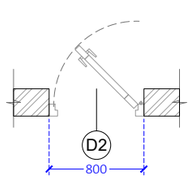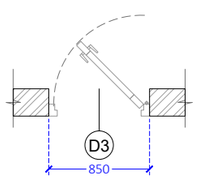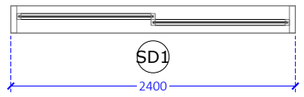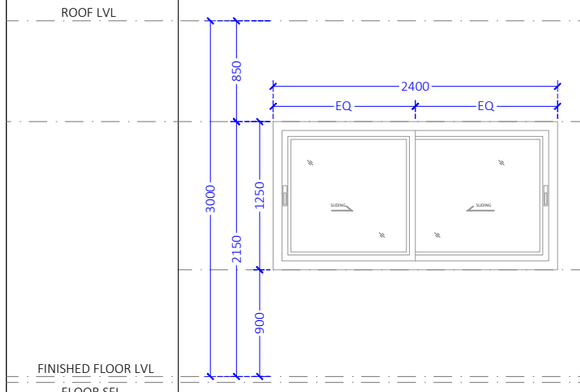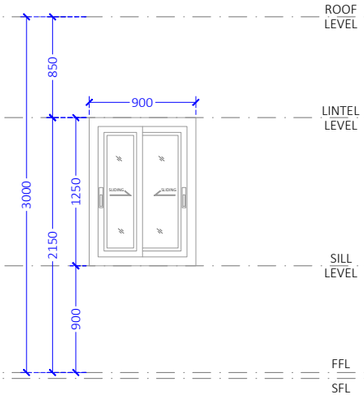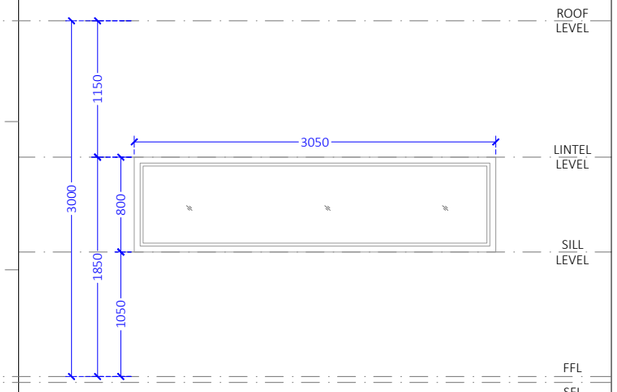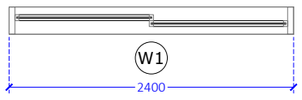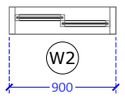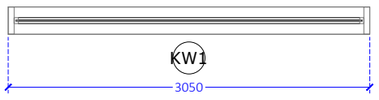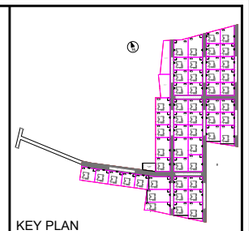

KEY PLAN

GENERAL NOTES:

- ALL DIMENSIONS ARE IN MILLIMETERS

- THIS DRAWING IS A COPYRIGHT AND PROPERTY OF THE ARCHITECT. IS NOT TO BE PRODUCED, COPIED, HANDED OVER TO THIRD PARTY OR USED FOR ANY OTHER PURPOSE OTHER THAN FOR WHICH IT IS INTENDED.

- ALL DIMENSIONS SHALL BE VERIFIED ON SITE PRIOR TO START OF WORK ANY DISCREPANCY SHALL BE BROUGHT TO THE NOTICE OF THE ARCHITECT.

- THE CONTRACTOR MUST CHECK ALL DIMENSIONS AND DETAILS AND BE RESPONSIBLE FOR THE SAME. ANY DISCREPANCY SHALL BE BROUGHT TO THE NOTICE OF THE ARCHITECT.

- THIS DRAWING IS TO BE READ AND NOT SCALED.

- THIS DRAWING SHALL BE READ IN CONJUNCTION WITH ALL RELEVANT ARCHITECTURAL, STRUCTURAL AND SERVICES DRAWINGS. ANY DISCREPANCY NOTICED SHALL BE BROUGHT TO THE ATTENTION OF THE CONSULTANTS AND RESOLVED AS SOON AS POSSIBLE BUT ALWAYS PRIOR TO

NO	DESCRIPTION	DATE	SIGN

ARCHITECTURAL CONSULTANT:

also. design

MEP CONSULTANT:

STRUCTURAL CONSULTANT:

PROJECT:

ANKURA HOMES_THE WOODS AT KEESARAGUTTA

GOOD FOR CONSTRUCTION

DRAWING TITLE:

SCHEDULE OF OPENINGS

ARCHITECT : HARISH	APPROVED : HARISH
SCALE : NTS	DRAWN : DHARANI
DATE : 08-10-2026	CHECKED : SHANMUKHI

DRAWING NO: REV.NO: