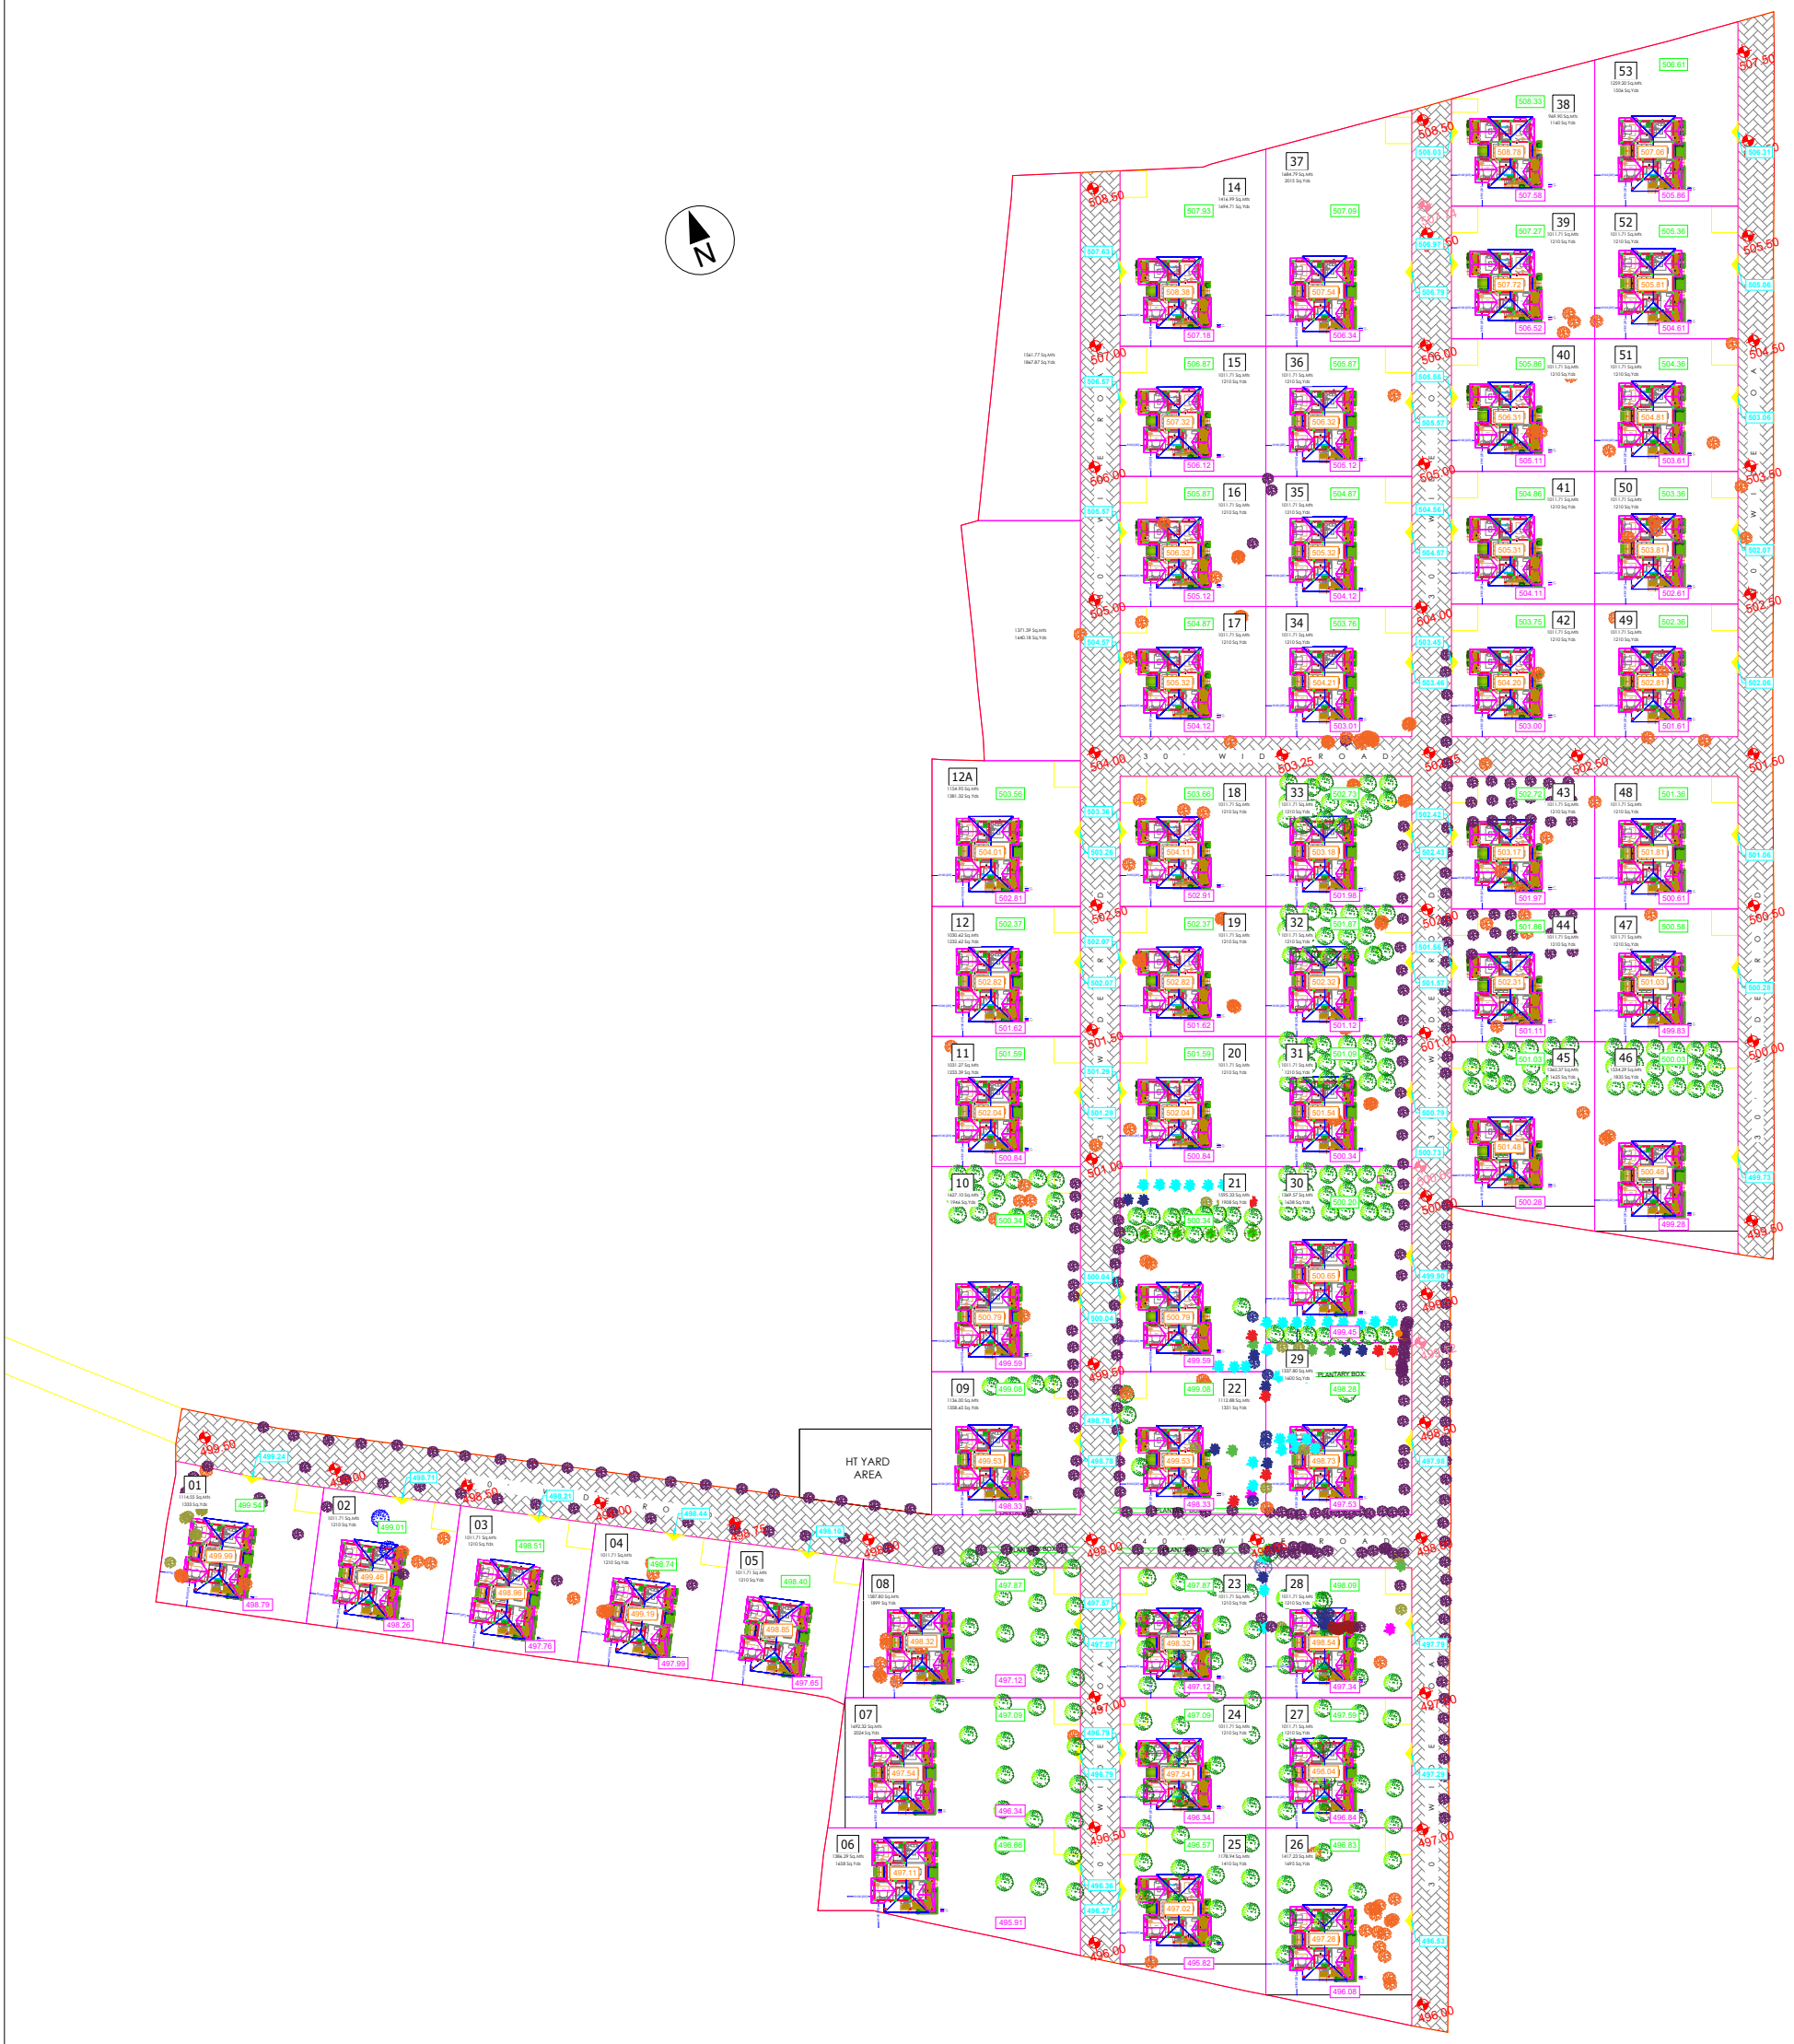

SITE PLAN

KEY PLAN

LEGEND:

- Lvl — PLOT ENTRANCE AT ROAD LEVEL
- Lvl — LAWN LEVEL (+0.3M FROM ENTRANCE LEVEL)
- Lvl — PLINTH TOP LEVEL (+0.75M FROM ENTRANCE LEVEL)
- Lvl — BACKYARD LEVEL (-0.45M FROM ENTRANCE LEVEL)

NOTE : ALL LEVELS ARE IN METERS

also. design — GFC — HYDERABAD

PROJECT
ANKURA HOMES_THE WOODS
AT KEESARAGUTTA

STRUCTURAL CONSULTANTS

MEP CONSULTANTS

GOOD FOR CONSTRUCTION

ANKURA-THE WOODS
SITE PLAN

ARCHITECT :	HARISH	APPROVED :	HARISH
SCALE :	NTS	DRAWN :	DHARANI
DATE :	21-10-2026	CHECKED :	SHANMUKHI

DRAWING NO : | REV.NO: